Hogwarts, floor by floor: every place and every space between

The Architect, 12 October 2026, for Godric. The castle model (page/castle-model.js, version 4) and the step 3 sheet, under 1.1, 2.1, 3.1, Q48b's 3 and 4.1.

How to read it

One floor a page, below ground to the tower tops, all at one scale (north up, the bar 50 m), a schedule under each plan.

Numbers are the named places: the first draft's (1 to 48) and the canon sweep's (+1 to +48), each with its book line. Brown is built, hatched designed, blue placed by the books, dotted inferred, dashed proposed.

Letters, in purple rooms, are this drawing's fill: every range has a corridor along one face and rooms along the other, cut from whatever the named places leave free, and each room is given a use and a name. Green: a place the books name but do not place (the sweep's unplaced rows, each checked in the text); purple: ours. A room of ours with a canon nod names its line.

The rule of the fill

Canon first. Then what a working castle school needs near what it serves: each subject's second classroom, store and teacher's rooms beside its named classroom; the kitchens' rooms by the kitchens; washrooms, stairs and cupboards in the deep middle of the north range, where no window reaches. Then a few rooms for the boys to find (a wizard chess room, Peeves's den of stolen chalk, portraits waiting for walls). No corridor runs past nothing.

The count

260 spaces given a use: 15 canon, 245 ours. By floor: B 28, G 27, 1 28, 2 33, 3 24, 4 27, 5 30, 6 33, 7 30, T 0.

Open


All of the fill is a proposal: mark any room and it changes. The fill goes into the model only once you have looked; the Map is inked from the model.

The castle's layout, below ground: the cellars and dungeons

The Architect, 12 October 2026, for Godric. Under 1.1, 2.1, 3.1 and Q48b's 3. North up; the bar 50 m. Numbers: the step 3 sheet's places (+ the canon sweep's); letters, purple: this sheet's fill, every space given a use.

Below ground: the dungeons and the cellars

floor at -5.2 m

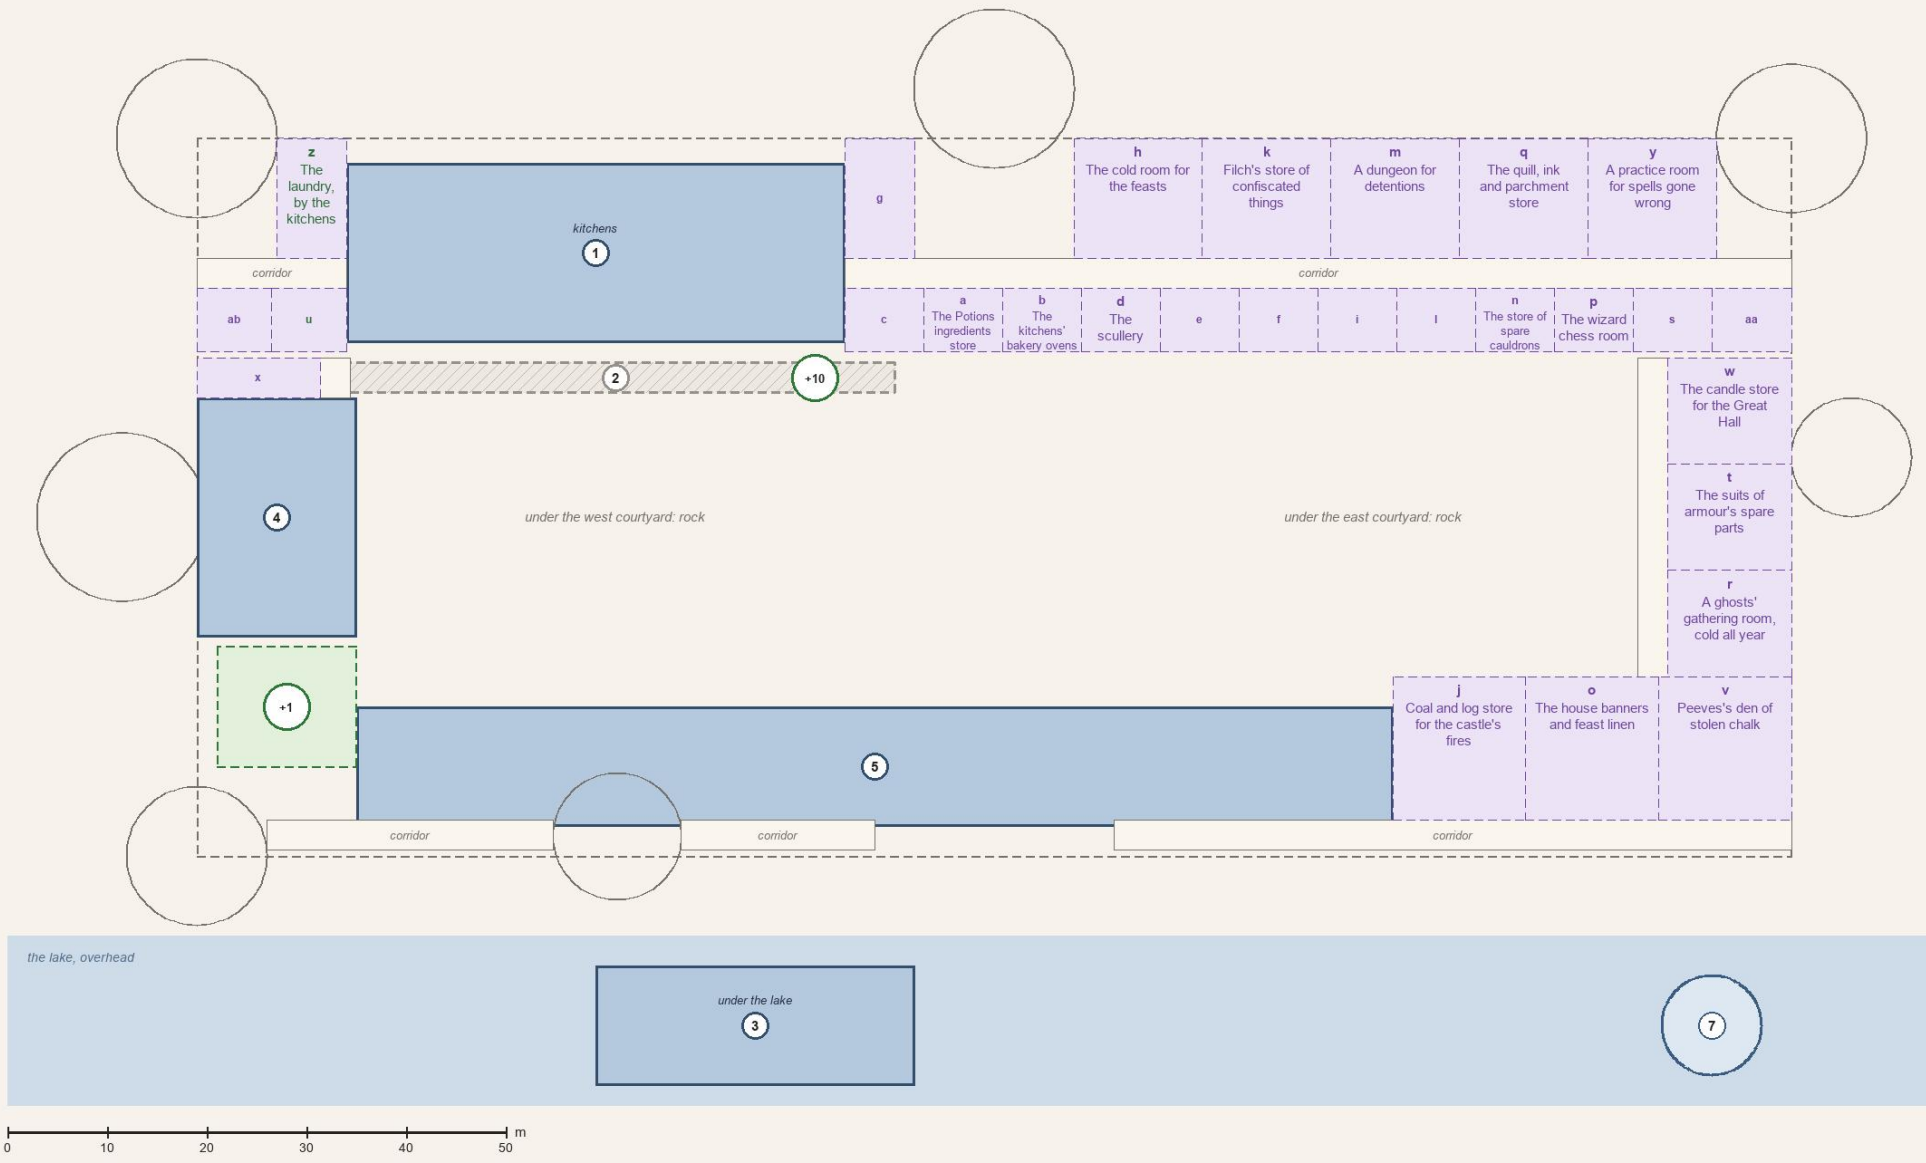

Named places on this floor (the step 3 sheet: numbers the first draft's, + the canon sweep's)

1 Kitchens [books] (GoF 21)
2 Hufflepuff's basement corridor, which also leads to the kitchens (Hufflepuff's room off the list) [off] (OotP 18, HBP 21)
3 Slytherin common room [books] (DH 23)
4 Potions classroom, down in a dungeon (the spot proposed) [books] (PS 8)
5 Dungeon corridors, the deathday party (the spot proposed) [books] (CoS 8)
6 The chambers under the trapdoor, "miles under the school" [inferred] (PS 16)
7 Chamber of Secrets [inferred] (CoS 16)
+1 Snape's office, halfway down the cold passage, by Potions (CoS 5, GoF 25) [canon]
+10 The fruit-bowl painting, the kitchens' door (GoF 21) [canon]

The towers at this level

Astronomy Tower: its stair to the top
Ravenclaw Tower: its tight spiral stair (+23)
Gryffindor Tower: below the common room: the house's storerooms (ours)
West Tower: its stair; Flitwick's office on 7 (42)
North Tower: its stair; the trapdoor landing on 7 (+3)
south-west tower: a stair and staff rooms (ours)
Dumbledore's tower: the gargoyle's moving stair on 7 (41)


This sheet's fill, every space given a use (green: canon, purple: ours)

a The Potions ingredients store [ours] north range, 8 by 6 m
b The kitchens' bakery ovens [ours] north range, 8 by 6 m
c Potions dungeon for the N.E.W.T. years [ours] north range, 8 by 6 m
d The scullery [ours] north range, 8 by 6 m
e The kitchen stores: flour, sugar, the pumpkins [ours] north range, 8 by 6 m
f The brewing cellar, where slow potions steep [ours] north range, 8 by 6 m
g The house-elves' quarters [ours] north range, 7 by 12 m
h The cold room for the feasts [ours] north range, 13 by 12 m
i The cellar of butterbeer and pumpkin juice [ours] north range, 8 by 6 m
j Coal and log store for the castle's fires [ours] south range, east, 13 by 14 m
k Filch's store of confiscated things [ours] north range, 13 by 12 m
l The old dungeon cells, empty and cold [ours] north range, 8 by 6 m
m A dungeon for detentions [ours] north range, 13 by 12 m
n The store of spare cauldrons [ours] north range, 8 by 6 m
o The house banners and feast linen [ours] south range, east, 13 by 14 m
p The wizard chess room [ours] north range, 8 by 6 m
q The quill, ink and parchment store [ours] north range, 13 by 12 m
r A ghosts' gathering room, cold all year [ours] east range, 12 by 11 m
s The Christmas decorations, a dozen trees' worth [ours] north range, 8 by 6 m
t The suits of armour's spare parts [ours] east range, 12 by 11 m
u Dungeon five, a Potions-wing classroom [canon: CoS 8] north range, 8 by 6 m
v Peeves's den of stolen chalk [ours] south range, east, 13 by 14 m
w The candle store for the Great Hall [ours] east range, 12 by 11 m
x A spiral stair between the floors [ours: PS 8: "a hundred and forty-two staircases"] west range, 12 by 4 m
y A practice room for spells gone wrong [ours] north range, 13 by 12 m
z The laundry, by the kitchens [canon: CoS 12; its spot ours] north range, 7 by 12 m
aa Portraits stacked, waiting for walls [ours] north range, 8 by 6 m
ab Potions dungeon for the O.W.L. years [ours] north range, 8 by 6 m

The castle's layout, the ground floor

The Architect, 12 October 2026, for Godric. Under 1.1, 2.1, 3.1 and Q48b's 3. North up; the bar 50 m. Numbers: the step 3 sheet's places (+ the canon sweep's); letters, purple: this sheet's fill, every space given a use.

Ground floor

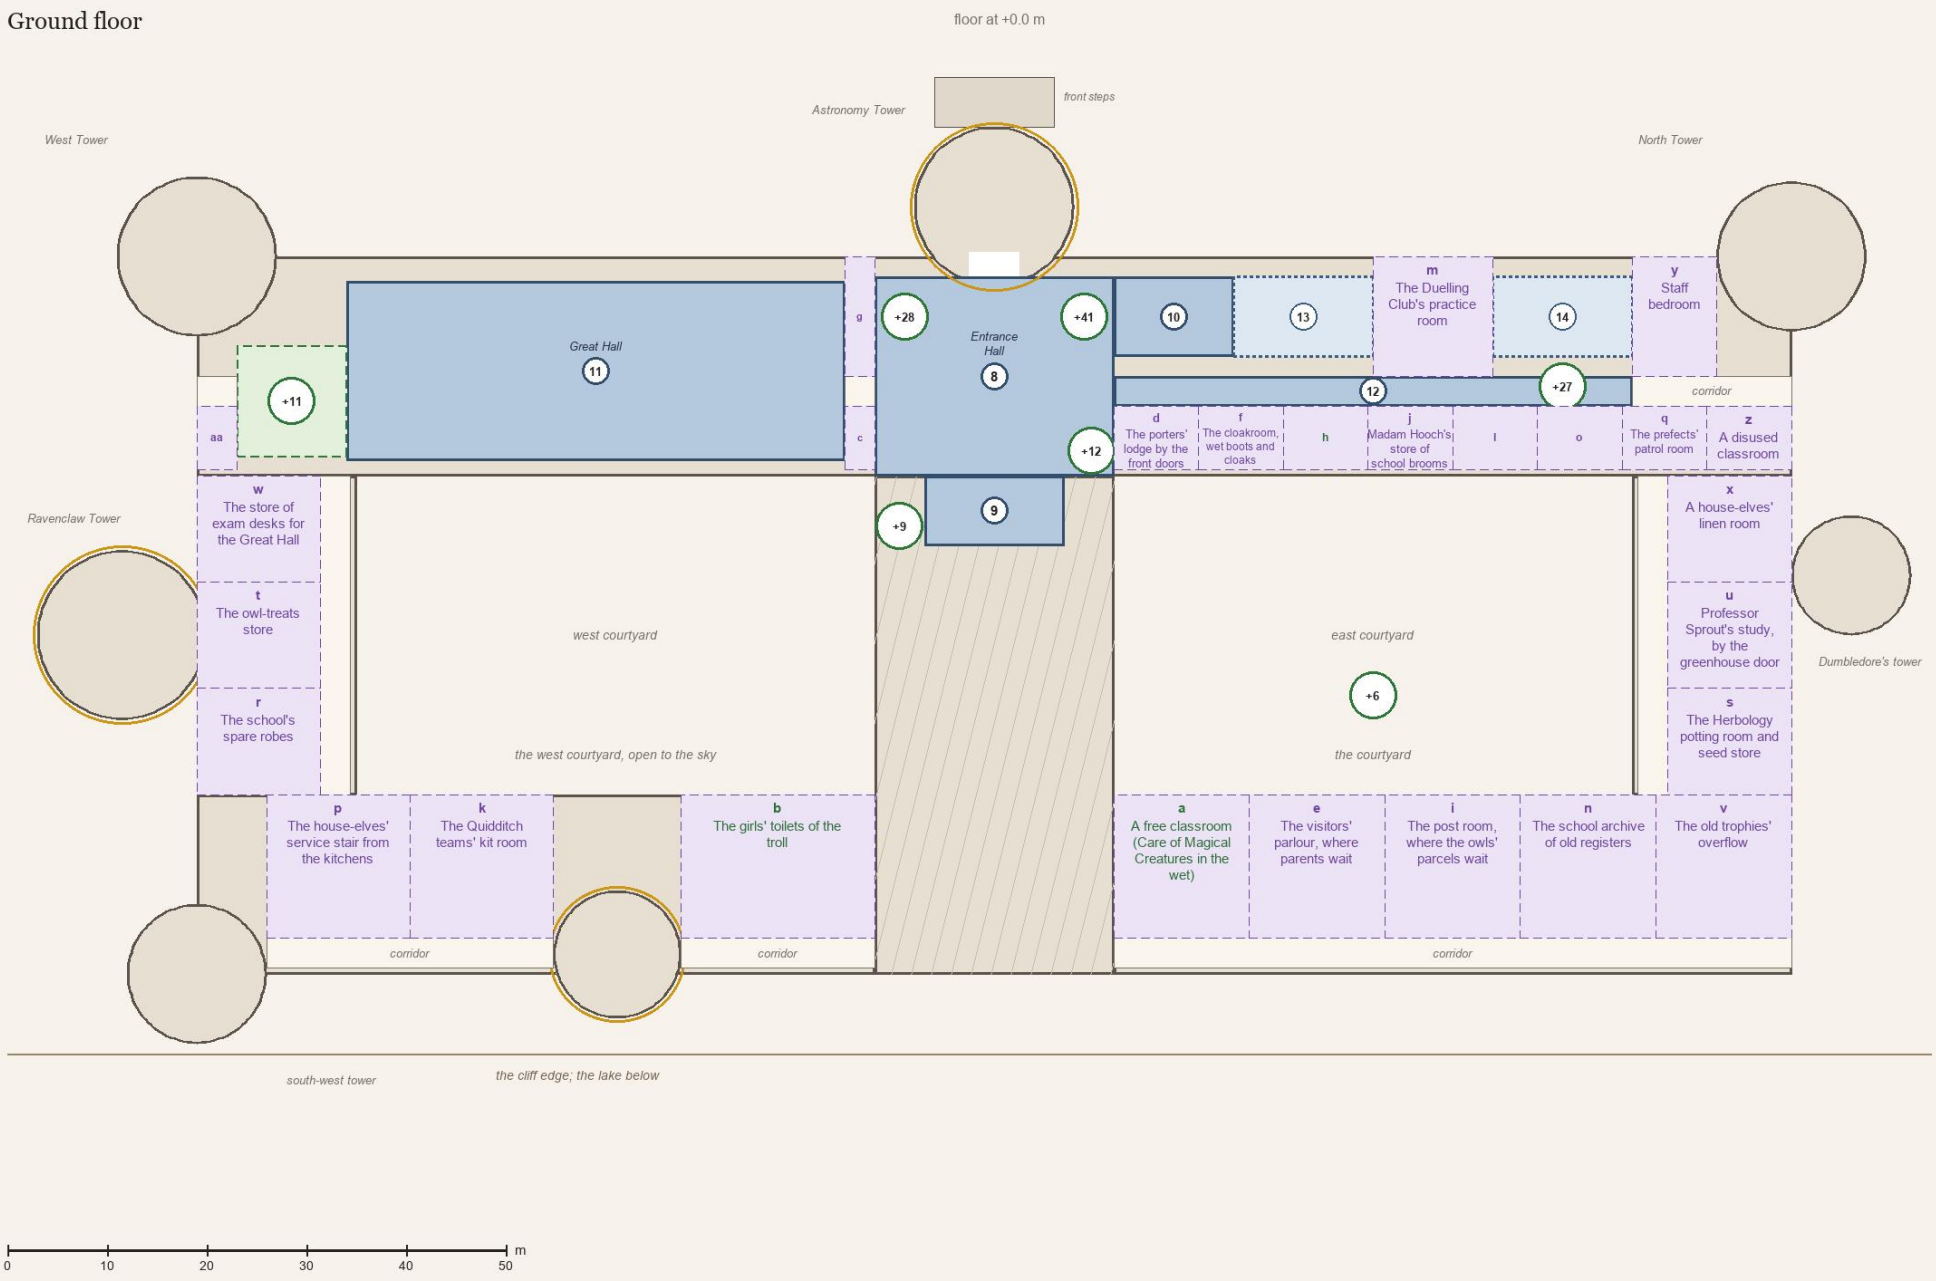

Named places on this floor (the step 3 sheet: numbers the first draft's, + the canon sweep's)

8 Entrance Hall, its front doors in the north face under the Astronomy Tower [books] (PS 7, OotP 31)
9 Marble staircase, facing the front doors [books] (PS 7, PoA 14)
10 The small, empty chamber off the hall (the side proposed) [books] (PS 7)
11 Great Hall, through a doorway to the right on entering, so west of the hall [books] (PS 7)
12 The corridor of classrooms opposite the Great Hall's door [books] (OotP 27)
13 Filch's office [inferred] (CoS 8)
14 The staff room [inferred] (PS 11)
+9 The Hufflepuff door, right of the marble staircase, steps down (GoF 17) [canon]
+6 The courtyard, by the staff room, its balcony and steps (OotP 17, OotP 12, CoS 6) [canon]
+11 The chamber off the Great Hall, behind the staff table (GoF 16, 17) [canon]
+12 The broom cupboard across the hall (PoA 21) [canon]
+27 The staff room's two gargoyles at its door (OotP 17) [canon]
+28 The Entrance Hall's balcony (DH 32) [canon]
+41 The tapestry door and narrow stair up from the hall (GoF 12) [canon]

The towers at this level

Astronomy Tower: its stair to the top
Ravenclaw Tower: its tight spiral stair (+23)
Gryffindor Tower: below the common room: the house's storerooms (ours)
West Tower: its stair; Flitwick's office on 7 (42)
North Tower: its stair; the trapdoor landing on 7 (+3)
south-west tower: a stair and staff rooms (ours)
Dumbledore's tower: the gargoyle's moving stair on 7 (41)

This sheet's fill, every space given a use (green: canon, purple: ours)


a A free classroom (Care of Magical Creatures in the wet) [canon: OotP 18] south range, east, 14 by 14 m
b The girls' toilets of the troll [canon: PS 10; its floor ours] south range, west, 19 by 14 m
c A spiral stair between the floors [ours: PS 8: "a hundred and forty-two staircases"] north range, 3 by 6 m
d The porters' lodge by the front doors [ours] north range, 8 by 6 m
e The visitors' parlour, where parents wait [ours] south range, east, 14 by 14 m
f The cloakroom, wet boots and cloaks [ours] north range, 8 by 6 m
g Washrooms, girls' and boys' [ours] north range, 3 by 12 m
h Classroom eleven, a forest room for Firenze [canon: OotP 27: off the Entrance Hall, opposite the Great Hall] north range, 8 by 6 m
i The post room, where the owls' parcels wait [ours] south range, east, 14 by 14 m
j Madam Hooch's store of school brooms [ours] north range, 8 by 6 m
k The Quidditch teams' kit room [ours] south range, west, 14 by 14 m
l The treatment room for Quidditch knocks [ours] north range, 8 by 6 m
m The Duelling Club's practice room [ours: the club canon (CoS 11)] north range, 12 by 12 m
n The school archive of old registers [ours] south range, east, 14 by 14 m
o The staff dining room, behind the staff room [ours] north range, 8 by 6 m
p The house-elves' service stair from the kitchens [ours] south range, west, 14 by 14 m
q The prefects' patrol room [ours] north range, 8 by 6 m
r The school's spare robes [ours] west range, 12 by 11 m
s The Herbology potting room and seed store [ours] east range, 12 by 11 m
t The owl-treats store [ours] west range, 12 by 11 m
u Professor Sprout's study, by the greenhouse door [ours] east range, 12 by 11 m
v The old trophies' overflow [ours] south range, east, 14 by 14 m
w The store of exam desks for the Great Hall [ours] west range, 12 by 11 m
x A house-elves' linen room [ours] east range, 12 by 11 m
y Staff bedroom [ours] north range, 8 by 12 m
z A disused classroom [ours] north range, 8 by 6 m
aa A broom cupboard [ours] north range, 4 by 6 m

The castle's layout, the first floor

The Architect, 12 October 2026, for Godric. Under 1.1, 2.1, 3.1 and Q48b's 3. North up; the bar 50 m. Numbers: the step 3 sheet's places (+ the canon sweep's); letters, purple: this sheet's fill, every space given a use.

First floor

floor at +5.2 m

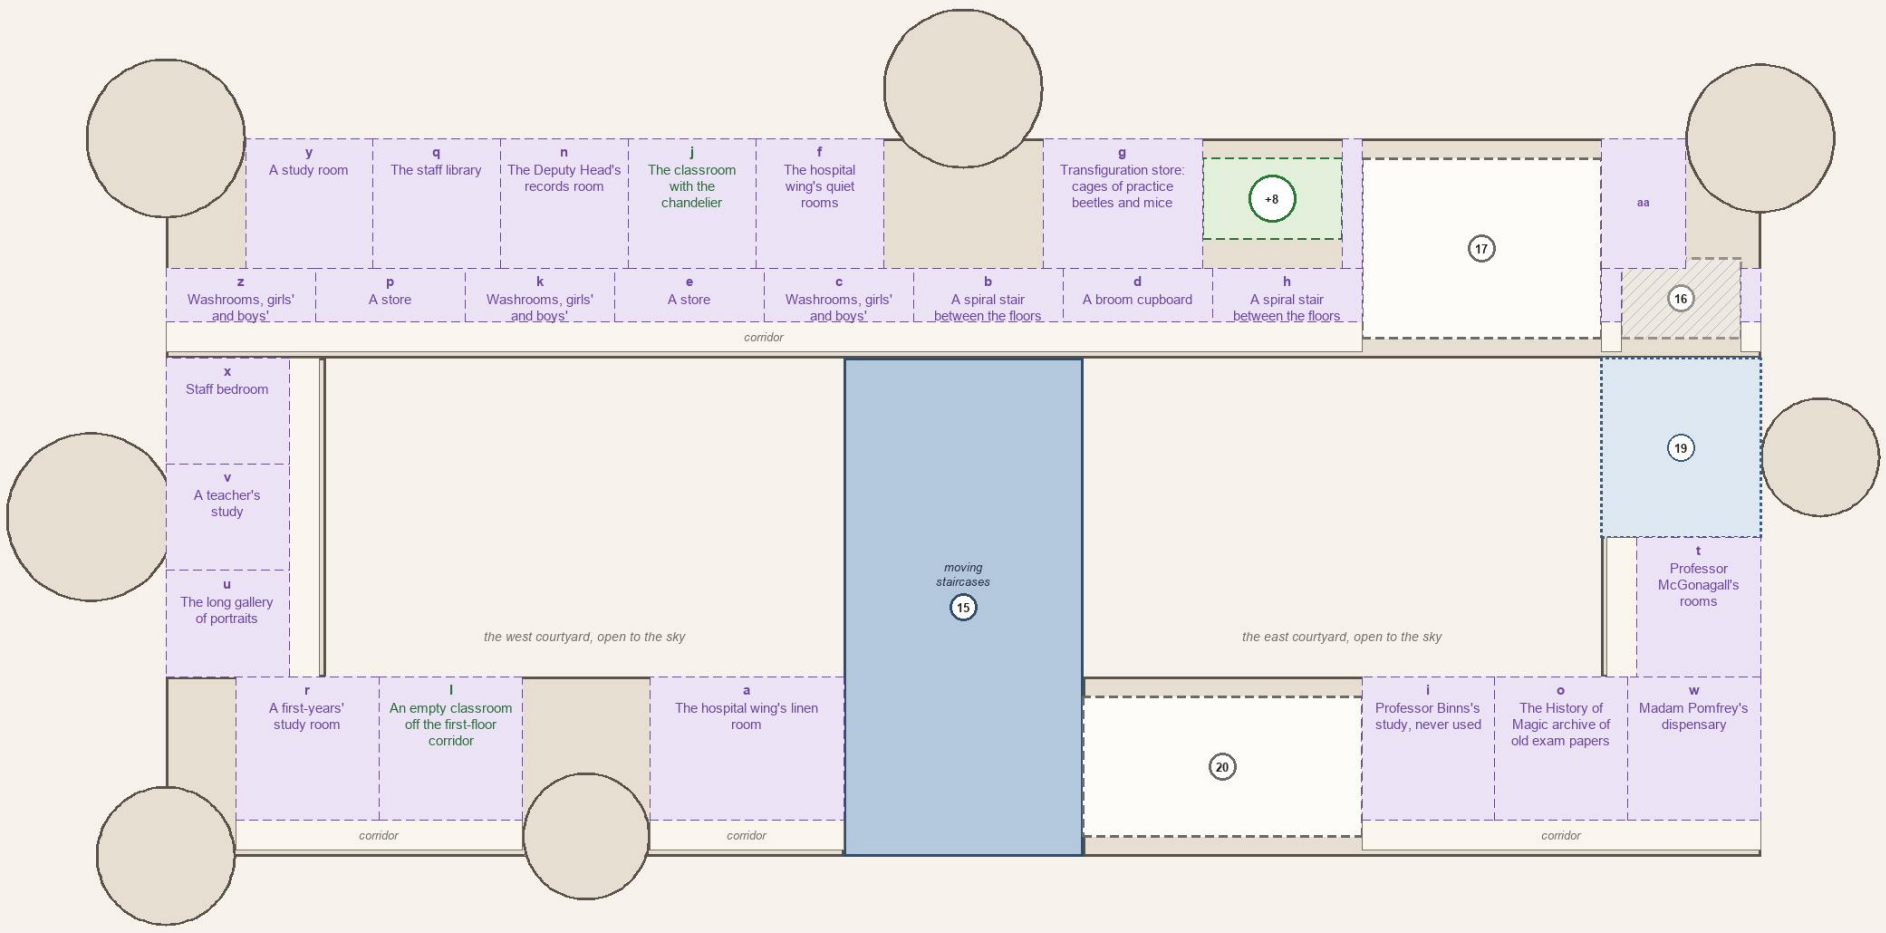

0 10 20 30 40 50 m

N

Named places on this floor (the step 3 sheet: numbers the first draft's, + the canon sweep's)

15 The moving staircases and the marble staircase in one hall, the front doors to the cliff face [books] (PS 8)
16 McGonagall's study, first floor (off the list [off] (PS 15)
17 Transfiguration classroom, beside her study [proposed]
19 Hospital wing [inferred] (PS 8)
20 History of Magic classroom, "large enough" for a class [proposed] (PoA 12)
+8 The Vanishing Cabinet's room, right over Filch's office (OotP 28, CoS 8) [canon]

The towers at this level

Astronomy Tower: its stair to the top
Ravenclaw Tower: its tight spiral stair (+23)
Gryffindor Tower: below the common room: the house's storerooms (ours)
West Tower: its stair; Flitwick's office on 7 (42)
North Tower: its stair; the trapdoor landing on 7 (+3)
south-west tower: a stair and staff rooms (ours)
Dumbledore's tower: the gargoyle's moving stair on 7 (41)

This sheet's fill, every space given a use (green: canon, purple: ours)


a The hospital wing's linen room [ours] south range, west, 19 by 14 m
b A spiral stair between the floors [ours: PS 8: "a hundred and forty-two staircases"] north range, 15 by 5 m
c Washrooms, girls' and boys' [ours] north range, 15 by 5 m
d A broom cupboard [ours] north range, 15 by 5 m
e A store [ours] north range, 15 by 5 m
f The hospital wing's quiet rooms [ours] north range, 13 by 13 m
g Transfiguration store: cages of practice beetles and mice [ours] north range, 16 by 13 m
h A spiral stair between the floors [ours: PS 8: "a hundred and forty-two staircases"] north range, 15 by 5 m
i Professor Binns's study, never used [ours] south range, east, 13 by 14 m
j The classroom with the chandelier [canon: OotP 18] north range, 13 by 13 m
k Washrooms, girls' and boys' [ours] north range, 15 by 5 m
l An empty classroom off the first-floor corridor [canon: OotP 32] south range, west, 14 by 14 m
m A broom cupboard [ours] north range, 2 by 13 m
n The Deputy Head's records room [ours] north range, 13 by 13 m
o The History of Magic archive of old exam papers [ours] south range, east, 13 by 14 m
p A store [ours] north range, 15 by 5 m
q The staff library [ours] north range, 13 by 13 m
r A first-years' study room [ours] south range, west, 14 by 14 m
s A spiral stair between the floors [ours: PS 8: "a hundred and forty-two staircases"] north range, 2 by 5 m
t Professor McGonagall's rooms [ours] east range, 12 by 14 m
u The long gallery of portraits [ours] west range, 12 by 11 m
v A teacher's study [ours] west range, 12 by 11 m
w Madam Pomfrey's dispensary [ours] south range, east, 13 by 14 m
x Staff bedroom [ours] west range, 12 by 11 m
y A study room [ours] north range, 13 by 13 m
z Washrooms, girls' and boys' [ours] north range, 15 by 5 m
aa Transfiguration classroom for the N.E.W.T. years [ours] north range, 8 by 13 m
ab A broom cupboard [ours] north range, 2 by 5 m

The castle's layout, the second floor

The Architect, 12 October 2026, for Godric. Under 1.1, 2.1, 3.1 and Q48b's 3. North up; the bar 50 m. Numbers: the step 3 sheet's places (+ the canon sweep's); letters, purple: this sheet's fill, every space given a use.

Second floor

floor at +10.4 m

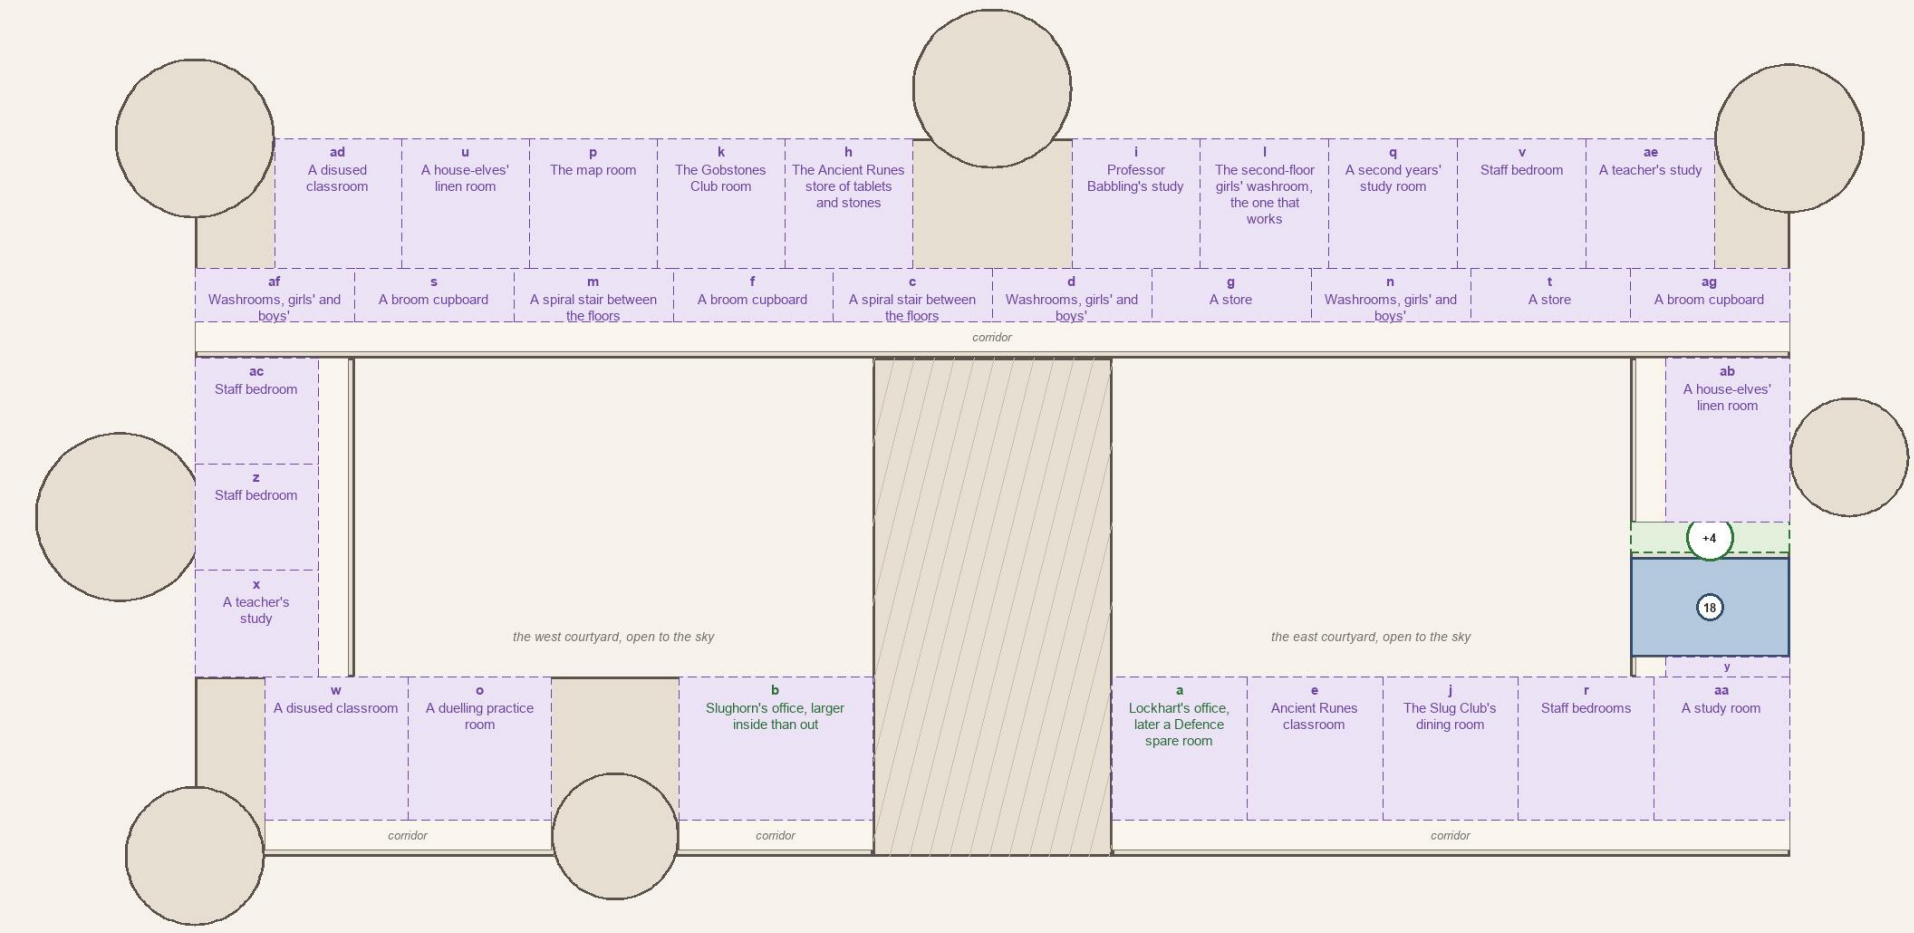

Named places on this floor (the step 3 sheet: numbers the first draft's, + the canon sweep's)

18 Myrtle's bathroom, the Chamber's door [books] (CoS 8, GoF 22)
+4 The writing on the wall: the last, deserted passage, by Myrtle's (CoS 8, 16) [canon]
+7 The trick-step tapestry stair, four down to two (GoF 25, HBP 14) [canon]
+29 The fireworks corridor, one floor below the Defence office (OotP 28) [canon]

The towers at this level

Astronomy Tower: its stair to the top
Ravenclaw Tower: its tight spiral stair (+23)
Gryffindor Tower: below the common room: the house's storerooms (ours)
West Tower: its stair; Flitwick's office on 7 (42)
North Tower: its stair; the trapdoor landing on 7 (+3)
south-west tower: a stair and staff rooms (ours)
Dumbledore's tower: the gargoyle's moving stair on 7 (41)

This sheet's fill, every space given a use (green: canon, purple: ours)


a Lockhart's office, later a Defence spare room [canon: CoS 7, CoS 9, CoS 16] south range, east, 14 by 14 m
b Slughorn's office, larger inside than out [canon: HBP 15: up the marble staircase; its floor ours] south range, west, 19 by 14 m
c A spiral stair between the floors [ours: PS 8: "a hundred and forty-two staircases"] north range, 16 by 5 m
d Washrooms, girls' and boys' [ours] north range, 16 by 5 m
e Ancient Runes classroom [ours: the subject canon, the room ours] south range, east, 14 by 14 m
f A broom cupboard [ours] north range, 16 by 5 m
g A store [ours] north range, 16 by 5 m
h The Ancient Runes store of tablets and stones [ours] north range, 13 by 13 m
i Professor Babbling's study [ours] north range, 13 by 13 m
j The Slug Club's dining room [ours: the club canon (HBP 7)] south range, east, 14 by 14 m
k The Gobstones Club room [ours: the club canon (OotP 17)] north range, 13 by 13 m
l The second-floor girls' washroom, the one that works [ours] north range, 13 by 13 m
m A spiral stair between the floors [ours: PS 8: "a hundred and forty-two staircases"] north range, 16 by 5 m
n Washrooms, girls' and boys' [ours] north range, 16 by 5 m
o A duelling practice room [ours] south range, west, 14 by 14 m
p The map room [ours] north range, 13 by 13 m
q A second years' study room [ours] north range, 13 by 13 m
r Staff bedrooms [ours] south range, east, 14 by 14 m
s A broom cupboard [ours] north range, 16 by 5 m
t A store [ours] north range, 16 by 5 m
u A house-elves' linen room [ours] north range, 13 by 13 m
v Staff bedroom [ours] north range, 13 by 13 m
w A disused classroom [ours] south range, west, 14 by 14 m
x A teacher's study [ours] west range, 12 by 11 m
y A spiral stair between the floors [ours: PS 8: "a hundred and forty-two staircases"] east range, 12 by 2 m
z Staff bedroom [ours] west range, 12 by 11 m
aa A study room [ours] south range, east, 14 by 14 m
ab A house-elves' linen room [ours] east range, 12 by 16 m
ac Staff bedroom [ours] west range, 12 by 11 m
ad A disused classroom [ours] north range, 13 by 13 m
ae A teacher's study [ours] north range, 13 by 13 m
af Washrooms, girls' and boys' [ours] north range, 16 by 5 m
ag A broom cupboard [ours] north range, 16 by 5 m

The castle's layout, the third floor

The Architect, 12 October 2026, for Godric. Under 1.1, 2.1, 3.1 and Q48b's 3. North up; the bar 50 m. Numbers: the step 3 sheet's places (+ the canon sweep's); letters, purple: this sheet's fill, every space given a use.

Third floor

floor at +15.6 m

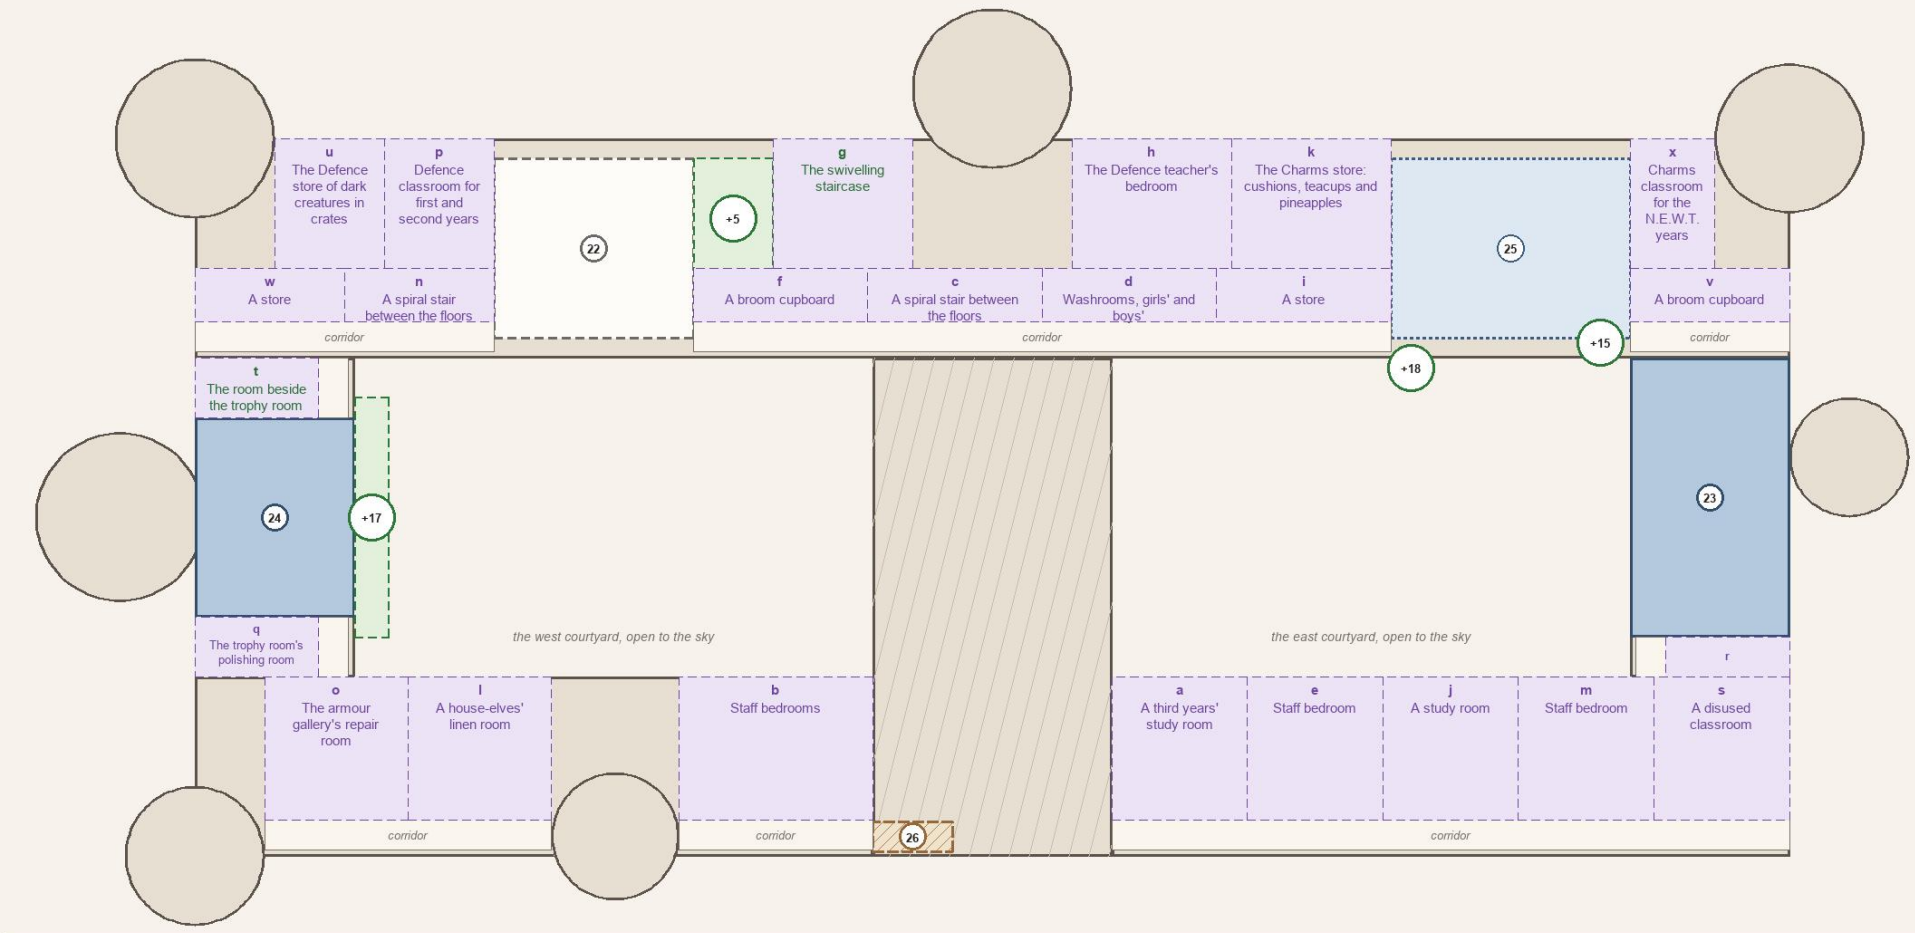





Named places on this floor (the step 3 sheet: numbers the first draft's, + the canon sweep's)

22 Defence Against the Dark Arts classroom [proposed] (PoA 9)
23 The forbidden corridor [books] (PS 7)
24 Trophy room, third floor (the spot proposed) [books] (PS 9)
25 Charms classroom [inferred] (PS 9)
26 The one-eyed witch's landing, directly beneath the corridor's landing, on the stair hall's well [designed] (PoA 10, 14)
+5 The Defence office (Umbridge's), its corridor's suit of armour (OotP 13, 29) [canon]
+15 The Charms corridor, ending at the forbidden door (PS 9) [canon]
+17 The long gallery of armour, by the trophy room (PS 9) [canon]
+18 The drunk monks, by the Charms corridor (HBP 17) [canon]

The towers at this level

Astronomy Tower: its stair to the top
Ravenclaw Tower: its tight spiral stair (+23)
Gryffindor Tower: below the common room: the house's storerooms (ours)
West Tower: its stair; Flitwick's office on 7 (42)
North Tower: its stair; the trapdoor landing on 7 (+3)
south-west tower: a stair and staff rooms (ours)
Dumbledore's tower: the gargoyle's moving stair on 7 (41)

This sheet's fill, every space given a use (green: canon, purple: ours)


a A third years' study room [ours] south range, east, 14 by 14 m
b Staff bedrooms [ours] south range, west, 19 by 14 m
c A spiral stair between the floors [ours: PS 8: "a hundred and forty-two staircases"] north range, 18 by 5 m
d Washrooms, girls' and boys' [ours] north range, 18 by 5 m
e Staff bedroom [ours] south range, east, 14 by 14 m
f A broom cupboard [ours] north range, 18 by 5 m
g The swivelling staircase [canon: OotP 32] north range, 14 by 13 m
h The Defence teacher's bedroom [ours] north range, 16 by 13 m
i A store [ours] north range, 18 by 5 m
j A study room [ours] south range, east, 14 by 14 m
k The Charms store: cushions, teacups and pineapples [ours] north range, 16 by 13 m
l A house-elves' linen room [ours] south range, west, 14 by 14 m
m Staff bedroom [ours] south range, east, 14 by 14 m
n A spiral stair between the floors [ours: PS 8: "a hundred and forty-two staircases"] north range, 15 by 5 m
o The armour gallery's repair room [ours] south range, west, 14 by 14 m
p Defence classroom for first and second years [ours] north range, 11 by 13 m
q The trophy room's polishing room [ours] west range, 12 by 6 m
r Washrooms, girls' and boys' [ours] east range, 12 by 4 m
s A disused classroom [ours] south range, east, 14 by 14 m
t The room beside the trophy room [canon: PS 9] west range, 12 by 6 m
u The Defence store of dark creatures in crates [ours] north range, 11 by 13 m
v A broom cupboard [ours] north range, 16 by 5 m
w A store [ours] north range, 15 by 5 m
x Charms classroom for the N.E.W.T. years [ours] north range, 8 by 13 m

The castle's layout, the fourth floor

The Architect, 12 October 2026, for Godric. Under 1.1, 2.1, 3.1 and Q48b's 3. North up; the bar 50 m. Numbers: the step 3 sheet's places (+ the canon sweep's); letters, purple: this sheet's fill, every space given a use.

Fourth floor

floor at +20.8 m

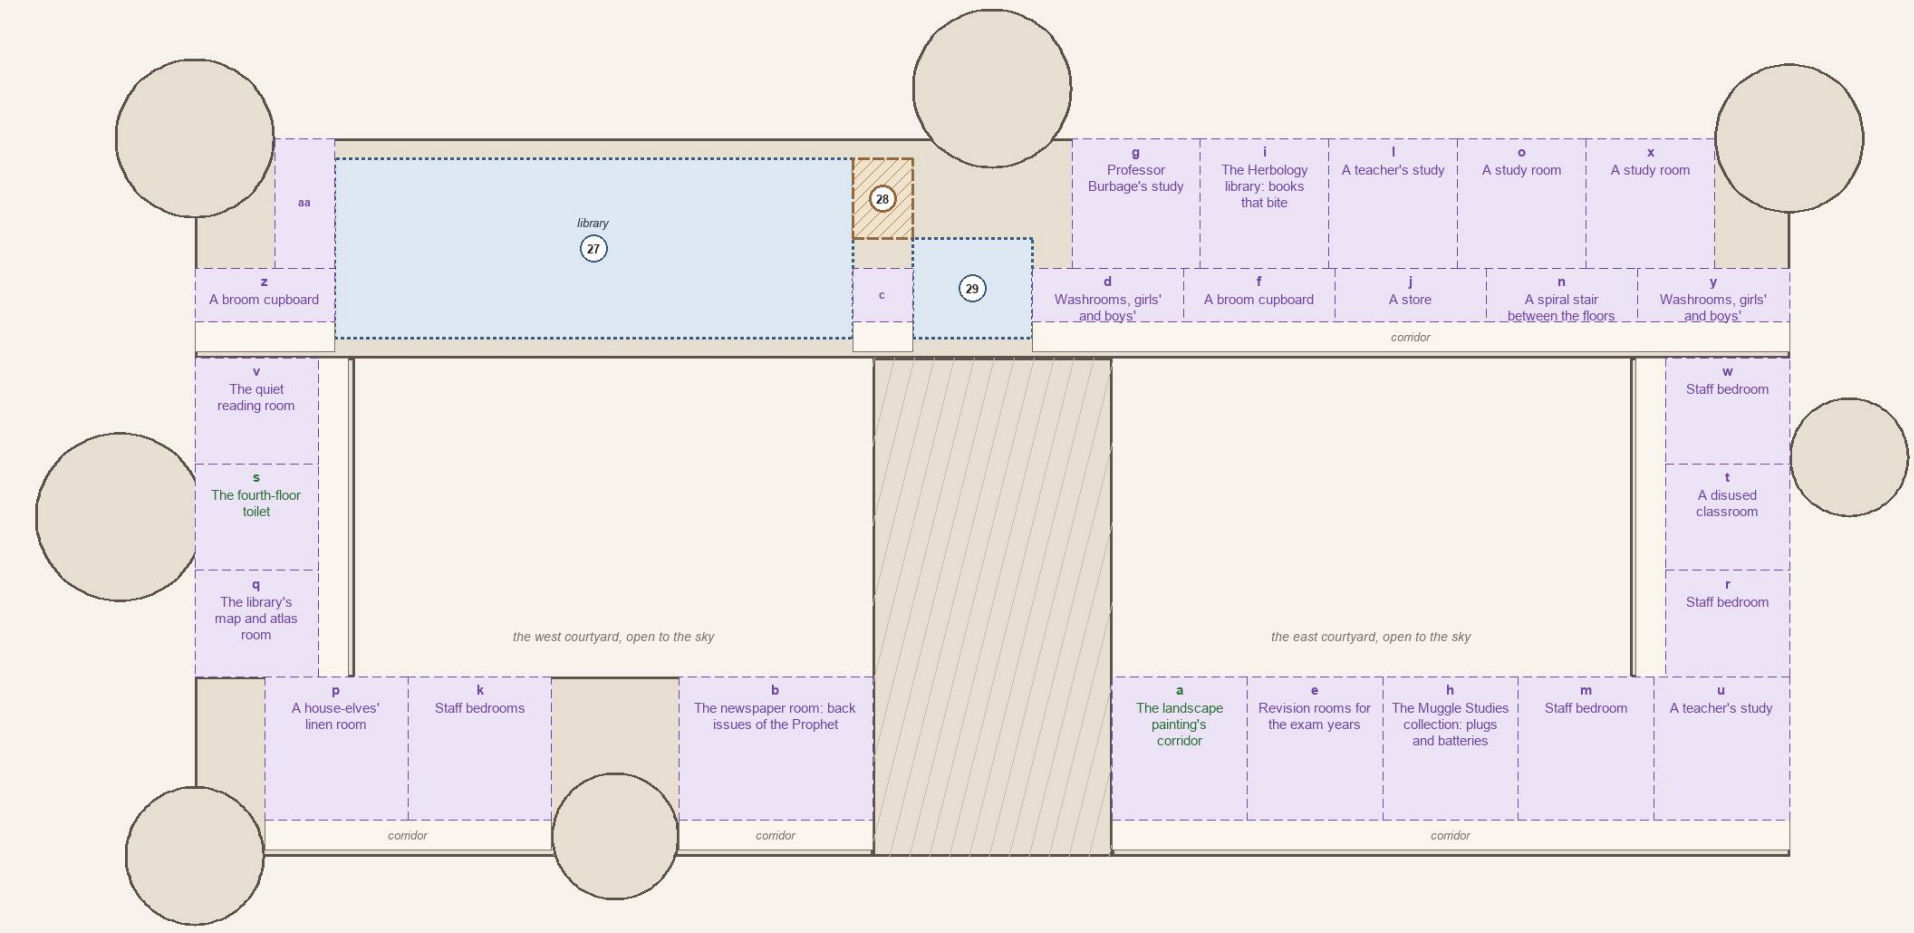

0 10 20 30 40 50 m

N

Named places on this floor (the step 3 sheet: numbers the first draft's, + the canon sweep's)

27 Library, the Restricted Section at the back [inferred] (PS 12)
28 The Muggle Studies room, past the last stack (Magic) [designed]
29 The unused classroom with the Mirror of Erised, near the library [inferred] (PS 12)
30 The passage behind the mirror, fourth floor, caved in [inferred] (PoA 10, OotP 17)

The towers at this level

Astronomy Tower: its stair to the top
Ravenclaw Tower: its tight spiral stair (+23)
Gryffindor Tower: below the common room: the house's storerooms (ours)
West Tower: its stair; Flitwick's office on 7 (42)
North Tower: its stair; the trapdoor landing on 7 (+3)
south-west tower: a stair and staff rooms (ours)
Dumbledore's tower: the gargoyle's moving stair on 7 (41)

This sheet's fill, every space given a use (green: canon, purple: ours)


a The landscape painting's corridor [canon: PoA 8] south range, east, 14 by 14 m
b The newspaper room: back issues of the Prophet [ours] south range, west, 19 by 14 m
c A spiral stair between the floors [ours: PS 8: "a hundred and forty-two staircases"] north range, 6 by 5 m
d Washrooms, girls' and boys' [ours] north range, 15 by 5 m
e Revision rooms for the exam years [ours] south range, east, 14 by 14 m
f A broom cupboard [ours] north range, 15 by 5 m
g Professor Burbage's study [ours: Muggle Studies, Magic's room beside it] north range, 13 by 13 m
h The Muggle Studies collection: plugs and batteries [ours: a nod to CoS 3] south range, east, 14 by 14 m
i The Herbology library: books that bite [ours] north range, 13 by 13 m
j A store [ours] north range, 15 by 5 m
k Staff bedrooms [ours] south range, west, 14 by 14 m
l A teacher's study [ours] north range, 13 by 13 m
m Staff bedroom [ours] south range, east, 14 by 14 m
n A spiral stair between the floors [ours: PS 8: "a hundred and forty-two staircases"] north range, 15 by 5 m
o A study room [ours] north range, 13 by 13 m
p A house-elves' linen room [ours] south range, west, 14 by 14 m
q The library's map and atlas room [ours] west range, 12 by 11 m
r Staff bedroom [ours] east range, 12 by 11 m
s The fourth-floor toilet [canon: OotP 28] west range, 12 by 11 m
t A disused classroom [ours] east range, 12 by 11 m
u A teacher's study [ours] south range, east, 14 by 14 m
v The quiet reading room [ours] west range, 12 by 11 m
w Staff bedroom [ours] east range, 12 by 11 m
x A study room [ours] north range, 13 by 13 m
y Washrooms, girls' and boys' [ours] north range, 15 by 5 m
z A broom cupboard [ours] north range, 14 by 5 m
aa Madam Pince's office and book-mending room [ours] north range, 6 by 13 m

The castle's layout, the fifth floor

The Architect, 12 October 2026, for Godric. Under 1.1, 2.1, 3.1 and Q48b's 3. North up; the bar 50 m. Numbers: the step 3 sheet's places (+ the canon sweep's); letters, purple: this sheet's fill, every space given a use.

Fifth floor

floor at +26.0 m

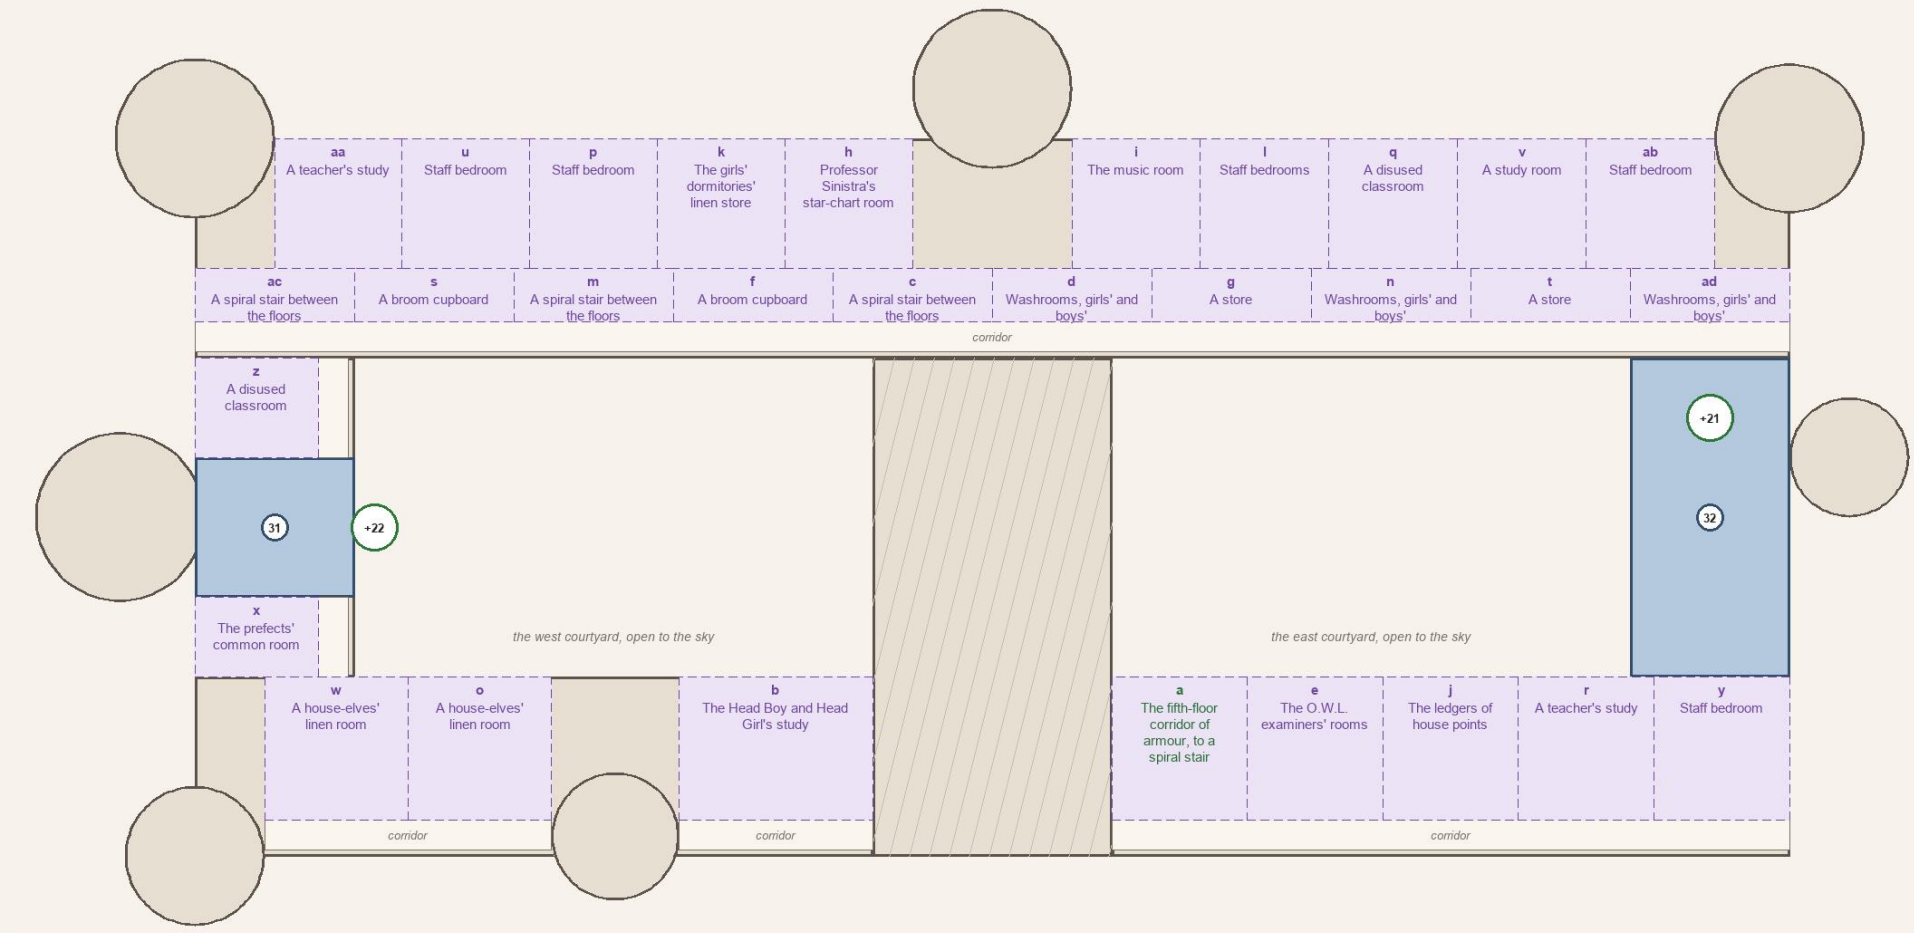





Named places on this floor (the step 3 sheet: numbers the first draft's, + the canon sweep's)

31 Prefects' bathroom, by Boris the Bewildered (the spot proposed) [books] (GoF 23)
32 The east wing, named on the fifth floor [books] (OotP 30)
+22 Boris the Bewildered; the fourth door to his left (GoF 23, 25) [canon]
+21 Gregory the Smarmy's corridor, the east wing (OotP 29, 30) [canon]

The towers at this level

Astronomy Tower: its stair to the top
Ravenclaw Tower: its tight spiral stair (+23)
Gryffindor Tower: below the common room: the house's storerooms (ours)
West Tower: its stair; Flitwick's office on 7 (42)
North Tower: its stair; the trapdoor landing on 7 (+3)
south-west tower: a stair and staff rooms (ours)
Dumbledore's tower: the gargoyle's moving stair on 7 (41)

This sheet's fill, every space given a use (green: canon, purple: ours)


a The fifth-floor corridor of armour, to a spiral stair [canon: DH 29] south range, east, 14 by 14 m
b The Head Boy and Head Girl's study [ours] south range, west, 19 by 14 m
c A spiral stair between the floors [ours: PS 8: "a hundred and forty-two staircases"] north range, 16 by 5 m
d Washrooms, girls' and boys' [ours] north range, 16 by 5 m
e The O.W.L. examiners' rooms [ours] south range, east, 14 by 14 m
f A broom cupboard [ours] north range, 16 by 5 m
g A store [ours] north range, 16 by 5 m
h Professor Sinistra's star-chart room [ours] north range, 13 by 13 m
i The music room [ours] north range, 13 by 13 m
j The ledgers of house points [ours] south range, east, 14 by 14 m
k The girls' dormitories' linen store [ours] north range, 13 by 13 m
l Staff bedrooms [ours] north range, 13 by 13 m
m A spiral stair between the floors [ours: PS 8: "a hundred and forty-two staircases"] north range, 16 by 5 m
n Washrooms, girls' and boys' [ours] north range, 16 by 5 m
o A house-elves' linen room [ours] south range, west, 14 by 14 m
p Staff bedroom [ours] north range, 13 by 13 m
q A disused classroom [ours] north range, 13 by 13 m
r A teacher's study [ours] south range, east, 14 by 14 m
s A broom cupboard [ours] north range, 16 by 5 m
t A store [ours] north range, 16 by 5 m
u Staff bedroom [ours] north range, 13 by 13 m
v A study room [ours] north range, 13 by 13 m
w A house-elves' linen room [ours] south range, west, 14 by 14 m
x The prefects' common room [ours] west range, 12 by 8 m
y Staff bedroom [ours] south range, east, 14 by 14 m
z A disused classroom [ours] west range, 12 by 10 m
aa A teacher's study [ours] north range, 13 by 13 m
ab Staff bedroom [ours] north range, 13 by 13 m
ac A spiral stair between the floors [ours: PS 8: "a hundred and forty-two staircases"] north range, 16 by 5 m
ad Washrooms, girls' and boys' [ours] north range, 16 by 5 m

The castle's layout, the sixth floor

The Architect, 12 October 2026, for Godric. Under 1.1, 2.1, 3.1 and Q48b's 3. North up; the bar 50 m. Numbers: the step 3 sheet's places (+ the canon sweep's); letters, purple: this sheet's fill, every space given a use.

Sixth floor

floor at +31.2 m

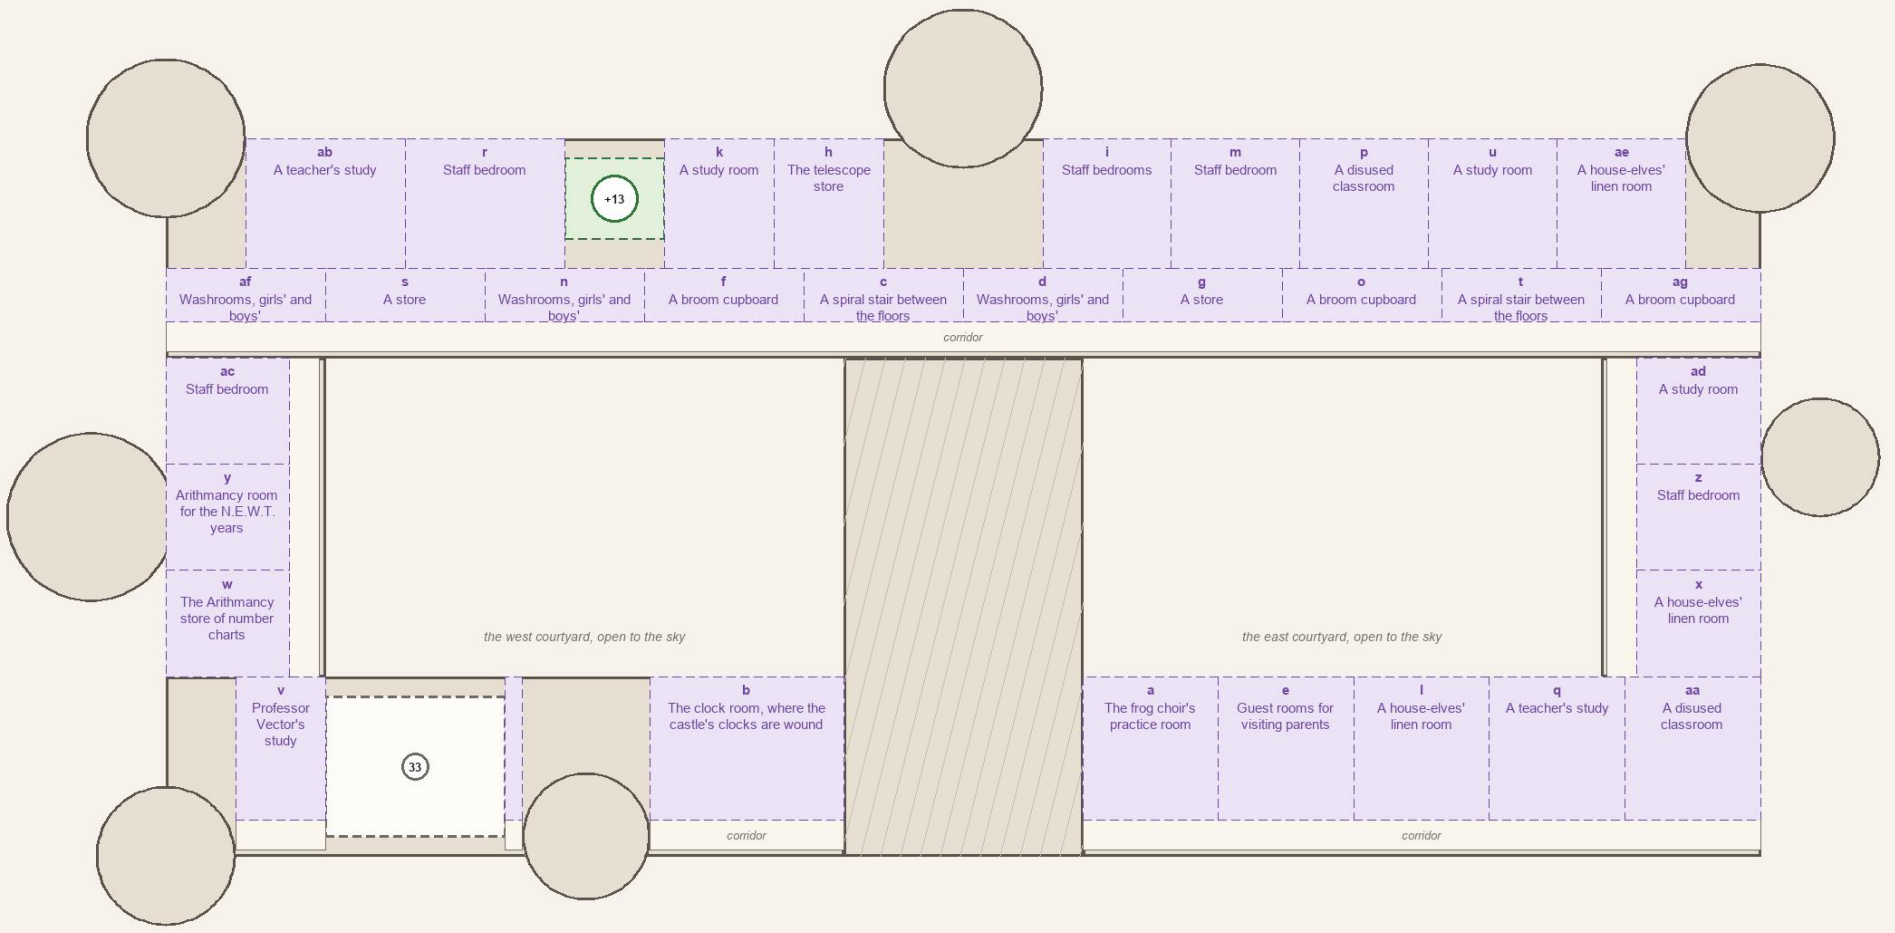

0 10 20 30 40 50 m

N

Named places on this floor (the step 3 sheet: numbers the first draft's, + the canon sweep's)

33 Arithmancy classroom (proposed) [proposed]
+13 The boys' bathroom, the floor below the Room (HBP 24) [canon]

The towers at this level

Astronomy Tower: its stair to the top
Ravenclaw Tower: its tight spiral stair (+23)
Gryffindor Tower: below the common room: the house's storerooms (ours)
West Tower: its stair; Flitwick's office on 7 (42)
North Tower: its stair; the trapdoor landing on 7 (+3)
south-west tower: a stair and staff rooms (ours)
Dumbledore's tower: the gargoyle's moving stair on 7 (41)

This sheet's fill, every space given a use (green: canon, purple: ours)


a The frog choir's practice room [ours] south range, east, 14 by 14 m
b The clock room, where the castle's clocks are wound [ours] south range, west, 19 by 14 m
c A spiral stair between the floors [ours: PS 8: "a hundred and forty-two staircases"] north range, 16 by 5 m
d Washrooms, girls' and boys' [ours] north range, 16 by 5 m
e Guest rooms for visiting parents [ours] south range, east, 14 by 14 m
f A broom cupboard [ours] north range, 16 by 5 m
g A store [ours] north range, 16 by 5 m
h The telescope store [ours] north range, 11 by 13 m
i Staff bedrooms [ours] north range, 13 by 13 m
j A spiral stair between the floors [ours: PS 8: "a hundred and forty-two staircases"] south range, west, 2 by 14 m
k A study room [ours] north range, 11 by 13 m
l A house-elves' linen room [ours] south range, east, 14 by 14 m
m Staff bedroom [ours] north range, 13 by 13 m
n Washrooms, girls' and boys' [ours] north range, 16 by 5 m
o A broom cupboard [ours] north range, 16 by 5 m
p A disused classroom [ours] north range, 13 by 13 m
q A teacher's study [ours] south range, east, 14 by 14 m
r Staff bedroom [ours] north range, 16 by 13 m
s A store [ours] north range, 16 by 5 m
t A spiral stair between the floors [ours: PS 8: "a hundred and forty-two staircases"] north range, 16 by 5 m
u A study room [ours] north range, 13 by 13 m
v Professor Vector's study [ours: Arithmancy's teacher canon] south range, west, 9 by 14 m
w The Arithmancy store of number charts [ours] west range, 12 by 11 m
x A house-elves' linen room [ours] east range, 12 by 11 m
y Arithmancy room for the N.E.W.T. years [ours] west range, 12 by 11 m
z Staff bedroom [ours] east range, 12 by 11 m
aa A disused classroom [ours] south range, east, 14 by 14 m
ab A teacher's study [ours] north range, 16 by 13 m
ac Staff bedroom [ours] west range, 12 by 11 m
ad A study room [ours] east range, 12 by 11 m
ae A house-elves' linen room [ours] north range, 13 by 13 m
af Washrooms, girls' and boys' [ours] north range, 16 by 5 m
ag A broom cupboard [ours] north range, 16 by 5 m

The castle's layout, the seventh floor

The Architect, 12 October 2026, for Godric. Under 1.1, 2.1, 3.1 and Q48b's 3. North up; the bar 50 m. Numbers: the step 3 sheet's places (+ the canon sweep's); letters, purple: this sheet's fill, every space given a use.

Seventh floor: the built suite at true size, in place

floor at +36.4 m

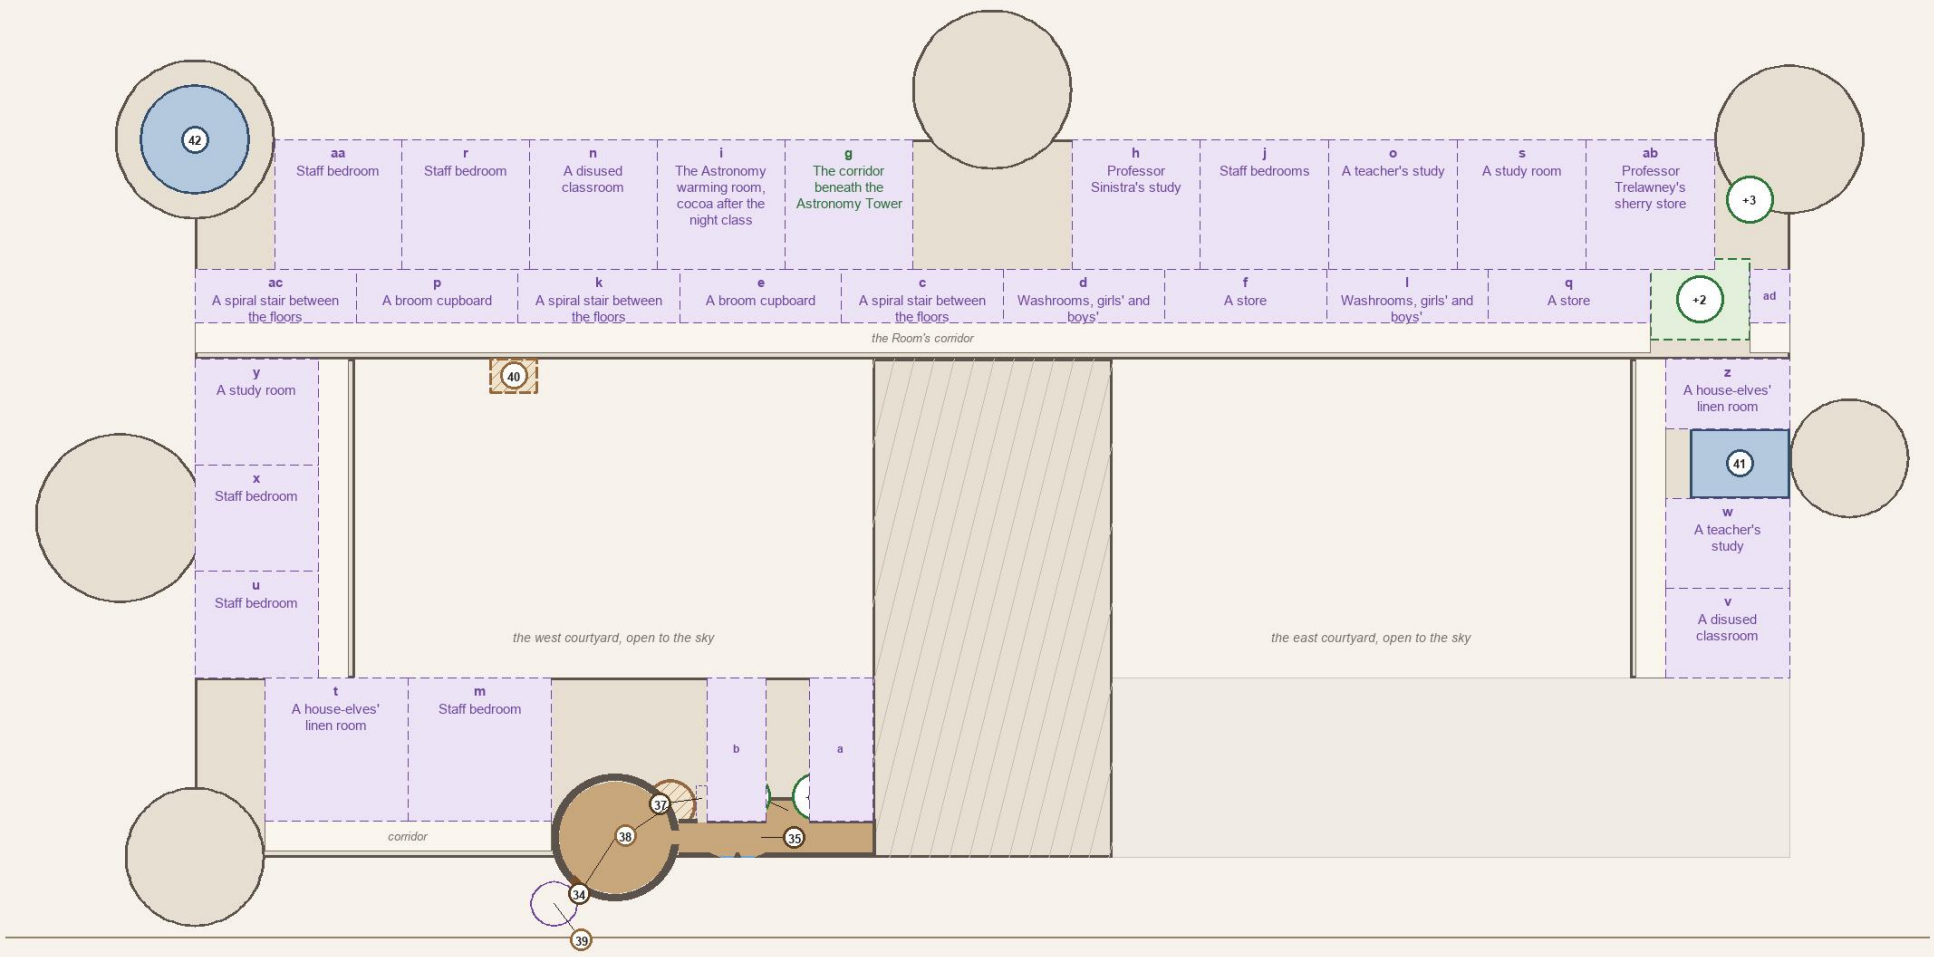

Named places on this floor (the step 3 sheet: numbers the first draft's, + the canon sweep's)

34 Gryffindor common room [built] (PS 9)
35 The Fat Lady's corridor [built] (PS 7, OotP 13)
36 The inglenook, where visitors wait [built]
37 The polite door (built) and the room of lost things behind it, bigger inside (designed) [built]
38 Clementine's study [designed]
39 The little door at the stair's foot (built in grey) and the den behind it [designed]
40 Room of Requirement on its own seventh-floor corridor (Q48b's option 3 [designed] (OotP 18, HBP 24)
41 Dumbledore's corridor and the lone gargoyle, round the other side of the castle from the Room (HBP 21, HBP 10) [books] (HBP 25)
42 Flitwick's office, seventh floor of the West Tower [books] (PoA 21)
+2 Sir Cadogan's landing, at the top of the seventh long stair (PoA 6, 14) [canon]
+3 The North Tower stair and the trapdoor landing (PoA 6, 16) [canon]
+14 Lachlan the Lanky, at the stair head, turning right (OotP 13) [canon]
+20 Paracelsus halfway down the passage; Wilfred the Wistful (OotP 14) [canon]

The towers at this level

Astronomy Tower: its stair to the top
Ravenclaw Tower: its tight spiral stair (+23)
Gryffindor Tower: below the common room: the house's storerooms (ours)
West Tower: its stair; Flitwick's office on 7 (42)
North Tower: its stair; the trapdoor landing on 7 (+3)
south-west tower: a stair and staff rooms (ours)
Dumbledore's tower: the gargoyle's moving stair on 7 (41)

This sheet's fill, every space given a use (green: canon, purple: ours)


a The Headmaster's guest rooms [ours] south range, west, 6 by 14 m
b The seventh-floor broom cupboard [ours] south range, west, 6 by 14 m
c A spiral stair between the floors [ours: PS 8: "a hundred and forty-two staircases"] north range, 16 by 5 m
d Washrooms, girls' and boys' [ours] north range, 16 by 5 m
e A broom cupboard [ours] north range, 16 by 5 m
f A store [ours] north range, 16 by 5 m
g The corridor beneath the Astronomy Tower [canon: PS 14] north range, 13 by 13 m
h Professor Sinistra's study [ours] north range, 13 by 13 m
i The Astronomy warming room, cocoa after the night class [ours] north range, 13 by 13 m
j Staff bedrooms [ours] north range, 13 by 13 m
k A spiral stair between the floors [ours: PS 8: "a hundred and forty-two staircases"] north range, 16 by 5 m
l Washrooms, girls' and boys' [ours] north range, 16 by 5 m
m Staff bedroom [ours] south range, west, 14 by 14 m
n A disused classroom [ours] north range, 13 by 13 m
o A teacher's study [ours] north range, 13 by 13 m
p A broom cupboard [ours] north range, 16 by 5 m
q A store [ours] north range, 16 by 5 m
r Staff bedroom [ours] north range, 13 by 13 m
s A study room [ours] north range, 13 by 13 m
t A house-elves' linen room [ours] south range, west, 14 by 14 m
u Staff bedroom [ours] west range, 12 by 11 m
v A disused classroom [ours] east range, 12 by 9 m
w A teacher's study [ours] east range, 12 by 9 m
x Staff bedroom [ours] west range, 12 by 11 m
y A study room [ours] west range, 12 by 11 m
z A house-elves' linen room [ours] east range, 12 by 7 m
aa Staff bedroom [ours] north range, 13 by 13 m
ab Professor Trelawney's sherry store [ours: a nod to HBP 25] north range, 13 by 13 m
ac A spiral stair between the floors [ours: PS 8: "a hundred and forty-two staircases"] north range, 16 by 5 m
ad Washrooms, girls' and boys' [ours] north range, 4 by 5 m

The castle's layout, the tower tops

The Architect, 12 October 2026, for Godric. Under 1.1, 2.1, 3.1 and Q48b's 3. North up; the bar 50 m. Numbers: the step 3 sheet's places (+ the canon sweep's); letters, purple: this sheet's fill, every space given a use.

Above the seventh: the tower tops

the dormitory at +43.8 m

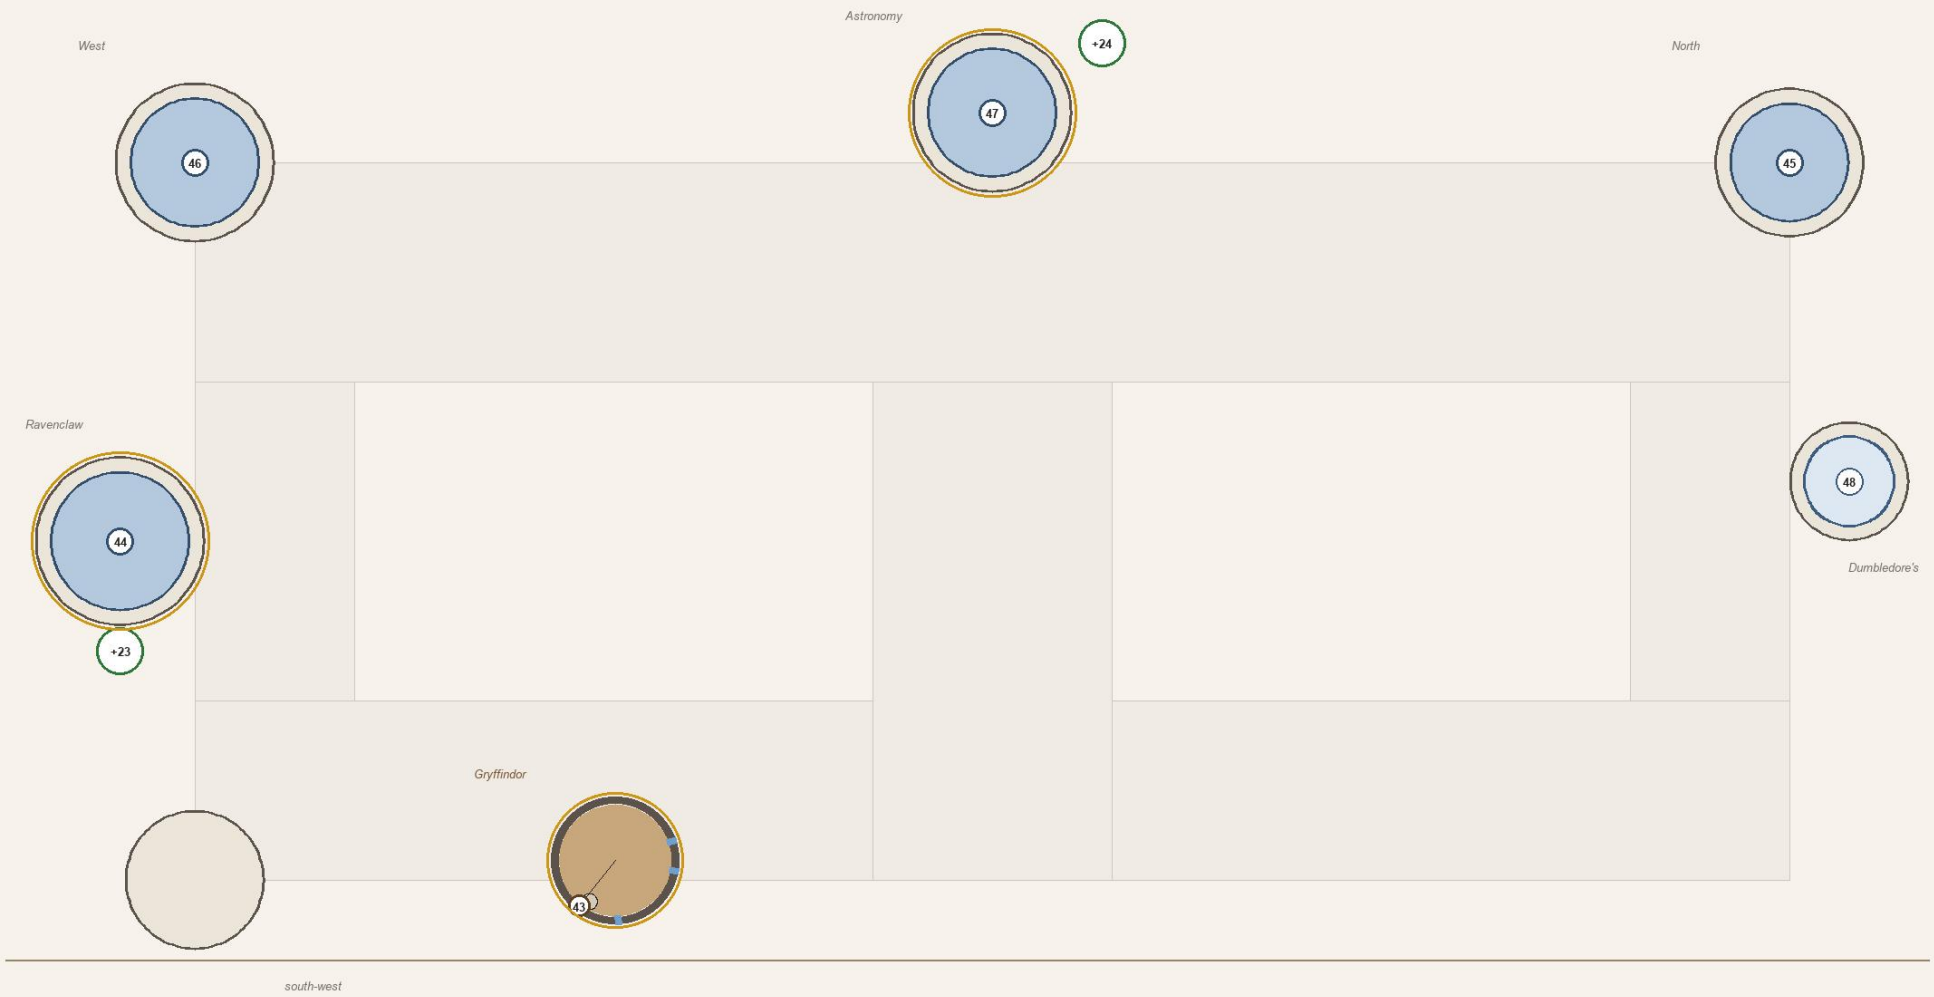





Named places on this floor (the step 3 sheet: numbers the first draft's, + the canon sweep's)

43 Gryffindor dormitory, 7.4 m above the common room [built] (PS 7)
44 Ravenclaw common room [books] (OotP 18, DH 29)
45 Divination, the top of the North Tower [books] (PoA 6, GoF 13)
46 The Owlery, the top of the West Tower [books] (GoF 15)
47 Astronomy Tower, the tallest, directly above the front doors [books] (PS 15, OotP 31)
48 Dumbledore's office [inferred] (CoS 12)
+24 The Astronomy Tower's ramparts, the parapet over the doors (HBP 27, OotP 31) [canon]
+23 Ravenclaw's tight spiral stair and the eagle door (DH 29) [canon]

The towers at this level

Astronomy Tower: the Astronomy classroom and ramparts (47, +24)
Ravenclaw Tower: Ravenclaw common room and dormitories (44)
Gryffindor Tower: the dormitories (43)
West Tower: the Owlery (46)
North Tower: Divination, through the trapdoor (45)
south-west tower: a lookout over the lake (ours)
Dumbledore's tower: the Headmaster's office (48)