The disposition of the agreed layout's rooms, by floor (model v238, layout v71), sheet 1 of 5

Wall rule applied: inner walls 0.5, outer walls outward. Now: the room's state in the model today. Disposition: built; as drawn; trimmed round a kept room; follows a room the model holds elsewhere; reimagine (cannot be built as the layout drew it).

Cellars and dungeons (B): 51 built; 2 true voids, 12 thick walls

Code	Layout room	m2	Now	Disposition	Note
5	Dungeon corridors, the deathday party (t	1248	built otherwise	built	as dungeon-corridor, hall-undercroft, founders-unde
1	Kitchens: four long tables, each exactly	900	built	built	as kitchens
3	Slytherin common room: the dungeons, und	384	built	built	as slytherin-common-room
4	Potions classroom, down in a dungeon (th	384	built	built	as potions-classroom-b
2	Hufflepuff's basement corridor, which al	168	partly 72%	built	as hufflepuff-basement-corridor, kitchens-corridor,
r	The wizard chess room	161	built	built	as wizard-chess-room
n	The dungeon store of old benches and des	161	built	built	as dungeon-bench-store
v	The suits of armour's spare parts	161	built	built	as armour-spare-parts-store
l	Coal and log store for the castle's fire	148	built	built	as coal-and-log-store
q	The house banners and feast linen	148	built	built	as banner-and-linen-store
af	The prefects' patrol room	148	built	built	as prefects-patrol-room
o	A dungeon for detentions	148	built	built	as detention-dungeon
u	The Christmas decorations, a dozen trees	148	built	built	as christmas-decorations-store
aj	A store	136	built	built	as service-store-b
ae	Portraits stacked, waiting for walls	132	built	built	as portraits-store
ad	Potions dungeon for the N.E.W.T. years	132	built otherwise	built	as potions-classroom-b, potions-dungeon-newt
y	Peeves's den of stolen chalk	132	built	built	as peeves-chalk-den
ab	A practice room for spells gone wrong	132	built	built	as spell-practice-room
x	Potions dungeon for the O.W.L. years	132	built otherwise	built	as potions-classroom-b, potions-dungeon-owl
aa	Dungeon five, where the frog brains went	132	built otherwise	built	as potions-classroom-b
w	The Potions ingredients store	130	built	built	as potions-ingredients-store
ak	A store	75	built	built	as east-corner-store-b
t	A ghosts' gathering room, cold all year	55	built	built	as ghosts-gathering-room
f	The cold room for the feasts	55	built	built	as feast-cold-room
g	The house-elves' quarters	55	built	built	as house-elves-quarters
h	The kitchen stores: flour, sugar, the pu	55	built	built	as kitchen-stores
i	The brewing cellar, where slow potions s	55	built	built	as brewing-cellar
m	Filch's store of confiscated things	55	built	built	as caretakers-confiscations-store
p	The store of spare cauldrons	55	built	built	as spare-cauldrons-store
e	The scullery	55	built	built	as scullery
j	The cellar of butterbeer and pumpkin jui	55	built	built	as butterbeer-cellar
s	The quill, ink and parchment store	55	built	built	as quill-ink-store
z	The candle store for the Great Hall	55	built	built	as candle-store
ag	The school's spare robes	55	built	built	as spare-robes-store
ac	The laundry, by the kitchens	52	built	built	as laundry, secret-s3
ah	The kitchens' bakery ovens	52	built	built	as bakery-ovens
k	A broom cupboard	46	built	built	as broom-cupboard
d	Washrooms, girls' and boys'	42	built	built	as washrooms-sw
c	The south-west tower's stair foot, a sta	35	built	built	as sw-stair-foot-b
ai	A store of spare desks and chairs	34	built	built	as spare-desks-store-b
b	The North Tower's stair foot, a stair be	30	built	built	as north-stair-foot-b
a	The West Tower's stair foot, a stair bet	28	built	built	as west-stair-foot-b
+1	Snape's office, halfway down the cold pa	20	built	built	as snape-office
c1	corridor	285	built	built	as service-corridor-b
c2	corridor	184	built	built	as lake-corridor-b-east
c3	corridor	96	built otherwise	built	as potions-classroom-b, potions-link-corridor
c4	corridor	96	built	built	as east-wing-corridor-b
c5	corridor	86	built	built	as lake-corridor-b-west
c6	corridor	58	built	built	as lake-corridor-b-keep
c7	corridor	33	built	built	as west-stair-corridor-b, west-stair-foot-b
c8	corridor	13	built	built	as old-cells-passage

Ground floor (G): 50 built, 1 follows; 14 true voids, 33 thick walls

Code	Layout room	m2	Now	Disposition	Note
v	A service passage	14	missing	follows	hung on 14, which stands as staff-room
11	Great Hall, through a doorway to the rig	900	built	built	as great-hall
8	Entrance Hall, its front doors in the no	480	built	built	as entrance-hall
h	The girls' toilets by the Great Hall's w	279	built otherwise	built	as peeves-lumber-room, girls-toilets-g, boys-toilet
p	The Quidditch teams' kit room	207	built	built	as quidditch-kit-room, drum-bend-g-west, kit-broom-
s	The Duelling Club's practice room	207	built	built	as duelling-practice-room, sw-corner-lobby-g
n	The post room, where the owls' parcels w	177	built	built	as post-room
t	The school archive of old registers	177	built	built	as registers-archive
g	A free classroom (Care of Magical Creatu	177	built	built	as free-classroom-g
k	The visitors' parlour, where parents wai	177	built	built	as visitors-parlour
q	The treatment room for Quidditch knocks	177	built	built	as treatment-room
12	The corridor of classrooms opposite the	156	built otherwise	built	as classroom-corridor, classroom-corridor-east
ab	The old trophies' overflow	132	built	built	as old-trophies-overflow
aa	The store of exam desks for the Great Ha	132	built	built	as exam-desks-store
x	The Herbology potting room and seed stor	132	built	built	as potting-room
z	Professor Sprout's study, by the greenho	132	built	built	as herbology-study-g
w	The house-elves' service stair from the	132	built	built	as elves-service-stair-g
y	The owl-treats store	132	built	built	as owl-treats-store
r	Classroom eleven, a forest room for Fire	132	built	built	as classroom-eleven
u	The staff dining room, behind the staff	132	built	built	as staff-dining-room
ac	A house-elves' linen room	132	built	built	as elves-linen-room-g
+11	The chamber off the Great Hall, behind t	121	built	built	as hall-chamber
13	Filch's office: Harry follows him "back	112	built otherwise	built	as filchs-office, filchs-store
14	The staff room: Harry goes "down" to it	112	built	built	as staff-dining-room, elves-linen-room-g
9	Marble staircase, facing the front doors	98	built otherwise	built	as stair hall
10	The small, empty chamber off the hall (t	96	built otherwise	built	as waiting-chamber, punishments-room
f	A Gryffindor storeroom at the tower's fo	85	built	built	as gryffindor-store-g
af	A teacher's study	75	built	built	as teachers-study-g
d	Washrooms, girls' and boys'	55	built	built	as washrooms-g-north
e	Washrooms, girls' and boys'	55	built	built	as washrooms-g-east
ad	Staff bedroom	55	built	built	as staff-bedroom-g
m	The cloakroom, wet boots and cloaks	47	built	built	as cloakroom-g
l	The porters' lodge by the front doors	47	built	built	as porters-lodge
o	Madam Hooch's store of school brooms	47	built	built	as school-brooms-store
c	Washrooms, girls' and boys'	42	built	built	as washrooms-g
b	The south-west tower's stair foot, a sta	35	built	built	as sw-stair-foot-g
a	The North Tower's stair foot, a stair be	30	built	built	as north-stair-foot-g
j	A store of spare desks and chairs	28	built	built	as spare-desks-store, entrance-hall
ae	A linen cupboard	28	built	built	as linen-cupboard-g-west
i	A broom cupboard	21	partly 54%	built	as hall-slot-cupboard, entrance-hall, great-hall (5
+12	The broom cupboard across the hall	2	built	built	as hall-cupboard
c1	corridor	184	built	built	as lake-corridor-g-east
c2	corridor	97	built	built	as classroom-corridor-east
c3	corridor	96	built	built	as west-wing-corridor-g
c4	corridor	96	built	built	as east-wing-corridor-g
c5	corridor	86	built	built	as lake-corridor-g-west
c6	corridor	60	built	built	as gate-passage
c7	corridor	58	built	built	as lake-corridor-g-mid
c8	corridor	21	built	built	as staff-passage
c9	corridor	12	built	built	as hall-chamber-way, hall-chamber
c10	corridor	9	built otherwise	built	as great-hall-doors-passage

First floor (1): 51 built, 2 follows; 10 true voids, 51 thick walls

Code	Layout room	m2	Now	Disposition	Note
c8	corridor	41	missing	follows	it lies in the walls of the rooms beside it
c17	corridor	6	missing	follows	it lies in the walls of the rooms beside it
15	The moving staircases and the marble sta	1200	built otherwise	built	as stair hall
17	Transfiguration classroom, beside her st	432	built otherwise	built	as history-of-magic-classroom, linen-cupboard-1, hi
20	History of Magic classroom, "large enoug	392	built	built	as history-of-magic-lecture-hall, lake-corridor-1-e
19	Hospital wing: "up" from the dungeons; t	288	built otherwise	built	as hospital-wing, east-first-floor-corridor, pomfre
h	The History of Magic archive of old exam	279	built	built	as exam-papers-archive
m	Madam Pomfrey's dispensary	207	built	built	as west-dispensary
q	The hospital wing's quiet rooms	207	built	built	as quiet-rooms
o	Transfiguration store: cages of practice	161	built	built	as transfiguration-beast-store

The disposition of the agreed layout's rooms, by floor (model v238, layout v71), sheet 2 of 5

Wall rule applied: inner walls 0.5, outer walls outward. Now: the room's state in the model today. Disposition: built; as drawn; trimmed round a kept room; follows a room the model holds elsewhere; reimagine (cannot be built as the layout drew it).

l	Professor Binns's study, never used	161	built	**built**	as history-teachers-study
s	Professor McGonagall's rooms	161	built	**built**	as transfiguration-teachers-rooms
j	Transfiguration classroom for the N.E.W.	156	built	**built**	as newt-transfiguration-classroom
x	The Deputy Head's records room	132	built	**built**	as deputy-heads-records-room
t	The classroom with the chandelier	132	built	**built**	as chandelier-classroom
v	An empty classroom off the first-floor c	132	built	**built**	as empty-classroom-1
+8	The first-floor room over Filch's office	112	built	**built**	as room-over-caretakers-office
16	McGonagall's study, first floor (off the	96	built otherwise	**built**	as washrooms-1-east, transfiguration-teachers-study
k	A broom cupboard	95	built	**built**	as broom-cupboard-1
y	A teacher's study	91	built	**built**	as teachers-study-1
g	A Gryffindor storeroom at the tower's fo	85	built	**built**	as gryffindor-tower-storeroom
aa	The staff library	75	built	**built**	as staff-library
p	A linen cupboard	65	built	**built**	as linen-cupboard-1
n	A store of spare desks and chairs	47	built	**built**	as spare-desks-store-1, history-of-magic-passage
u	A store of old textbooks	45	built	**built**	as old-textbooks-store, hospital-passage
e	Washrooms, girls' and boys'	43	built	**built**	as washrooms-1-gate
f	Washrooms, girls' and boys'	43	built	**built**	as washrooms-1-east
d	Washrooms, girls' and boys'	42	built	**built**	as washrooms-1-south-west
b	The North Tower's stair foot, a stair be	41	built	**built**	as north-stair-foot-1
a	The West Tower's stair foot, a stair bet	40	built	**built**	as west-stair-foot-1
z	A store	38	built	**built**	as store-1-west
c	The south-west tower's stair foot, a sta	35	built	**built**	as sw-stair-foot-1
w	The hospital wing's linen room	32	built	**built**	as west-linen-room
r	Filch's cleaning cupboard	26	built	**built**	as cleaning-cupboard-1
ac	A passage to the rooms behind	12	partly 73%	**built**	as passage-to-rooms-behind-1, entrance-hall (73% of
i	A service passage	11	built	**built**	as service-passage-1
ab	A passage to the rooms behind	11	built	**built**	as passage-behind-west-1
ad	A passage to the rooms behind	11	built otherwise	**built**	as mcgonagall-landing-passage-1
c1	corridor	205	built	**built**	as first-floor-corridor
c2	corridor	100	built otherwise	**built**	as lake-corridor-1-east
c3	corridor	96	built	**built**	as east-first-floor-corridor
c4	corridor	96	built	**built**	as west-range-corridor-1
c5	corridor	86	built	**built**	as lake-corridor-1-west
c6	corridor	58	built	**built**	as lake-corridor-1-mid
c7	corridor	45	built	**built**	as west-cross-corridor-1
c9	corridor	37	built	**built**	as transfiguration-passage
c10	corridor	37	built	**built**	as history-of-magic-passage
c11	corridor	35	built	**built**	as hospital-passage
c12	corridor	12	partly 73%	**built**	as passage-to-rooms-behind-1, entrance-hall (73% of
c13	corridor	11	built	**built**	as passage-behind-west-1
c14	corridor	11	built otherwise	**built**	as mcgonagall-landing-passage-1
c15	corridor	9	partly 72%	**built**	as back-stair-corridor-1, entrance-hall, great-hall
c16	corridor	6	built otherwise	**built**	as mcgonagall-landing-passage-1

Second floor (2): 57 built, 1 reimagine; 11 true voids, 37 thick walls

Code	Layout room	m2	Now	Disposition	Note
18	Myrtle's bathroom, the Chamber's door: t	160	partly 48%	**reimagine**	a smaller room, 44 of 160 m2: 11.9 x 3.7 m left by
p	The Gobstones Club room	177	built	**built**	as gobstones-club-room
v	Staff bedrooms	177	built	**built**	as staff-bedrooms-2-east
h	Lockhart's office, later a Defence spare	177	built	**built**	as defence-office-2-north
k	Slughorn's office, larger inside than ou	177	built	**built**	as teachers-office-2-north
s	A duelling practice room	177	built	**built**	as duelling-practice-room-2
o	The Slug Club's dining room	168	built	**built**	as slug-club-dining-room, astronomy-stair-foot-2
t	The map room	168	built	**built**	as map-room, girls-washroom-2
af	A disused classroom	168	built	**built**	as disused-classroom-2-east, second-years-study-roo
q	The second-floor girls' washroom, the on	168	built	**built**	as girls-washroom-2
u	A second years' study room	168	built	**built**	as second-years-study-room
aa	Staff bedroom	155	partly 60%	**built**	as staff-bedroom-2-east (60% of it; the rest read w
ad	A house-elves' linen room	155	built	**built**	as elves-linen-room-2
ae	Staff bedroom	132	built	**built**	as staff-bedroom-2-west
y	A teacher's study	132	built	**built**	as teachers-study-2-west
ab	A study room	132	built	**built**	as study-room-2-west
x	A disused classroom	130	built	**built**	as disused-classroom-2-northwest
r	A store of old textbooks	128	built	**built**	as old-textbooks-store-2
+4	The second-floor corridor by Myrtle's do	96	built	**built**	as second-floor-east-corridor
ag	A teacher's study	91	built	**built**	as teachers-study-2-southwest
i	A broom cupboard	81	built	**built**	as broom-cupboard-2-middle
aj	A teacher's study	75	built	**built**	as teachers-study-2-southeast
g	The Astronomy Tower's stair foot, its st	60	built	**built**	as astronomy-stair-foot-2
m	A linen cupboard	52	built	**built**	as linen-cupboard-2
n	Filch's cleaning cupboard	48	built	**built**	as cleaning-cupboard-2
e	Washrooms, girls' and boys'	43	built	**built**	as washrooms-2-north
f	Washrooms, girls' and boys'	43	built	**built**	as washrooms-2-east
d	Washrooms, girls' and boys'	42	built	**built**	as washrooms-2-west
b	The North Tower's stair foot, a stair be	41	built	**built**	as north-stair-foot-2
a	The West Tower's stair foot, a stair bet	40	built	**built**	as west-stair-foot-2
l	A store of spare desks and chairs	38	built	**built**	as spare-desks-store-2-middle
ah	A broom cupboard	38	built	**built**	as broom-cupboard-2-west
c	The south-west tower's stair foot, a sta	35	built	**built**	as sw-stair-foot-2
ac	A store	32	built	**built**	as store-2-southwest
ai	A store of spare desks and chairs	30	built	**built**	as spare-desks-store-2-east
z	A service passage	25	built	**built**	as service-passage-2-east, myrtles-bathroom
+5	The Defence office, its corridor's suit	20	built	**built**	as defence-office
w	A lamp and candle cupboard	18	built	**built**	as lamp-candle-cupboard-2
ap	A passage to the rooms behind	14	built	**built**	as passage-2-east
j	A service passage	11	built	**built**	as service-passage-2-lobby, back-stair-lobby-2
ak	A passage to the rooms behind	11	built	**built**	as passage-2-west
al	A passage to the rooms behind	11	built	**built**	as passage-2-linen
am	A passage to the rooms behind	11	built	**built**	as passage-2-gate
an	A passage to the rooms behind	11	built	**built**	as passage-2-middle
ao	A passage to the rooms behind	11	built	**built**	as passage-2-study
c1	corridor	285	built	**built**	as north-range-corridor-2
c2	corridor	184	built	**built**	as lake-corridor-2-east
c3	corridor	156	built	**built**	as second-floor-corridor
c4	corridor	96	built	**built**	as west-wing-corridor-2
c5	corridor	86	built otherwise	**built**	as unused-classroom-2-west, lake-workroom-2-west, c
c6	corridor	58	built otherwise	**built**	as unused-classroom-2-east, defence-sitting-room, d
c7	corridor	45	built	**built**	as west-corridor-2-south
c8	corridor	14	built	**built**	as passage-2-east
c9	corridor	11	built	**built**	as passage-2-west
c10	corridor	11	built	**built**	as passage-2-linen
c11	corridor	11	built	**built**	as passage-2-gate
c12	corridor	11	built	**built**	as passage-2-middle
c13	corridor	11	built	**built**	as passage-2-study

Third floor (3): 65 built, 1 reimagine, 1 follows; 10 true voids, 37 thick walls

Code	Layout room	m2	Now	Disposition	Note
aq	A passage to the rooms behind	14	partly 31%	**reimagine**	a thick wall, 0.6 x 4.7 m left by stone-bay
c14	corridor	14	partly 31%	follows	its ground is now stone-bay and their walls
23	The forbidden corridor: "the third-floor	448	built	**built**	as right-hand-corridor-3
25	Charms classroom: near the forbidden cor	432	built otherwise	**built**	as charms-classroom-3-west, store-3-east, charms-pa
22	Defence Against the Dark Arts classroom:	360	built otherwise	**built**	as defence-practice-room-3, defence-classroom, lamp
24	Trophy room, third floor (the spot propo	320	built	**built**	as trophy-room
i	Staff bedrooms	279	built	**built**	as staff-bedrooms-3-lake, drum-bend-3-east, staff-b
u	The armour gallery's repair room	207	built	**built**	as armour-repair-room-3, drum-bend-3-west, armour-r
ab	The trophy room's polishing room	207	built	**built**	as trophy-polishing-room-3
s	The swivelling staircase	203	built	**built**	as swivelling-staircase-room-3
h	A third years' study room	174	built	**built**	as third-years-study-room-3
y	A disused classroom	174	built	**built**	as disused-classroom-3-lake
ac	A teacher's study	174	built	**built**	as teachers-study-3-lake-east

The disposition of the agreed layout's rooms, by floor (model v238, layout v71), sheet 3 of 5

Wall rule applied: inner walls 0.5, outer walls outward. Now: the room's state in the model today. Disposition: built; as drawn; trimmed round a kept room; follows a room the model holds elsewhere; reimagine (cannot be built as the layout drew it).

m	Staff bedroom	174	built	**built**	as staff-bedroom-3-lake
r	A study room	174	built	**built**	as study-room-3-lake
z	The Defence practice room, for jinxes an	169	built	**built**	as defence-practice-room-3
ah	The room beside the trophy room	169	built	**built**	as room-beside-trophy-room-3
q	The Defence teacher's bedroom	160	built	**built**	as defence-teachers-bedroom-3
t	A teacher's study	160	built	**built**	as teachers-study-3-north
x	The Charms store: cushions, teacups and	160	built otherwise	**built**	as charms-store-3, charms-classroom-3-west, charms-
aa	Charms classroom for the N.E.W.T. years	160	built	**built**	as charms-classroom-3-west, charms-preparation-room
+17	The long gallery of armour, by the troph	156	built	**built**	as armour-gallery
ai	A study room	132	built otherwise	**built**	as right-hand-corridor-3
af	A teacher's study	132	built otherwise	**built**	as right-hand-corridor-3, teachers-study-3-east
ag	Staff bedroom	132	built otherwise	**built**	as right-hand-corridor-3
w	A store	127	built	**built**	as store-3-east, tapestry-passage-3-east
v	A lamp and candle cupboard	126	built	**built**	as lamp-candle-cupboard-3, tapestry-passage-3-west
g	A Gryffindor storeroom at the tower's fo	85	built	**built**	as gryffindor-storeroom-3
n	A linen cupboard	84	built	**built**	as linen-cupboard-3-west, tapestry-passage-3
j	A broom cupboard	81	built	**built**	as broom-cupboard-3-middle, tapestry-passage-3-east
al	A house-elves' linen room	75	built	**built**	as elves-linen-room-3-east
ae	A store of spare desks and chairs	65	built	**built**	as spare-desks-store-3-west, tapestry-passage-3-wes
f	The Astronomy Tower's stair foot, its st	60	built	**built**	as astronomy-stair-foot-3
o	Filch's cleaning cupboard	52	built	**built**	as cleaning-cupboard-3-lobby
c	Washrooms, girls' and boys'	42	built	**built**	as washrooms-3-trophy
a	The North Tower's stair foot, a stair be	41	built	**built**	as north-stair-foot-3
p	A house-elves' linen room	41	built	**built**	as elves-linen-room-3-middle, tapestry-passage-3-ea
l	A store of spare desks and chairs	38	built	**built**	as spare-desks-store-3-middle, tapestry-passage-3-e
d	Washrooms, girls' and boys'	35	built	**built**	as washrooms-3-middle, tapestry-passage-3-east
e	Washrooms, girls' and boys'	35	partly 80%	**built**	as washrooms-3-east, stone-bay (80% of it; the rest
b	The south-west tower's stair foot, a sta	35	built	**built**	as sw-stair-foot-3
aj	A linen cupboard	30	built	**built**	as linen-cupboard-3-east
ak	Filch's cleaning cupboard	27	built	**built**	as cleaning-cupboard-3-west
ad	A broom cupboard	26	built	**built**	as broom-cupboard-3-east
26	The one-eyed witch's landing, directly b	24	built otherwise	**built**	as stair hall
ap	A passage to the rooms behind	12	partly 77%	**built**	as passage-3-charms, tapestry-passage-3-east (77% of
k	A service passage	11	partly 80%	**built**	as service-passage-3-lobby, tapestry-passage-3-east
am	A passage to the rooms behind	11	built otherwise	**built**	as passage-3-west, tapestry-passage-3-west
an	A passage to the rooms behind	11	partly 79%	**built**	as passage-3-middle, tapestry-passage-3-east (79% o
ao	A passage to the rooms behind	11	partly 79%	**built**	as passage-3-study, tapestry-passage-3-east (79% of
c1	corridor	184	built	**built**	as lake-corridor-3-east
c2	corridor	165	built	**built**	as charms-corridor
c3	corridor	156	built	**built**	as third-floor-north-corridor
c4	corridor	126	built otherwise	**built**	as tapestry-passage-3-east, tapestry-passage-3-west
c5	corridor	96	built otherwise	**built**	as right-hand-corridor-3, east-corridor-3-north
c6	corridor	86	built	**built**	as lake-corridor-3-west
c7	corridor	65	built	**built**	as north-corridor-3-link
c8	corridor	58	built	**built**	as lake-corridor-3-mid
c9	corridor	37	built	**built**	as charms-passage
c10	corridor	30	built	**built**	as defence-passage
c11	corridor	18	built	**built**	as west-wing-corridor-3
c12	corridor	15	built	**built**	as west-cross-corridor-3-end
c13	corridor	15	built	**built**	as west-cross-corridor-3
c15	corridor	12	partly 77%	**built**	as passage-3-charms, tapestry-passage-3-east (77% o
c16	corridor	11	built otherwise	**built**	as passage-3-west, tapestry-passage-3-west
c17	corridor	11	partly 79%	**built**	as passage-3-middle, tapestry-passage-3-east (79% o
c18	corridor	11	partly 79%	**built**	as passage-3-study, tapestry-passage-3-east (79% of

Fourth floor (4): 62 built; 10 true voids, 27 thick walls

Code	Layout room	m2	Now	Disposition	Note
27	Library, the Restricted Section at the b	936	built otherwise	**built**	as library, fourth-floor-corridor, ancient-runes-cl
j	The newspaper room: back issues of the P	279	built	**built**	as newspaper-room-4
r	A house-elves' linen room	207	built	**built**	as elves-linen-room-4-lake
x	Staff bedroom	207	built	**built**	as staff-bedroom-4-lake-west
i	The landscape painting's corridor	174	built	**built**	as landscape-painting-corridor-4
u	A disused classroom	174	built	**built**	as disused-classroom-4-lake-east
y	A study room	174	built	**built**	as study-room-4-lake-east
m	Revision rooms for the exam years	174	built	**built**	as revision-rooms-4
p	The Muggle Studies collection: plugs and	174	built	**built**	as muggle-studies-collection-4
o	The Herbology library: books that bite	168	built	**built**	as herbology-library-4
t	Staff bedroom	168	built	**built**	as staff-bedroom-4-north-east
ah	A study room	168	built	**built**	as study-room-4-north-east
q	Staff bedrooms	168	built	**built**	as staff-bedrooms-4-north
w	A teacher's study	168	built	**built**	as teachers-study-4-north
ag	A disused classroom	132	built	**built**	as disused-classroom-4-east
af	The Ancient Runes store of tablets and s	132	built	**built**	as runes-store-4
ac	A house-elves' linen room	132	built	**built**	as elves-linen-room-4-east
ae	Staff bedroom	132	built	**built**	as staff-bedroom-4-east
ab	The Ancient Runes teacher's study	132	built	**built**	as runes-teachers-study-4
ad	The fourth-floor toilet	132	built	**built**	as fourth-floor-washroom
s	Filch's cleaning cupboard	128	built	**built**	as cleaning-cupboard-4, elves-passage-4
29	The unused classroom with the Mirror of	120	built otherwise	**built**	as unused-classroom-4-mirror, north-range-corridor-
k	A broom cupboard	86	built otherwise	**built**	as unused-classroom-4-mirror, elves-passage-4, broo
h	A Gryffindor storeroom at the tower's fo	85	built	**built**	as gryffindor-storeroom-4
ak	A teacher's study	75	built	**built**	as teachers-study-4-lake-east
v	A store of old textbooks	63	built	**built**	as old-textbooks-store-4
aa	A store	62	built	**built**	as store-4-west
g	The Astronomy Tower's stair foot, its st	60	built	**built**	as astronomy-stair-foot-4
28	The Muggle Studies room, past the last s	48	built otherwise	**built**	as library-corridor, back-stair-lobby-4, library-re
n	A linen cupboard	48	built	**built**	as linen-cupboard-4, elves-passage-4
d	Washrooms, girls' and boys'	42	built	**built**	as washrooms-4-west
b	The North Tower's stair foot, a stair be	41	built	**built**	as north-stair-foot-4
a	The West Tower's stair foot, a stair bet	40	built	**built**	as west-stair-foot-4
l	A store of spare desks and chairs	38	built	**built**	as spare-desks-store-4-middle, elves-passage-4
e	Washrooms, girls' and boys'	35	built	**built**	as washrooms-4-north, elves-passage-4
of	Washrooms, girls' and boys'	35	built	**built**	as washrooms-4-east, elves-passage-4
c	The south-west tower's stair foot, a sta	35	built	**built**	as sw-stair-foot-4
ai	A broom cupboard	32	built	**built**	as broom-cupboard-4-west
aj	A store of spare desks and chairs	30	built	**built**	as spare-desks-store-4-east, north-stair-foot-4
z	A lamp and candle cupboard	18	built	**built**	as lamp-candle-cupboard-4, elves-passage-4
ap	A passage to the rooms behind	14	built otherwise	**built**	as passage-4-east, north-stair-foot-4
al	A passage to the rooms behind	11	built	**built**	as passage-4-west
am	A passage to the rooms behind	11	partly 79%	**built**	as passage-4-gate, elves-passage-4 (79% of it; the
an	A passage to the rooms behind	11	partly 79%	**built**	as passage-4-middle, elves-passage-4 (79% of it; th
ao	A passage to the rooms behind	11	partly 79%	**built**	as passage-4-study, elves-passage-4 (79% of it; the
c1	corridor	267	built	**built**	as north-range-corridor-4
c2	corridor	184	built	**built**	as lake-corridor-4-east
c3	corridor	156	built	**built**	as fourth-floor-corridor
c4	corridor	96	built	**built**	as west-wing-corridor-4
c5	corridor	96	built	**built**	as east-wing-corridor-4
c6	corridor	86	built	**built**	as lake-corridor-4-west
c7	corridor	84	built	**built**	as elves-passage-4
c8	corridor	58	built	**built**	as lake-corridor-4-keep
c9	corridor	54	built	**built**	as library-corridor, back-stair-lobby-4
c10	corridor	48	built	**built**	as west-corridor-4-south
c11	corridor	36	built	**built**	as electives-passage-4
c12	corridor	14	built otherwise	**built**	as passage-4-east, north-stair-foot-4
c13	corridor	11	built	**built**	as passage-4-west
c14	corridor	11	partly 79%	**built**	as passage-4-gate, elves-passage-4 (79% of it; the
c15	corridor	11	partly 79%	**built**	as passage-4-middle, elves-passage-4 (79% of it; th
c16	corridor	11	partly 79%	**built**	as passage-4-study, elves-passage-4 (79% of it; the
c17	corridor	5	built	**built**	as sw-turret-passage

The disposition of the agreed layout's rooms, by floor (model v238, layout v71), sheet 4 of 5

Wall rule applied: inner walls 0.5, outer walls outward. Now: the room's state in the model today. Disposition: built; as drawn; trimmed round a kept room; follows a room the model holds elsewhere; reimagine (cannot be built as the layout drew it).

Fifth floor (5): 62 built; 13 true voids, 34 thick walls

Code	Layout room	m2	Now	Disposition	Note
32	The east wing, named on the fifth floor	512	built	**built**	as east-wing-5
j	The Head Boy and Head Girl's study	279	built	**built**	as head-boy-girl-study-5, drum-bend-5-east
31	Prefects' bathroom, by Boris the Bewilde	224	built	**built**	as prefects-bathroom
v	The girls' dormitories' linen store	207	built	**built**	as dormitory-linen-store-5, drum-bend-5-west, true-
ab	Staff bedroom	207	built	**built**	as staff-bedroom-5-west, sw-corner-lobby-5
s	The music room	177	built	**built**	as music-room-5
ad	A disused classroom	177	built	**built**	as disused-classroom-5-east
i	The fifth-floor corridor of armour, to a	177	built	**built**	as armour-corridor-5
m	The O.W.L. examiners' rooms	177	built	**built**	as owl-examiners-rooms-5
x	Staff bedrooms	177	built	**built**	as staff-bedrooms-5-east
r	Professor Sinistra's star-chart room	168	built	**built**	as star-chart-room-5
y	Staff bedroom	168	built	**built**	as staff-bedroom-5-east
ai	A teacher's study	168	built	**built**	as teachers-study-5-east
t	The ledgers of house points	168	built	**built**	as house-points-ledgers-5
z	A study room	168	built	**built**	as study-room-5
aa	A teacher's study	162	built	**built**	as teachers-study-5-southwest
ah	A disused classroom	162	built	**built**	as disused-classroom-5-west
w	A store	128	built	**built**	as store-5-east, elves-passage-5
ag	A teacher's study	124	built	**built**	as teachers-study-5-west
ac	A house-elves' linen room	119	built	**built**	as elves-linen-room-5
al	A teacher's study	100	built	**built**	as teachers-study-5-middle
af	The prefects' common room	99	built	**built**	as prefects-common-room
h	A Gryffindor storeroom at the tower's fo	85	built	**built**	as gryffindor-storeroom-5
o	A linen cupboard	84	built	**built**	as linen-cupboard-5
u	A lamp and candle cupboard	84	built	**built**	as lamp-candle-cupboard-5
k	A broom cupboard	81	built	**built**	as broom-cupboard-5-middle, elves-passage-5
am	A teacher's study	75	built	**built**	as teachers-study-5-southeast
g	The Astronomy Tower's stair foot, its st	60	built	**built**	as astronomy-stair-foot-5
p	Filch's cleaning cupboard	52	built	**built**	as cleaning-cupboard-5-middle
q	A store of old textbooks	48	built	**built**	as old-textbooks-store-5, elves-passage-5
d	Washrooms, girls' and boys'	42	built	**built**	as washrooms-5-west
b	The North Tower's stair foot, a stair be	41	built	**built**	as north-stair-foot-5
a	The West Tower's stair foot, a stair bet	40	built	**built**	as west-stair-foot-5
n	A store of spare desks and chairs	38	built	**built**	as spare-desks-store-5-middle, elves-passage-5
aj	A linen cupboard	38	built	**built**	as linen-cupboard-5-west
e	Washrooms, girls' and boys'	35	built	**built**	as washrooms-5-north, elves-passage-5
f	Washrooms, girls' and boys'	35	built	**built**	as washrooms-5-east, elves-passage-5
c	The south-west tower's stair foot, a sta	35	built	**built**	as sw-stair-foot-5
ak	Filch's cleaning cupboard	30	built	**built**	as cleaning-cupboard-5-east, north-stair-foot-5
ae	A store of spare desks and chairs	18	built	**built**	as spare-desks-store-5-east, elves-passage-5
at	A passage to the rooms behind	14	built otherwise	**built**	as passage-5-east, north-stair-foot-5
l	A service passage	11	partly 80%	**built**	as service-passage-5-lobby, elves-passage-5, back-s
an	A passage to the rooms behind	11	built	**built**	as passage-5-west
ao	A passage to the rooms behind	11	built	**built**	as passage-5-southwest
ap	A passage to the rooms behind	11	partly 79%	**built**	as passage-5-cleaning, elves-passage-5 (79% of it;
aq	A passage to the rooms behind	11	partly 79%	**built**	as passage-5-astronomy, elves-passage-5 (79% of it;
ar	A passage to the rooms behind	11	partly 79%	**built**	as passage-5-middle, elves-passage-5 (79% of it; th
as	A passage to the rooms behind	11	partly 79%	**built**	as passage-5-study, elves-passage-5 (79% of it; the
c1	corridor	480	built	**built**	as north-range-corridor-5
c2	corridor	184	built	**built**	as lake-corridor-5-east
c3	corridor	86	built	**built**	as lake-corridor-5-west
c4	corridor	84	built	**built**	as elves-passage-5
c5	corridor	58	built	**built**	as fifth-floor-south-corridor
c6	corridor	30	built	**built**	as west-wing-corridor-5-south
c7	corridor	24	built	**built**	as west-wing-corridor-5-north
c8	corridor	14	built otherwise	**built**	as passage-5-east, north-stair-foot-5
c9	corridor	11	built	**built**	as passage-5-west
c10	corridor	11	built	**built**	as passage-5-southwest
c11	corridor	11	partly 79%	**built**	as passage-5-cleaning, elves-passage-5 (79% of it;
c12	corridor	11	partly 79%	**built**	as passage-5-astronomy, elves-passage-5 (79% of it;
c13	corridor	11	partly 79%	**built**	as passage-5-middle, elves-passage-5 (79% of it; th
c14	corridor	11	partly 79%	**built**	as passage-5-study, elves-passage-5 (79% of it; the

Sixth floor (6): 71 built; 16 true voids, 36 thick walls

Code	Layout room	m2	Now	Disposition	Note
j	The clock room, where the castle's clock	279	partly 80%	**built**	as clock-room-6, lake-corridor-6-turn, drum-bend-6-
33	Arithmancy classroom (proposed); the six	252	built otherwise	**built**	as arithmancy-classroom, arithmancy-marking-room-6,
t	A teacher's study	208	built otherwise	**built**	as scroll-hall
ab	A study room	208	built otherwise	**built**	as study-room-6-west, scroll-hall
al	Staff bedroom	208	built	**built**	as staff-bedroom-6-west
s	Staff bedrooms	177	built	**built**	as staff-bedrooms-6-lake
ad	A house-elves' linen room	177	built	**built**	as elves-linen-room-6-lake
i	The frog choir's practice room	177	built	**built**	as frog-choir-room-6
m	Guest rooms for visiting parents	177	built	**built**	as guest-rooms-6
y	A disused classroom	177	built	**built**	as disused-classroom-6-east
r	A teacher's study	168	built	**built**	as teachers-study-6-middle
z	A teacher's study	168	built	**built**	as teachers-study-6-east
ao	Staff bedroom	168	built	**built**	as staff-bedroom-6-east
v	Staff bedroom	168	built	**built**	as staff-bedroom-6-middle
ac	A disused classroom	168	built	**built**	as disused-classroom-6-middle
an	A house-elves' linen room	132	built	**built**	as elves-linen-room-6-east-wing
am	A study room	132	built	**built**	as study-room-6-west-wing
ai	Staff bedroom	132	built	**built**	as staff-bedroom-6-east-wing
ak	A teacher's study	132	built	**built**	as teachers-study-6-east-wing
ah	Arithmancy room for the N.E.W.T. years	132	built	**built**	as arithmancy-room-6
aj	A disused classroom	132	built	**built**	as disused-classroom-6-west-wing
af	The Arithmancy store of number charts	130	partly 72%	**built**	as arithmancy-chart-store-6, sw-corner-lobby-6 (72%
x	A store	128	built	**built**	as store-6-middle, elves-passage-6
ar	A teacher's study	100	built	**built**	as teachers-study-6-astronomy
w	Professor Vector's study	92	built otherwise	**built**	as vectors-study-6, drum-bend-6-west, arithmancy-re
h	A Gryffindor storeroom at the tower's fo	85	built	**built**	as gryffindor-storeroom-6
k	A broom cupboard	81	built	**built**	as broom-cupboard-6-middle, elves-passage-6
+13	A boys' bathroom on the sixth floor, the	80	built otherwise	**built**	as scroll-hall
aa	A broom cupboard	78	built	**built**	as broom-cupboard-6-west, elves-passage-6-west
ag	A linen cupboard	78	built	**built**	as linen-cupboard-6, elves-passage-6-west
as	A teacher's study	75	built	**built**	as teachers-study-6-lake-east
o	A house-elves' linen room	65	built	**built**	as elves-linen-room-6-middle, elves-passage-6-west
u	A lamp and candle cupboard	65	built	**built**	as lamp-candle-cupboard-6, elves-passage-6-west
g	The Astronomy Tower's stair foot, its st	60	built	**built**	as astronomy-stair-foot-6
p	Filch's cleaning cupboard	52	built	**built**	as cleaning-cupboard-6-middle
q	A store of old textbooks	48	built	**built**	as old-textbooks-store-6-middle, elves-passage-6
d	Washrooms, girls' and boys'	42	built	**built**	as washrooms-6-west
b	The North Tower's stair foot, a stair be	41	built	**built**	as north-stair-foot-6
a	The West Tower's stair foot, a stair bet	40	built	**built**	as west-stair-foot-6
n	The telescope store	38	built	**built**	as telescope-store-6, elves-passage-6
ap	Filch's cleaning cupboard	38	built	**built**	as cleaning-cupboard-6-west, west-stair-foot-6
e	Washrooms, girls' and boys'	35	built	**built**	as washrooms-6-north, elves-passage-6
f	Washrooms, girls' and boys'	35	built	**built**	as washrooms-6-east, elves-passage-6
c	The south-west tower's stair foot, a sta	35	built	**built**	as sw-stair-foot-6
aq	A store of old textbooks	30	built	**built**	as old-textbooks-store-6-east, north-stair-foot-6
ae	A store of spare desks and chairs	18	built	**built**	as spare-desks-store-6, elves-passage-6
ba	A passage to the rooms behind	14	built otherwise	**built**	as passage-6-east, north-stair-foot-6
l	A service passage	11	partly 80%	**built**	as service-passage-6-lobby, elves-passage-6, back-s
at	A passage to the rooms behind	11	partly 79%	**built**	as passage-6-west, west-stair-foot-6, elves-passage
au	A passage to the rooms behind	11	partly 79%	**built**	as passage-6-west-middle, elves-passage-6-west (79%
av	A passage to the rooms behind	11	partly 80%	**built**	as passage-6-lobby-west, elves-passage-6-west, back
aw	A passage to the rooms behind	11	partly 79%	**built**	as passage-6-cleaning, elves-passage-6 (79% of it;
ax	A passage to the rooms behind	11	partly 79%	**built**	as passage-6-astronomy, elves-passage-6 (79% of it;

The disposition of the agreed layout's rooms, by floor (model v238, layout v71), sheet 5 of 5

Wall rule applied: inner walls 0.5, outer walls outward. Now: the room's state in the model today. Disposition: built; as drawn; trimmed round a kept room; follows a room the model holds elsewhere; reimagine (cannot be built as the layout drew it).


ay	A passage to the rooms behind	11	partly 79%	**built**	as passage-6-middle, elves-passage-6 (79% of it; th
az	A passage to the rooms behind	11	partly 79%	**built**	as passage-6-east-middle, elves-passage-6 (79% of i
c1	corridor	480	built	**built**	as north-range-corridor-6
c2	corridor	184	built	**built**	as lake-corridor-6-east
c3	corridor	144	built otherwise	**built**	as elves-passage-6, elves-passage-6-west
c4	corridor	96	built	**built**	as west-wing-corridor-6
c5	corridor	96	built	**built**	as east-wing-corridor-6
c6	corridor	86	built	**built**	as lake-corridor-6-west
c7	corridor	51	built	**built**	as lake-corridor-6-middle
c8	corridor	28	built	**built**	as arithmancy-passage
c9	corridor	14	built otherwise	**built**	as passage-6-east, north-stair-foot-6
c10	corridor	11	partly 79%	**built**	as passage-6-west, west-stair-foot-6, elves-passage
c11	corridor	11	partly 79%	**built**	as passage-6-west-middle, elves-passage-6-west (79%
c12	corridor	11	partly 80%	**built**	as passage-6-lobby-west, elves-passage-6-west, back
c13	corridor	11	partly 79%	**built**	as passage-6-cleaning, elves-passage-6 (79% of it;
c14	corridor	11	partly 79%	**built**	as passage-6-astronomy, elves-passage-6 (79% of it;
c15	corridor	11	partly 79%	**built**	as passage-6-middle, elves-passage-6 (79% of it; th
c16	corridor	11	partly 79%	**built**	as passage-6-east-middle, elves-passage-6 (79% of i

Seventh floor (7): 63 built; 10 true voids, 24 thick walls

Code	Layout room	m2	Now	Disposition	Note
r	Staff bedrooms	207	built	**built**	as staff-bedrooms-7
y	A house-elves' linen room	207	built	**built**	as linen-room-7-west
o	Professor Sinistra's study	188	built otherwise	**built**	as scroll-hall
s	A disused classroom	188	built otherwise	**built**	as scroll-hall
w	Staff bedroom	188	built	**built**	as staff-bedroom-7-north, scroll-hall
af	A teacher's study	188	built	**built**	as teachers-study-7-west
n	The corridor beneath the tallest tower	168	partly 73%	**built**	as astronomy-waiting-room-7, astronomy-corridor-7 (
u	A teacher's study	168	built	**built**	as teachers-study-7-east-a
ai	A teacher's study	168	built	**built**	as teachers-study-7-east-b
q	The Astronomy warming room, cocoa after	168	built	**built**	as astronomy-warming-room
x	A study room	168	built	**built**	as study-room-7-east
40	Room of Requirement on its own seventh-f	160	built otherwise	**built**	as staff-bedroom-7-north, scroll-hall, back-passage
ag	A house-elves' linen room	132	built	**built**	as linen-room-7-north-west
ab	Staff bedroom	132	built	**built**	as staff-bedroom-7-west
ae	A study room	132	built	**built**	as study-room-7-west
t	A store	128	built	**built**	as store-7-middle, elves-passage-7-east
ac	A disused classroom	112	partly 77%	**built**	as old-exam-hall-store, heads-corridor, old-exam-ha
ad	A teacher's study	112	built otherwise	**built**	as old-exam-hall, heads-corridor
ak	A teacher's study	100	built	**built**	as teachers-study-7-north
f	The Headmaster's guest rooms	91	built	**built**	as headmaster-guest-rooms-7
ah	Staff bedroom	87	built otherwise	**built**	as old-exam-hall, heads-corridor
h	A broom cupboard	81	built	**built**	as broom-cupboard-7-north-east, elves-passage-7
+2	Sir Cadogan's landing, at the top of the	80	built	**built**	as sir-cadogans-landing-7, seventh-floor-north-corr
v	A broom cupboard	73	built otherwise	**built**	as broom-cupboard-7-north-west, back-passage-7-west
aa	A house-elves' linen room	73	built	**built**	as linen-room-7-north, elves-passage-7-west
g	The seventh-floor broom cupboard	71	built	**built**	as broom-cupboard-7-south, headmaster-guest-sitting
k	A linen cupboard	70	built	**built**	as linen-cupboard-7, elves-passage-7-west
p	A lamp and candle cupboard	70	built otherwise	**built**	as lamp-candle-cupboard-7, elves-passage-7-west
41	Dumbledore's corridor and the lone gargo	70	built otherwise	**built**	as old-exam-hall, heads-corridor
e	The Astronomy Tower's stair foot, its st	60	built	**built**	as astronomy-stair-foot-7
l	Filch's cleaning cupboard	52	built	**built**	as caretakers-cleaning-cupboard-7
m	A store of old textbooks	48	built	**built**	as old-textbooks-store-7, elves-passage-7
c	Washrooms, girls' and boys'	42	built	**built**	as washrooms-7-sw
a	The West Tower's stair foot, a stair bet	40	built	**built**	as west-stair-foot-7
j	A store of spare desks and chairs	38	built otherwise	**built**	as desk-store-7, elves-passage-7, washrooms-7-north
aj	Filch's cleaning cupboard	38	built	**built**	as caretakers-cleaning-cupboard-7-west, west-stair-
d	Washrooms, girls' and boys'	35	built	**built**	as washrooms-7-north-east, seventh-floor-north-corr
b	The south-west tower's stair foot, a sta	35	built	**built**	as sw-stair-foot-7
z	Professor Trelawney's sherry store	29	built otherwise	**built**	as sherry-store-7, elves-passage-7-east
i	A service passage	11	built otherwise	**built**	as service-passage-7-lobby, elves-passage-7, back-s
al	A passage to the rooms behind	11	partly 79%	**built**	as passage-7-west-stair, west-stair-foot-7, elves-p
am	A passage to the rooms behind	11	built otherwise	**built**	as back-passage-7-west, passage-7-cupboard-row, elv
an	A passage to the rooms behind	11	built otherwise	**built**	as passage-7-back-stair, elves-passage-7-west, back
ao	A passage to the rooms behind	11	partly 78%	**built**	as passage-7-cleaning, elves-passage-7 (78% of it;
ap	A passage to the rooms behind	11	partly 77%	**built**	as passage-7-stair-hall, elves-passage-7 (77% of it
aq	A passage to the rooms behind	11	built	**built**	as warming-room-passage
ar	A passage to the rooms behind	11	built	**built**	as passage-7-east-middle, elves-passage-7-east
c1	corridor	234	built	**built**	as seventh-floor-north-corridor-east
c2	corridor	156	built	**built**	as room-corridor
c3	corridor	138	built otherwise	**built**	as elves-passage-7-west, elves-passage-7, elves-pas
c4	corridor	96	built	**built**	as west-range-corridor-7
c5	corridor	96	partly 52%	**built**	as old-exam-hall, old-exam-hall-store (52% of it; t
c6	corridor	86	built	**built**	as lake-corridor-7-west
c7	corridor	48	built	**built**	as west-corridor-7
c8	corridor	43	built	**built**	as north-tower-passage
c9	corridor	12	built otherwise	**built**	as seventh-floor-north-corridor-east
c10	corridor	11	partly 79%	**built**	as passage-7-west-stair, west-stair-foot-7, elves-p
c11	corridor	11	built otherwise	**built**	as back-passage-7-west, passage-7-cupboard-row, elv
c12	corridor	11	built otherwise	**built**	as passage-7-back-stair, elves-passage-7-west, back
c13	corridor	11	partly 78%	**built**	as passage-7-cleaning, elves-passage-7 (78% of it;
c14	corridor	11	partly 77%	**built**	as passage-7-stair-hall, elves-passage-7 (77% of it
c15	corridor	11	built	**built**	as warming-room-passage
c16	corridor	11	built	**built**	as passage-7-east-middle, elves-passage-7-east

Cellars and dungeons (B): the layout's rooms after the wall rule, the true voids flagged


51 built. Voids: V2 34 m2 (3.8 wide), V3 30 m2 (3.4 wide).

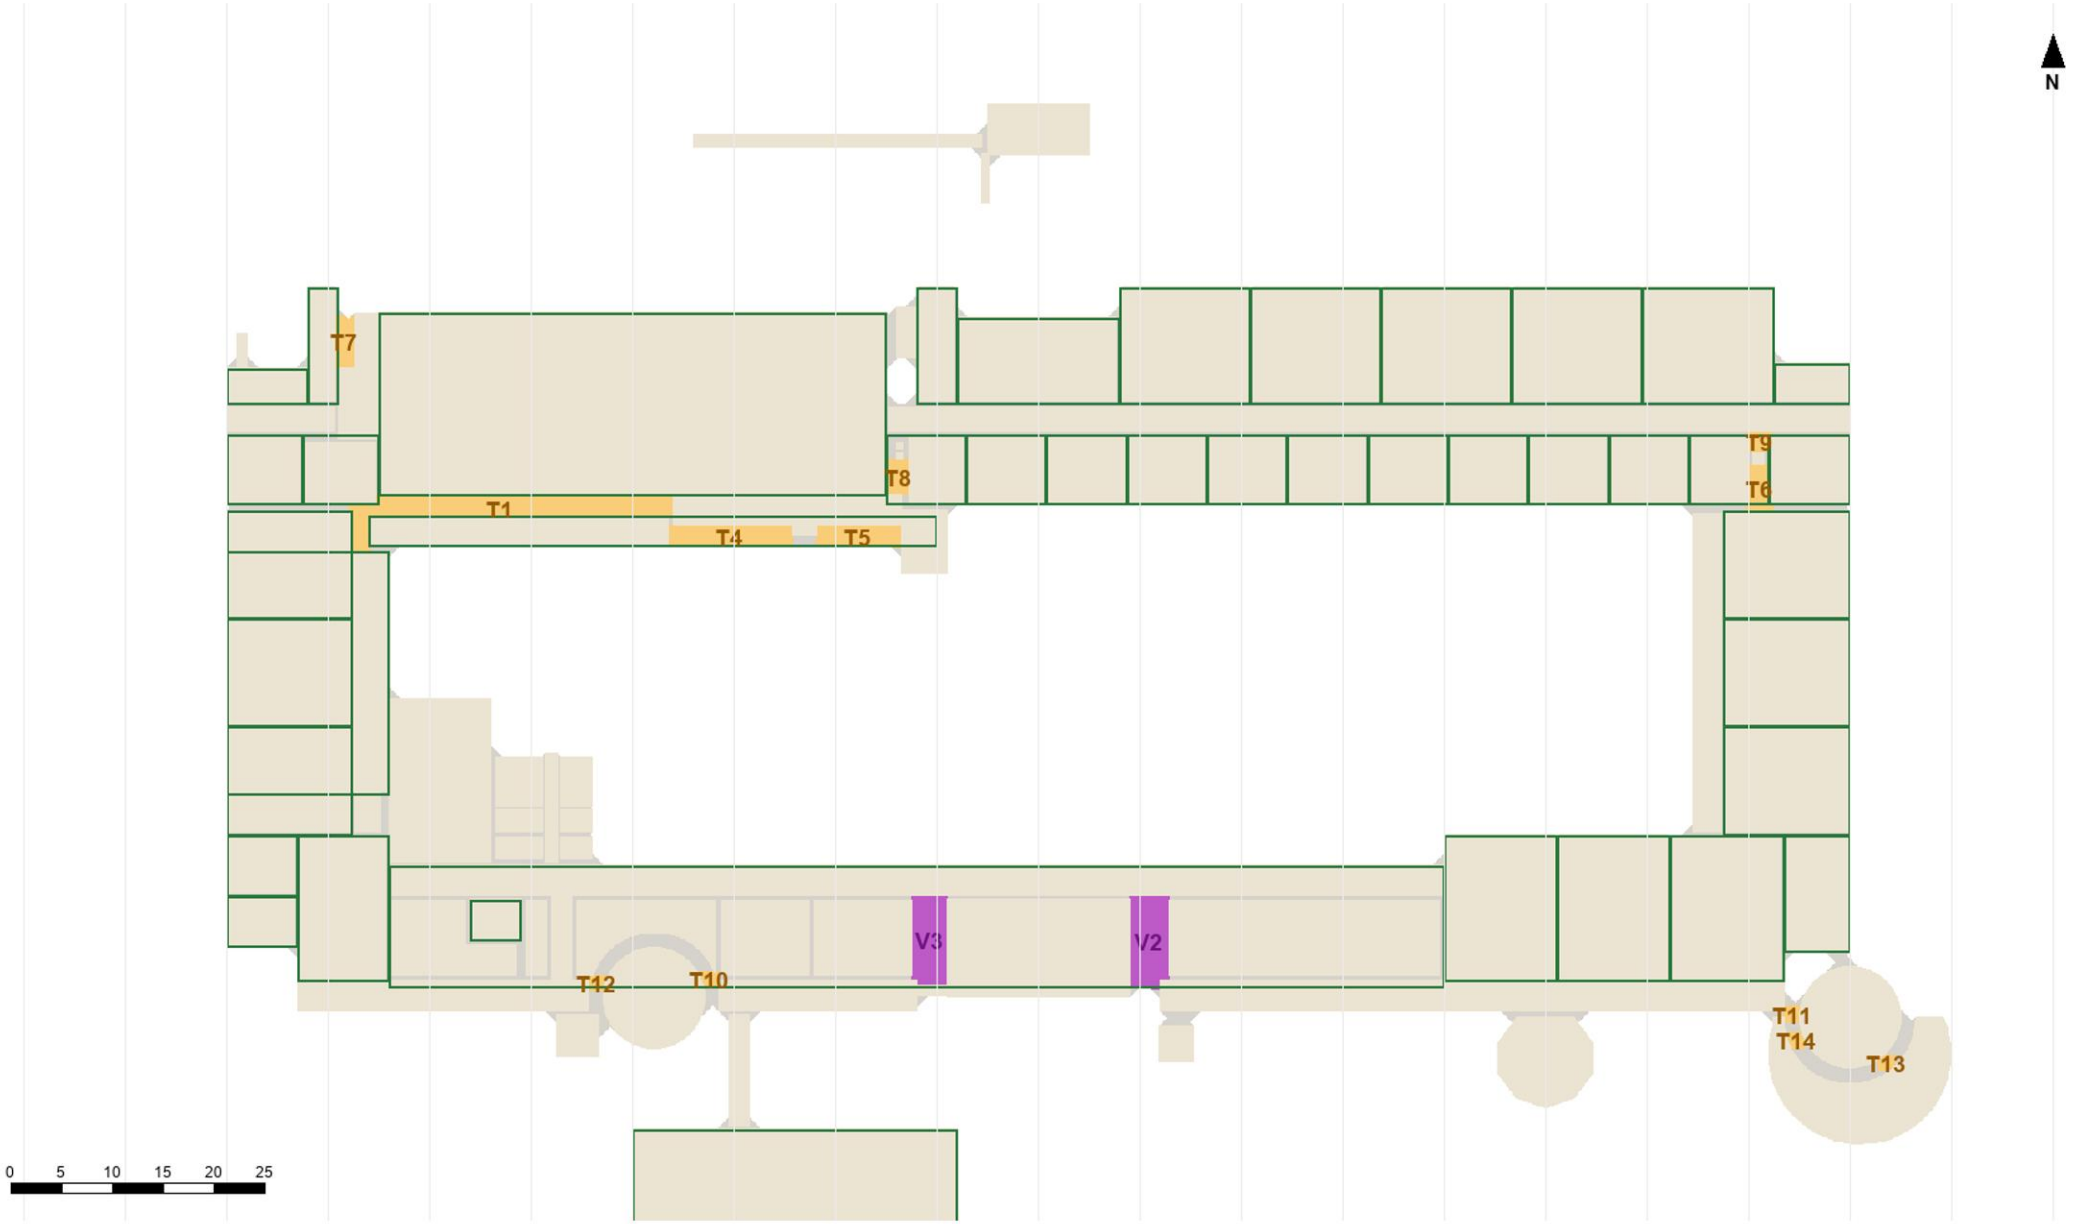

Fill: beige, built in the model; green, layout room as drawn inside its walls; teal, trimmed; pale red, what a reimagined room keeps; purple, a true void (3 m wide or more); amber, a thick wall (1.5 to 3 m). Outlines: the layout's rects; red thick, reimagine.

Ground floor (G): the layout's rooms after the wall rule, the true voids flagged


50 built, 1 follows. Voids: V1 524 m2 (21.3 wide), V2 271 m2 (9.2 wide), V3 156 m2 (14.1 wide), V4 137 m2 (6.0 wide), V5 129 m2 (5.0 wide), V8 42 m2 (4.6 wide), V9 42 m2 (3.6 wide), V10 32 m2 (3.6 wide), V11 30 m2 (4.0 wide), V12 29 m2 (4.0 wide), .

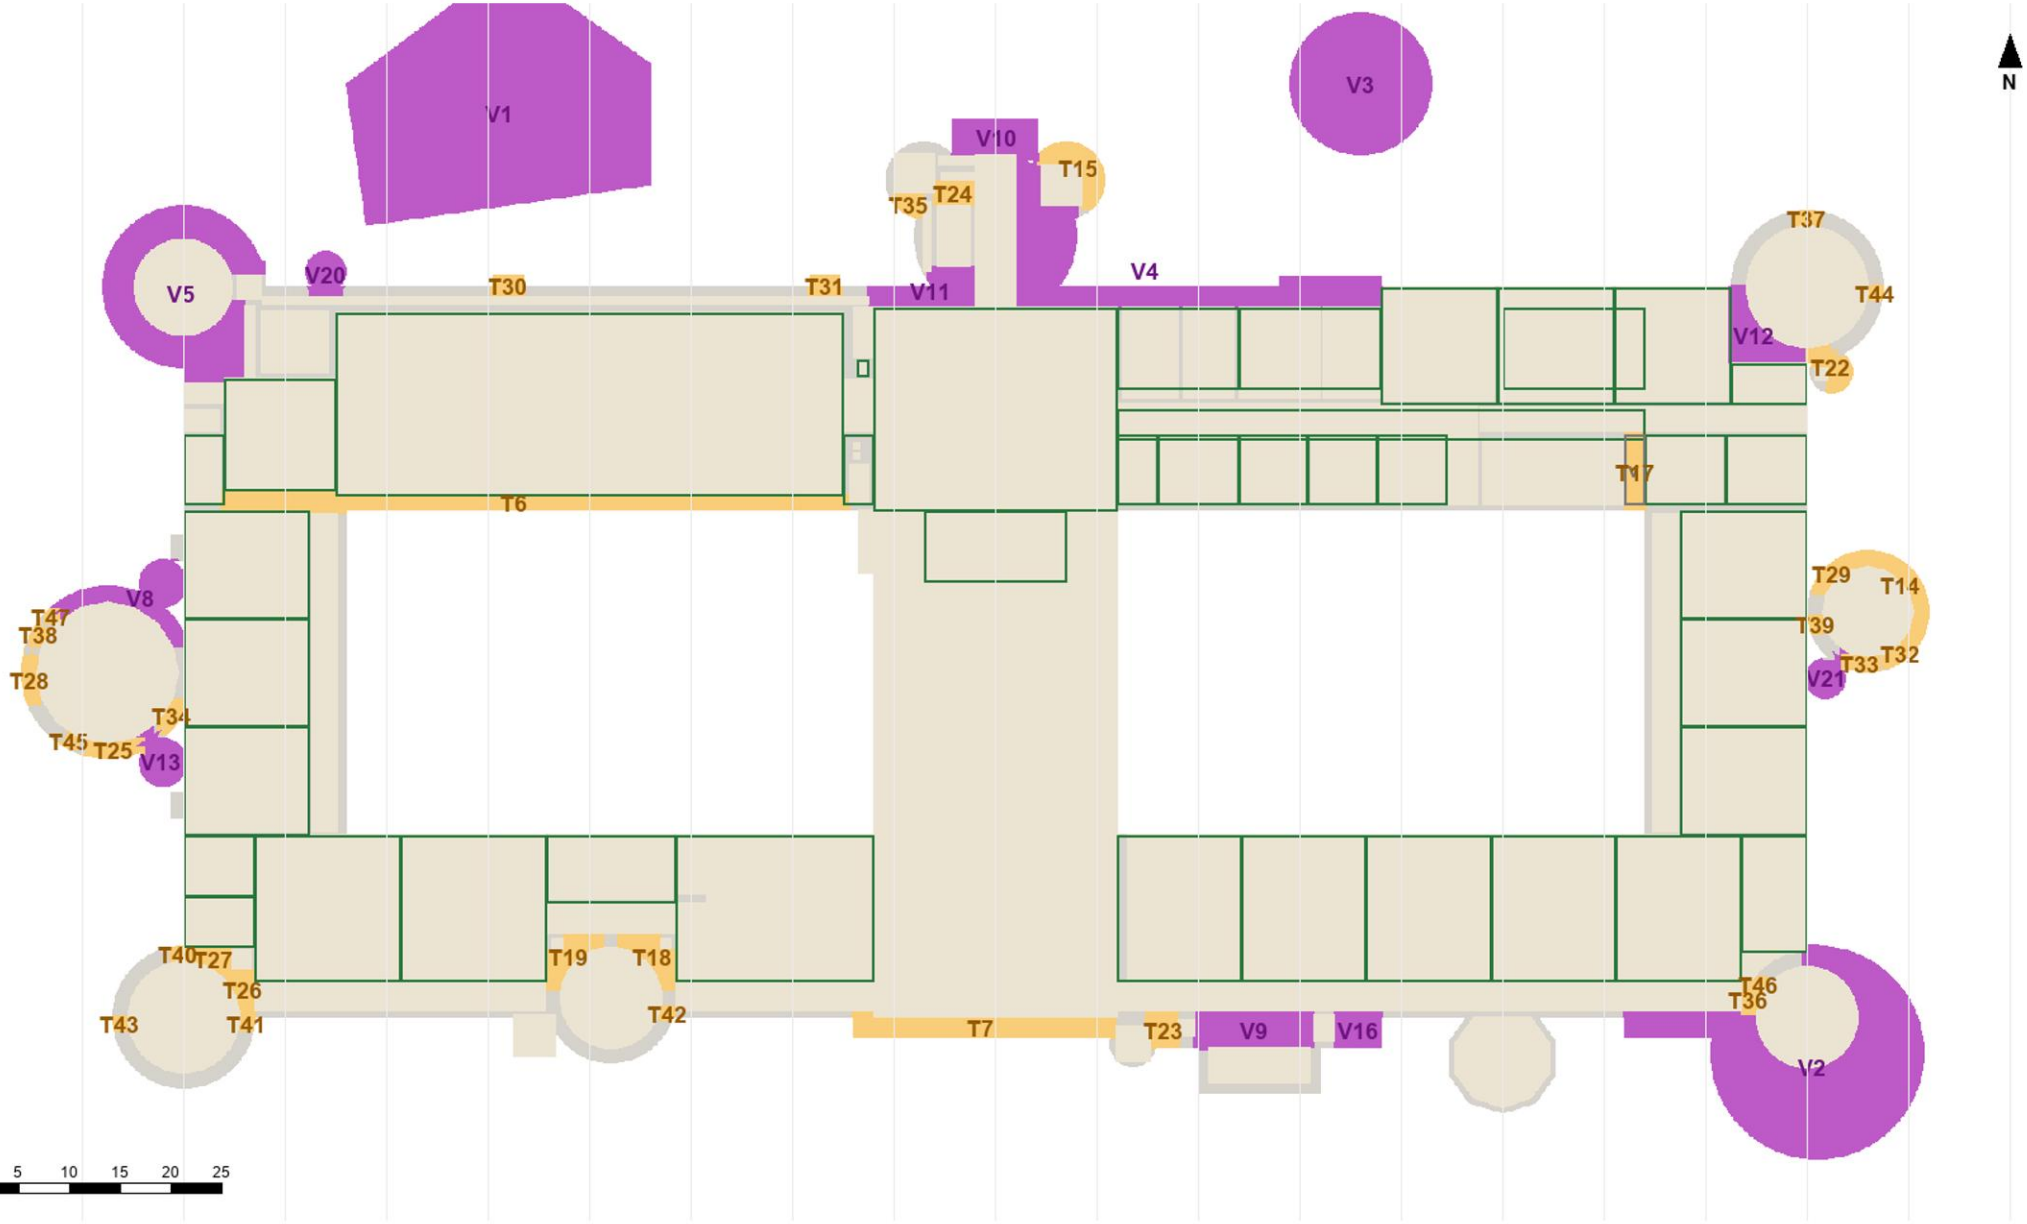

Fill: beige, built in the model; green, layout room as drawn inside its walls; teal, trimmed; pale red, what a reimagined room keeps; purple, a true void (3 m wide or more); amber, a thick wall (1.5 to 3 m). Outlines: the layout's rects; red thick, reimagine.

First floor (1): the layout's rooms after the wall rule, the true voids flagged


51 built, 2 follows. Voids: V1 121 m2 (4.2 wide), V3 76 m2 (3.7 wide), V6 54 m2 (4.0 wide), V7 45 m2 (5.2 wide), V8 44 m2 (4.7 wide), V9 41 m2 (4.6 wide), V10 39 m2 (4.6 wide), V12 25 m2 (4.6 wide), V16 16 m2 (4.1 wide), V19 15 m2 (4.1 wide).

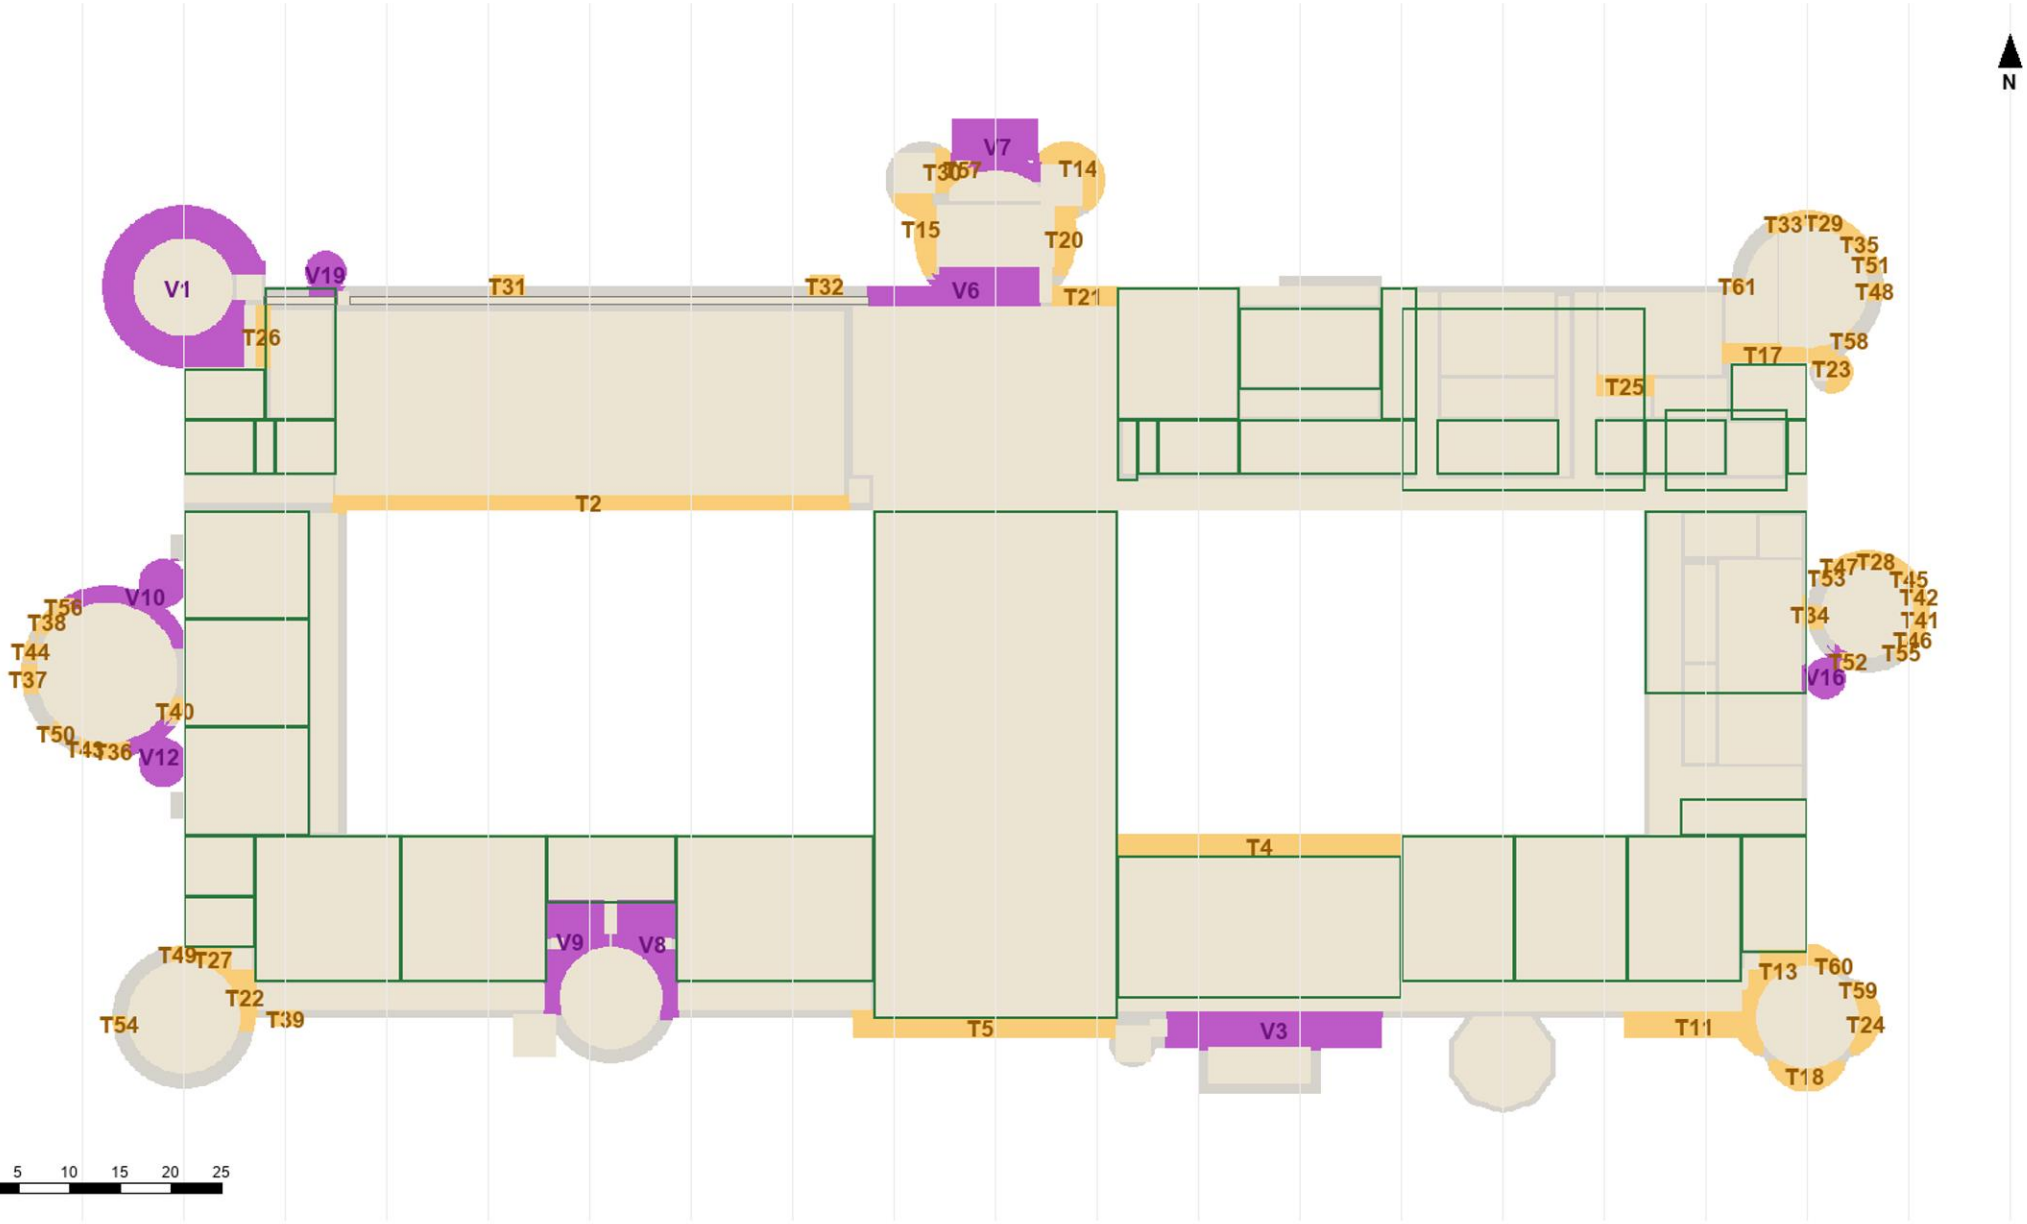

Fill: beige, built in the model; green, layout room as drawn inside its walls; teal, trimmed; pale red, what a reimagined room keeps; purple, a true void (3 m wide or more); amber, a thick wall (1.5 to 3 m). Outlines: the layout's rects; red thick, reimagine.

Second floor (2): the layout's rooms after the wall rule, the true voids flagged

57 built, 1 reimagine. Voids: V1 135 m2 (3.6 wide), V2 82 m2 (3.7 wide), V6 48 m2 (3.4 wide), V7 42 m2 (4.6 wide), V9 29 m2 (4.0 wide), V11 23 m2 (4.0 wide), V12 23 m2 (3.6 wide), V13 20 m2 (4.6 wide), V16 18 m2 (3.2 wide), V19 13 m2 (3.8 wide), V20

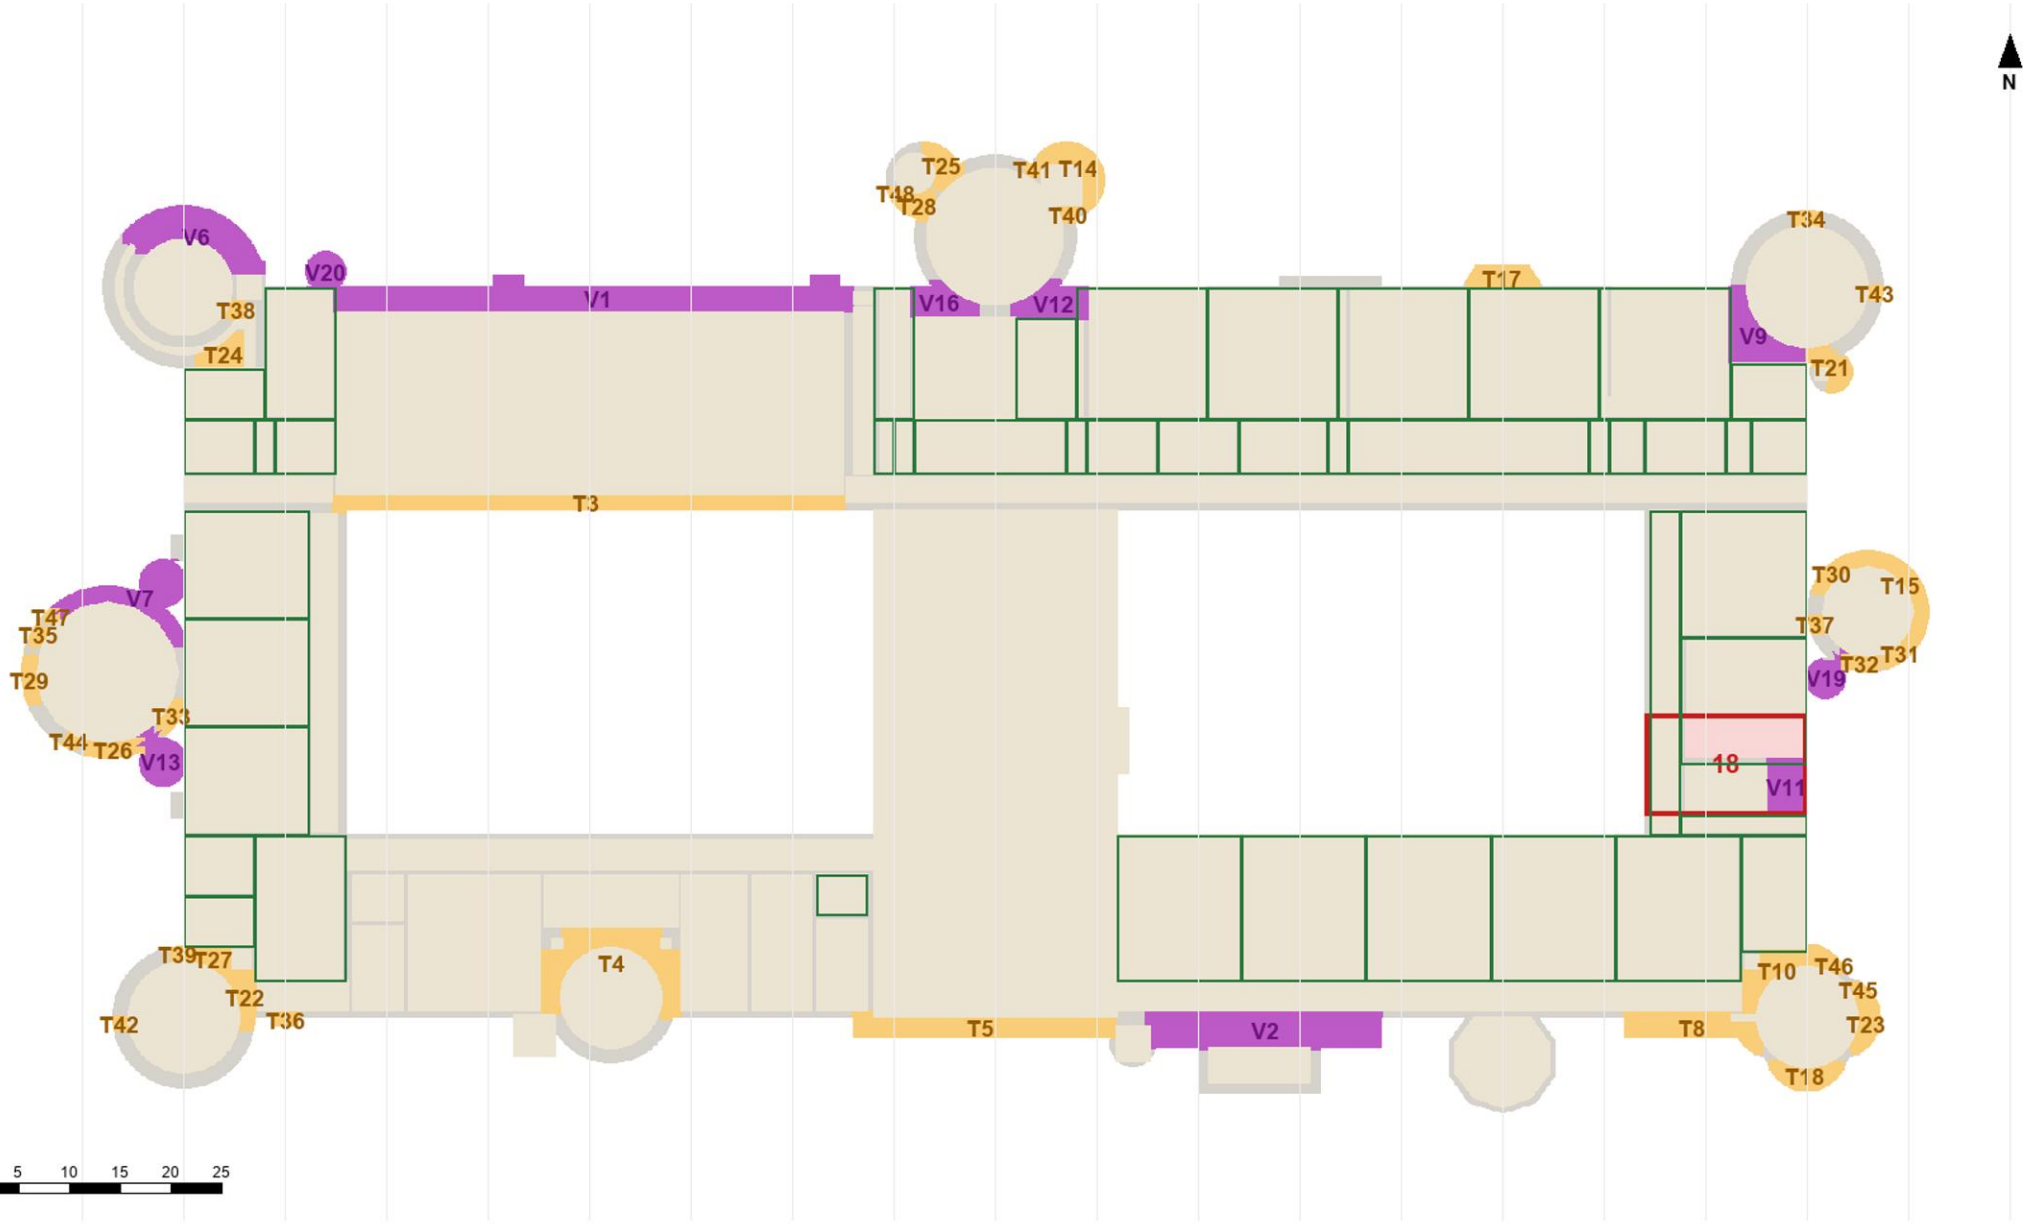


Fill: beige, built in the model; green, layout room as drawn inside its walls; teal, trimmed; pale red, what a reimagined room keeps; purple, a true void (3 m wide or more); amber, a thick wall (1.5 to 3 m). Outlines: the layout's rects; red thick, reimagine.

18 Myrtle's bathroom, the Chamb: a smaller room, 44 of 160 m2: 11.9 x 3.7 m left by myrtles-bathroom, second-floor-east-corridor

Third floor (3): the layout's rooms after the wall rule, the true voids flagged

65 built, 1 reimagine, 1 follows. Voids: V1 113 m2 (3.8 wide), V2 82 m2 (3.7 wide), V5 41 m2 (6.0 wide), V6 40 m2 (4.4 wide), V8 21 m2 (3.0 wide), V12 20 m2 (3.6 wide), V13 20 m2 (4.4 wide), V14 18 m2 (3.2 wide), V16 13 m2 (3.8 wide), V21 12 m2 (3.5

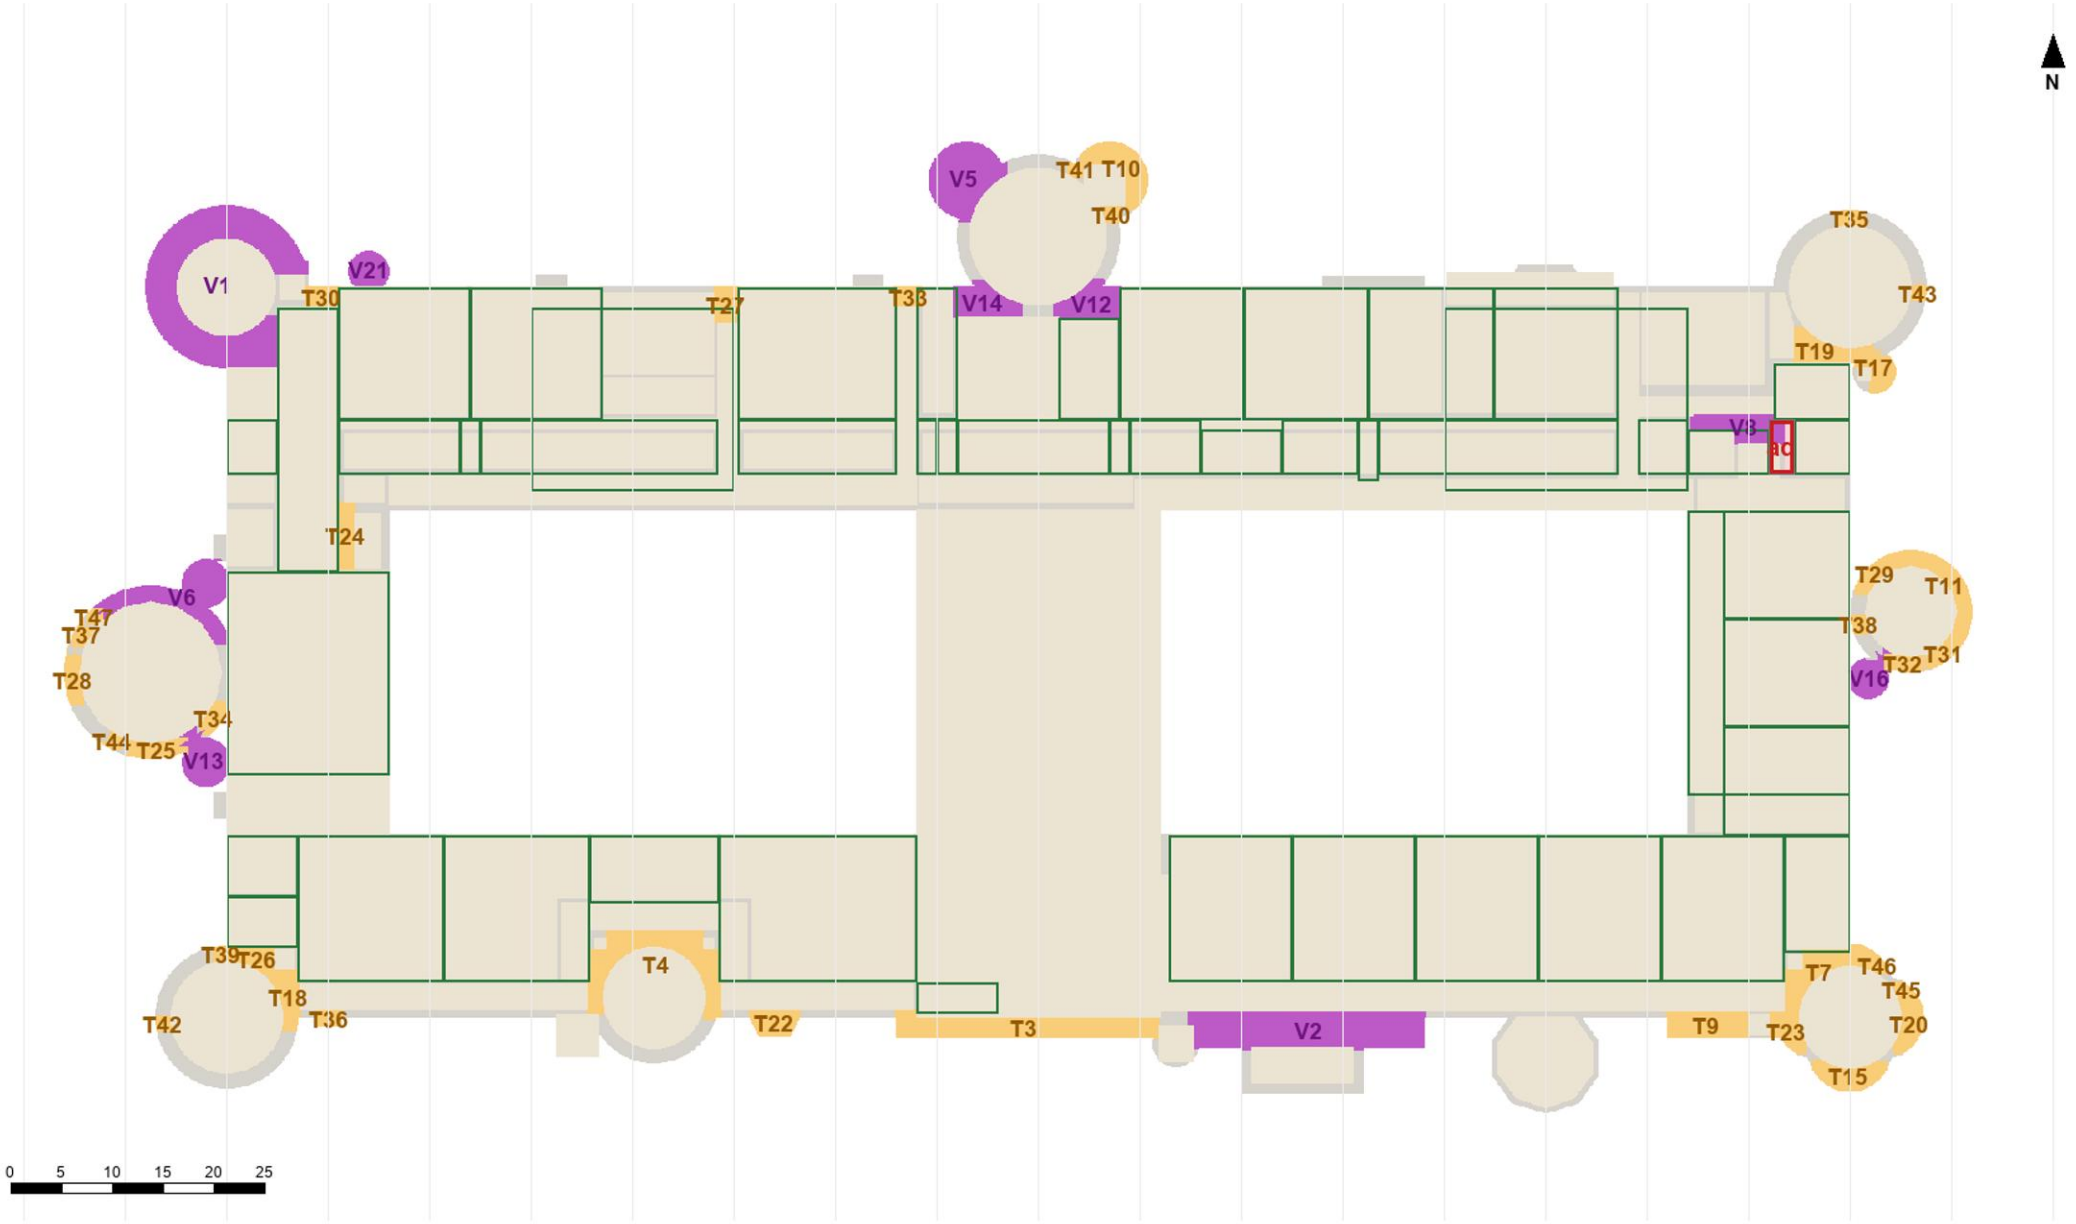


Fill: beige, built in the model; green, layout room as drawn inside its walls; teal, trimmed; pale red, what a reimagined room keeps; purple, a true void (3 m wide or more); amber, a thick wall (1.5 to 3 m). Outlines: the layout's rects; red thick, reimagine.

aq A passage to the rooms behin: a thick wall, 0.6 x 4.7 m left by stone-bay

Fourth floor (4): the layout's rooms after the wall rule, the true voids flagged


62 built. Voids: V1 121 m2 (4.2 wide), V2 70 m2 (3.0 wide), V4 44 m2 (4.7 wide), V5 42 m2 (4.6 wide), V6 41 m2 (4.6 wide), V8 29 m2 (4.0 wide), V10 24 m2 (3.6 wide), V11 20 m2 (4.6 wide), V15 14 m2 (4.1 wide), V16 13 m2 (3.8 wide).

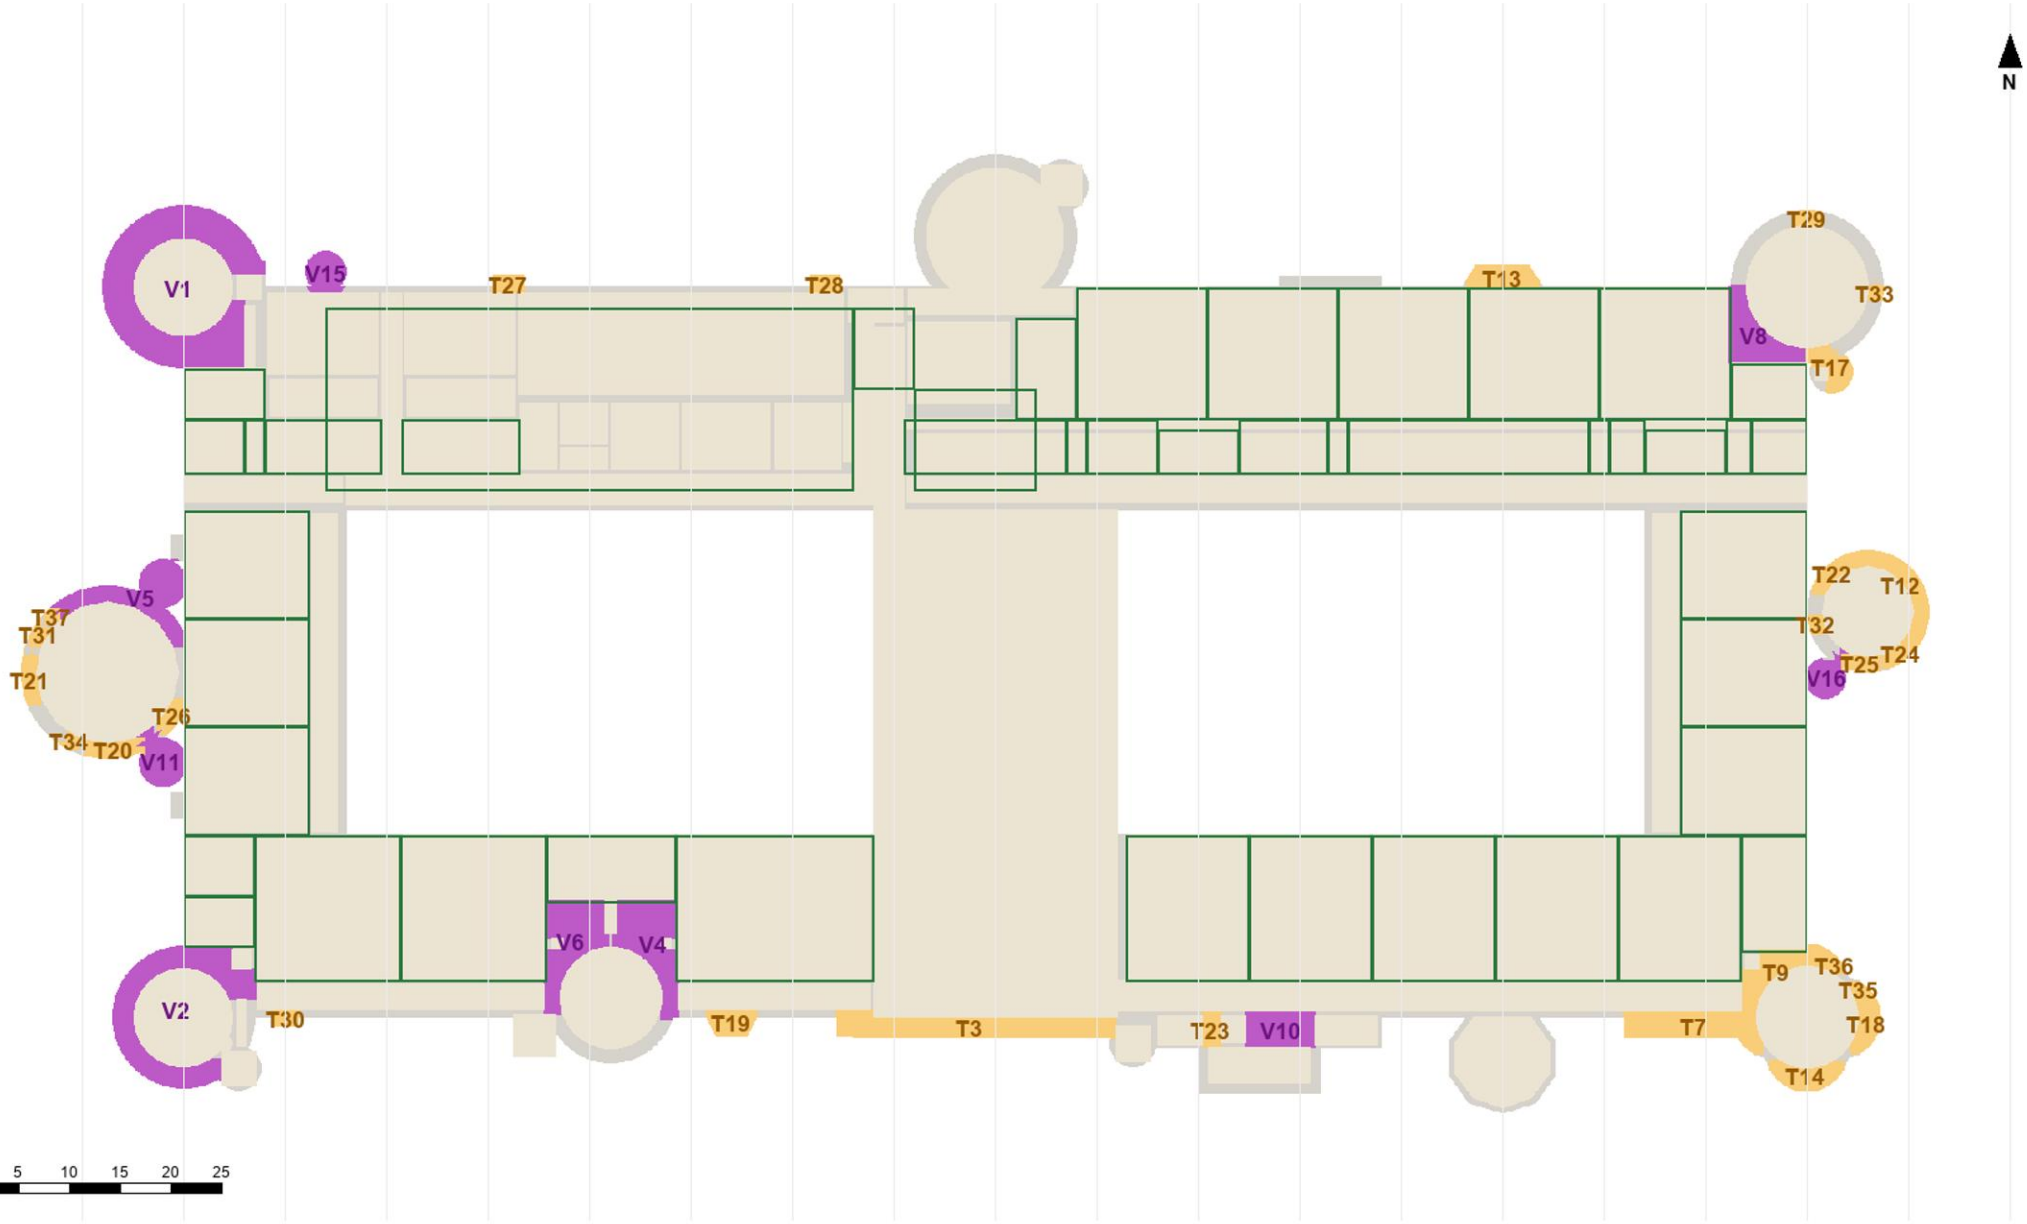

Fill: beige, built in the model; green, layout room as drawn inside its walls; teal, trimmed; pale red, what a reimagined room keeps; purple, a true void (3 m wide or more); amber, a thick wall (1.5 to 3 m). Outlines: the layout's rects; red thick, reimagine.

Fifth floor (5): the layout's rooms after the wall rule, the true voids flagged


62 built. Voids: V1 121 m2 (4.2 wide), V2 80 m2 (3.0 wide), V4 48 m2 (3.7 wide), V5 42 m2 (4.6 wide), V7 30 m2 (3.4 wide), V8 29 m2 (4.0 wide), V9 26 m2 (3.7 wide), V11 23 m2 (3.4 wide), V12 22 m2 (3.6 wide), V13 22 m2 (3.5 wide), V14 20.

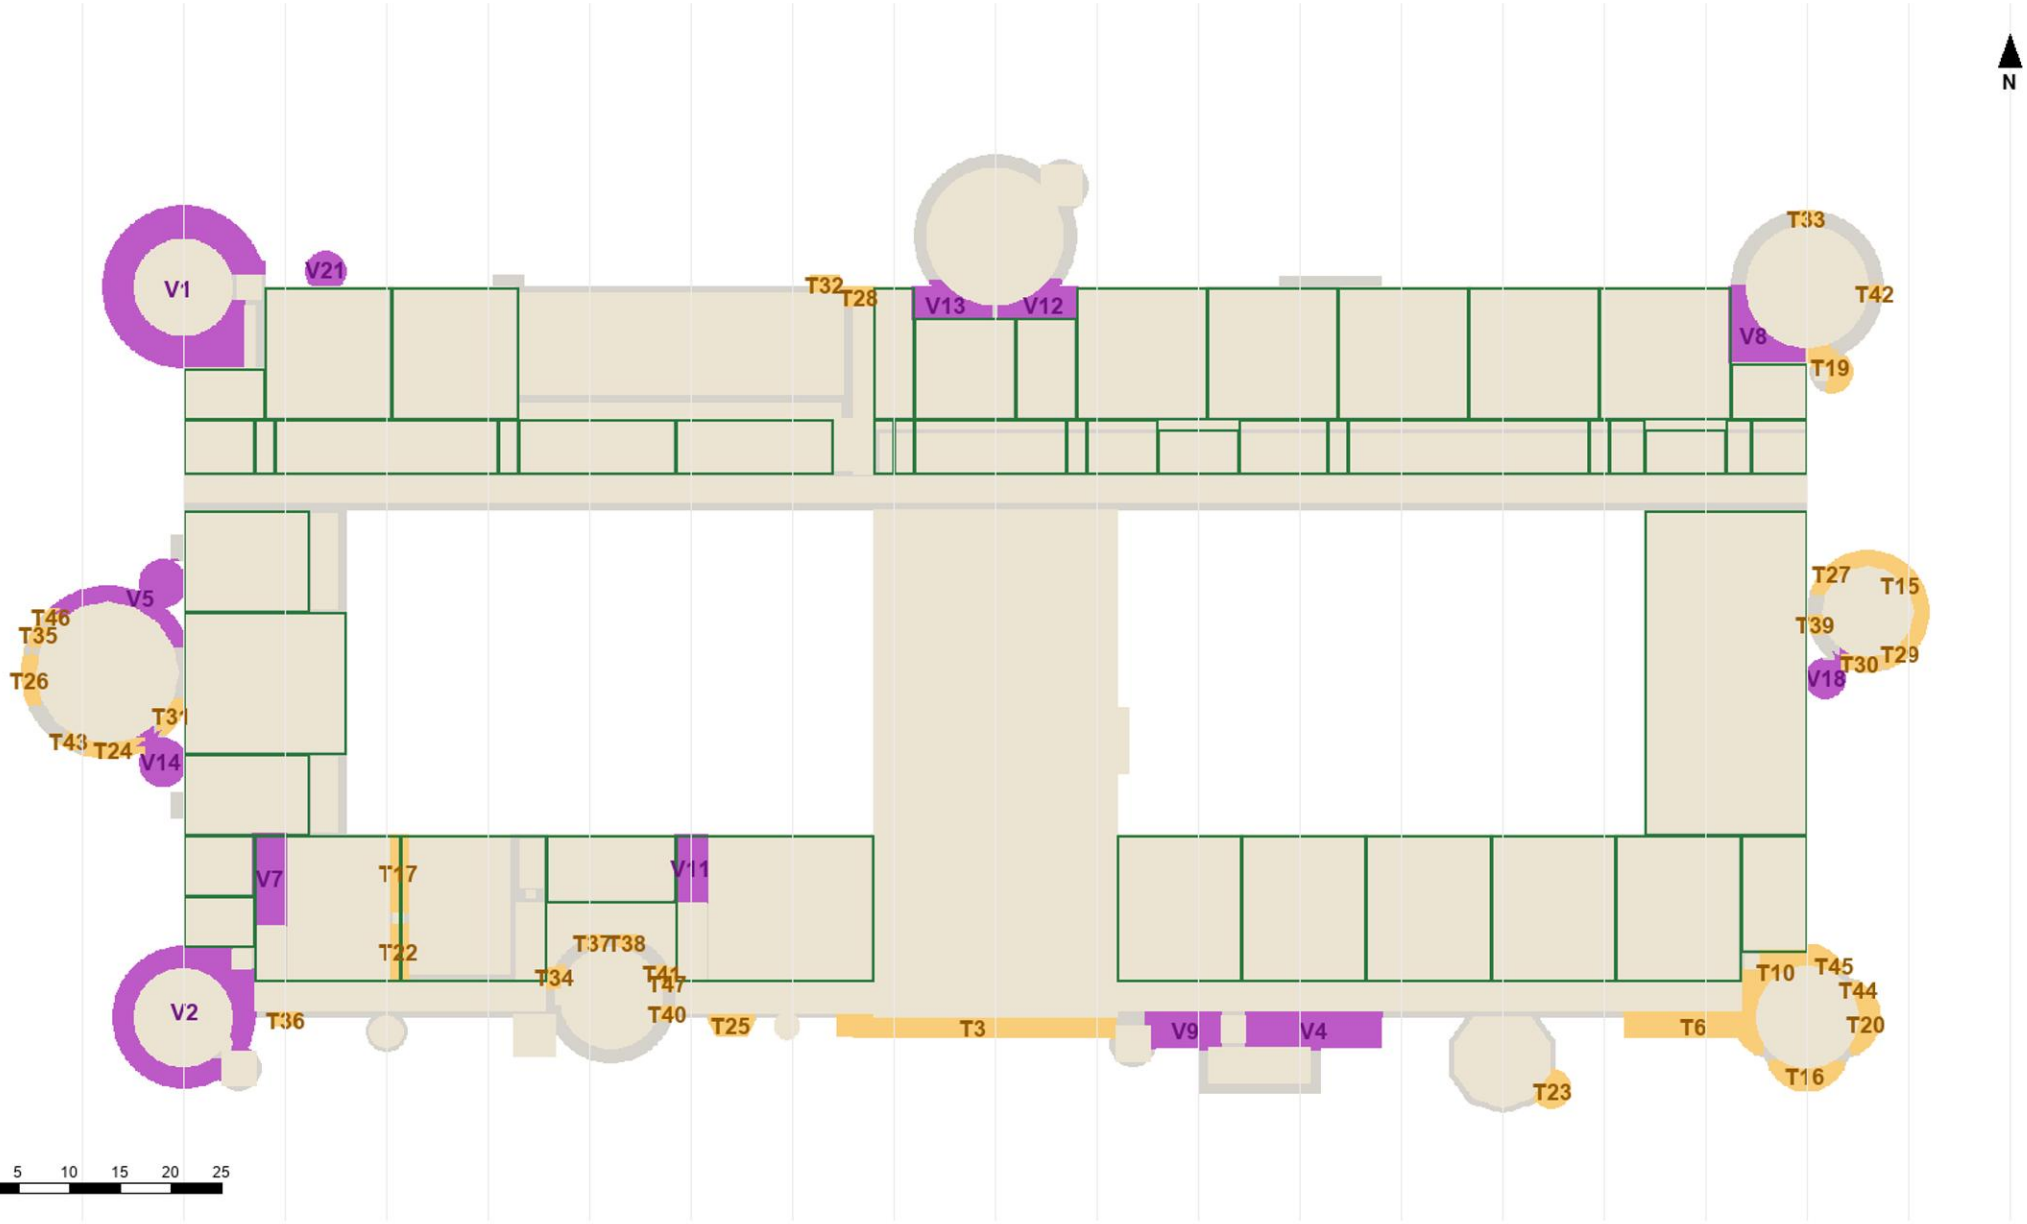

Fill: beige, built in the model; green, layout room as drawn inside its walls; teal, trimmed; pale red, what a reimagined room keeps; purple, a true void (3 m wide or more); amber, a thick wall (1.5 to 3 m). Outlines: the layout's rects; red thick, reimagine.

Sixth floor (6): the layout's rooms after the wall rule, the true voids flagged


71 built. Voids: V1 123 m2 (4.3 wide), V2 81 m2 (3.0 wide), V3 39 m2 (4.6 wide), V4 38 m2 (3.6 wide), V6 34 m2 (3.8 wide), V7 28 m2 (3.8 wide), V8 28 m2 (3.6 wide), V9 27 m2 (3.2 wide), V10 25 m2 (4.6 wide), V11 25 m2 (3.8 wide), V12 22 .

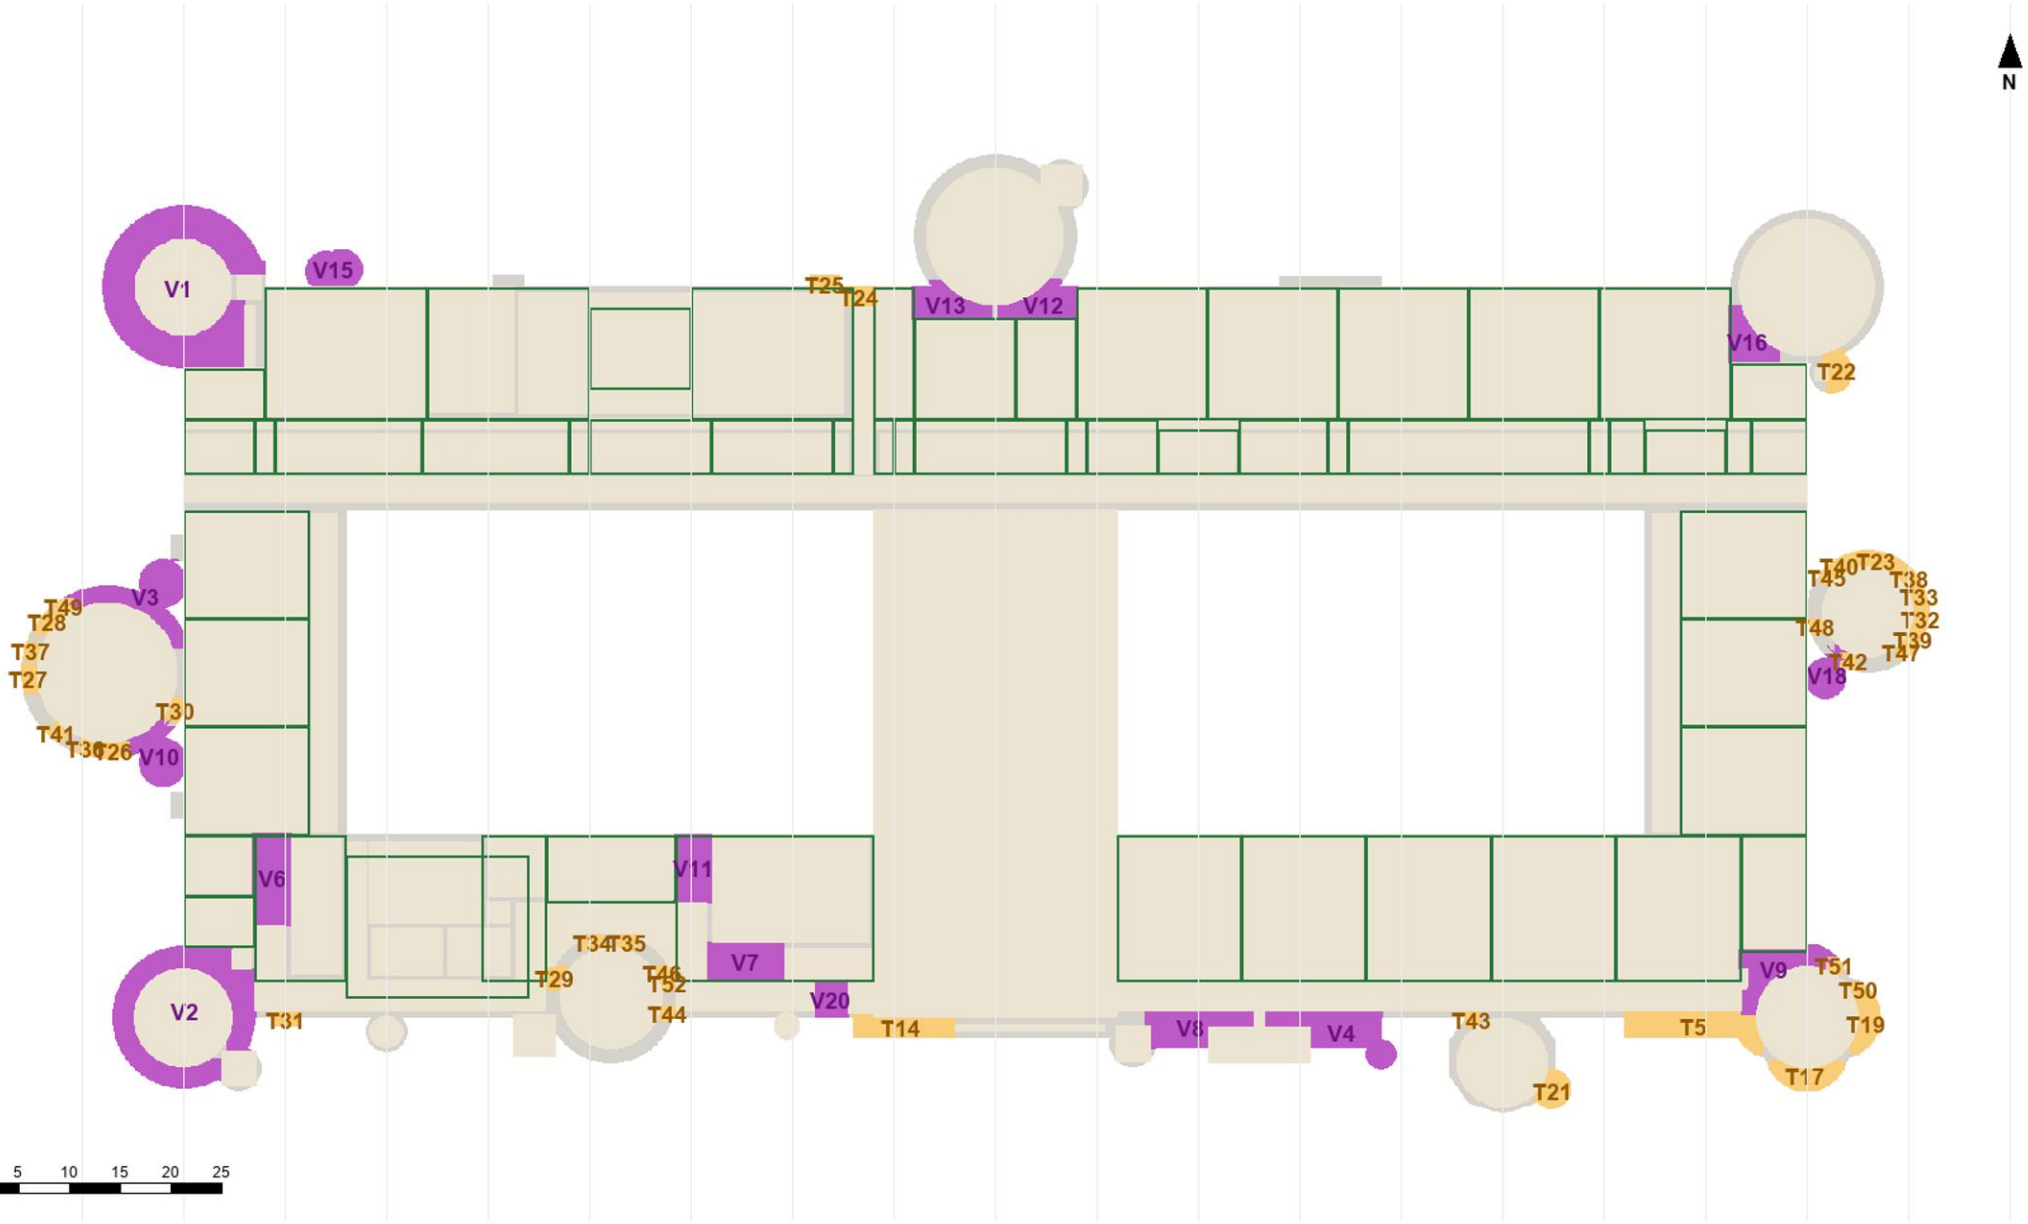

Fill: beige, built in the model; green, layout room as drawn inside its walls; teal, trimmed; pale red, what a reimagined room keeps; purple, a true void (3 m wide or more); amber, a thick wall (1.5 to 3 m). Outlines: the layout's rects; red thick, reimagine.

Seventh floor (7): the layout's rooms after the wall rule, the true voids flagged

63 built. Voids: V1 169 m2 (5.2 wide), V2 123 m2 (4.4 wide), V4 61 m2 (3.0 wide), V6 45 m2 (4.4 wide), V7 42 m2 (4.6 wide), V8 40 m2 (3.6 wide), V10 22 m2 (3.2 wide), V11 22 m2 (3.5 wide), V12 20 m2 (4.6 wide), V14 18 m2 (3.7 wide).

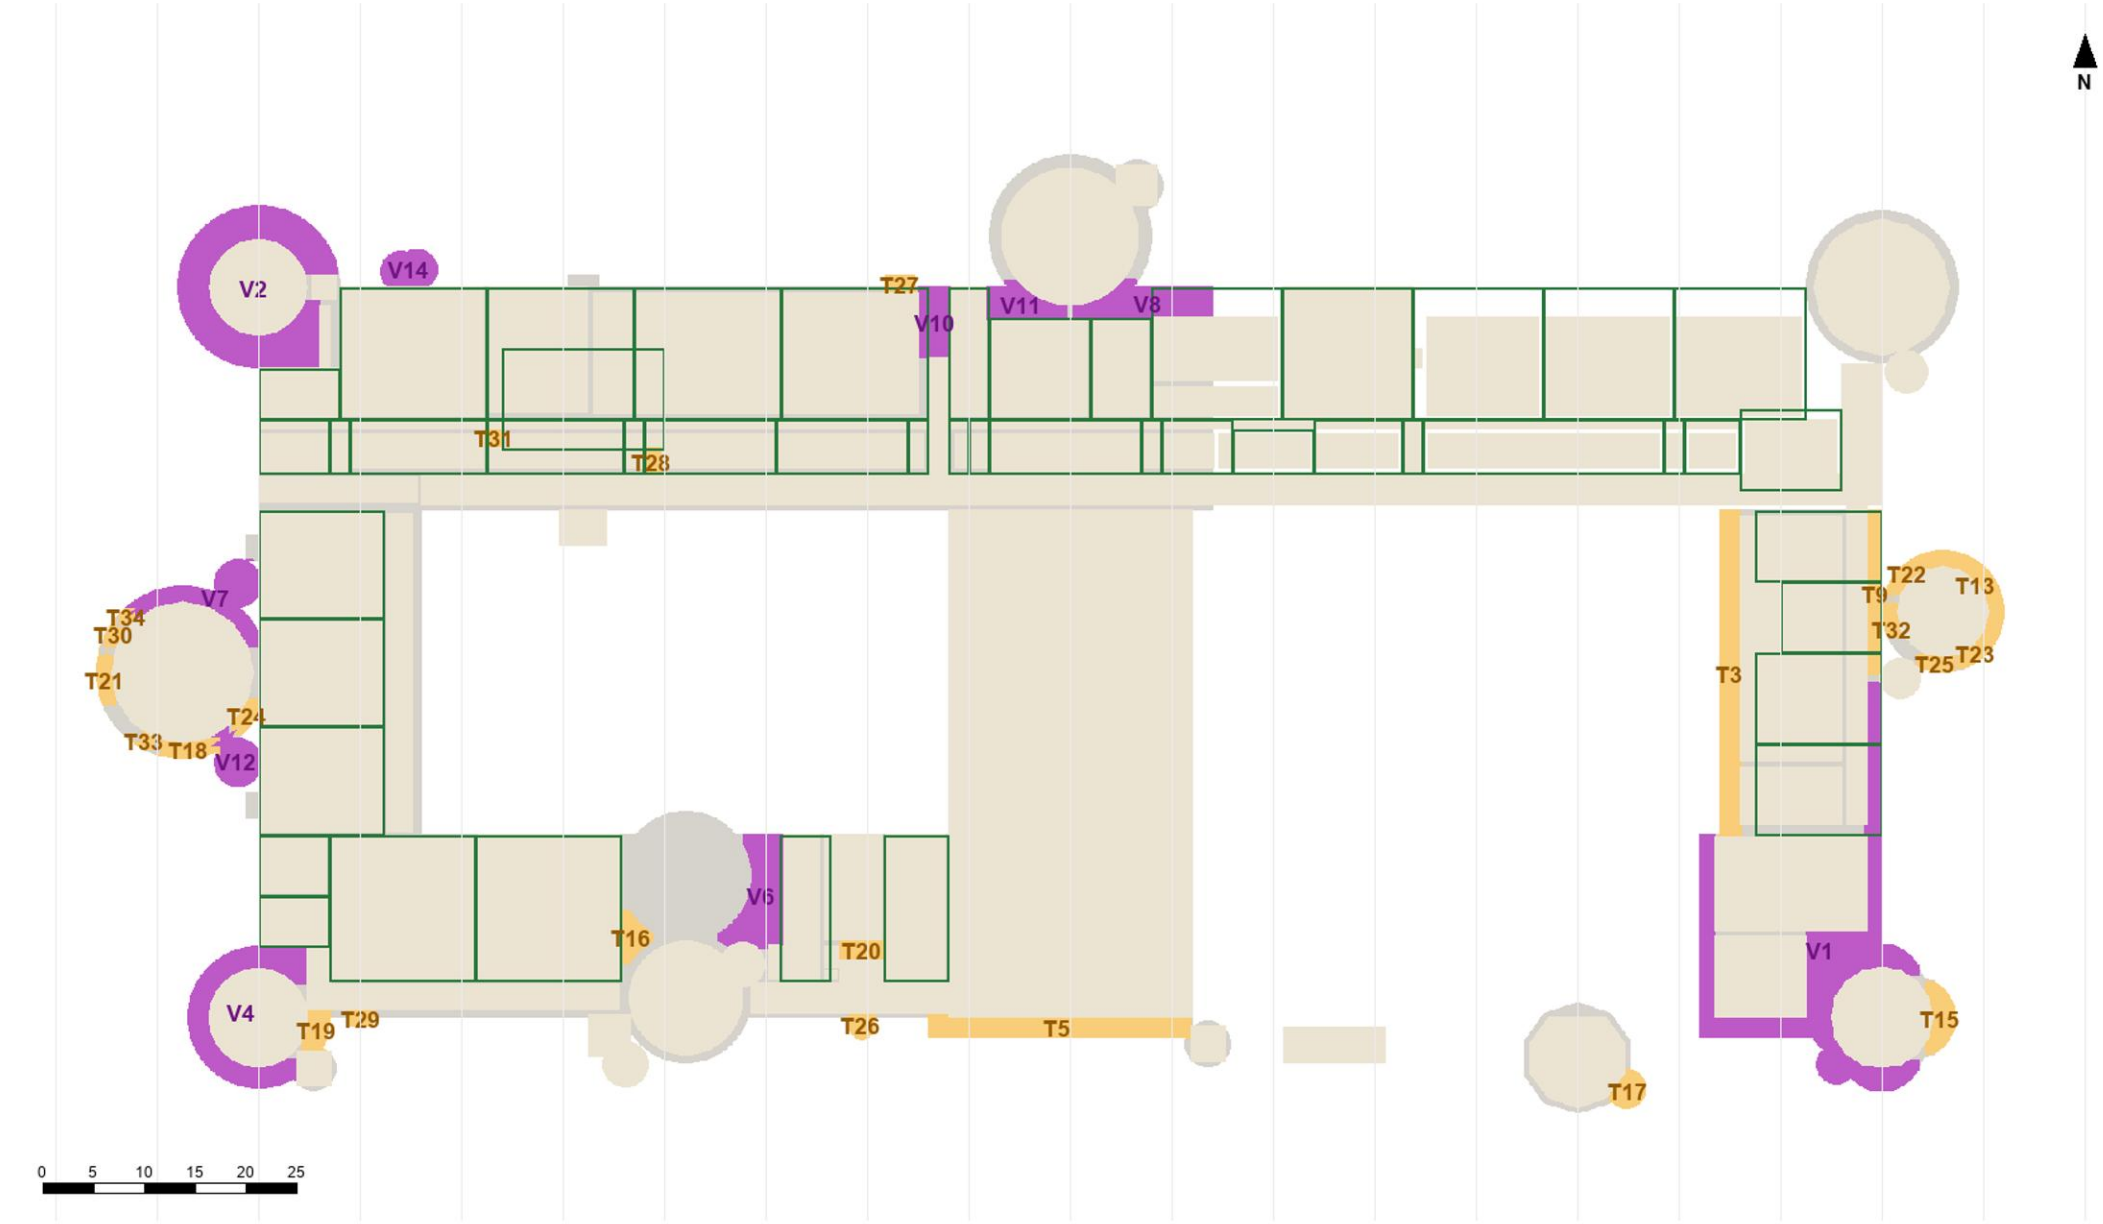

Fill: beige, built in the model; green, layout room as drawn inside its walls; teal, trimmed; pale red, what a reimagined room keeps; purple, a true void (3 m wide or more); amber, a thick wall (1.5 to 3 m). Outlines: the layout's rects; red thick, reimagine.