Hogwarts, floor by floor: every place and every space between

The Architect, 20 October 2026, for Godric. The castle model (page/castle-model.js, version 71) and the step 3 sheet, under 1.1, 2.1, 3.1, Q48b's 3 and 4.1.

How to read it

One floor a page, below ground to the tower tops, all at one scale (north up, the bar 50 m), a schedule under each plan.

Numbers are the named places: the first draft's (1 to 48) and the canon sweep's (+1 to +48), each with its book line. Brown is built, hatched designed, blue placed by the books, dotted inferred, dashed proposed.

Built so far, the places the boys can already walk: the Gryffindor common room, the dormitory above it, and the Fat Lady's corridor to her portrait (the seventh floor and the tower tops, in brown).

Letters, in purple rooms, are this drawing's fill: every range has a corridor along one face and rooms along the other, cut from whatever the named places leave free, and each room is given a use and a name. Green: a place the books name but do not place (the sweep's unplaced rows, each checked in the text); purple: ours. A room of ours with a canon nod names its line.

The rule of the fill

Canon first. Then what a working castle school needs near what it serves: each subject's second classroom, store and teacher's rooms beside its named classroom; the kitchens' rooms by the kitchens. Stairs and washrooms stack: each tower's foot gives a stair between every floor in the corner it leaves in its range, and the washrooms keep the same three places on every floor (two in the north range, one by the south-west tower), skipped only where a named place takes the spot. Cupboards and stores fill the deep middle of the north range, where no window reaches. A classroom goes only in a room at least 7 m across, and no range repeats a room's name on one floor. Then a few rooms for the boys to find (a wizard chess room, Peeves's den of stolen chalk, portraits waiting for walls). No corridor runs past nothing.

The count

369 spaces given a use: 14 canon, 355 ours. By floor: B 37, G 32, 1 30, 2 42, 3 43, 4 42, 5 46, 6 53, 7 44, T 0.

Open


All of the fill is a proposal: mark any room and it changes. The fill goes into the model only once you have looked; the Map is inked from the model.

The castle's layout, below ground: the cellars and dungeons

The Architect, 20 October 2026, for Godric, on the castle model, version 71. Under 1.1, 2.1, 3.1 and Q48b's 3. North up; the bar 50 m. Numbers: the step 3 sheet's places (+ the canon sweep's); letters, purple: this sheet's fill, every space given a use.

Below ground: the dungeons and the cellars

floor at -5.2 m

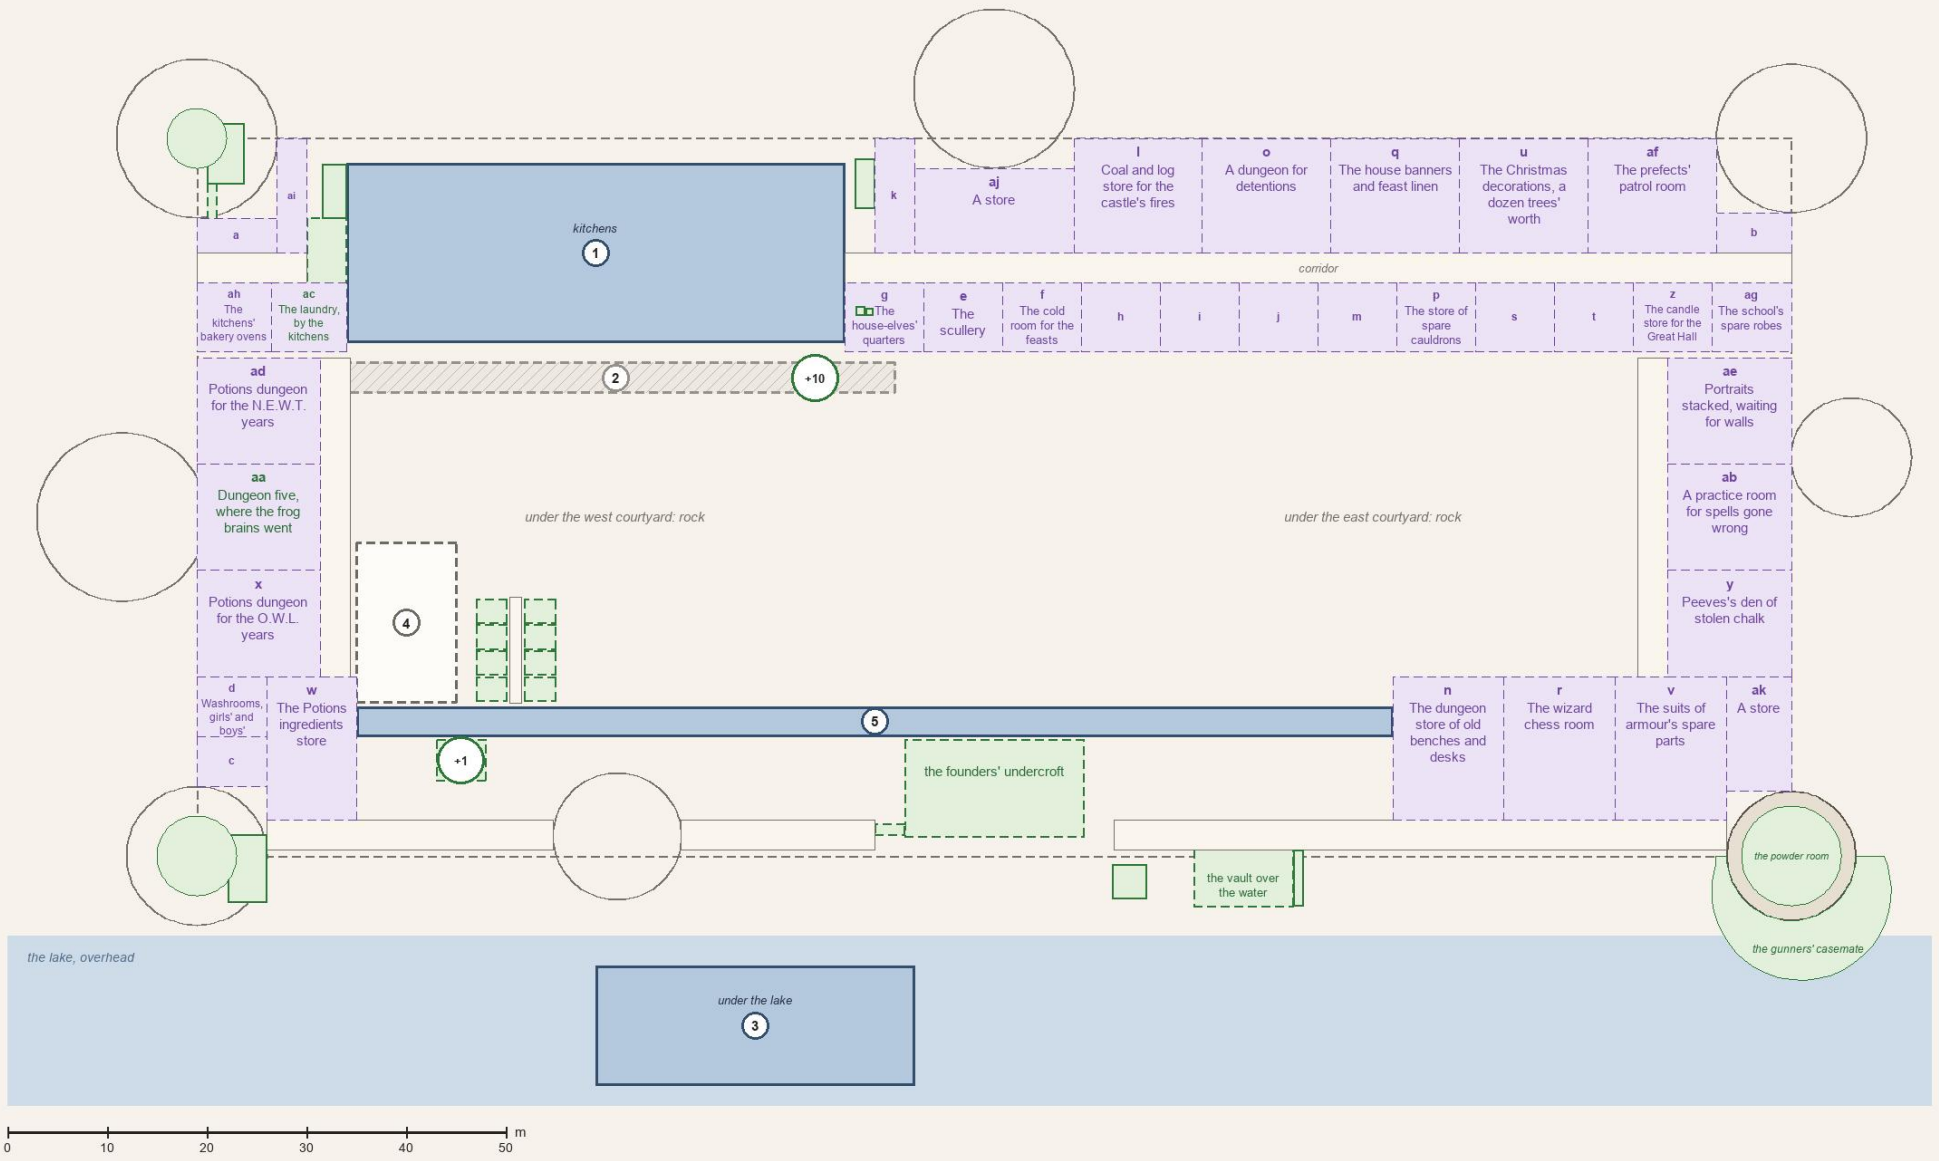

Named places on this floor (the step 3 sheet: numbers the first draft's, + the canon sweep's)

1 Kitchens [books] (GoF 21)
2 Hufflepuff's basement corridor, which also leads to the kitchens (Hufflepuff's room off the list) [off] (OotP 18, HBP 21)
3 Slytherin common room [books] (DH 23)
4 Potions classroom, down in a dungeon (the spot proposed) [proposed] (PS 8)
5 Dungeon corridors [books] (CoS 8)
+1 Snape's office, halfway down the cold passage, by Potions (CoS 5, GoF 25) [canon]
+10 The fruit-bowl painting, the kitchens' door (GoF 21) [canon]

The model's rooms with no number (page/castle-model.js, version 71)

a warm room behind the kitchens' great fireplace (secret-s3)
the founders' undercroft (founders-undercroft)
the way through the keep's west wall to the undercroft (undercroft-west-way)
the vault over the water (cliff-vault)
the short passage north from the stair foot into the West Tower's drum (ice-house-way)
the passage of the old cells under the west courtyard (old-cells-passage)
an old cell (old-cell-w1)
an old cell (old-cell-w2)
an old cell (old-cell-w3)
an old cell (old-cell-w4)
an old cell (old-cell-e1)
an old cell (old-cell-e2)
an old cell (old-cell-e3)
an old cell (old-cell-e4)
the lake-face corridor on B (lake-corridor-b-east)
the lake-face corridor on B (lake-corridor-b-keep)
the lake-face corridor on B (lake-corridor-b-west)

The towers at this level

Astronomy Tower: its stair to the top
Ravenclaw Tower: its tight spiral stair (+23)
Gryffindor Tower: below the common room: the house's storerooms (ours)
West Tower: its stair; Flitwick's office on 7 (42)
North Tower: its spiral from the seventh floor (+3) to the tiny landing at +45.4
south-west tower: a stair and staff rooms (ours)
south-east tower: blank, but the model room on 4 (H40) and the casemate round its foot on B (H41)
Dumbledore's tower: the gargoyle's moving stair on 7 (41)

Cores not on this floor (a named place takes the spot)

A Gryffindor storeroom at the tower's foot: 5 takes it


This sheet's fill, every space given a use (green: canon, purple: ours)

a The West Tower's stair foot, a stair between every floor [ours: PS 8: "a hundred and forty-two staircases"] core, 8 by 4 m
b The North Tower's stair foot, a stair between every floor [ours: PS 8: "a hundred and forty-two staircases"] core, 8 by 4 m
c The south-west tower's stair foot, a stair between every floor [ours: PS 8: "a hundred and forty-two staircases"] core, 7 by 5 m
d Washrooms, girls' and boys' [ours] core, 7 by 6 m
e The scullery [ours] north range, 8 by 7 m
f The cold room for the feasts [ours] north range, 8 by 7 m
g The house-elves' quarters [ours] north range, 8 by 7 m
h The kitchen stores: flour, sugar, the pumpkins [ours] north range, 8 by 7 m
i The brewing cellar, where slow potions steep [ours] north range, 8 by 7 m
j The cellar of butterbeer and pumpkin juice [ours] north range, 8 by 7 m
k A broom cupboard [ours] north range, 4 by 12 m
l Coal and log store for the castle's fires [ours] north range, 13 by 12 m
m Filch's store of confiscated things [ours] north range, 8 by 7 m
n The dungeon store of old benches and desks [ours] south range, east, 11 by 14 m
o A dungeon for detentions [ours] north range, 13 by 12 m
p The store of spare cauldrons [ours] north range, 8 by 7 m
q The house banners and feast linen [ours] north range, 13 by 12 m
r The wizard chess room [ours] south range, east, 11 by 14 m
s The quill, ink and parchment store [ours] north range, 8 by 7 m
t A ghosts' gathering room, cold all year [ours] north range, 8 by 7 m
u The Christmas decorations, a dozen trees' worth [ours] north range, 13 by 12 m
v The suits of armour's spare parts [ours] south range, east, 11 by 14 m
w The Potions ingredients store [ours] south range, west, 9 by 14 m
x Potions dungeon for the O.W.L. years [ours] west range, 12 by 11 m
y Peeves's den of stolen chalk [ours] east range, 12 by 11 m
z The candle store for the Great Hall [ours] north range, 8 by 7 m
aa Dungeon five, where the frog brains went [canon: CoS 8] west range, 12 by 11 m
ab A practice room for spells gone wrong [ours] east range, 12 by 11 m
ac The laundry, by the kitchens [canon: CoS 12; its spot ours] north range, 8 by 7 m
ad Potions dungeon for the N.E.W.T. years [ours] west range, 12 by 11 m
ae Portraits stacked, waiting for walls [ours] east range, 12 by 11 m
af The prefects' patrol room [ours] north range, 13 by 12 m
ag The school's spare robes [ours] north range, 8 by 7 m
ah The kitchens' bakery ovens [ours] north range, 8 by 7 m
ai A store of spare desks and chairs [ours] north range, 3 by 12 m
aj A store [ours] north range, 16 by 8 m
ak A store [ours] south range, east, 6 by 12 m

The castle's layout, the ground floor

The Architect, 20 October 2026, for Godric, on the castle model, version 71. Under 1.1, 2.1, 3.1 and Q48b's 3. North up; the bar 50 m. Numbers: the step 3 sheet's places (+ the canon sweep's); letters, purple: this sheet's fill, every space given a use.

Ground floor

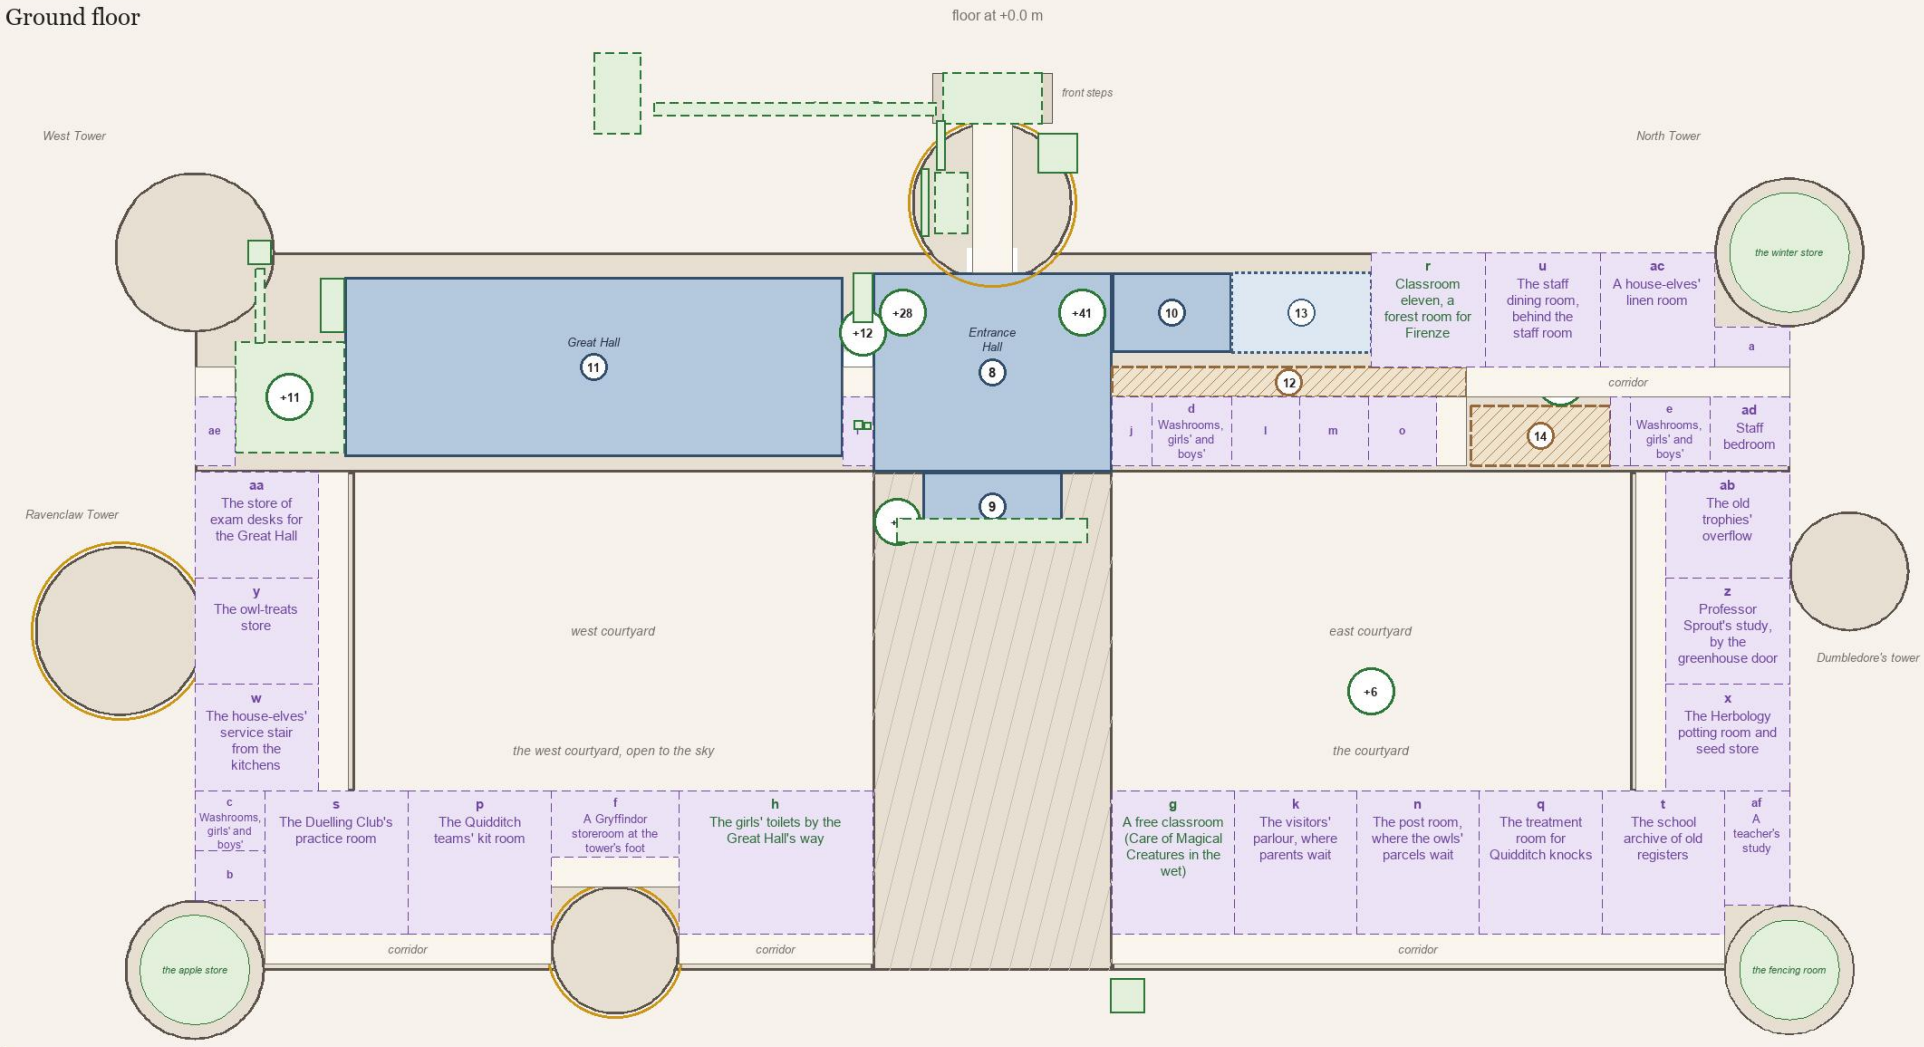

Named places on this floor (the step 3 sheet: numbers the first draft's, + the canon sweep's)

8 Entrance Hall, its front doors in the north face under the Astronomy Tower [books] (PS 7, OotP 31)
9 Marble staircase, facing the front doors [books] (PS 7, PoA 14)
10 The small, empty chamber off the hall (the side proposed) [books] (PS 7)
11 Great Hall, through a doorway to the right on entering, so west of the hall [books] (PS 7)
12 The corridor of classrooms opposite the Great Hall's door [designed] (OotP 27)
13 Filch's office [inferred] (CoS 8)
14 The staff room [designed] (PS 11)
+9 The Hufflepuff door, right of the marble staircase, steps down (GoF 17) [canon]
+6 The courtyard, by the staff room, its balcony and steps (OotP 17, OotP 12, CoS 6) [canon]
+11 The chamber off the Great Hall, behind the staff table (GoF 16, 17) [canon]
+12 The broom cupboard across the hall (PoA 21) [canon]
+27 The staff room's two gargoyles at its door (OotP 17) [canon]
+28 The Entrance Hall's balcony (DH 32) [canon]
+41 The tapestry door and narrow stair up from the hall (GoF 12) [canon]

The model's rooms with no number (page/castle-model.js, version 71)

the passage past the staff room door (staff-passage)
a low room under the marble staircase's half-landing (secret-s2)
the old gate passage through the Astronomy Tower's foot (gate-passage)
the old gate's guard room (guard-room)
the gun room under the front steps (gun-room)
the listeners' gallery under the gun terrace (listeners-gallery)
the bastion's flanker (bastion-flanker)
the passage from the West Tower's stair south to the chamber off the Hall (west-tower-way-g)

The towers at this level

Astronomy Tower: its stair to the top
Ravenclaw Tower: its tight spiral stair (+23)
Gryffindor Tower: below the common room: the house's storerooms (ours)
West Tower: its stair; Flitwick's office on 7 (42)
North Tower: its spiral from the seventh floor (+3) to the tiny landing at +45.4
south-west tower: a stair and staff rooms (ours)
south-east tower: blank, but the model room on 4 (H40) and the casemate round its foot on B (H41)
Dumbledore's tower: the gargoyle's moving stair on 7 (41)

Cores not on this floor (a named place takes the spot)

The West Tower's stair foot, a stair between every floor: +11 takes it

This sheet's fill, every space given a use (green: canon, purple: ours)


a The North Tower's stair foot, a stair between every floor [ours: PS 8: "a hundred and forty-two staircases"] core, 8 by 4 m
b The south-west tower's stair foot, a stair between every floor [ours: PS 8: "a hundred and forty-two staircases"] core, 7 by 5 m
c Washrooms, girls' and boys' [ours] core, 7 by 6 m
d Washrooms, girls' and boys' [ours] core, 8 by 7 m
e Washrooms, girls' and boys' [ours] core, 8 by 7 m
f A Gryffindor storeroom at the tower's foot [ours] core, 13 by 7 m
g A free classroom (Care of Magical Creatures in the wet) [canon: OotP 18] south range, east, 12 by 14 m
h The girls' toilets by the Great Hall's way [canon: PS 10; its floor ours] south range, west, 19 by 14 m
i A broom cupboard [ours] north range, 3 by 7 m
j A store of spare desks and chairs [ours] north range, 4 by 7 m
k The visitors' parlour, where parents wait [ours] south range, east, 12 by 14 m
l The porters' lodge by the front doors [ours] north range, 7 by 7 m
m The cloakroom, wet boots and cloaks [ours] north range, 7 by 7 m
n The post room, where the owls' parcels wait [ours] south range, east, 12 by 14 m
o Madam Hooch's store of school brooms [ours] north range, 7 by 7 m
p The Quidditch teams' kit room [ours] south range, west, 14 by 14 m
q The treatment room for Quidditch knocks [ours] south range, east, 12 by 14 m
r Classroom eleven, a forest room for Firenze [canon: OotP 27: off the Entrance Hall, opposite the Great Hall] north range, 12 by 12 m
s The Duelling Club's practice room [ours: the club canon (CoS 11)] south range, west, 14 by 14 m
t The school archive of old registers [ours] south range, east, 12 by 14 m
u The staff dining room, behind the staff room [ours] north range, 12 by 12 m
v A service passage [ours] north range, 2 by 7 m
w The house-elves' service stair from the kitchens [ours] west range, 12 by 11 m
x The Herbology potting room and seed store [ours] east range, 12 by 11 m
y The owl-treats store [ours] west range, 12 by 11 m
z Professor Sprout's study, by the greenhouse door [ours] east range, 12 by 11 m
aa The store of exam desks for the Great Hall [ours] west range, 12 by 11 m
ab The old trophies' overflow [ours] east range, 12 by 11 m
ac A house-elves' linen room [ours] north range, 12 by 12 m
ad Staff bedroom [ours] north range, 8 by 7 m
ae A linen cupboard [ours] north range, 4 by 7 m
af A teacher's study [ours] south range, east, 6 by 12 m

The castle's layout, the first floor

The Architect, 20 October 2026, for Godric, on the castle model, version 71. Under 1.1, 2.1, 3.1 and Q48b's 3. North up; the bar 50 m. Numbers: the step 3 sheet's places (+ the canon sweep's); letters, purple: this sheet's fill, every space given a use.

First floor

floor at +5.2 m

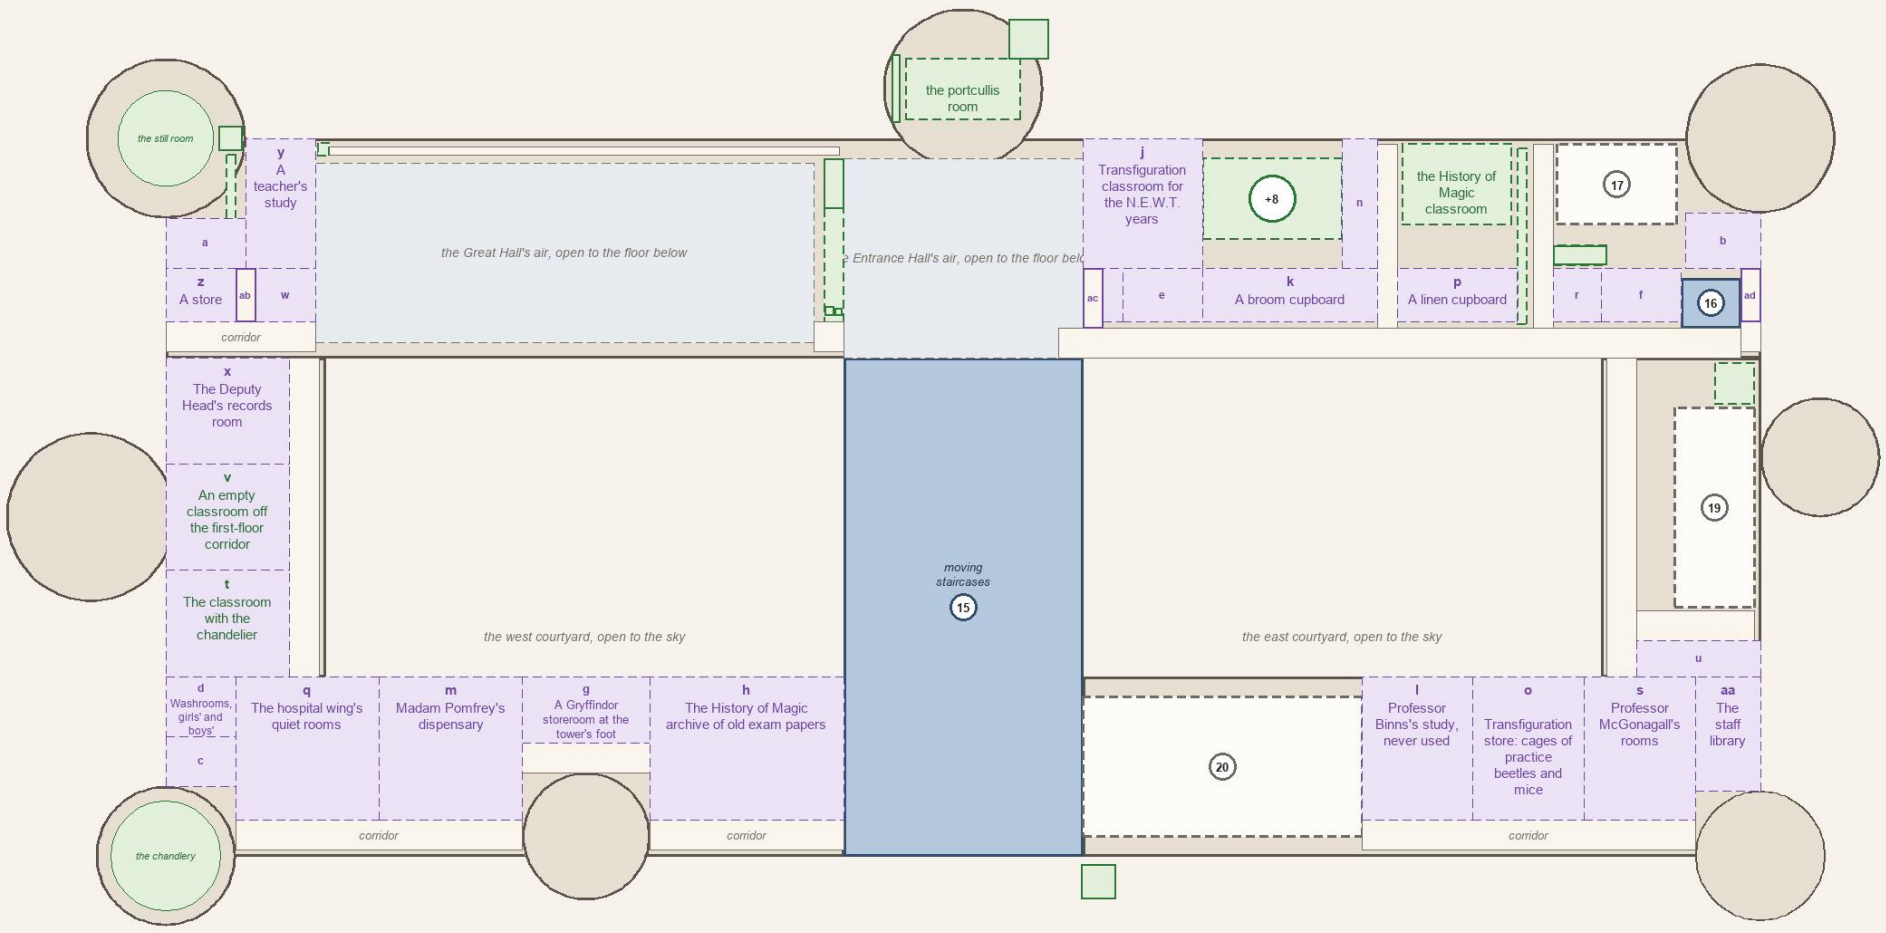

0 10 20 30 40 50 m

N

Named places on this floor (the step 3 sheet: numbers the first draft's, + the canon sweep's)

15 The moving staircases and the marble staircase in one hall, the front doors to the cliff face [books] (PS 8)
16 McGonagall's study, first floor (off the list [books] (PS 15)
17 Transfiguration classroom, beside her study [proposed]
19 Hospital wing [proposed] (PS 8)
20 History of Magic classroom, "large enough" for a class [proposed] (PoA 12)
+8 The first-floor room over Filch's office (OotP 28, CoS 8) [canon]

The model's rooms with no number (page/castle-model.js, version 71)

the first floor's corridor (first-floor-corridor)
the first floor's corridor down the east range (east-first-floor-corridor)
the passage outside the hospital wing (hospital-passage)
Madam Pomfrey's office (pomfrey-office)
the passage to the Transfiguration classroom (transfiguration-passage)
the back stair's lobby on 1 (back-stair-lobby-1)
the History of Magic classroom (history-of-magic-classroom)
the passage to the History of Magic classroom (history-of-magic-passage)
the narrow way behind the History of Magic classroom's cold fireplace (history-hearth-way)
the hall's wall passage (hall-wall-passage)
the lug over the staff table (hall-lug)
the wall passage's west leg (hall-wall-passage-west)
the portcullis room (portcullis-room)
the tapestry stair's well (tapestry-stairwell)
the passage from the West Tower's stair south to its stair foot on the first floor (west-tower-way-1)

Open to the floor below (a hall or room rising through this storey)

the Entrance Hall's air, 24 by 20 m
the Great Hall's air, 50 by 18 m

The towers at this level

Astronomy Tower: its stair to the top
Ravenclaw Tower: its tight spiral stair (+23)
Gryffindor Tower: below the common room: the house's storerooms (ours)
West Tower: its stair; Flitwick's office on 7 (42)
North Tower: its spiral from the seventh floor (+3) to the tiny landing at +45.4
south-west tower: a stair and staff rooms (ours)
south-east tower: blank, but the model room on 4 (H40) and the casemate round its foot on B (H41)
Dumbledore's tower: the gargoyle's moving stair on 7 (41)

Cores not on this floor (a named place takes the spot)

The Astronomy Tower's stair foot, its stair to the top: the Entrance Hall's air takes it

This sheet's fill, every space given a use (green: canon, purple: ours)


a The West Tower's stair foot, a stair between every floor [ours: PS 8: "a hundred and forty-two staircases"] core, 8 by 5 m; in by passage ab, shared
b The North Tower's stair foot, a stair between every floor [ours: PS 8: "a hundred and forty-two staircases"] core, 8 by 6 m; in by passage ad
c The south-west tower's stair foot, a stair between every floor [ours: PS 8: "a hundred and forty-two staircases"] core, 7 by 5 m
d Washrooms, girls' and boys' [ours] core, 7 by 6 m
e Washrooms, girls' and boys' [ours] core, 8 by 5 m
f Washrooms, girls' and boys' [ours] core, 8 by 5 m
g A Gryffindor storeroom at the tower's foot [ours] core, 13 by 7 m
h The History of Magic archive of old exam papers [ours] south range, west, 19 by 14 m
i A service passage [ours] north range, 2 by 5 m
j Transfiguration classroom for the N.E.W.T. years [ours] north range, 12 by 13 m; in by passage ac
k A broom cupboard [ours] north range, 18 by 5 m
l Professor Binns's study, never used [ours] south range, east, 11 by 14 m
m Madam Pomfrey's dispensary [ours] south range, west, 14 by 14 m
n A store of spare desks and chairs [ours] north range, 4 by 13 m; opens off history of magic passage
o Transfiguration store: cages of practice beetles and mice [ours] south range, east, 11 by 14 m
p A linen cupboard [ours] north range, 12 by 5 m
q The hospital wing's quiet rooms [ours] south range, west, 14 by 14 m
r Filch's cleaning cupboard [ours] north range, 5 by 5 m
s Professor McGonagall's rooms [ours] south range, east, 11 by 14 m
t The classroom with the chandelier [canon: OotP 18] west range, 12 by 11 m
u A store of old textbooks [ours] east range, 12 by 4 m
v An empty classroom off the first-floor corridor [canon: OotP 32] west range, 12 by 11 m
w The hospital wing's linen room [ours] north range, 6 by 5 m
x The Deputy Head's records room [ours] west range, 12 by 11 m
y A teacher's study [ours] north range, 7 by 13 m; in by passage ab, shared
z A store [ours] north range, 7 by 5 m
aa The staff library [ours] south range, east, 6 by 12 m
ab A passage to the rooms behind [ours: Godric's note, 15 October 2026, 4.12 pm] north range, 2.0 by 5.4 m, to a and y
ac A passage to the rooms behind [ours: Godric's note, 15 October 2026, 4.12 pm] north range, 2.0 by 6.0 m, to j
ad A passage to the rooms behind [ours: Godric's note, 15 October 2026, 4.12 pm] north range, 2.0 by 5.4 m, to b

The castle's layout, the second floor

The Architect, 20 October 2026, for Godric, on the castle model, version 71. Under 1.1, 2.1, 3.1 and Q48b's 3. North up; the bar 50 m. Numbers: the step 3 sheet's places (+ the canon sweep's); letters, purple: this sheet's fill, every space given a use.

Second floor

floor at +10.4 m

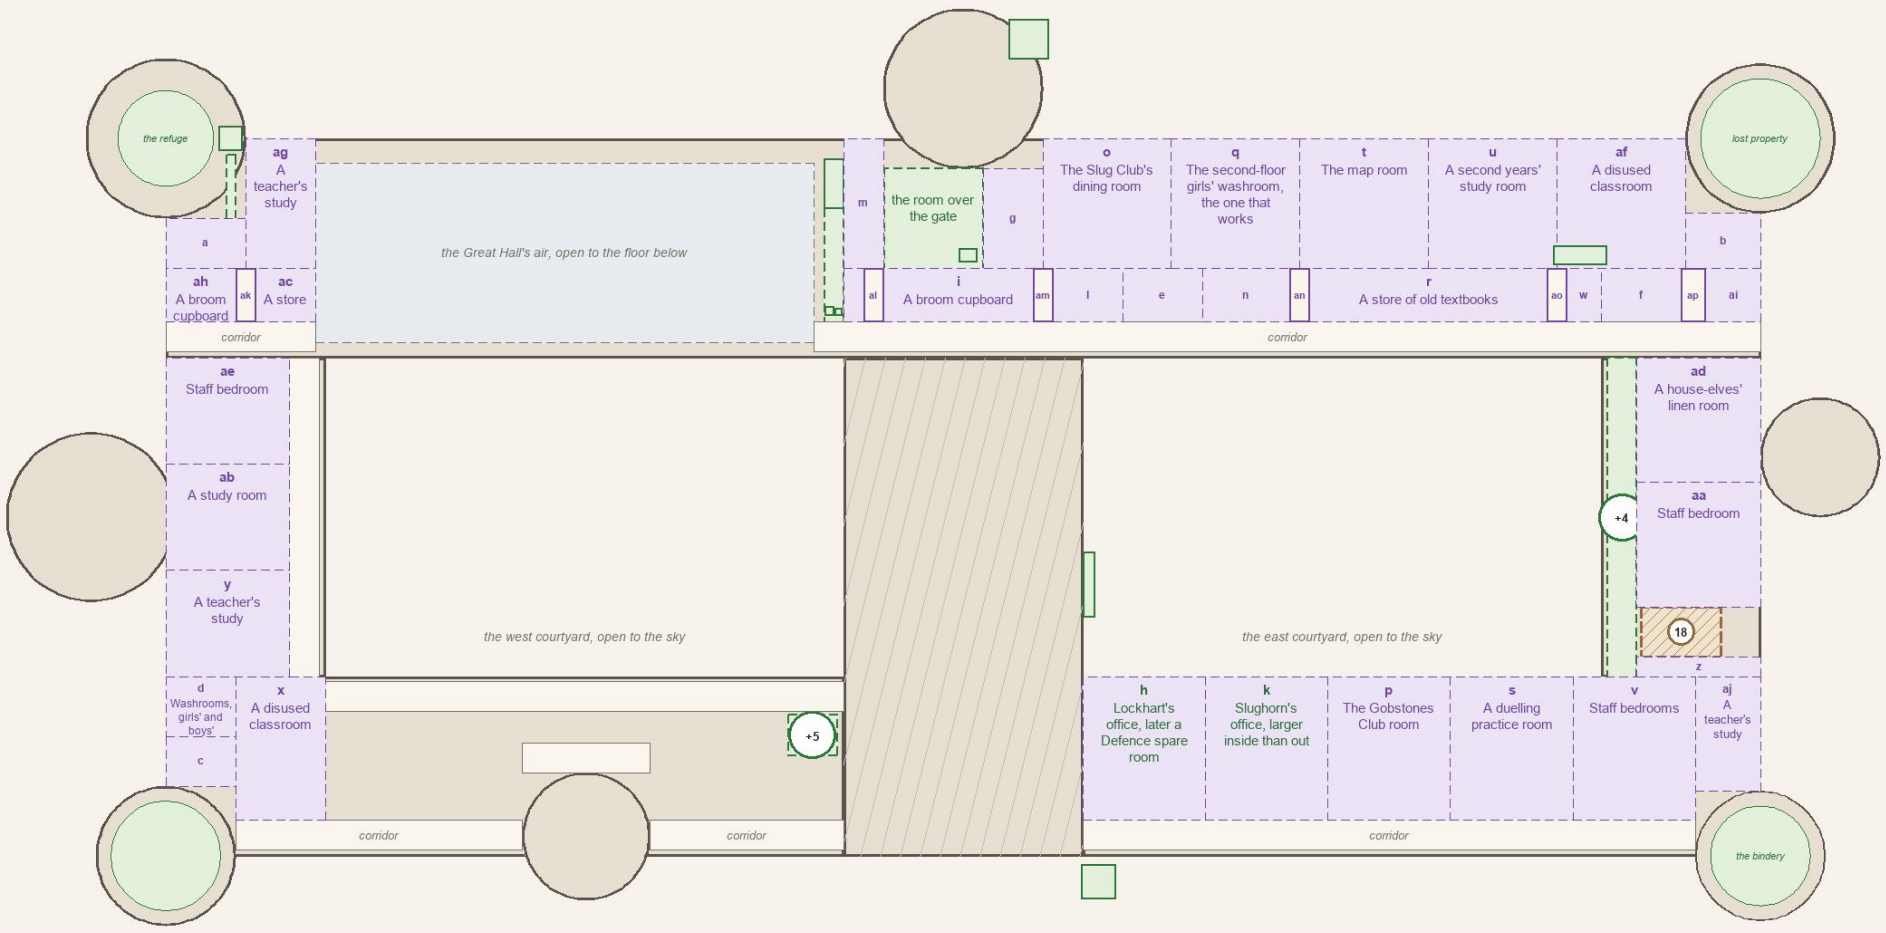

0 10 20 30 40 50 m

N

Named places on this floor (the step 3 sheet: numbers the first draft's, + the canon sweep's)

18 The second-floor girls' bathroom, Myrtle's (CoS 8, GoF 22, GoF 25) [designed] (CoS 8, GoF 22)
+4 The second-floor corridor by Myrtle's door (CoS 8, 16) [canon]
+7 The trick-step tapestry stair, four down to two (GoF 25, HBP 14) [canon]
+29 A second-floor corridor, one floor below the Defence office (OotP 28) [canon]
+5 The Defence office, its corridor's suit of armour (OotP 13, 29) [canon]

The model's rooms with no number (page/castle-model.js, version 71)

the second floor's corridor (second-floor-corridor)
the back stair's lobby on 2 (back-stair-lobby-2)
the room over the gate (gate-room)
the passage from the West Tower's stair south to its stair foot on the second floor (west-tower-way-2)

Open to the floor below (a hall or room rising through this storey)

the Great Hall's air, 50 by 18 m
the tapestry stair's well's air, 5 by 2 m

The towers at this level

Astronomy Tower: its stair to the top
Ravenclaw Tower: its tight spiral stair (+23)
Gryffindor Tower: below the common room: the house's storerooms (ours)
West Tower: its stair; Flitwick's office on 7 (42)
North Tower: its spiral from the seventh floor (+3) to the tiny landing at +45.4
south-west tower: a stair and staff rooms (ours)
south-east tower: blank, but the model room on 4 (H40) and the casemate round its foot on B (H41)
Dumbledore's tower: the gargoyle's moving stair on 7 (41)

Cores not on this floor (a named place takes the spot)

A Gryffindor storeroom at the tower's foot: the second floor's corridor takes it

This sheet's fill, every space given a use (green: canon, purple: ours)


a The West Tower's stair foot, a stair between every floor [ours: PS 8: "a hundred and forty-two staircases"] core, 8 by 5 m; in by passage ak, shared
b The North Tower's stair foot, a stair between every floor [ours: PS 8: "a hundred and forty-two staircases"] core, 8 by 6 m; in by passage ap
c The south-west tower's stair foot, a stair between every floor [ours: PS 8: "a hundred and forty-two staircases"] core, 7 by 5 m
d Washrooms, girls' and boys' [ours] core, 7 by 6 m
e Washrooms, girls' and boys' [ours] core, 8 by 5 m
f Washrooms, girls' and boys' [ours] core, 8 by 5 m
g The Astronomy Tower's stair foot, its stair to the top [ours] core, 6 by 10 m; in by passage am, shared
h Lockhart's office, later a Defence spare room [canon: CoS 7, CoS 9, CoS 16] south range, east, 12 by 14 m
i A broom cupboard [ours] north range, 15 by 5 m
j A service passage [ours] north range, 2 by 5 m
k Slughorn's office, larger inside than out [canon: HBP 15: up the marble staircase; its floor ours] south range, east, 12 by 14 m
l A store of spare desks and chairs [ours] north range, 7 by 5 m
m A linen cupboard [ours] north range, 4 by 13 m; in by passage al
n Filch's cleaning cupboard [ours] north range, 9 by 5 m
o The Slug Club's dining room [ours: the club canon (HBP 7)] north range, 13 by 13 m; in by passage am, shared
p The Gobstones Club room [ours: the club canon (OotP 17)] south range, east, 12 by 14 m
q The second-floor girls' washroom, the one that works [ours] north range, 13 by 13 m; in by passage an, shared
r A store of old textbooks [ours] north range, 24 by 5 m
s A duelling practice room [ours] south range, east, 12 by 14 m
t The map room [ours] north range, 13 by 13 m; in by passage an, shared
u A second years' study room [ours] north range, 13 by 13 m; in by passage ao, shared
v Staff bedrooms [ours] south range, east, 12 by 14 m
w A lamp and candle cupboard [ours] north range, 3 by 5 m
x A disused classroom [ours] south range, west, 9 by 14 m
y A teacher's study [ours] west range, 12 by 11 m
z A service passage [ours] east range, 12 by 2 m
aa Staff bedroom [ours] east range, 12 by 12 m
ab A study room [ours] west range, 12 by 11 m
ac A store [ours] north range, 6 by 5 m
ad A house-elves' linen room [ours] east range, 12 by 12 m
ae Staff bedroom [ours] west range, 12 by 11 m
af A disused classroom [ours] north range, 13 by 13 m; in by passage ao, shared
ag A teacher's study [ours] north range, 7 by 13 m; in by passage ak, shared
ah A broom cupboard [ours] north range, 7 by 5 m
ai A store of spare desks and chairs [ours] north range, 6 by 5 m
aj A teacher's study [ours] south range, east, 6 by 12 m
ak A passage to the rooms behind [ours: Godric's note, 15 October 2026, 4.12 pm] north range, 2.0 by 5.4 m, to a and ag
al A passage to the rooms behind [ours: Godric's note, 15 October 2026, 4.12 pm] north range, 2.0 by 5.4 m, to m
am A passage to the rooms behind [ours: Godric's note, 15 October 2026, 4.12 pm] north range, 2.0 by 5.4 m, to g and o
an A passage to the rooms behind [ours: Godric's note, 15 October 2026, 4.12 pm] north range, 2.0 by 5.4 m, to q and t
ao A passage to the rooms behind [ours: Godric's note, 15 October 2026, 4.12 pm] north range, 2.0 by 5.4 m, to u and af
ap A passage to the rooms behind [ours: Godric's note, 15 October 2026, 4.12 pm] north range, 2.5 by 5.4 m, to b

The castle's layout, the third floor

The Architect, 20 October 2026, for Godric, on the castle model, version 71. Under 1.1, 2.1, 3.1 and Q48b's 3. North up; the bar 50 m. Numbers: the step 3 sheet's places (+ the canon sweep's); letters, purple: this sheet's fill, every space given a use.

Third floor

floor at +15.6 m

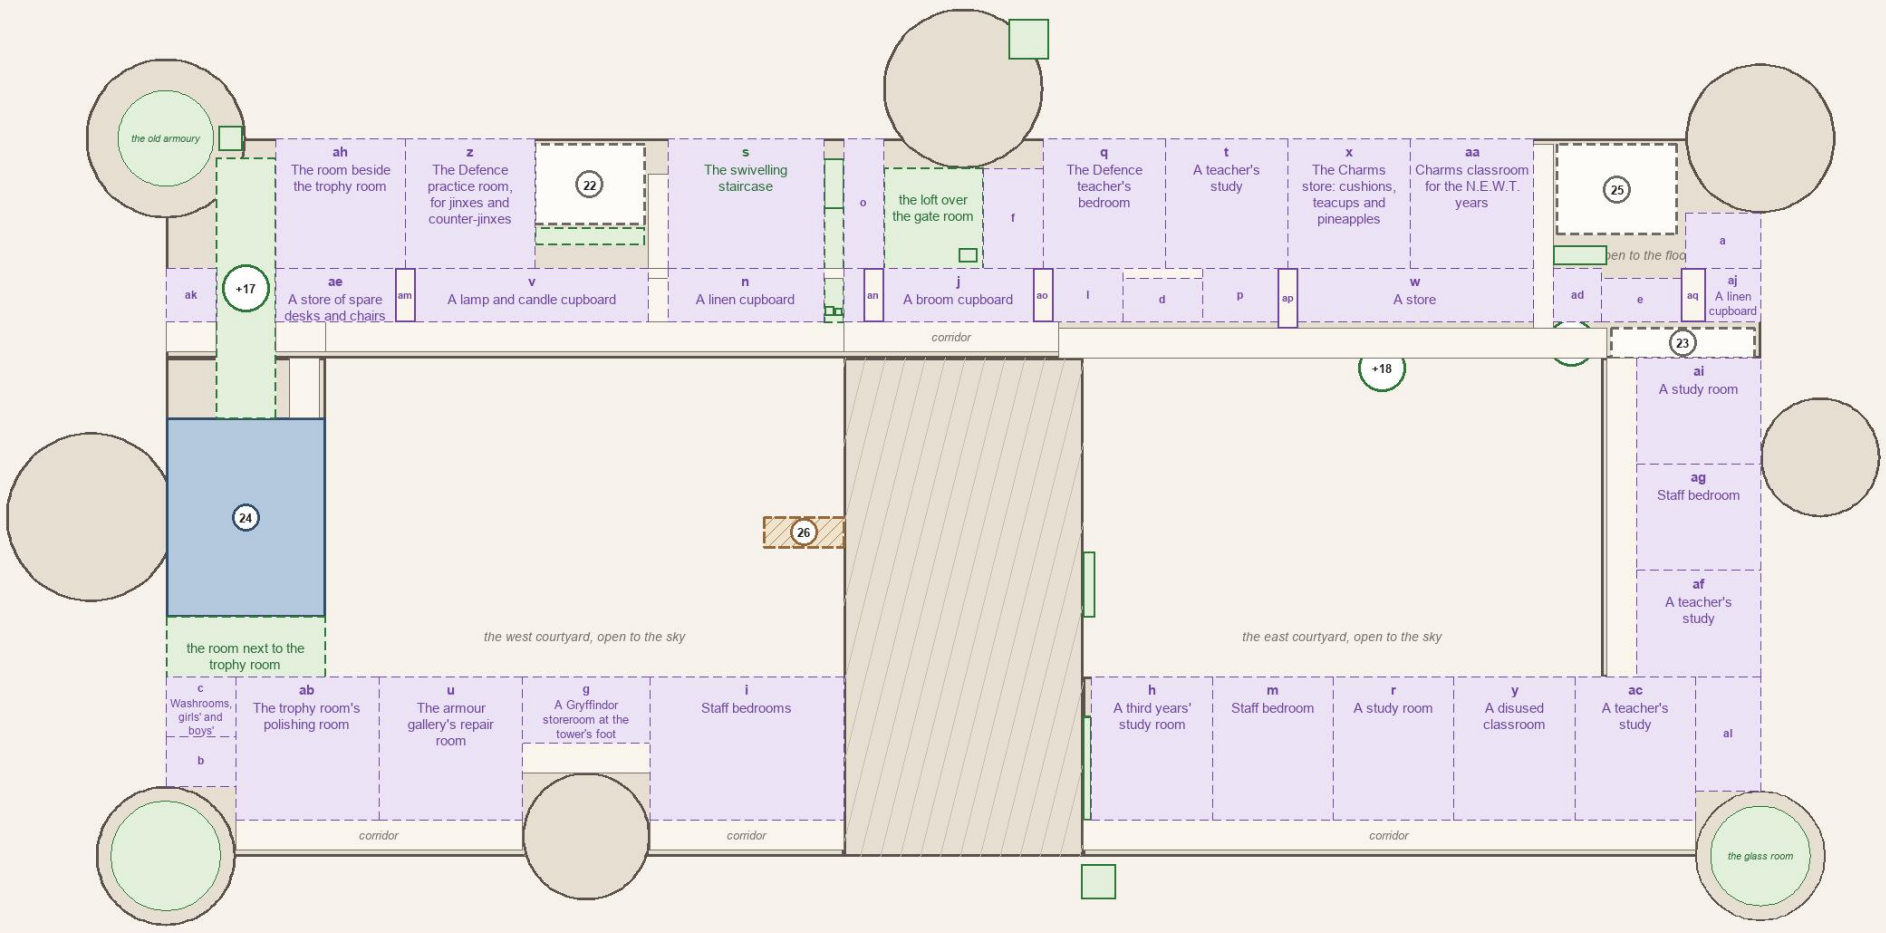

0 10 20 30 40 50 m

N

Named places on this floor (the step 3 sheet: numbers the first draft's, + the canon sweep's)

22 Defence Against the Dark Arts classroom [proposed] (PoA 9)
23 The third-floor corridor behind the locked door at the Charms corridor's end (model data, never walked) [proposed] (PS 7)
24 Trophy room, third floor (the spot proposed) [books] (PS 9)
25 Charms classroom [proposed] (PS 9)
26 The one-eyed witch's landing, directly beneath the corridor's landing, on the stair hall's well [designed] (PoA 10, 14)
+15 The Charms corridor, ending at a locked door (PS 9) [canon]
+17 The long gallery of armour, by the trophy room (PS 9) [canon]
+18 The drunk monks, by the Charms corridor (HBP 17) [canon]

The model's rooms with no number (page/castle-model.js, version 71)

the room next to the trophy room (trophy-next-room)
the third floor's corridor along the west courtyard (third-floor-north-corridor)
the passage to the Defence classroom (defence-passage)
the Defence store of dark creatures in crates (defence-store)
the Charms corridor (charms-corridor)
the passage to the Charms classroom (charms-passage)
the back stair's lobby on 3 (back-stair-lobby-3)
the passage behind the tapestries (tapestry-passage-3)
the loft over the gate room (gate-loft)
the stair that never moves (keep-east-stairwell)

Open to the floor below (a hall or room rising through this storey)

the tapestry stair's well's air, 5 by 2 m

The towers at this level

Astronomy Tower: its stair to the top
Ravenclaw Tower: its tight spiral stair (+23)
Gryffindor Tower: below the common room: the house's storerooms (ours)
West Tower: its stair; Flitwick's office on 7 (42)
North Tower: its spiral from the seventh floor (+3) to the tiny landing at +45.4
south-west tower: a stair and staff rooms (ours)
south-east tower: blank, but the model room on 4 (H40) and the casemate round its foot on B (H41)
Dumbledore's tower: the gargoyle's moving stair on 7 (41)

Cores not on this floor (a named place takes the spot)

The West Tower's stair foot, a stair between every floor: +17 takes it

This sheet's fill, every space given a use (green: canon, purple: ours)


a The North Tower's stair foot, a stair between every floor [ours: PS 8: "a hundred and forty-two staircases"] core, 8 by 6 m; in by passage aq
b The south-west tower's stair foot, a stair between every floor [ours: PS 8: "a hundred and forty-two staircases"] core, 7 by 5 m
c Washrooms, girls' and boys' [ours] core, 7 by 6 m
d Washrooms, girls' and boys' [ours] core, 8 by 4 m
e Washrooms, girls' and boys' [ours] core, 8 by 4 m
f The Astronomy Tower's stair foot, its stair to the top [ours] core, 6 by 10 m; in by passage ao, shared
g A Gryffindor storeroom at the tower's foot [ours] core, 13 by 7 m
h A third years' study room [ours] south range, east, 12 by 14 m
i Staff bedrooms [ours] south range, west, 19 by 14 m
j A broom cupboard [ours] north range, 15 by 5 m
k A service passage [ours] north range, 2 by 5 m
l A store of spare desks and chairs [ours] north range, 7 by 5 m
m Staff bedroom [ours] south range, east, 12 by 14 m
n A linen cupboard [ours] north range, 16 by 5 m
o Filch's cleaning cupboard [ours] north range, 4 by 13 m; in by passage an
p A house-elves' linen room [ours] north range, 8 by 5 m
q The Defence teacher's bedroom [ours] north range, 12 by 13 m; in by passage ao, shared
r A study room [ours] south range, east, 12 by 14 m
s The swivelling staircase [canon: OotP 32] north range, 16 by 13 m; opens off defence passage
t A teacher's study [ours] north range, 12 by 13 m; in by passage ap, shared
u The armour gallery's repair room [ours] south range, west, 14 by 14 m
v A lamp and candle cupboard [ours] north range, 23 by 5 m
w A store [ours] north range, 24 by 5 m
x The Charms store: cushions, teacups and pineapples [ours] north range, 12 by 13 m; in by passage ap, shared
y A disused classroom [ours] south range, east, 12 by 14 m
z The Defence practice room, for jinxes and counter-jinxes [ours] north range, 13 by 13 m; in by passage am, shared
aa Charms classroom for the N.E.W.T. years [ours] north range, 12 by 13 m; opens off charms passage
ab The trophy room's polishing room [ours] south range, west, 14 by 14 m
ac A teacher's study [ours] south range, east, 12 by 14 m
ad A broom cupboard [ours] north range, 5 by 5 m
ae A store of spare desks and chairs [ours] north range, 12 by 5 m
af A teacher's study [ours] east range, 12 by 11 m
ag Staff bedroom [ours] east range, 12 by 11 m
ah The room beside the trophy room [ours] north range, 13 by 13 m; in by passage am, shared
ai A study room [ours] east range, 12 by 11 m
aj A linen cupboard [ours] north range, 6 by 5 m
ak Filch's cleaning cupboard [ours] north range, 5 by 5 m
al A house-elves' linen room [ours] south range, east, 6 by 12 m
am A passage to the rooms behind [ours: Godric's note, 15 October 2026, 4.12 pm] north range, 2.0 by 5.4 m, to ah and z
an A passage to the rooms behind [ours: Godric's note, 15 October 2026, 4.12 pm] north range, 2.0 by 5.4 m, to o
ao A passage to the rooms behind [ours: Godric's note, 15 October 2026, 4.12 pm] north range, 2.0 by 5.4 m, to f and q
ap A passage to the rooms behind [ours: Godric's note, 15 October 2026, 4.12 pm] north range, 2.0 by 6.0 m, to t and x
aq A passage to the rooms behind [ours: Godric's note, 15 October 2026, 4.12 pm] north range, 2.5 by 5.4 m, to a

The castle's layout, the fourth floor

The Architect, 20 October 2026, for Godric, on the castle model, version 71. Under 1.1, 2.1, 3.1 and Q48b's 3. North up; the bar 50 m. Numbers: the step 3 sheet's places (+ the canon sweep's); letters, purple: this sheet's fill, every space given a use.

Fourth floor

floor at +20.8 m

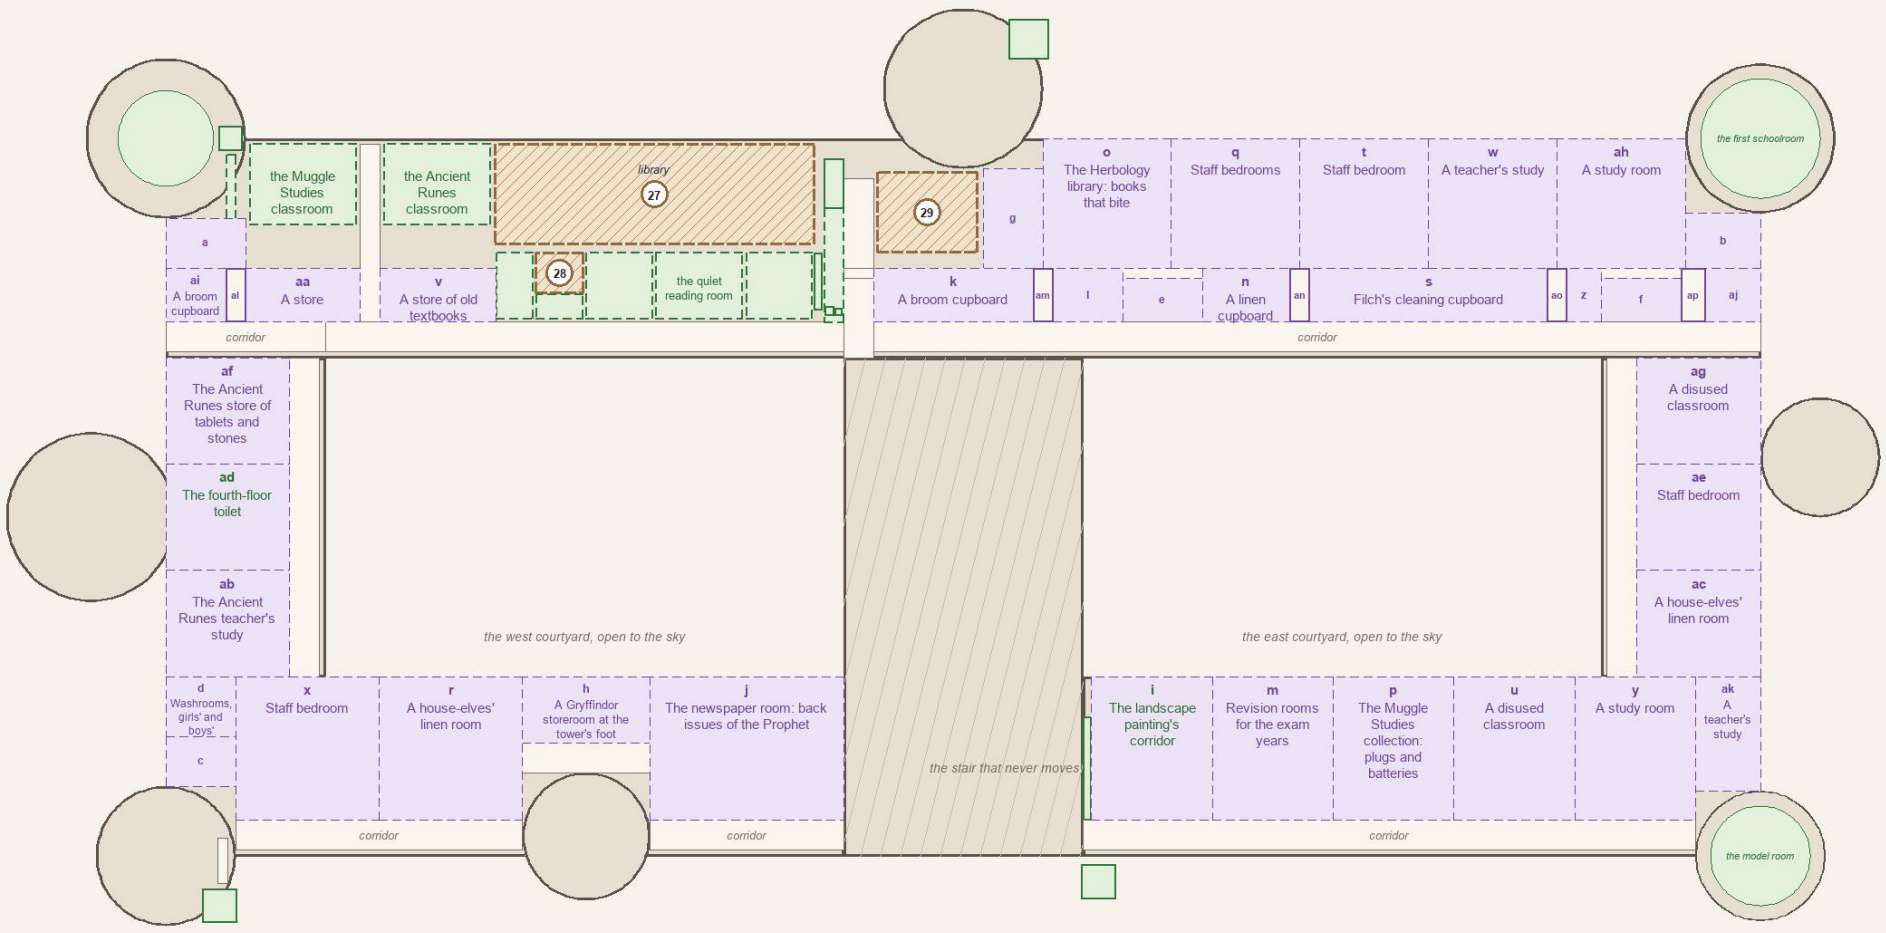

0 10 20 30 40 50 m

N

Named places on this floor (the step 3 sheet: numbers the first draft's, + the canon sweep's)

27 Library, the Restricted Section at the back [designed] (PS 12)
28 The Muggle Studies room, past the last stack (Magic) [designed]
29 The forgotten classroom, desks stacked against the walls (PS 12) [designed] (PS 12)
30 The passage behind the mirror, fourth floor, caved in [inferred] (PoA 10, OotP 17)

The model's rooms with no number (page/castle-model.js, version 71)

the fourth floor's corridor along the west courtyard (fourth-floor-corridor)
the corridor to the library (library-corridor)
Madam Pince's office and book-mending room (pince-office)
the quiet reading room (library-reading-room)
the library's map and atlas room (library-map-room)
the Muggle Studies collection's store (muggle-studies-store)
the Muggle Studies teacher's study (muggle-studies-study)
the back stair's lobby on 4 (back-stair-lobby-4)
the service passage along the cupboard row's back on 4 (elves-passage-4)
the short passage through the south-west drum's wall to its turret's foot (sw-turret-passage)
the passage from the West Tower's stair south to its stair foot on the fourth floor (west-tower-way-4)
the passage to the Muggle Studies and Ancient Runes classrooms (electives-passage-4)
the Ancient Runes classroom (ancient-runes-classroom)
the Muggle Studies classroom (muggle-studies-classroom)

Open to the floor below (a hall or room rising through this storey)

the stair that never moves's air, 1 by 10 m

The towers at this level

Astronomy Tower: its stair to the top
Ravenclaw Tower: its tight spiral stair (+23)
Gryffindor Tower: below the common room: the house's storerooms (ours)
West Tower: its stair; Flitwick's office on 7 (42)
North Tower: its spiral from the seventh floor (+3) to the tiny landing at +45.4
south-west tower: a stair and staff rooms (ours)
south-east tower: blank, but the model room on 4 (H40) and the casemate round its foot on B (H41)
Dumbledore's tower: the gargoyle's moving stair on 7 (41)

This sheet's fill, every space given a use (green: canon, purple: ours)


a The West Tower's stair foot, a stair between every floor [ours: PS 8: "a hundred and forty-two staircases"] core, 8 by 5 m; in by passage al
b The North Tower's stair foot, a stair between every floor [ours: PS 8: "a hundred and forty-two staircases"] core, 8 by 6 m; in by passage ap
c The south-west tower's stair foot, a stair between every floor [ours: PS 8: "a hundred and forty-two staircases"] core, 7 by 5 m
d Washrooms, girls' and boys' [ours] core, 7 by 6 m
e Washrooms, girls' and boys' [ours] core, 8 by 4 m
f Washrooms, girls' and boys' [ours] core, 8 by 4 m
g The Astronomy Tower's stair foot, its stair to the top [ours] core, 6 by 10 m; in by passage am, shared
h A Gryffindor storeroom at the tower's foot [ours] core, 13 by 7 m
i The landscape painting's corridor [canon: PoA 8] south range, east, 12 by 14 m
j The newspaper room: back issues of the Prophet [ours] south range, west, 19 by 14 m
k A broom cupboard [ours] north range, 16 by 5 m
l A store of spare desks and chairs [ours] north range, 7 by 5 m
m Revision rooms for the exam years [ours] south range, east, 12 by 14 m
n A linen cupboard [ours] north range, 9 by 5 m
o The Herbology library: books that bite [ours] north range, 13 by 13 m; in by passage am, shared
p The Muggle Studies collection: plugs and batteries [ours: a nod to CoS 3] south range, east, 12 by 14 m
q Staff bedrooms [ours] north range, 13 by 13 m; in by passage an, shared
r A house-elves' linen room [ours] south range, west, 14 by 14 m
s Filch's cleaning cupboard [ours] north range, 24 by 5 m
t Staff bedroom [ours] north range, 13 by 13 m; in by passage an, shared
u A disused classroom [ours] south range, east, 12 by 14 m
v A store of old textbooks [ours] north range, 12 by 5 m
w A teacher's study [ours] north range, 13 by 13 m; in by passage ao, shared
x Staff bedroom [ours] south range, west, 14 by 14 m
y A study room [ours] south range, east, 12 by 14 m
z A lamp and candle cupboard [ours] north range, 3 by 5 m
aa A store [ours] north range, 12 by 5 m
ab The Ancient Runes teacher's study [ours] west range, 12 by 11 m
ac A house-elves' linen room [ours] east range, 12 by 11 m
ad The fourth-floor toilet [canon: OotP 28] west range, 12 by 11 m
ae Staff bedroom [ours] east range, 12 by 11 m
af The Ancient Runes store of tablets and stones [ours] west range, 12 by 11 m
ag A disused classroom [ours] east range, 12 by 11 m
ah A study room [ours] north range, 13 by 13 m; in by passage ao, shared
ai A broom cupboard [ours] north range, 6 by 5 m
aj A store of spare desks and chairs [ours] north range, 6 by 5 m
ak A teacher's study [ours] south range, east, 6 by 12 m
al A passage to the rooms behind [ours: Godric's note, 15 October 2026, 4.12 pm] north range, 2.0 by 5.4 m, to a
am A passage to the rooms behind [ours: Godric's note, 15 October 2026, 4.12 pm] north range, 2.0 by 5.4 m, to g and o
an A passage to the rooms behind [ours: Godric's note, 15 October 2026, 4.12 pm] north range, 2.0 by 5.4 m, to q and t
ao A passage to the rooms behind [ours: Godric's note, 15 October 2026, 4.12 pm] north range, 2.0 by 5.4 m, to w and ah
ap A passage to the rooms behind [ours: Godric's note, 15 October 2026, 4.12 pm] north range, 2.5 by 5.4 m, to b

The castle's layout, the fifth floor

The Architect, 20 October 2026, for Godric, on the castle model, version 71. Under 1.1, 2.1, 3.1 and Q48b's 3. North up; the bar 50 m. Numbers: the step 3 sheet's places (+ the canon sweep's); letters, purple: this sheet's fill, every space given a use.

Fifth floor

floor at +26.0 m

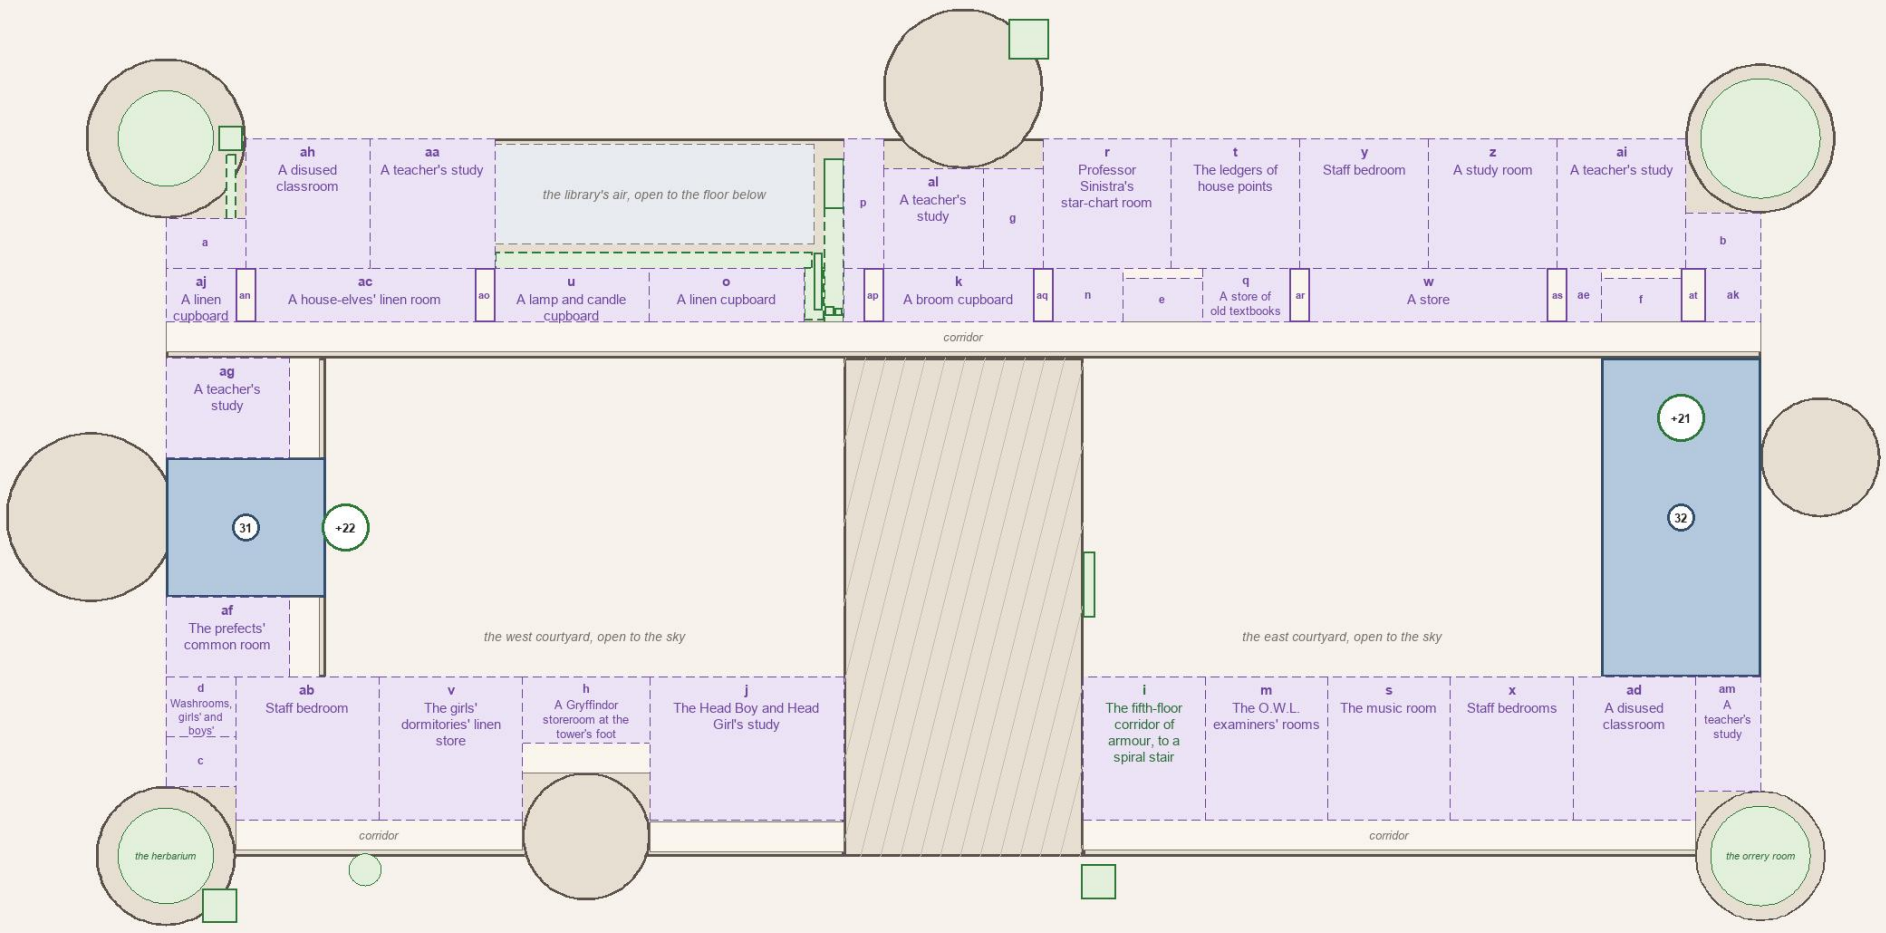

0 10 20 30 40 50 m

N

Named places on this floor (the step 3 sheet: numbers the first draft's, + the canon sweep's)

31 Prefects' bathroom, by Boris the Bewildered (the spot proposed) [books] (GoF 23)
32 The east wing, named on the fifth floor [books] (OotP 30)
+22 Boris the Bewildered; the fourth door to his left (GoF 23, 25) [canon]
+21 Gregory the Smarmy's corridor, the east wing (OotP 29, 30) [canon]

The model's rooms with no number (page/castle-model.js, version 71)

the fifth floor's corridor along the lake face (fifth-floor-south-corridor)
the back stair's lobby on 5 (back-stair-lobby-5)
the service passage along the cupboard row's back on 5 (elves-passage-5)
the gallery behind the library's shelves (library-gallery)
the head of the gallery's stair and the walk back to the gallery (library-gallery-way)
the hide in the chimney breast (chimney-hide)
the passage from the West Tower's stair south to its stair foot on the fifth floor (west-tower-way-5)

Open to the floor below (a hall or room rising through this storey)

the library's air, 32 by 10 m

The towers at this level

Astronomy Tower: its stair to the top
Ravenclaw Tower: its tight spiral stair (+23)
Gryffindor Tower: below the common room: the house's storerooms (ours)
West Tower: its stair; Flitwick's office on 7 (42)
North Tower: its spiral from the seventh floor (+3) to the tiny landing at +45.4
south-west tower: a stair and staff rooms (ours)
south-east tower: blank, but the model room on 4 (H40) and the casemate round its foot on B (H41)
Dumbledore's tower: the gargoyle's moving stair on 7 (41)

This sheet's fill, every space given a use (green: canon, purple: ours)


a The West Tower's stair foot, a stair between every floor [ours: PS 8: "a hundred and forty-two staircases"] core, 8 by 5 m; in by passage an, shared
b The North Tower's stair foot, a stair between every floor [ours: PS 8: "a hundred and forty-two staircases"] core, 8 by 6 m; in by passage at
c The south-west tower's stair foot, a stair between every floor [ours: PS 8: "a hundred and forty-two staircases"] core, 7 by 5 m
d Washrooms, girls' and boys' [ours] core, 7 by 6 m
e Washrooms, girls' and boys' [ours] core, 8 by 4 m
f Washrooms, girls' and boys' [ours] core, 8 by 4 m
g The Astronomy Tower's stair foot, its stair to the top [ours] core, 6 by 10 m; in by passage aq, shared
h A Gryffindor storeroom at the tower's foot [ours] core, 13 by 7 m
i The fifth-floor corridor of armour, to a spiral stair [canon: DH 29] south range, east, 12 by 14 m
j The Head Boy and Head Girl's study [ours] south range, west, 19 by 14 m
k A broom cupboard [ours] north range, 15 by 5 m
l A service passage [ours] north range, 2 by 5 m
m The O.W.L. examiners' rooms [ours] south range, east, 12 by 14 m
n A store of spare desks and chairs [ours] north range, 7 by 5 m
o A linen cupboard [ours] north range, 16 by 5 m
p Filch's cleaning cupboard [ours] north range, 4 by 13 m; in by passage ap
q A store of old textbooks [ours] north range, 9 by 5 m
r Professor Sinistra's star-chart room [ours] north range, 13 by 13 m; in by passage aq, shared
s The music room [ours] south range, east, 12 by 14 m
t The ledgers of house points [ours] north range, 13 by 13 m; in by passage ar, shared
u A lamp and candle cupboard [ours] north range, 16 by 5 m
v The girls' dormitories' linen store [ours] south range, west, 14 by 14 m
w A store [ours] north range, 24 by 5 m
x Staff bedrooms [ours] south range, east, 12 by 14 m
y Staff bedroom [ours] north range, 13 by 13 m; in by passage ar, shared
z A study room [ours] north range, 13 by 13 m; in by passage as, shared
aa A teacher's study [ours] north range, 12 by 13 m; in by passage ao
ab Staff bedroom [ours] south range, west, 14 by 14 m
ac A house-elves' linen room [ours] north range, 22 by 5 m
ad A disused classroom [ours] south range, east, 12 by 14 m
ae A store of spare desks and chairs [ours] north range, 3 by 5 m
af The prefects' common room [ours] west range, 12 by 8 m
ag A teacher's study [ours] west range, 12 by 10 m
ah A disused classroom [ours] north range, 12 by 13 m; in by passage an, shared
ai A teacher's study [ours] north range, 13 by 13 m; in by passage as, shared
aj A linen cupboard [ours] north range, 7 by 5 m
ak Filch's cleaning cupboard [ours] north range, 6 by 5 m
al A teacher's study [ours] north range, 10 by 10 m
am A teacher's study [ours] south range, east, 6 by 12 m
an A passage to the rooms behind [ours: Godric's note, 15 October 2026, 4.12 pm] north range, 2.0 by 5.4 m, to a and ah
ao A passage to the rooms behind [ours: Godric's note, 15 October 2026, 4.12 pm] north range, 2.0 by 5.4 m, to aa
ap A passage to the rooms behind [ours: Godric's note, 15 October 2026, 4.12 pm] north range, 2.0 by 5.4 m, to p
aq A passage to the rooms behind [ours: Godric's note, 15 October 2026, 4.12 pm] north range, 2.0 by 5.4 m, to g and r
ar A passage to the rooms behind [ours: Godric's note, 15 October 2026, 4.12 pm] north range, 2.0 by 5.4 m, to t and y
as A passage to the rooms behind [ours: Godric's note, 15 October 2026, 4.12 pm] north range, 2.0 by 5.4 m, to z and ai
at A passage to the rooms behind [ours: Godric's note, 15 October 2026, 4.12 pm] north range, 2.5 by 5.4 m, to b

The castle's layout, the sixth floor

The Architect, 20 October 2026, for Godric, on the castle model, version 71. Under 1.1, 2.1, 3.1 and Q48b's 3. North up; the bar 50 m. Numbers: the step 3 sheet's places (+ the canon sweep's); letters, purple: this sheet's fill, every space given a use.

Sixth floor

floor at +31.2 m

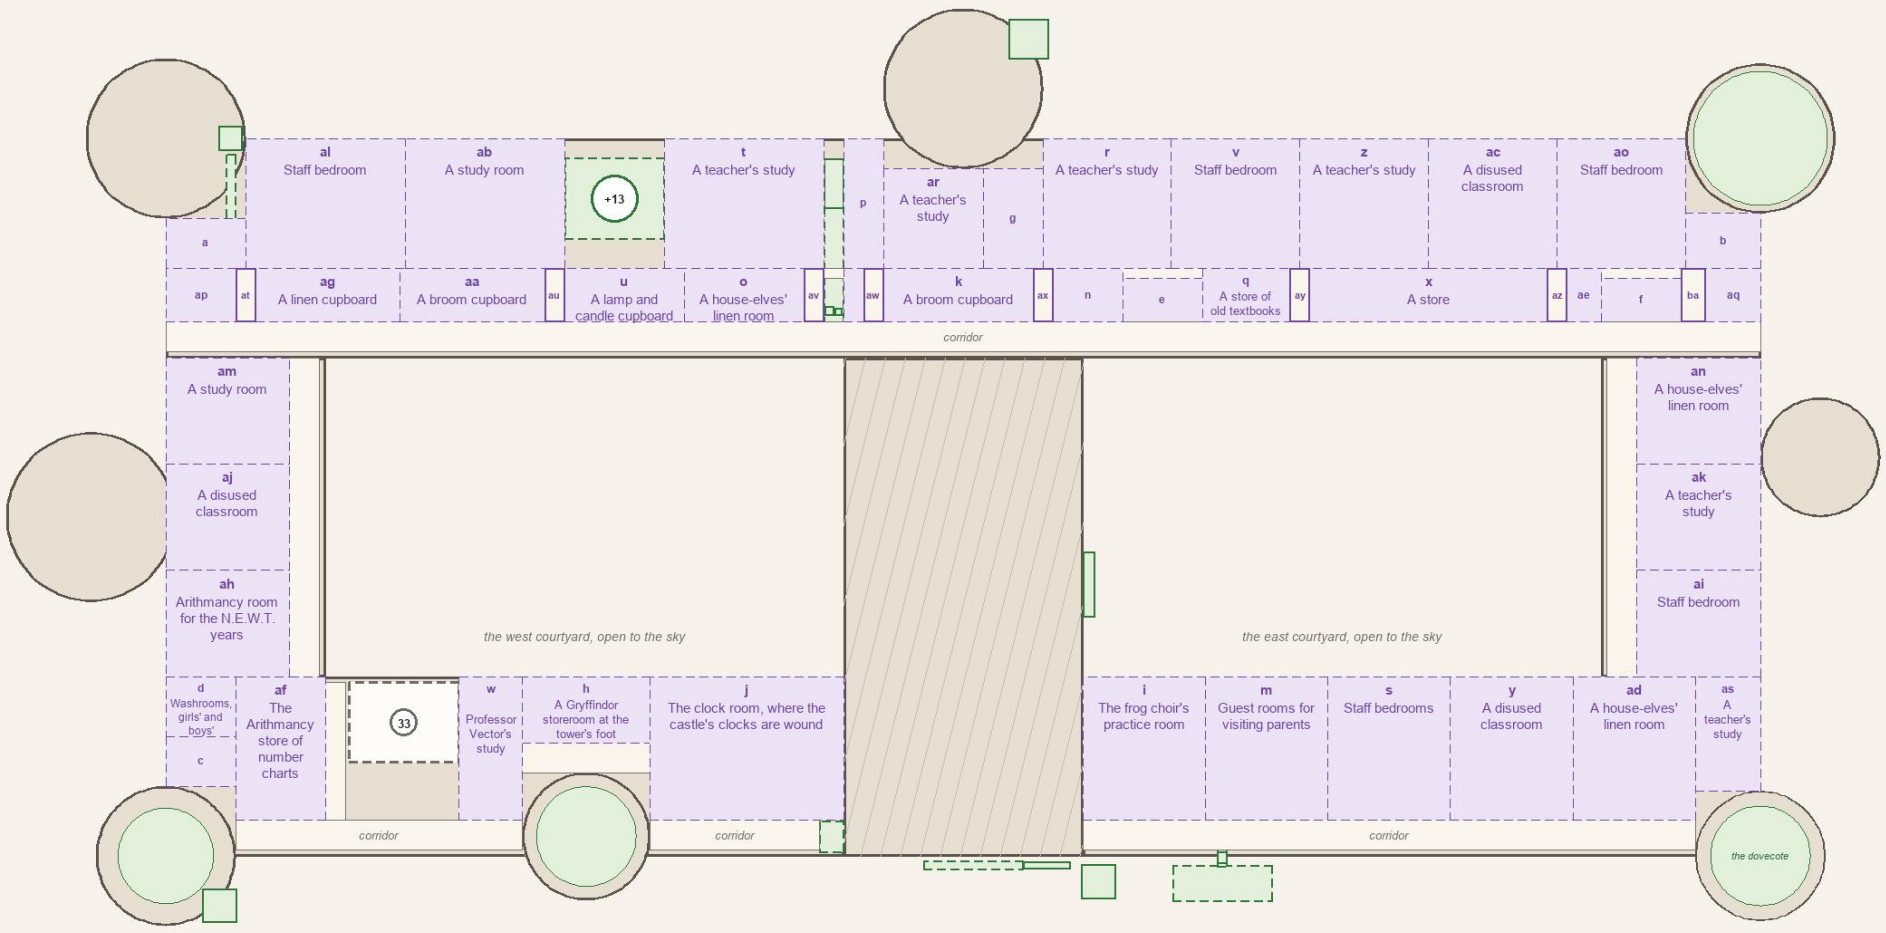

0 10 20 30 40 50 m

N

Named places on this floor (the step 3 sheet: numbers the first draft's, + the canon sweep's)

33 Arithmancy classroom (proposed) [proposed]
+13 A boys' bathroom on the sixth floor, the floor below the Room (HBP 24) [canon]

The model's rooms with no number (page/castle-model.js, version 71)

the back stair's lobby on 6 (back-stair-lobby-6)
the service passage along the cupboard row's back on 6 (elves-passage-6)
the store for the common room's fire (secret-s4b)
the founders' wall-walk (keep-wall-walk)
the room behind the rose (rose-room)
the short passage from the sixth floor's lake corridor to the room behind the rose (rose-room-way)
the passage from the West Tower's stair south to its stair foot on the sixth floor (west-tower-way-6)
the passage to the Arithmancy classroom (arithmancy-passage)

The towers at this level

Astronomy Tower: its stair to the top
Ravenclaw Tower: its tight spiral stair (+23)
Gryffindor Tower: below the common room: the house's storerooms (ours)
West Tower: its stair; Flitwick's office on 7 (42)
North Tower: its spiral from the seventh floor (+3) to the tiny landing at +45.4
south-west tower: a stair and staff rooms (ours)
south-east tower: blank, but the model room on 4 (H40) and the casemate round its foot on B (H41)
Dumbledore's tower: the gargoyle's moving stair on 7 (41)


This sheet's fill, every space given a use (green: canon, purple: ours)

a The West Tower's stair foot, a stair between every floor [ours: PS 8: "a hundred and forty-two staircases"] core, 8 by 5 m; in by passage at, shared
b The North Tower's stair foot, a stair between every floor [ours: PS 8: "a hundred and forty-two staircases"] core, 8 by 6 m; in by passage ba
c The south-west tower's stair foot, a stair between every floor [ours: PS 8: "a hundred and forty-two staircases"] core, 7 by 5 m
d Washrooms, girls' and boys' [ours] core, 7 by 6 m
e Washrooms, girls' and boys' [ours] core, 8 by 4 m
f Washrooms, girls' and boys' [ours] core, 8 by 4 m
g The Astronomy Tower's stair foot, its stair to the top [ours] core, 6 by 10 m; in by passage ax, shared
h A Gryffindor storeroom at the tower's foot [ours] core, 13 by 7 m
i The frog choir's practice room [ours] south range, east, 12 by 14 m
j The clock room, where the castle's clocks are wound [ours] south range, west, 19 by 14 m
k A broom cupboard [ours] north range, 15 by 5 m
l A service passage [ours] north range, 2 by 5 m
m Guest rooms for visiting parents [ours] south range, east, 12 by 14 m
n The telescope store [ours] north range, 7 by 5 m
o A house-elves' linen room [ours] north range, 12 by 5 m
p Filch's cleaning cupboard [ours] north range, 4 by 13 m; in by passage aw
q A store of old textbooks [ours] north range, 9 by 5 m
r A teacher's study [ours] north range, 13 by 13 m; in by passage ax, shared
s Staff bedrooms [ours] south range, east, 12 by 14 m
t A teacher's study [ours] north range, 16 by 13 m; in by passage av
u A lamp and candle cupboard [ours] north range, 12 by 5 m
v Staff bedroom [ours] north range, 13 by 13 m; in by passage ay, shared
w Professor Vector's study [ours: Arithmancy's teacher canon] south range, west, 6 by 14 m
x A store [ours] north range, 24 by 5 m
y A disused classroom [ours] south range, east, 12 by 14 m
z A teacher's study [ours] north range, 13 by 13 m; in by passage ay, shared
aa A broom cupboard [ours] north range, 14 by 5 m
ab A study room [ours] north range, 16 by 13 m; in by passage au
ac A disused classroom [ours] north range, 13 by 13 m; in by passage az, shared
ad A house-elves' linen room [ours] south range, east, 12 by 14 m
ae A store of spare desks and chairs [ours] north range, 3 by 5 m
af The Arithmancy store of number charts [ours] south range, west, 9 by 14 m
ag A linen cupboard [ours] north range, 14 by 5 m
ah Arithmancy room for the N.E.W.T. years [ours] west range, 12 by 11 m
ai Staff bedroom [ours] east range, 12 by 11 m
aj A disused classroom [ours] west range, 12 by 11 m
ak A teacher's study [ours] east range, 12 by 11 m
al Staff bedroom [ours] north range, 16 by 13 m; in by passage at, shared
am A study room [ours] west range, 12 by 11 m
an A house-elves' linen room [ours] east range, 12 by 11 m
ao Staff bedroom [ours] north range, 13 by 13 m; in by passage az, shared
ap Filch's cleaning cupboard [ours] north range, 7 by 5 m
aq A store of old textbooks [ours] north range, 6 by 5 m
ar A teacher's study [ours] north range, 10 by 10 m
as A teacher's study [ours] south range, east, 6 by 12 m
at A passage to the rooms behind [ours: Godric's note, 15 October 2026, 4.12 pm] north range, 2.0 by 5.4 m, to a and al
au A passage to the rooms behind [ours: Godric's note, 15 October 2026, 4.12 pm] north range, 2.0 by 5.4 m, to ab
av A passage to the rooms behind [ours: Godric's note, 15 October 2026, 4.12 pm] north range, 2.0 by 5.4 m, to t
aw A passage to the rooms behind [ours: Godric's note, 15 October 2026, 4.12 pm] north range, 2.0 by 5.4 m, to p
ax A passage to the rooms behind [ours: Godric's note, 15 October 2026, 4.12 pm] north range, 2.0 by 5.4 m, to g and r
ay A passage to the rooms behind [ours: Godric's note, 15 October 2026, 4.12 pm] north range, 2.0 by 5.4 m, to v and z
az A passage to the rooms behind [ours: Godric's note, 15 October 2026, 4.12 pm] north range, 2.0 by 5.4 m, to ac and ao
ba A passage to the rooms behind [ours: Godric's note, 15 October 2026, 4.12 pm] north range, 2.5 by 5.4 m, to b

The castle's layout, the seventh floor

The Architect, 20 October 2026, for Godric, on the castle model, version 71. Under 1.1, 2.1, 3.1 and Q48b's 3. North up; the bar 50 m. Numbers: the step 3 sheet's places (+ the canon sweep's); letters, purple: this sheet's fill, every space given a use.

Seventh floor: the built suite at true size, in place

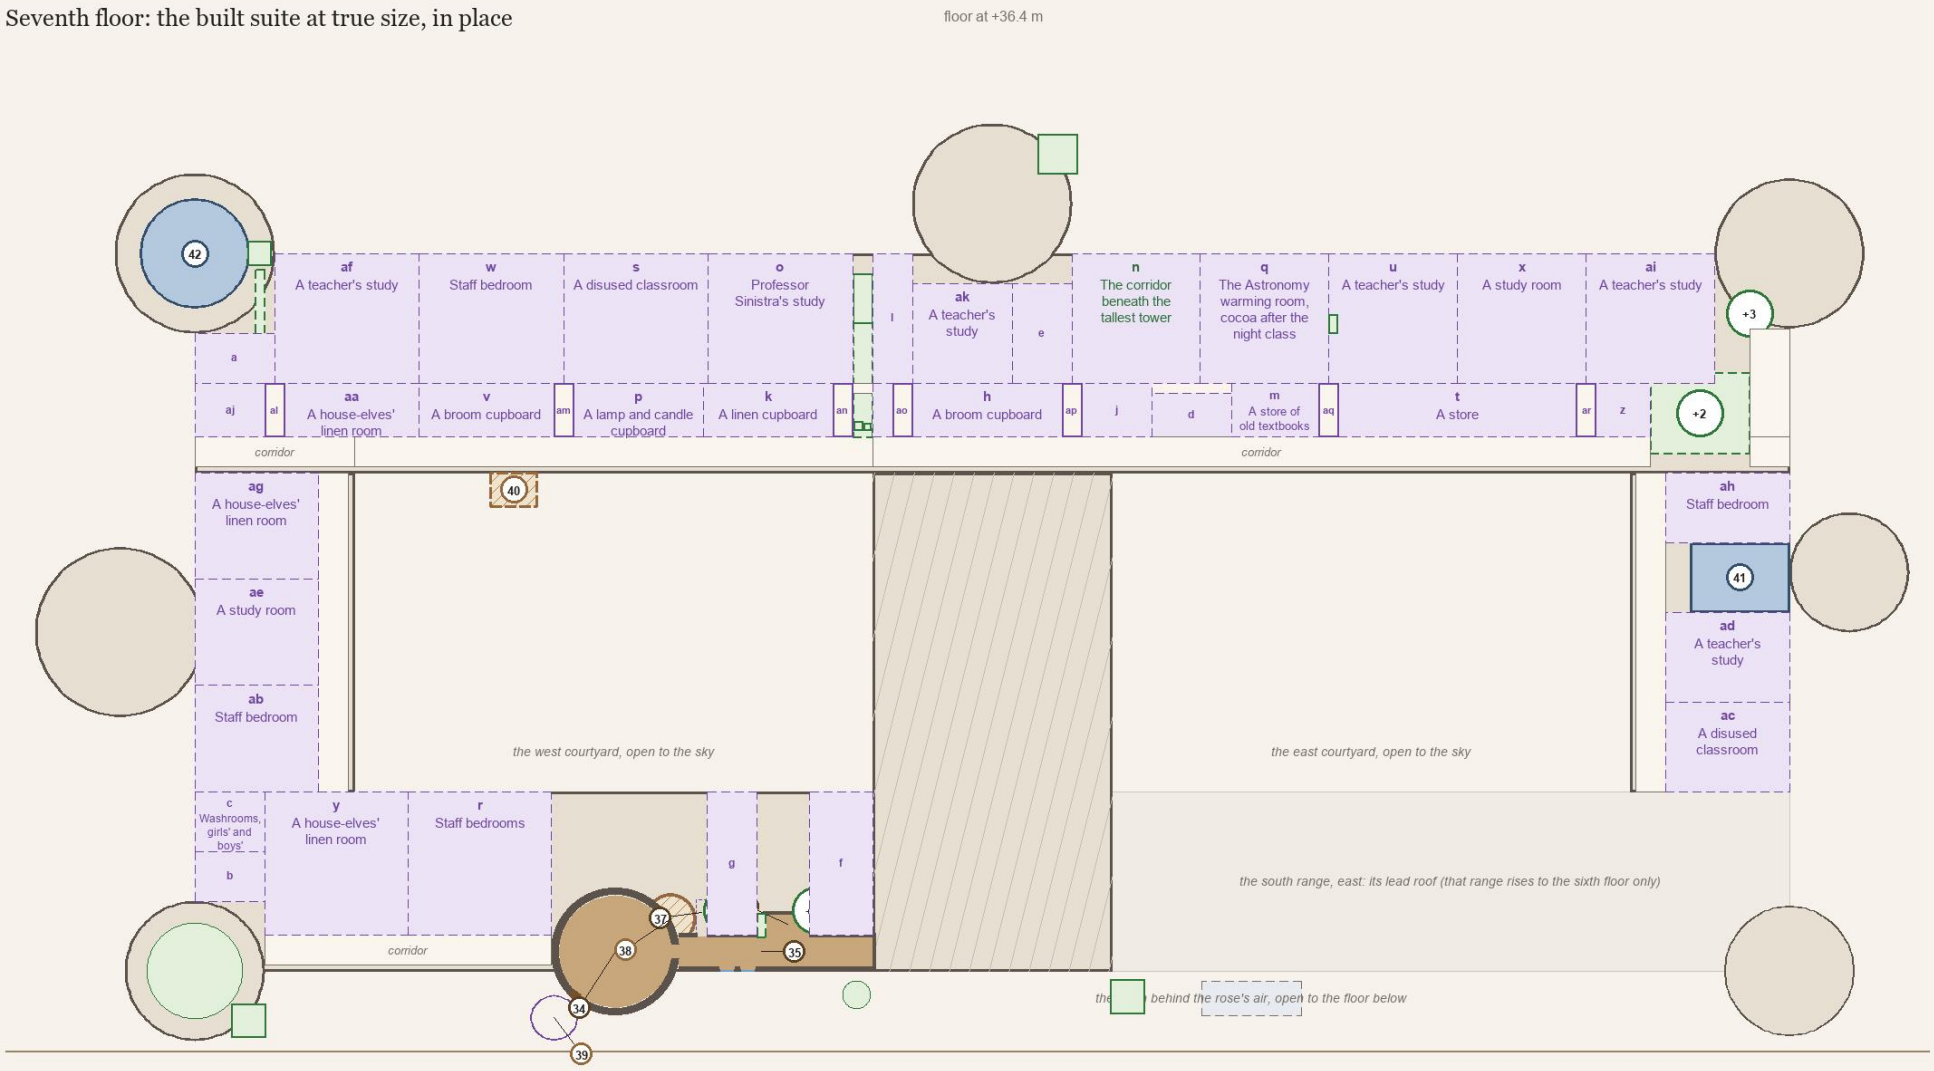

Named places on this floor (the step 3 sheet: numbers the first draft's, + the canon sweep's)

34 Gryffindor common room [built] (PS 9)
35 The Fat Lady's corridor [built] (PS 7, OotP 13)
36 The inglenook, where visitors wait [built]
37 The polite door (built) and the room of lost things behind it, bigger inside (designed) [built]
38 Clementine's study [designed]
39 The little door at the stair's foot (built in grey) and the den behind it [designed]
40 Room of Requirement on its own seventh-floor corridor (Q48b's option 3 [designed] (OotP 18, HBP 24)
41 Dumbledore's corridor and the lone gargoyle, round the other side of the castle from the Room (HBP 21, HBP 10) [books] (HBP 25)
42 Flitwick's office, seventh floor of the West Tower [books] (PoA 21)
+2 Sir Cadogan's landing, at the top of the seventh long stair (PoA 6, 14) [canon]
+3 The North Tower stair and the trapdoor landing (PoA 6, 16) [canon]
+14 Lachlan the Lanky, at the stair head, turning right (OotP 13) [canon]
+20 Paracelsus halfway down the passage; Wilfred the Wistful (OotP 14) [canon]

The model's rooms with no number (page/castle-model.js, version 71)

the passage from the seventh floor's north corridor to the North Tower's spiral (north-tower-passage)
the Room's corridor (room-corridor)
the back stair's lobby on 7 (back-stair-lobby-7)
the service passage along the cupboard row's back on 7 (elves-passage-7)
a hide beside the inglenook's flue (secret-s4a)
the slot behind the warming room's press (feast-ladder-well)
the passage from the West Tower's stair south to its stair foot on the seventh floor (west-tower-way-7)

Open to the floor below (a hall or room rising through this storey)

the room behind the rose's air, 10 by 4 m

The towers at this level

Astronomy Tower: its stair to the top
Ravenclaw Tower: its tight spiral stair (+23)
Gryffindor Tower: below the common room: the house's storerooms (ours)
West Tower: its stair; Flitwick's office on 7 (42)
North Tower: its spiral from the seventh floor (+3) to the tiny landing at +45.4
south-west tower: a stair and staff rooms (ours)
south-east tower: blank, but the model room on 4 (H40) and the casemate round its foot on B (H41)
Dumbledore's tower: the gargoyle's moving stair on 7 (41)

Cores not on this floor (a named place takes the spot)

The North Tower's stair foot, a stair between every floor: +2, the passage from the seventh floor's north corridor to the North Tower's spiral takes it
Washrooms, girls' and boys': +2 takes it

This sheet's fill, every space given a use (green: canon, purple: ours)


a The West Tower's stair foot, a stair between every floor [ours: PS 8: "a hundred and forty-two staircases"] core, 8 by 5 m; in by passage al, shared
b The south-west tower's stair foot, a stair between every floor [ours: PS 8: "a hundred and forty-two staircases"] core, 7 by 5 m
c Washrooms, girls' and boys' [ours] core, 7 by 6 m
d Washrooms, girls' and boys' [ours] core, 8 by 4 m
e The Astronomy Tower's stair foot, its stair to the top [ours] core, 6 by 10 m; in by passage ap, shared
f The Headmaster's guest rooms [ours] south range, west, 6 by 14 m
g The seventh-floor broom cupboard [ours] south range, west, 5 by 14 m
h A broom cupboard [ours] north range, 15 by 5 m
i A service passage [ours] north range, 2 by 5 m
j A store of spare desks and chairs [ours] north range, 7 by 5 m
k A linen cupboard [ours] north range, 13 by 5 m
l Filch's cleaning cupboard [ours] north range, 4 by 13 m; in by passage ao
m A store of old textbooks [ours] north range, 9 by 5 m
n The corridor beneath the tallest tower [canon: PS 14] north range, 13 by 13 m; in by passage ap, shared
o Professor Sinistra's study [ours] north range, 14 by 13 m; in by passage an
p A lamp and candle cupboard [ours] north range, 13 by 5 m
q The Astronomy warming room, cocoa after the night class [ours] north range, 13 by 13 m; in by passage aq, shared
r Staff bedrooms [ours] south range, west, 14 by 14 m
s A disused classroom [ours] north range, 14 by 13 m; in by passage am, shared
t A store [ours] north range, 24 by 5 m
u A teacher's study [ours] north range, 13 by 13 m; in by passage aq, shared
v A broom cupboard [ours] north range, 14 by 5 m
w Staff bedroom [ours] north range, 14 by 13 m; in by passage am, shared
x A study room [ours] north range, 13 by 13 m; in by passage ar, shared
y A house-elves' linen room [ours] south range, west, 14 by 14 m
z Professor Trelawney's sherry store [ours: a nod to HBP 25] north range, 5 by 5 m
aa A house-elves' linen room [ours] north range, 14 by 5 m
ab Staff bedroom [ours] west range, 12 by 11 m
ac A disused classroom [ours] east range, 12 by 9 m
ad A teacher's study [ours] east range, 12 by 9 m
ae A study room [ours] west range, 12 by 11 m
af A teacher's study [ours] north range, 14 by 13 m; in by passage al, shared
ag A house-elves' linen room [ours] west range, 12 by 11 m
ah Staff bedroom [ours] east range, 12 by 7 m
ai A teacher's study [ours] north range, 13 by 13 m; in by passage ar, shared
aj Filch's cleaning cupboard [ours] north range, 7 by 5 m
ak A teacher's study [ours] north range, 10 by 10 m
al A passage to the rooms behind [ours: Godric's note, 15 October 2026, 4.12 pm] north range, 2.0 by 5.4 m, to a and af
am A passage to the rooms behind [ours: Godric's note, 15 October 2026, 4.12 pm] north range, 2.0 by 5.4 m, to w and s
an A passage to the rooms behind [ours: Godric's note, 15 October 2026, 4.12 pm] north range, 2.0 by 5.4 m, to o
ao A passage to the rooms behind [ours: Godric's note, 15 October 2026, 4.12 pm] north range, 2.0 by 5.4 m, to l
ap A passage to the rooms behind [ours: Godric's note, 15 October 2026, 4.12 pm] north range, 2.0 by 5.4 m, to e and n
aq A passage to the rooms behind [ours: Godric's note, 15 October 2026, 4.12 pm] north range, 2.0 by 5.4 m, to q and u
ar A passage to the rooms behind [ours: Godric's note, 15 October 2026, 4.12 pm] north range, 2.0 by 5.4 m, to x and ai

The castle's layout, the tower tops

The Architect, 20 October 2026, for Godric, on the castle model, version 71. Under 1.1, 2.1, 3.1 and Q48b's 3. North up; the bar 50 m. Numbers: the step 3 sheet's places (+ the canon sweep's); letters, purple: this sheet's fill, every space given a use.

Above the seventh: the tower tops

the dormitory at +64.2 m

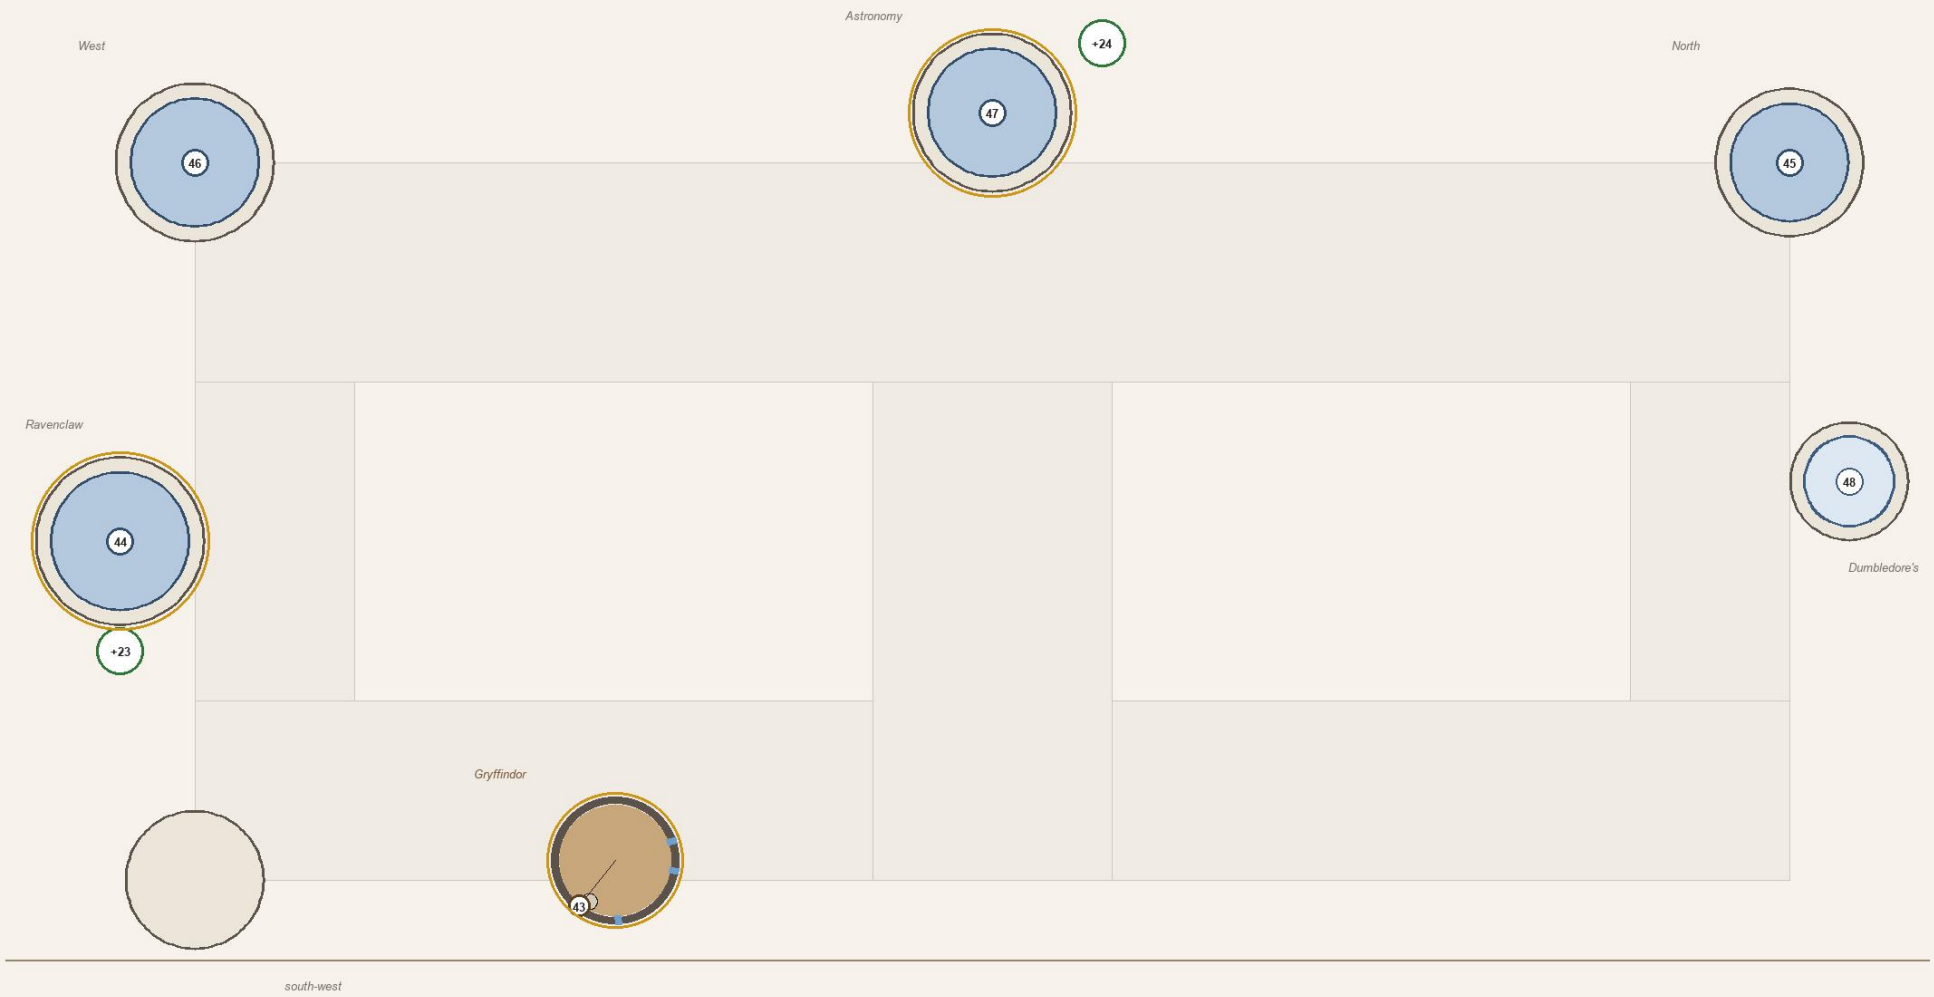





Named places on this floor (the step 3 sheet: numbers the first draft's, + the canon sweep's)

43 Gryffindor dormitory, 7.4 m above the common room [built] (PS 7)
44 Ravenclaw common room [books] (OotP 18, DH 29)
45 Divination, the top of the North Tower [books] (PoA 6, GoF 13)
46 The Owlery, the top of the West Tower [books] (GoF 15)
47 Astronomy Tower, the tallest, directly above the front doors [books] (PS 15, OotP 31)
48 Dumbledore's office [inferred] (CoS 12)
+24 The Astronomy Tower's ramparts, the parapet over the doors (HBP 27, OotP 31) [canon]
+23 Ravenclaw's tight spiral stair and the eagle door (DH 29) [canon]

The towers at this level

Astronomy Tower: the Astronomy classroom and ramparts (47, +24)
Ravenclaw Tower: Ravenclaw common room and dormitories (44)
Gryffindor Tower: the dormitories (43)
West Tower: the Owlery (46)
North Tower: Divination, through the trapdoor (45)
south-west tower: a lookout over the lake (ours)
south-east tower: its machicolated top at +40 (ours)
Dumbledore's tower: the Headmaster's office (48)