

The castle's materials: one schedule for every room, from the accreted model (model v71)

North up; each floor tinted by the stone its walls are of there, each model room hatched by its dressing and coded by its finish (the codes below). Nothing spent.


The cellars

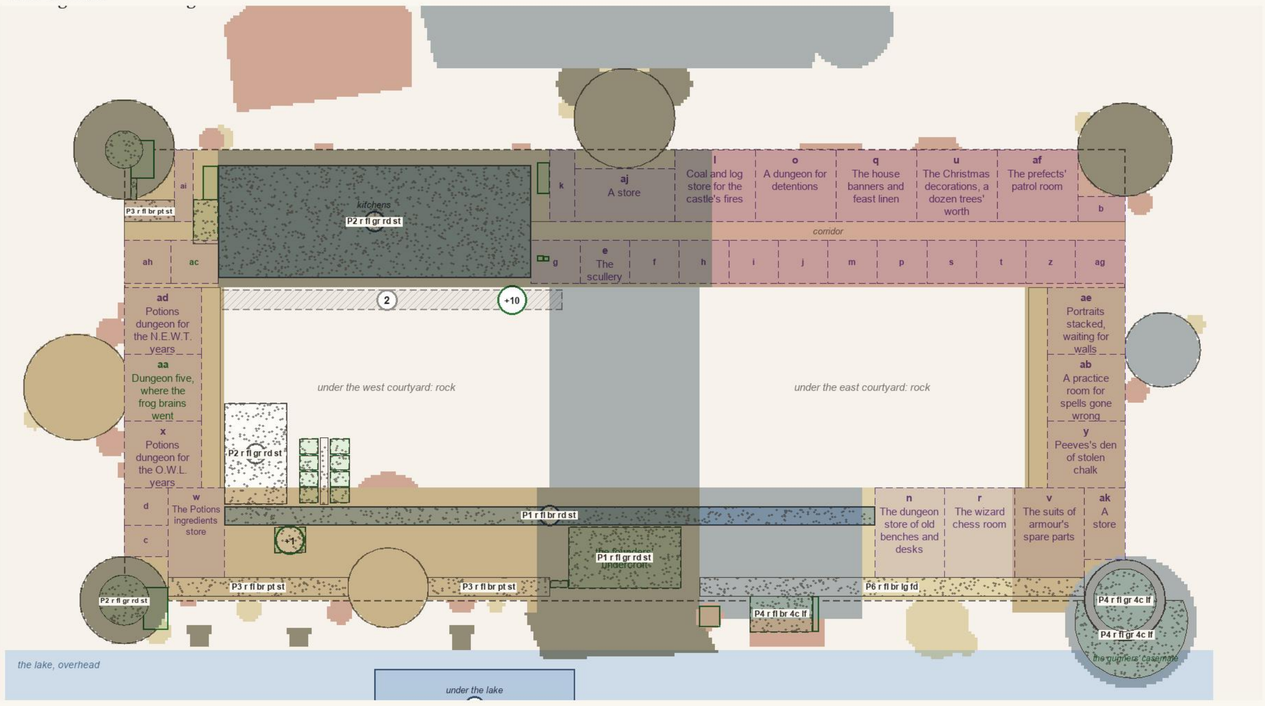


Ground floor

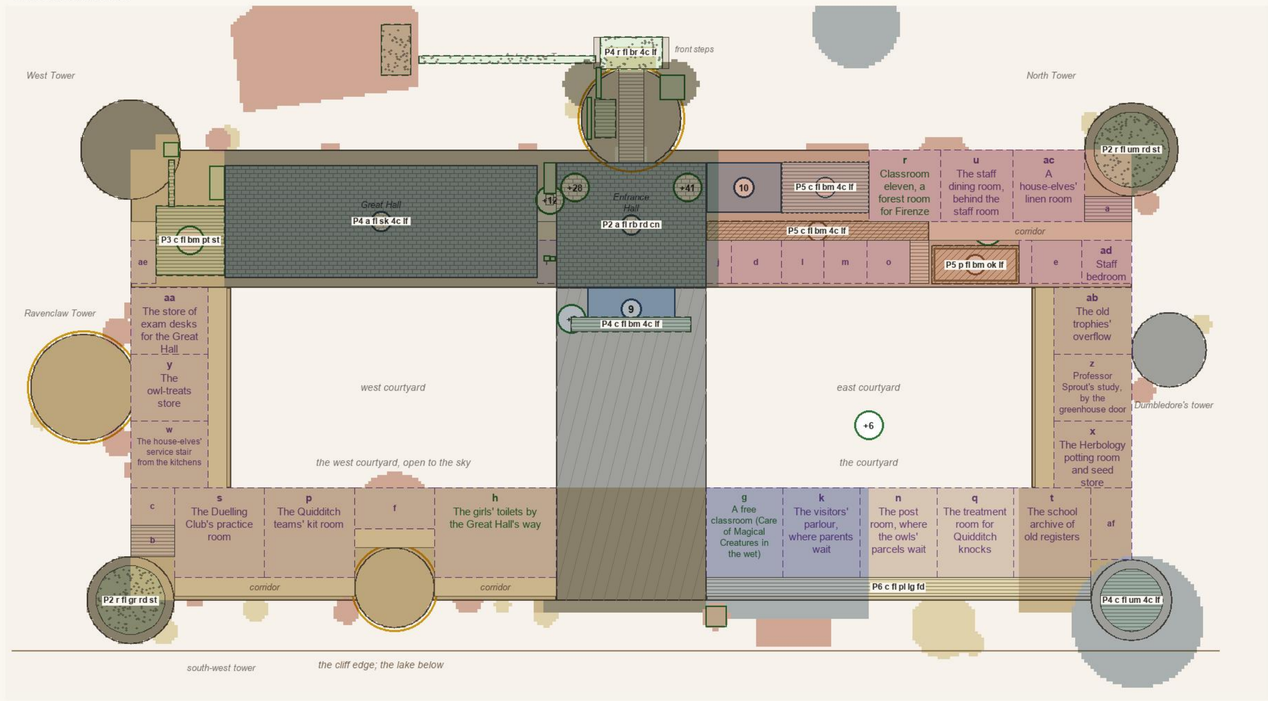

Fourth floor

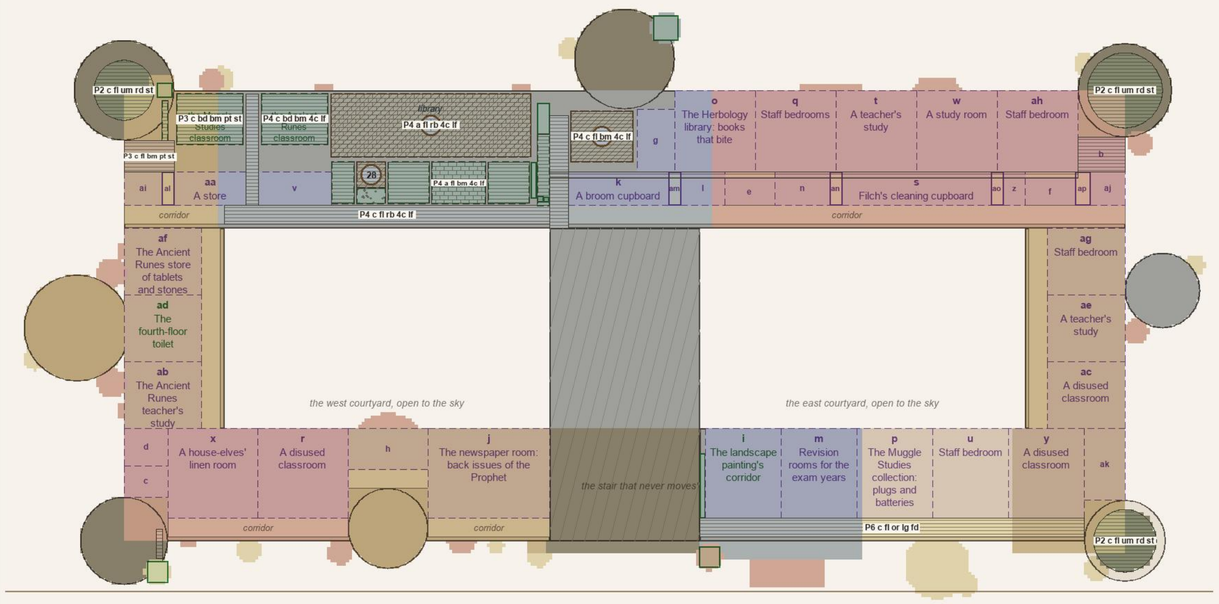

Seventh floor

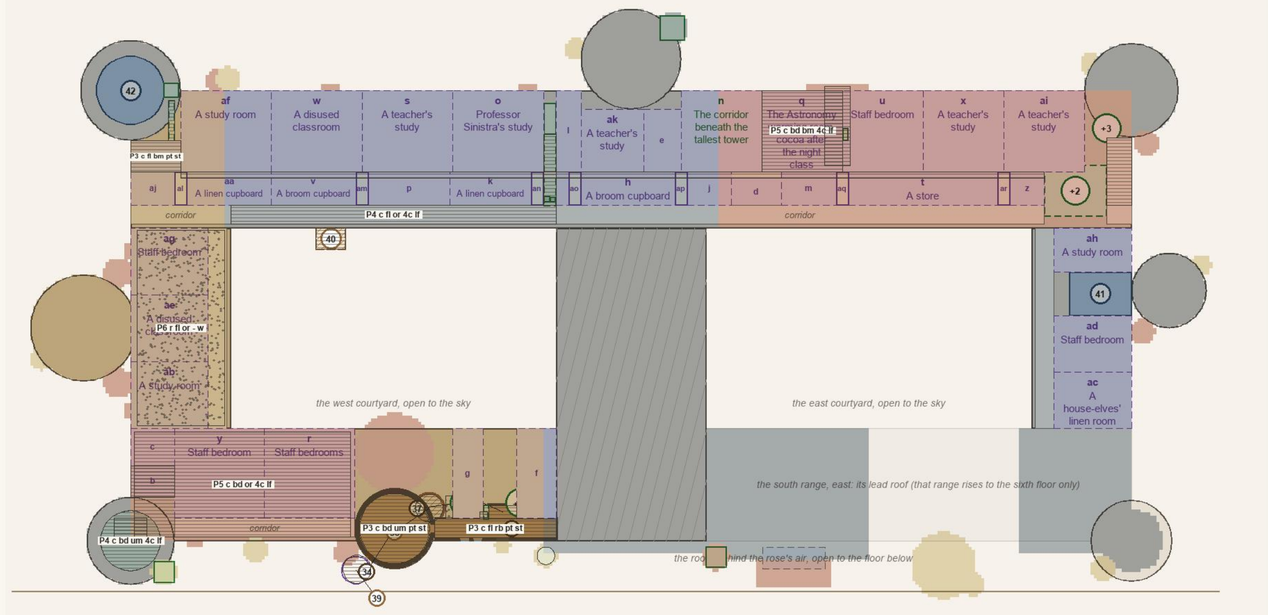

founders-rubble
P1+P2: unsquared rubble with deep joints, dressed o

houses-sandstone
P3: squared stone in even courses

high-grey
P4: ashlar, fine joints, moulded openings

tudor-pink
P5: ashlar, with oak beams, boards and panelling

late-pale
P6+P7: crisp ashlar at openings and corners, the wa

Door surrounds: the head follows the wall's age; every leaf set back in its reveal, never flat on a plain wall



round (P1+P2)
oldest walls

pointed (P3)
the houses' age

four-centred (P4+P5)
high towers, Tudor


lugged (P6+P7)
turrets, restorers

oak
panelled rooms

none
hidden ways

The common room's closet (the pale bookcase card left of the portrait hole): set into a recess in the round wall, the sandstone returning into its reveal, an oak frame at its face.

Ceilings: by the room's kind, span and age; a vault only where the storey lets it rise, wider rooms take beams

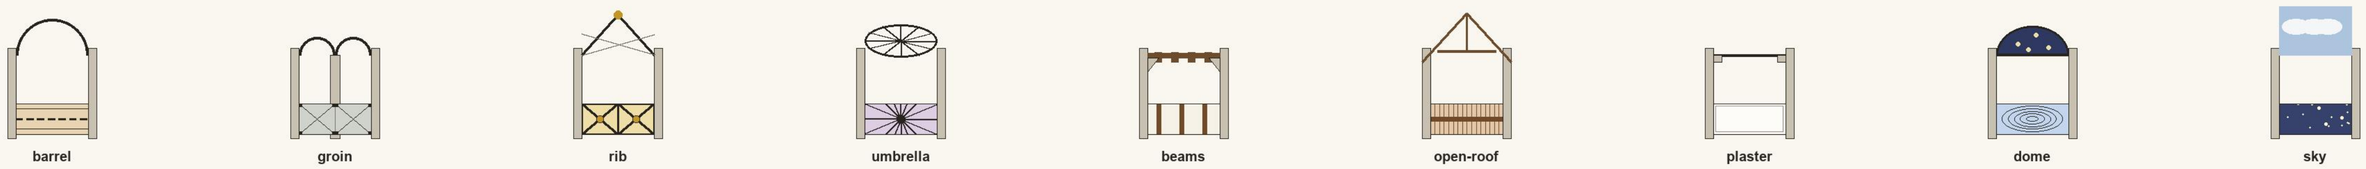

barrel

groin

rib

umbrella

beams

open-roof

plaster

dome

sky

The model's 192 rooms: founders-rubble 45, houses-sandstone 49, high-grey 49, tudor-pink 38, late-pale 11. Ceilings: barrel 39, groin 9, rib 25, umbrella 22, beams 79, open-roof 10, plaster 7, sky 1.

The finish code in each room: age, dressing, floor, ceiling, surround, door leaf (the Charms classroom's "P5 c bd bm 4c lf"); the whole list is docs/architect/materials-by-room.md

Dressing: r rubble (dots), c coursed (lines), a ashlar (a bond), p panelled (an oak border), l limewash (paled). Floor: fl flags, bd boards, mb marble.
Ceiling: br barrel, gr groin, rb rib, um umbrella, bm beams, or open roof, pl plaster, dm dome, sk sky. Surround: rd round, pt pointed, 4c four-centred, lg lugged, ok oak, - none.
Leaf: st oak boards on iron straps, lf linenfold, fd fielded, w the wall's own (a hidden way), cn the books' own (the front doors, the griffin door).