The castle: what is built against the agreed layout

Model v229 against the layout agreed 12 to 16 October (v71, architect-layout-v71.pdf). 28 October 2026.

Floor	Built rooms	Built m2	Layout: built	built otherwise	partly	missing	Model only	Layout m2 unbuilt
Cellars and dungeons	33	2953	7	0	2	42	14	4874
Ground floor	49	4892	20	3	2	26	8	2294
First floor	35	3304	8	5	2	38	7	4893
Second floor	29	2868	7	1	2	48	11	4226
Third floor	34	2626	9	1	21	36	10	5520
Fourth floor	27	2060	9	0	17	36	3	5177
Fifth floor	28	1677	7	0	18	37	9	5515
Sixth floor	30	1947	7	3	32	29	9	5345
Seventh floor	29	2199	8	7	28	20	8	3409
All floors	**294**	**24526**	**82**	**20**	**124**	**312**	**79**	**41253**


Built m2 is the floor area of the model's rooms standing at that storey (a tall room counts on each storey it rises through); walls are not counted.

Classes: built, one model room covers the layout room both ways at 60%; built otherwise, model rooms cover 80% but not as one room; partly, 20 to 80%; missing, under 20%.

Model only: a model room under 30% on paper; many are later picks of Godric's and stand. One page a floor follows.

Cellars and dungeons (B): actuals and busts

Built in the model (v229): 33 rooms, 2953 m2. Agreed layout (v71): 7 rooms built, 0 built otherwise, 2 partly, 42 missing; 4874 m2 of it unbuilt. 14 model rooms on no layout room.

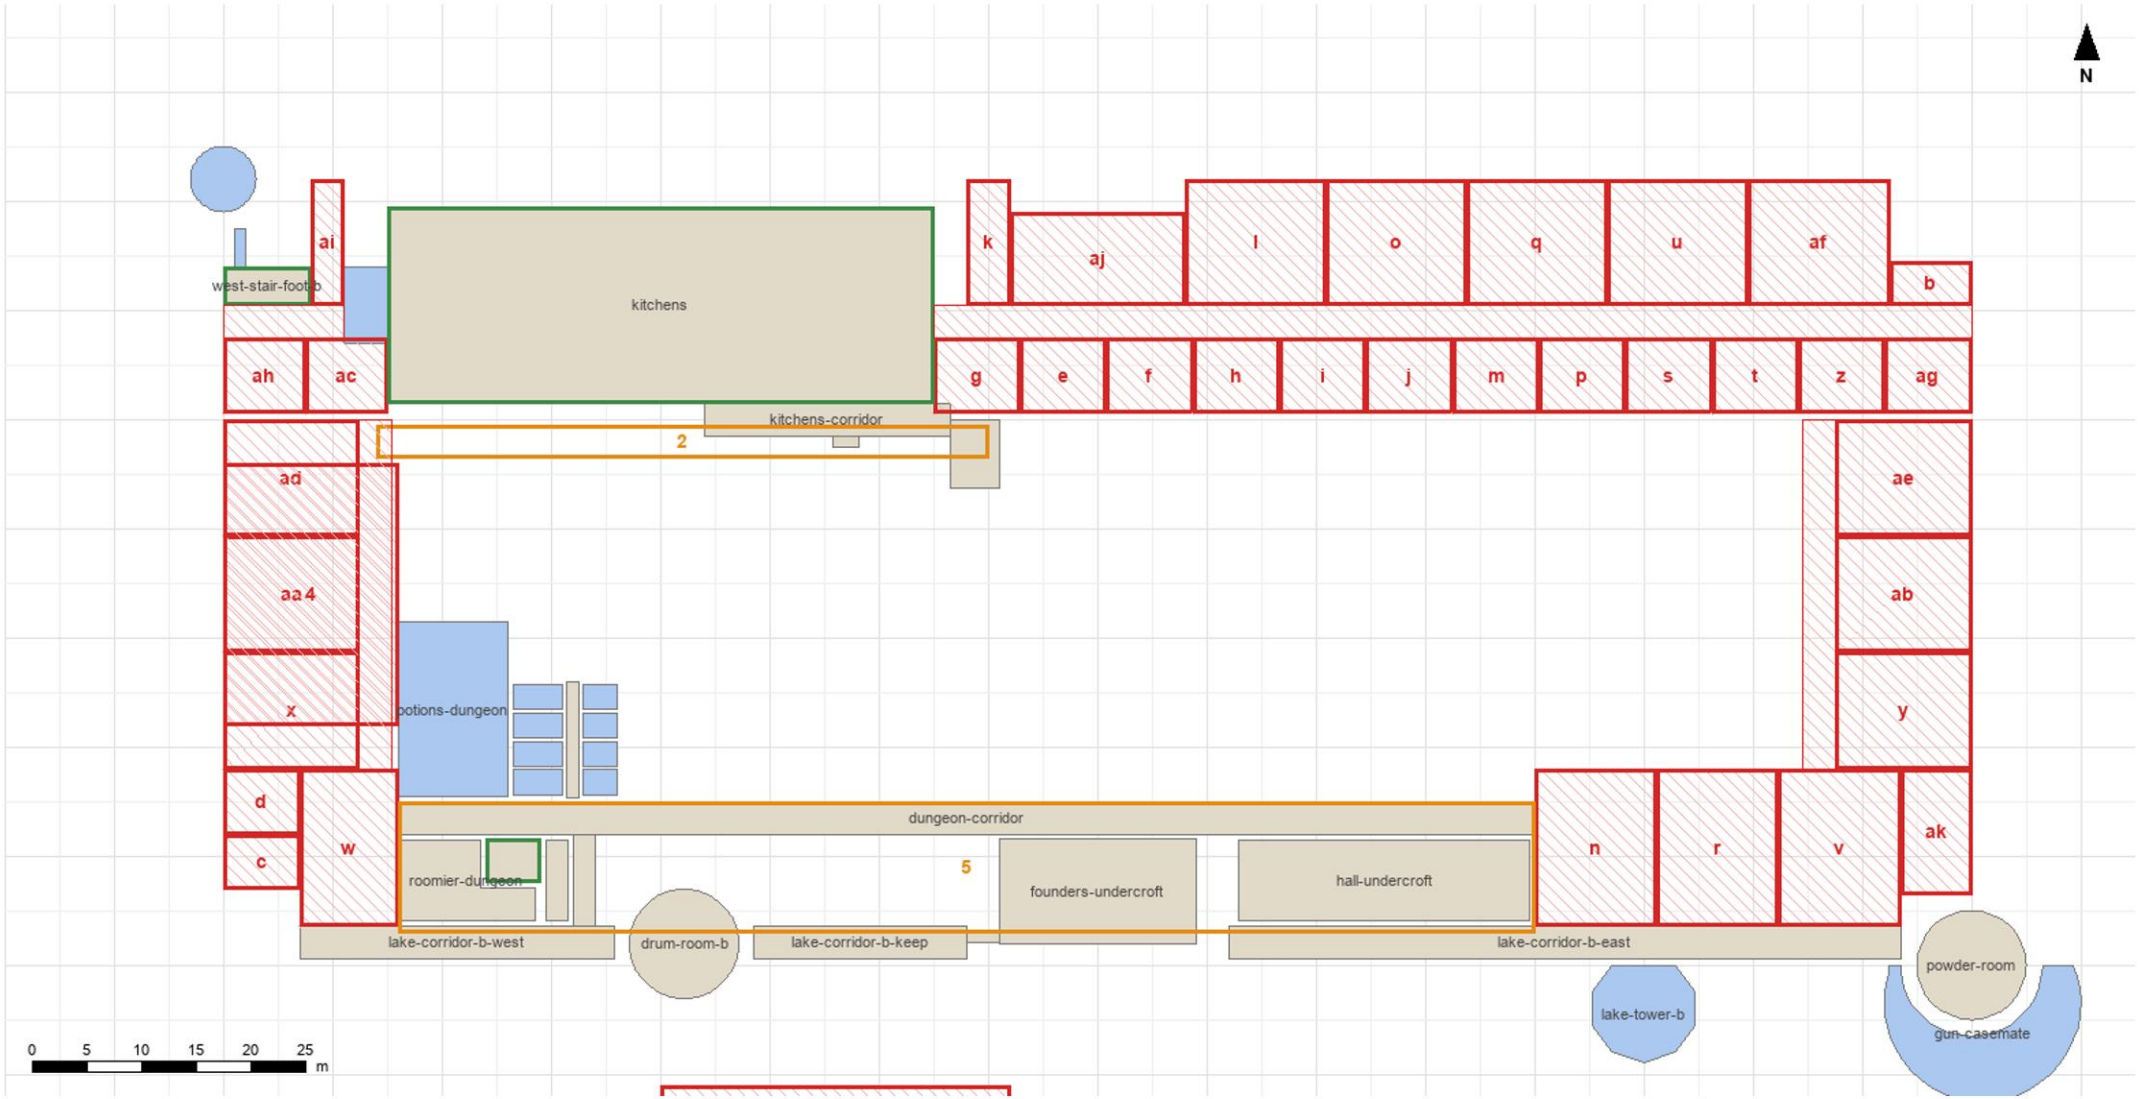


Plan: beige, built in the model (labelled by id); blue fill, built but on no layout room. Outlines, the agreed layout: red hatched missing, orange partly, blue built otherwise, green built. Grid 5 m.

missing fill b: The North Tower's stair foot, a stair between every floor
missing fill c: The south-west tower's stair foot, a stair between every
missing fill d: Washrooms, girls' and boys', 45 m2, 0% built
missing fill e: The scullery, 58 m2, 0% built
missing fill f: The cold room for the feasts, 58 m2, 0% built
missing fill g: The house-elves' quarters, 56 m2, 6% built
missing fill h: The kitchen stores: flour, sugar, the pumpkins, 56 m2, 0%
missing fill i: The brewing cellar, where slow potions steep, 58 m2, 0% b
missing fill j: The cellar of butterbeer and pumpkin juice, 58 m2, 0% bui
missing fill k: A broom cupboard, 50 m2, 0% built
missing fill l: Coal and log store for the castle's fires, 153 m2, 0% bui
missing fill m: Filch's store of confiscated things, 56 m2, 0% built
missing fill n: The dungeon store of old benches and desks, 163 m2, 2% bu
missing fill o: A dungeon for detentions, 156 m2, 0% built
missing fill p: The store of spare cauldrons, 58 m2, 0% built
missing fill q: The house banners and feast linen, 153 m2, 0% built
missing fill r: The wizard chess room, 167 m2, 2% built
missing fill s: The quill, ink and parchment store, 58 m2, 0% built
missing fill t: A ghosts' gathering room, cold all year, 56 m2, 0% built
missing fill u: The Christmas decorations, a dozen trees' worth, 156 m2,
missing fill v: The suits of armour's spare parts, 167 m2, 2% built
missing fill w: The Potions ingredients store, 134 m2, 4% built
missing fill x: Potions dungeon for the O.W.L. years, 138 m2, 0% built
missing fill y: Peeves's den of stolen chalk, 140 m2, 0% built
missing fill z: The candle store for the Great Hall, 58 m2, 0% built
missing fill aa: Dungeon five, where the frog brains went, 138 m2, 0% bui
missing fill ab: A practice room for spells gone wrong, 140 m2, 0% built
missing fill ac: The laundry, by the kitchens, 54 m2, 8% built
missing fill ad: Potions dungeon for the N.E.W.T. years, 134 m2, 0% built
missing fill ae: Portraits stacked, waiting for walls, 137 m2, 0% built
missing fill af: The prefects' patrol room, 156 m2, 0% built
missing fill ag: The school's spare robes, 58 m2, 0% built
missing fill ah: The kitchens' bakery ovens, 54 m2, 0% built
missing fill ai: A store of spare desks and chairs, 38 m2, 5% built
missing fill aj: A store, 142 m2, 0% built
missing fill ak: A store, 79 m2, 0% built
partly named 2: Hufflepuff's basement corridor, which also leads to the k
missing named 3: Slytherin common room: the dungeons, under the lake (the
missing named 4: Potions classroom, down in a dungeon (the spot proposed)
partly named 5: Dungeon corridors, the deathday party (the spot proposed)
corridors missing or partly: 4
model only potions-dungeon: the Potions dungeon, 167 m2
model only secret-s3: a warm room behind the kitchens' great fireplace, 3
model only ice-house: the ice house, a round brick pit under the West Tow
model only ice-house-way: the short passage north from the stair foot int
model only old-cell-w1: an old cell, its walls scratched with names, 12 m
model only old-cell-w2: an old cell, its walls scratched with names, 12 m
model only old-cell-w3: an old cell, its walls scratched with names, 12 m
model only old-cell-w4: an old cell, its walls scratched with names, 12 m
model only old-cell-e1: an old cell, its walls scratched with names, 9 m2
model only old-cell-e2: an old cell, its walls scratched with names, 9 m2
model only old-cell-e3: an old cell, its walls scratched with names, 9 m2
model only old-cell-e4: an old cell, its walls scratched with names, 9 m2
model only lake-tower-b: the lake tower's room on the cellars, 70 m2, aft
model only gun-casemate: the gunners' casemate, round the south-east drum

Ground floor (G): actuals and busts

Built in the model (v229): 49 rooms, 4892 m2. Agreed layout (v71): 20 rooms built, 3 built otherwise, 2 partly, 26 missing; 2294 m2 of it unbuilt. 8 model rooms on no layout room.

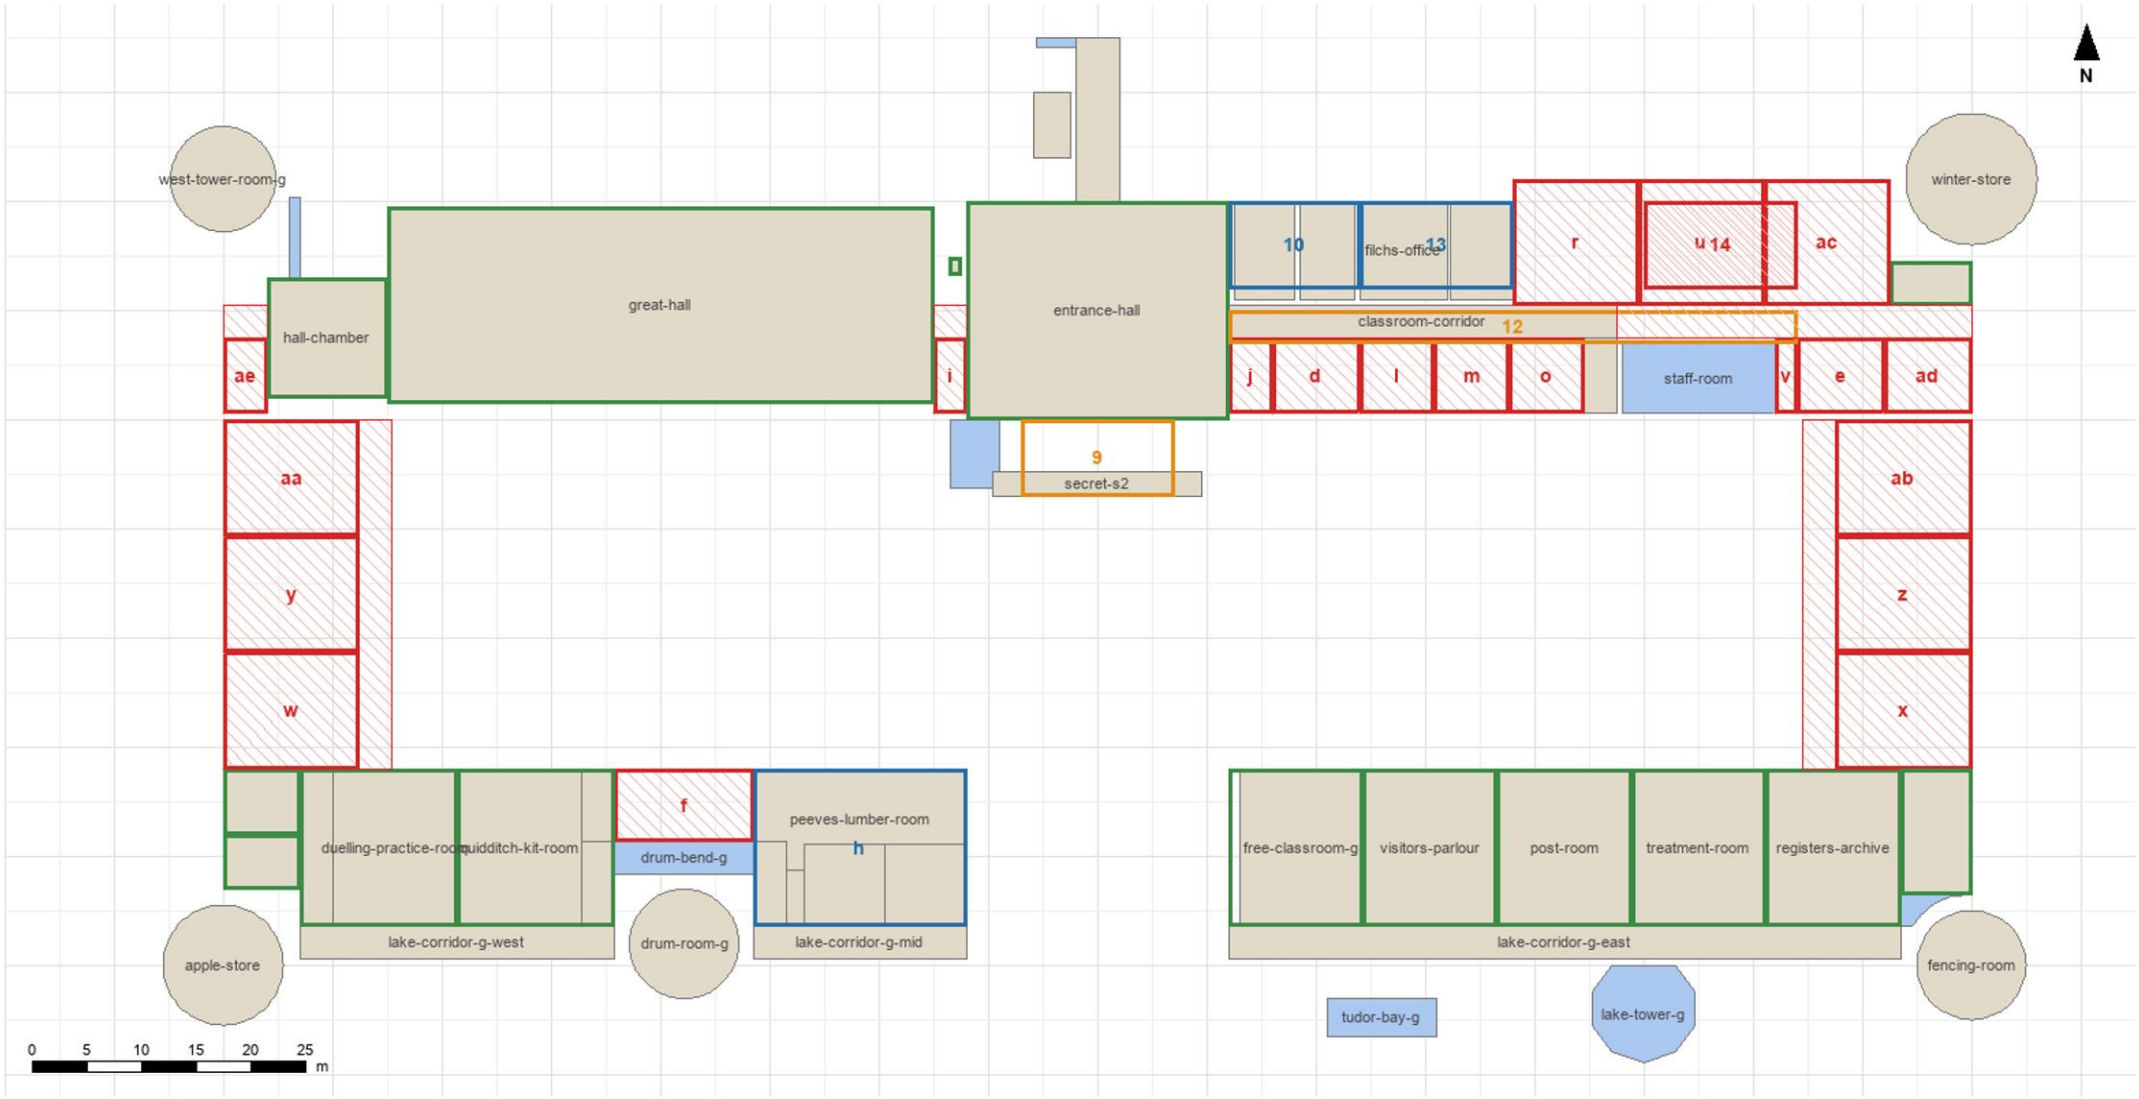

Plan: beige, built in the model (labelled by id); blue fill, built but on no layout room. Outlines, the agreed layout: red hatched missing, orange partly, blue built otherwise, green built. Grid 5 m.


missing fill d: Washrooms, girls' and boys', 58 m2, 4% built
missing fill e: Washrooms, girls' and boys', 58 m2, 0% built
missing fill f: A Gryffindor storeroom at the tower's foot, 88 m2, 7% built
missing fill i: A broom cupboard, 23 m2, 15% built
missing fill j: A store of spare desks and chairs, 30 m2, 9% built
missing fill l: The porters' lodge by the front doors, 49 m2, 4% built
missing fill m: The cloakroom, wet boots and cloaks, 49 m2, 4% built
missing fill o: Madam Hooch's store of school brooms, 51 m2, 7% built
missing fill r: Classroom eleven, a forest room for Firenze, 138 m2, 3% built
missing fill u: The staff dining room, behind the staff room, 138 m2, 0% built
missing fill v: A service passage, 16 m2, 10% built
missing fill w: The house-elves' service stair from the kitchens, 138 m2, 2% built
missing fill x: The Herbology potting room and seed store, 140 m2, 2% built
missing fill y: The owl-treats store, 138 m2, 0% built
missing fill z: Professor Sprout's study, by the greenhouse door, 140 m2, 0% built

missing fill aa: The store of exam desks for the Great Hall, 134 m2, 0% built
missing fill ab: The old trophies' overflow, 137 m2, 0% built
missing fill ac: A house-elves' linen room, 138 m2, 1% built
missing fill ad: Staff bedroom, 58 m2, 0% built
missing fill ae: A linen cupboard, 30 m2, 5% built
partly named 9: Marble staircase, facing the front doors; Harry passes the one-eyed wi, 103 m2, 38
partly named 12: The corridor of classrooms opposite the Great Hall's door: classroom e, 170 m2, 6
missing named 14: The staff room: Harry goes "down" to it, 118 m2, 0% built
corridors missing or partly: 5
model only staff-room: the staff room, 93 m2
model only kitchens-steps: the stone steps down from the Entrance Hall to the kitc, 29 m2, after v
model only s2-level-way-g: the level way from the two-handed door to the double st, 4 m2, after v7
model only lake-tower-g: the lake tower's room on the ground floor, 70 m2, after v71
model only tudor-bay-g: the Tudor bay's room on the ground floor, 38 m2, after v71
model only study-void: the passage round the drum's shoulder, behind the archi, 8 m2, after v71

model only drum-bend-g: the corridor round the Gryffindor Tower's foot on G, 41 m2, after v71
model only west-tower-way-g: the passage from the West Tower's stair south to the ch, 10 m2

First floor (1): actuals and busts

Built in the model (v229): 35 rooms, 3304 m2. Agreed layout (v71): 8 rooms built, 5 built otherwise, 2 partly, 38 missing; 4893 m2 of it unbuilt. 7 model rooms on no layout room.

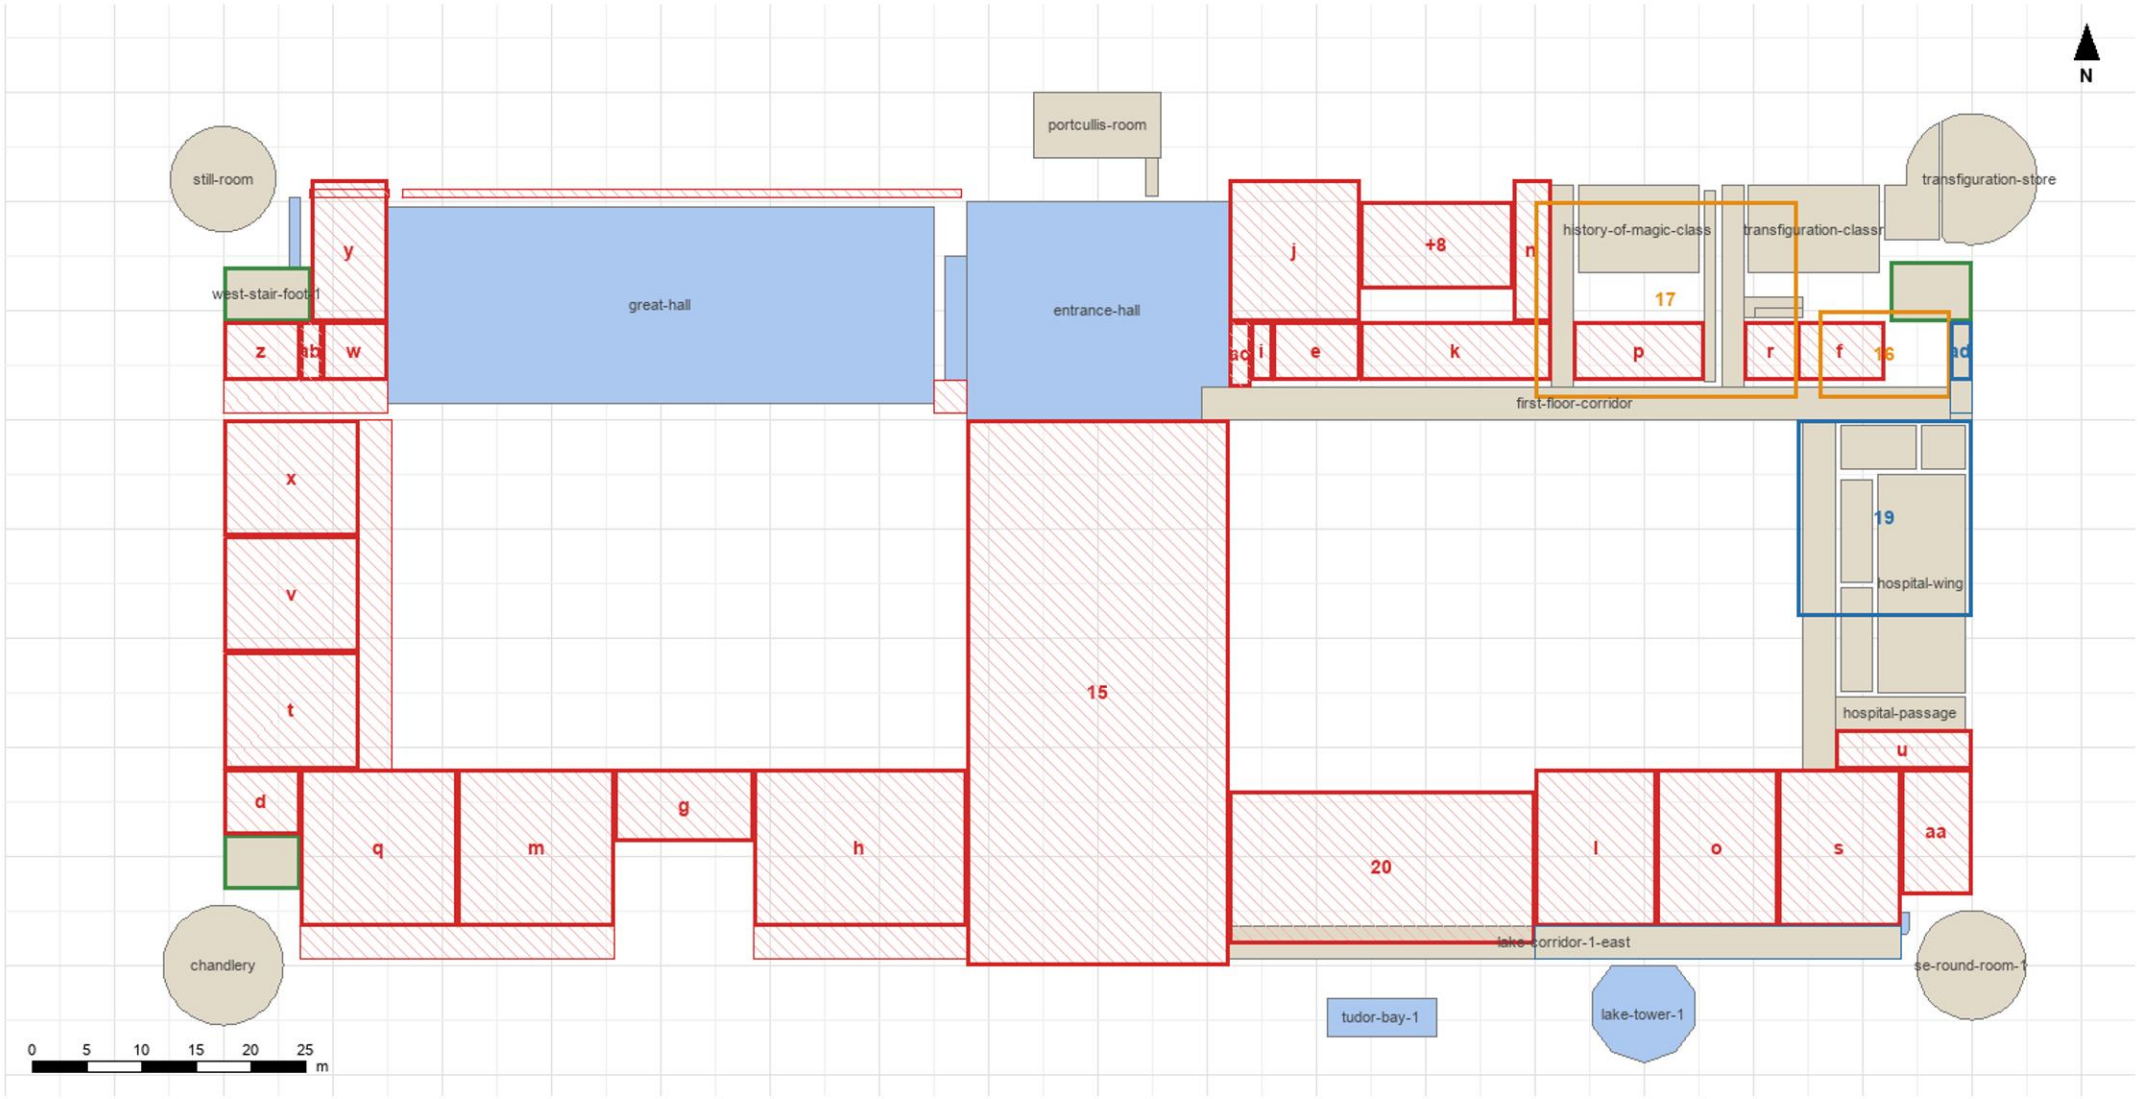


Plan: beige, built in the model (labelled by id); blue fill, built but on no layout room. Outlines, the agreed layout: red hatched missing, orange partly, blue built otherwise, green built. Grid 5 m.

missing fill d: Washrooms, girls' and boys', 45 m2, 4% built
missing fill e: Washrooms, girls' and boys', 45 m2, 0% built
missing fill f: Washrooms, girls' and boys', 45 m2, 0% built
missing fill g: A Gryffindor storeroom at the tower's foot, 88 m2, 0% built
missing fill h: The History of Magic archive of old exam papers, 286 m2, 0% built
missing fill i: A service passage, 12 m2, 0% built
missing fill j: Transfiguration classroom for the N.E.W.T. years, 162 m2, 2% built
missing fill k: A broom cupboard, 98 m2, 1% built
missing fill l: Professor Binns's study, never used, 163 m2, 2% built
missing fill m: Madam Pomfrey's dispensary, 214 m2, 0% built
missing fill n: A store of spare desks and chairs, 50 m2, 6% built
missing fill o: Transfiguration store: cages of practice beetles and mice, 167 m2, 2% built
missing fill p: A linen cupboard, 67 m2, 4% built
missing fill q: The hospital wing's quiet rooms, 210 m2, 1% built
missing fill r: Filch's cleaning cupboard, 29 m2, 5% built
missing fill s: Professor McGonagall's rooms, 167 m2, 2% built
missing fill t: The classroom with the chandelier, 138 m2, 0% built
missing fill u: A store of old textbooks, 51 m2, 8% built
missing fill v: An empty classroom off the first-floor corridor, 138 m2, 0% built
missing fill w: The hospital wing's linen room, 34 m2, 4% built
missing fill x: The Deputy Head's records room, 134 m2, 0% built
missing fill y: A teacher's study, 96 m2, 4% built
missing fill z: A store, 40 m2, 5% built
missing fill aa: The staff library, 79 m2, 0% built
missing fill ab: A passage to the rooms behind, 12 m2, 3% built
missing fill ac: A passage to the rooms behind, 14 m2, 15% built
missing named 15: The moving staircases and the marble staircase in one hall, the front , 1219 m2,
partly named 16: McGonagall's study, first floor (off the list; her classroom carries h, 101 m2, 2
partly named 17: Transfiguration classroom, beside her study, 443 m2, 56% built
missing named 20: History of Magic classroom, "large enough" for a class, 403 m2, 14% built
missing named +8: The first-floor room over Filch's office, 118 m2, 0% built
corridors missing or partly: 9
model only entrance-hall: the Entrance Hall, 479 m2
model only great-hall: the Great Hall, 917 m2
model only back-stair-lobby-1: the back stair's lobby on 1, 26 m2
model only lake-tower-1: the lake tower's room on the first floor, 70 m2, after v71
model only tudor-bay-1: the Tudor bay's room on the first floor, 38 m2, after v71
model only down-only-stair-way-1: the narrow way behind the lake corridor's end wall on 1, 2 m2, a
model only west-tower-way-1: the passage from the West Tower's stair south to its st, 8 m2

Second floor (2): actuals and busts

Built in the model (v229): 29 rooms, 2868 m2. Agreed layout (v71): 7 rooms built, 1 built otherwise, 2 partly, 48 missing; 4226 m2 of it unbuilt. 11 model rooms on no layout room.

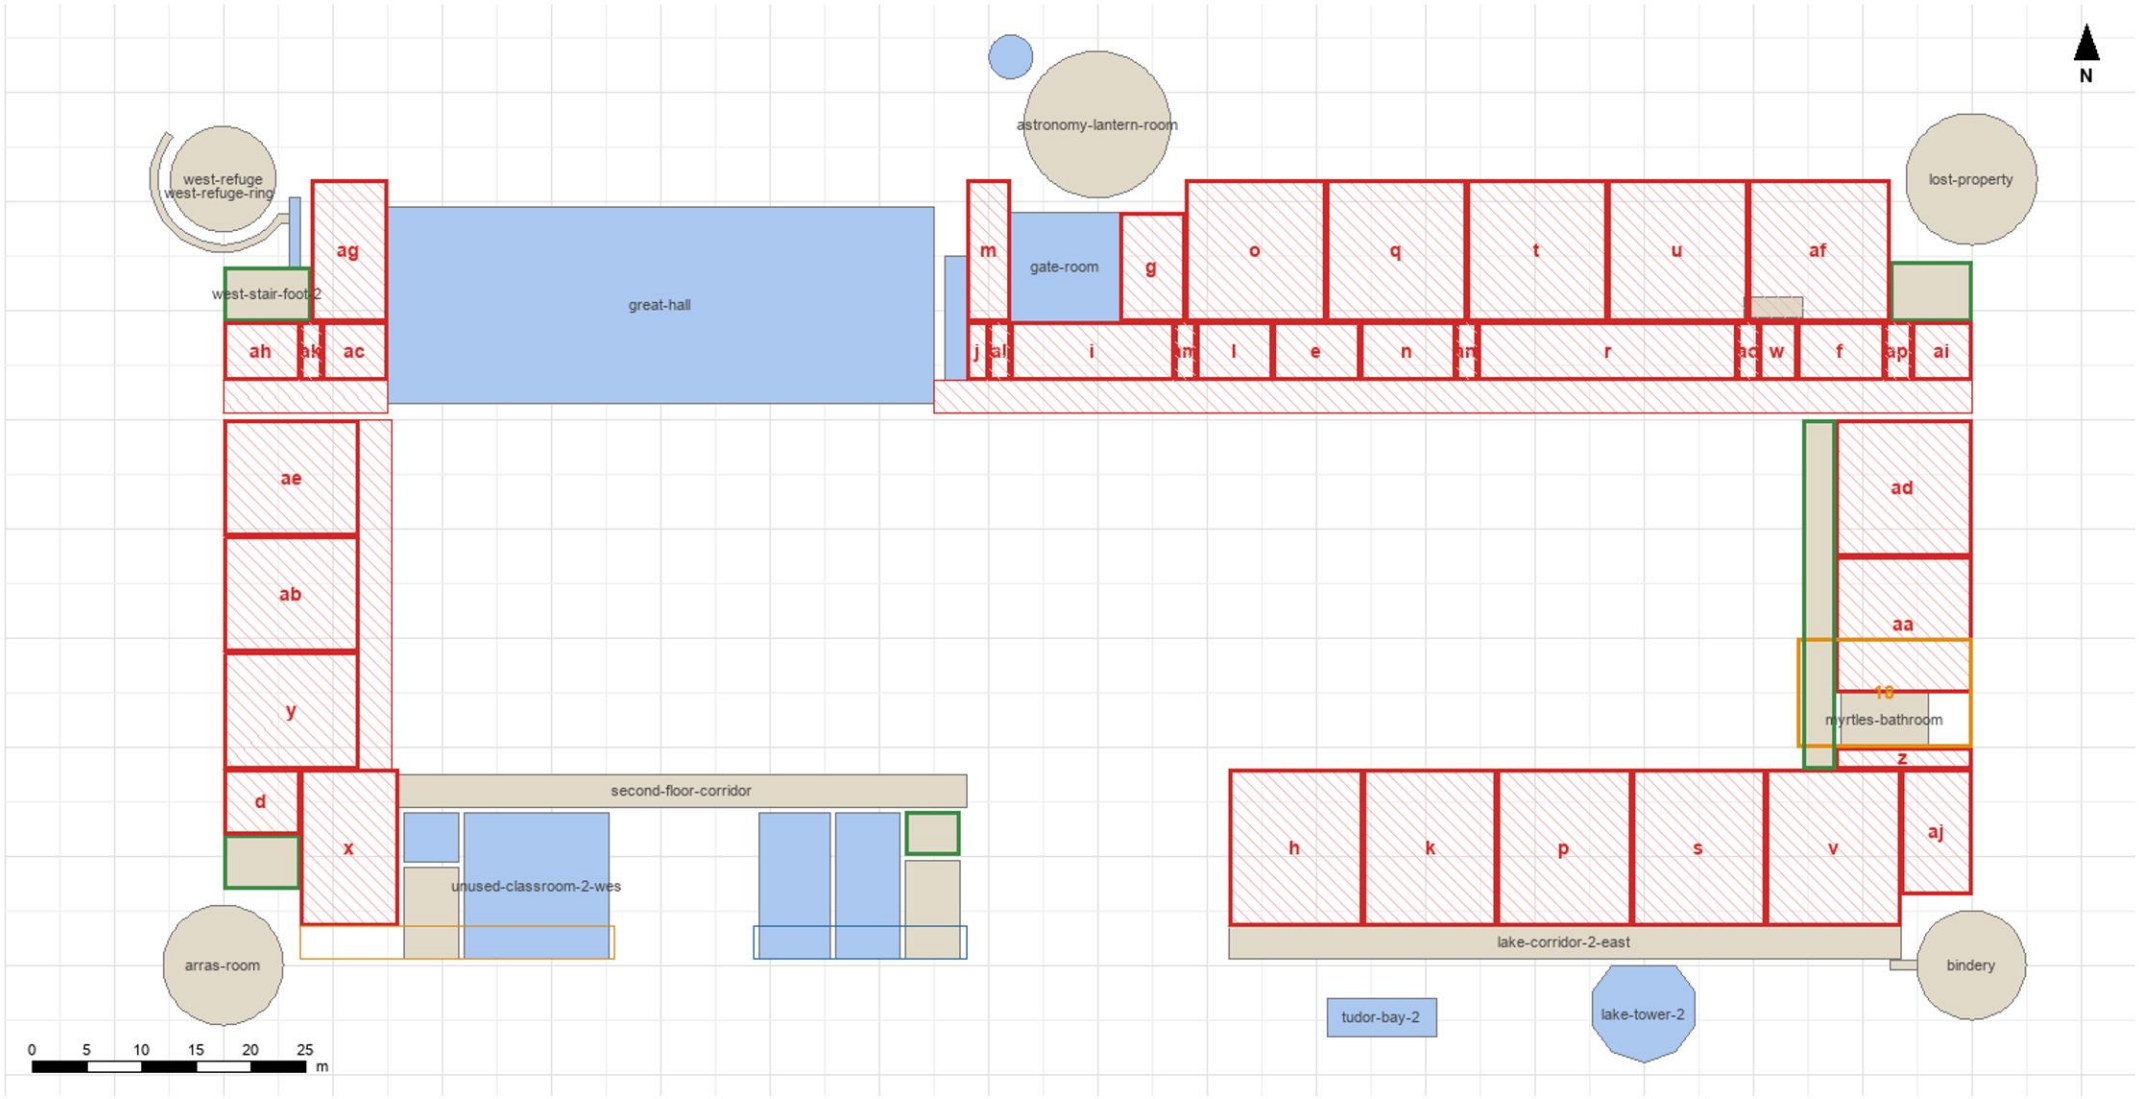


Plan: beige, built in the model (labelled by id); blue fill, built but on no layout room. Outlines, the agreed layout: red hatched missing, orange partly, blue built otherwise, green built. Grid 5 m.

missing fill d: Washrooms, girls' and boys', 45 m2, 4% built
missing fill e: Washrooms, girls' and boys', 45 m2, 0% built
missing fill f: Washrooms, girls' and boys', 45 m2, 0% built
missing fill g: The Astronomy Tower's stair foot, its stair to the top, 6
missing fill h: Lockhart's office, later a Defence spare room, 181 m2, 2%
missing fill i: A broom cupboard, 84 m2, 3% built
missing fill j: A service passage, 12 m2, 11% built
missing fill k: Slughorn's office, larger inside than out, 181 m2, 2% bui
missing fill l: A store of spare desks and chairs, 40 m2, 0% built
missing fill m: A linen cupboard, 56 m2, 7% built
missing fill n: Filch's cleaning cupboard, 50 m2, 0% built
missing fill o: The Slug Club's dining room, 172 m2, 0% built
missing fill p: The Gobstones Club room, 181 m2, 2% built
missing fill q: The second-floor girls' washroom, the one that works, 176
missing fill r: A store of old textbooks, 132 m2, 0% built
missing fill s: A duelling practice room, 181 m2, 2% built
missing fill t: The map room, 172 m2, 0% built
missing fill u: A second years' study room, 176 m2, 1% built
missing fill v: Staff bedrooms, 185 m2, 2% built
missing fill w: A lamp and candle cupboard, 21 m2, 0% built
missing fill x: A disused classroom, 134 m2, 2% built
missing fill y: A teacher's study, 138 m2, 0% built
missing fill z: A service passage, 29 m2, 9% built
missing fill aa: Staff bedroom, 163 m2, 3% built
missing fill ab: A study room, 138 m2, 0% built
missing fill ac: A store, 34 m2, 4% built
missing fill ad: A house-elves' linen room, 163 m2, 2% built
missing fill ae: Staff bedroom, 134 m2, 0% built
missing fill af: A disused classroom, 176 m2, 7% built
missing fill ag: A teacher's study, 96 m2, 4% built
missing fill ah: A broom cupboard, 40 m2, 5% built
missing fill ai: A store of spare desks and chairs, 32 m2, 5% built
missing fill aj: A teacher's study, 79 m2, 0% built
missing fill ak: A passage to the rooms behind, 12 m2, 3% built
missing fill al: A passage to the rooms behind, 12 m2, 1% built
missing fill am: A passage to the rooms behind, 12 m2, 0% built
missing fill an: A passage to the rooms behind, 12 m2, 0% built
missing fill ao: A passage to the rooms behind, 12 m2, 0% built
missing fill ap: A passage to the rooms behind, 15 m2, 4% built
partly named 18: Myrtle's bathroom, the Chamber's door: the second floor,
corridors missing or partly: 10
model only great-hall: the Great Hall, 917 m2
model only defence-sitting-room: the Defence teacher's sitting room, thro
model only unused-classroom-2-west: an unused classroom on the second flo
model only unused-classroom-2-east: an unused classroom on the second flo
model only back-stair-lobby-2: the back stair's lobby on 2, 26 m2
model only gate-room: the room over the gate, the first walls' porters' c
model only s2-room-2: the round room on 2 at the double stair's top, wher
model only lake-tower-2: the lake tower's room on the second floor, 70 m2
model only tudor-bay-2: the Tudor bay's room on the second floor, 38 m2,
model only strong-room: the strong room, 25 m2, after v71
model only west-tower-way-2: the passage from the West Tower's stair sout

Third floor (3): actuals and busts

Built in the model (v229): 34 rooms, 2626 m2. Agreed layout (v71): 9 rooms built, 1 built otherwise, 21 partly, 36 missing; 5520 m2 of it unbuilt. 10 model rooms on no layout room.

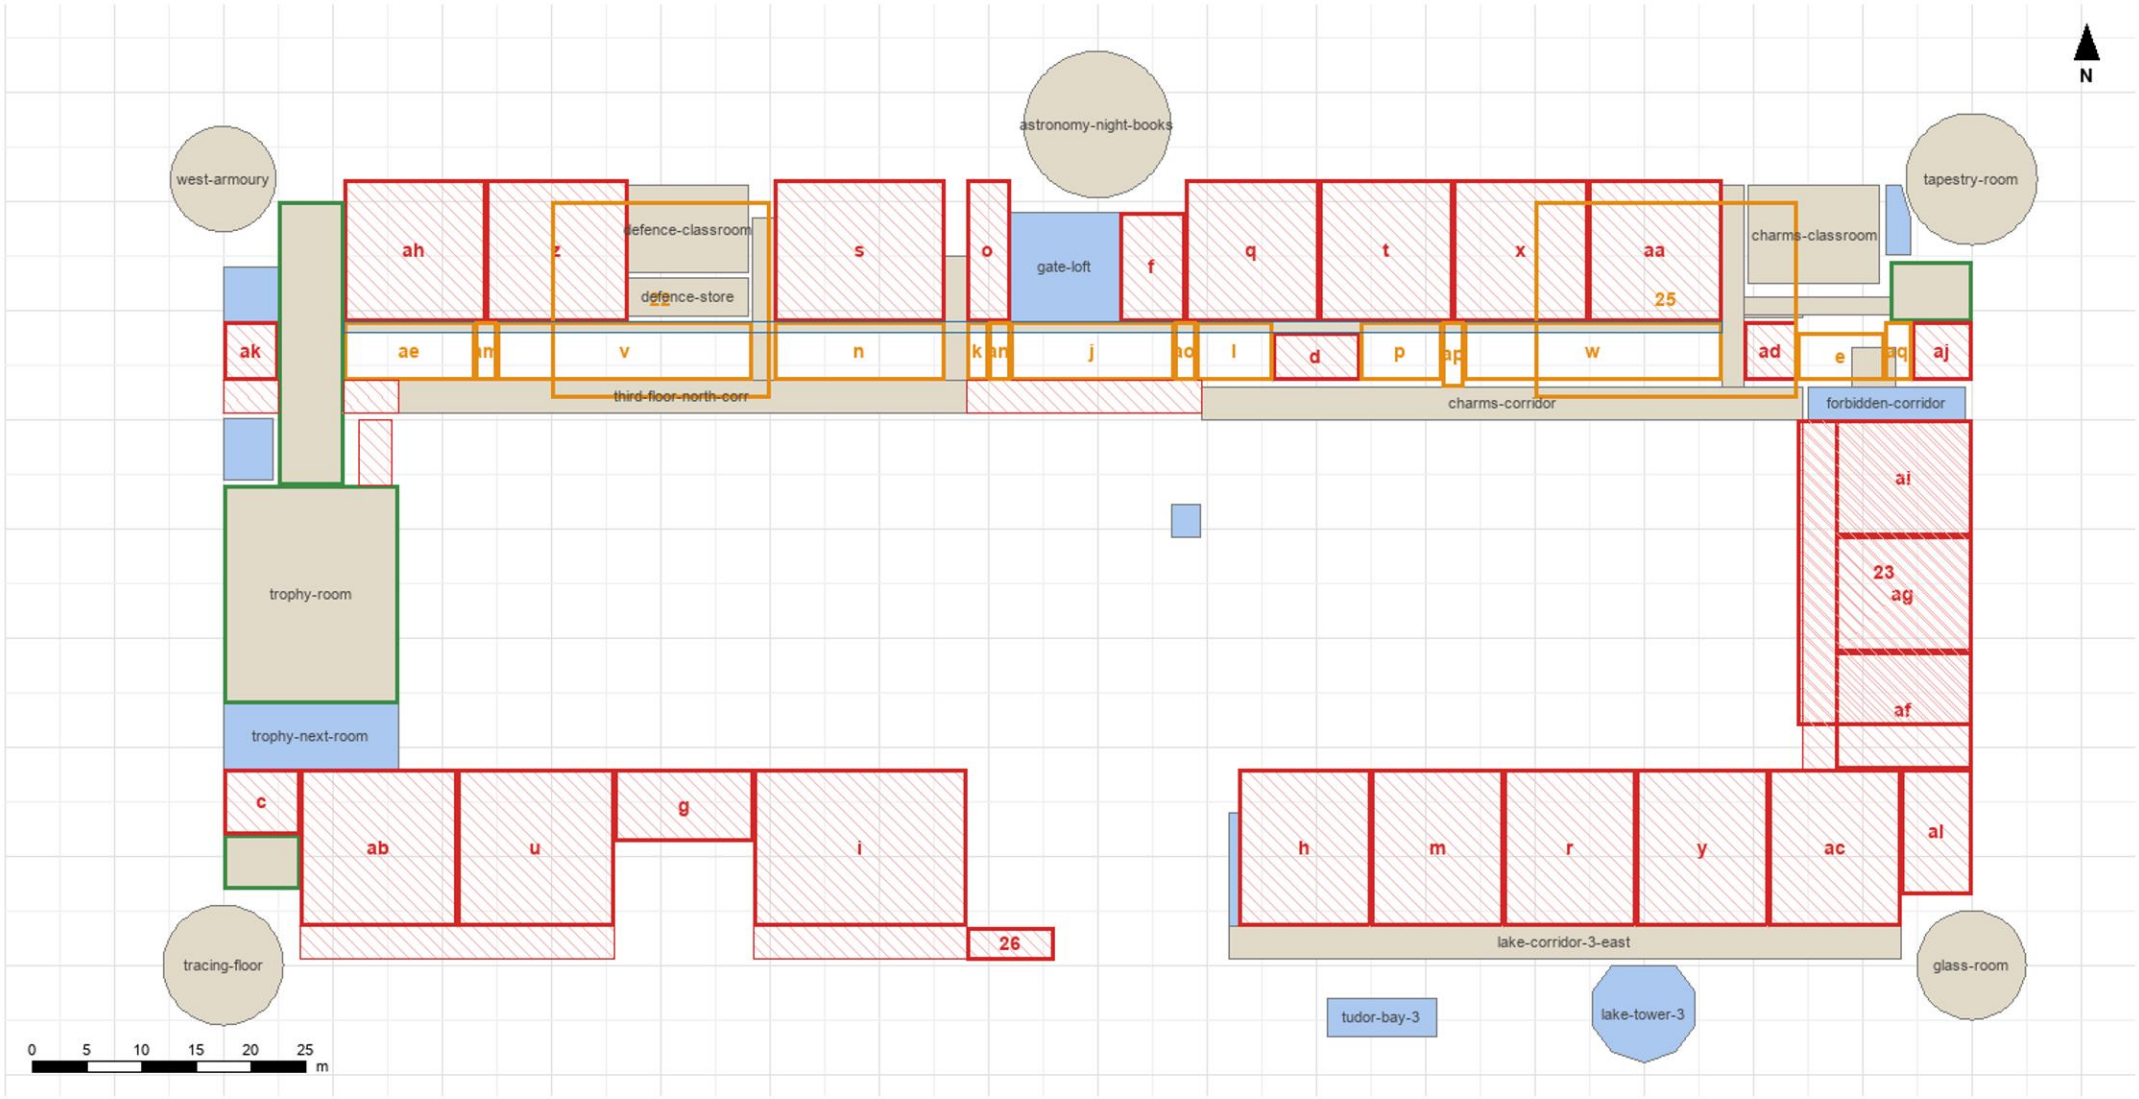

Plan: beige, built in the model (labelled by id); blue fill, built but on no layout room. Outlines, the agreed layout: red hatched missing, orange partly, blue built otherwise, green built. Grid 5 m.

missing fill c: Washrooms, girls' and boys', 45 m2, 8% built
missing fill d: Washrooms, girls' and boys', 37 m2, 6% built
partly fill e: Washrooms, girls' and boys', 37 m2, 28% built
missing fill f: The Astronomy Tower's stair foot, its stair to the top, 6
missing fill g: A Gryffindor storeroom at the tower's foot, 88 m2, 0% bui
missing fill h: A third years' study room, 181 m2, 3% built
missing fill i: Staff bedrooms, 286 m2, 0% built
partly fill j: A broom cupboard, 84 m2, 23% built
partly fill k: A service passage, 12 m2, 31% built
partly fill l: A store of spare desks and chairs, 40 m2, 23% built
missing fill m: Staff bedroom, 178 m2, 2% built
partly fill n: A linen cupboard, 88 m2, 30% built
missing fill o: Filch's cleaning cupboard, 56 m2, 9% built
partly fill p: A house-elves' linen room, 43 m2, 23% built
missing fill q: The Defence teacher's bedroom, 166 m2, 2% built


missing fill r: A study room, 181 m2, 2% built
missing fill s: The swivelling staircase, 212 m2, 4% built
missing fill t: A teacher's study, 166 m2, 2% built
missing fill u: The armour gallery's repair room, 214 m2, 0% built
partly fill v: A lamp and candle cupboard, 129 m2, 28% built
partly fill w: A store, 131 m2, 24% built
missing fill x: The Charms store: cushions, teacups and pineapples, 166 m
missing fill y: A disused classroom, 178 m2, 2% built
missing fill z: The Defence practice room, for jinxes and counter-jinxes,
missing fill aa: Charms classroom for the N.E.W.T. years, 166 m2, 4% buil
missing fill ab: The trophy room's polishing room, 210 m2, 2% built
missing fill ac: A teacher's study, 181 m2, 2% built
missing fill ad: A broom cupboard, 29 m2, 5% built
partly fill ae: A store of spare desks and chairs, 67 m2, 27% built
missing fill af: A teacher's study, 140 m2, 0% built

missing fill ag: Staff bedroom, 140 m2, 0% built
missing fill ah: The room beside the trophy room, 176 m2, 3% built
missing fill ai: A study room, 137 m2, 2% built
missing fill aj: A linen cupboard, 32 m2, 5% built
missing fill ak: Filch's cleaning cupboard, 29 m2, 9% built
missing fill al: A house-elves' linen room, 79 m2, 0% built
partly fill am: A passage to the rooms behind, 12 m2, 27% built
partly fill an: A passage to the rooms behind, 12 m2, 23% built
partly fill ao: A passage to the rooms behind, 12 m2, 23% built
partly fill ap: A passage to the rooms behind, 14 m2, 24% built
partly fill aq: A passage to the rooms behind, 15 m2, 31% built
partly named 22: Defence Against the Dark Arts classroom: four floors bel
missing named 23: The forbidden corridor: "the third-floor corridor on th
partly named 25: Charms classroom: near the forbidden corridor, "miles fr
missing named 26: The one-eyed witch's landing, directly beneath the corr

corridors missing or partly: 12
model only trophy-next-room: the room next to the trophy room, where Filc
model only lost-games-room: the trophies of the games nobody plays, behin
model only forbidden-corridor: the forbidden corridor on the third floor,
model only gate-loft: the loft over the gate room, 105 m2
model only accounts-room-3: the castle's accounts room, east of the Charm
model only lake-tower-3: the lake tower's room on the third floor, 70 m2,
model only tudor-bay-3: the Tudor bay's room on the third floor, 38 m2, a
model only keep-east-stairwell: the stair that never moves, in the keep's
model only vanishing-step-hollow: the hollow under the vanishing step, 9
model only west-stair-foot-3: the West Tower's stair landing on 3, the la

Fourth floor (4): actuals and busts

Built in the model (v229): 27 rooms, 2060 m2. Agreed layout (v71): 9 rooms built, 0 built otherwise, 17 partly, 36 missing; 5177 m2 of it unbuilt. 3 model rooms on no layout room.

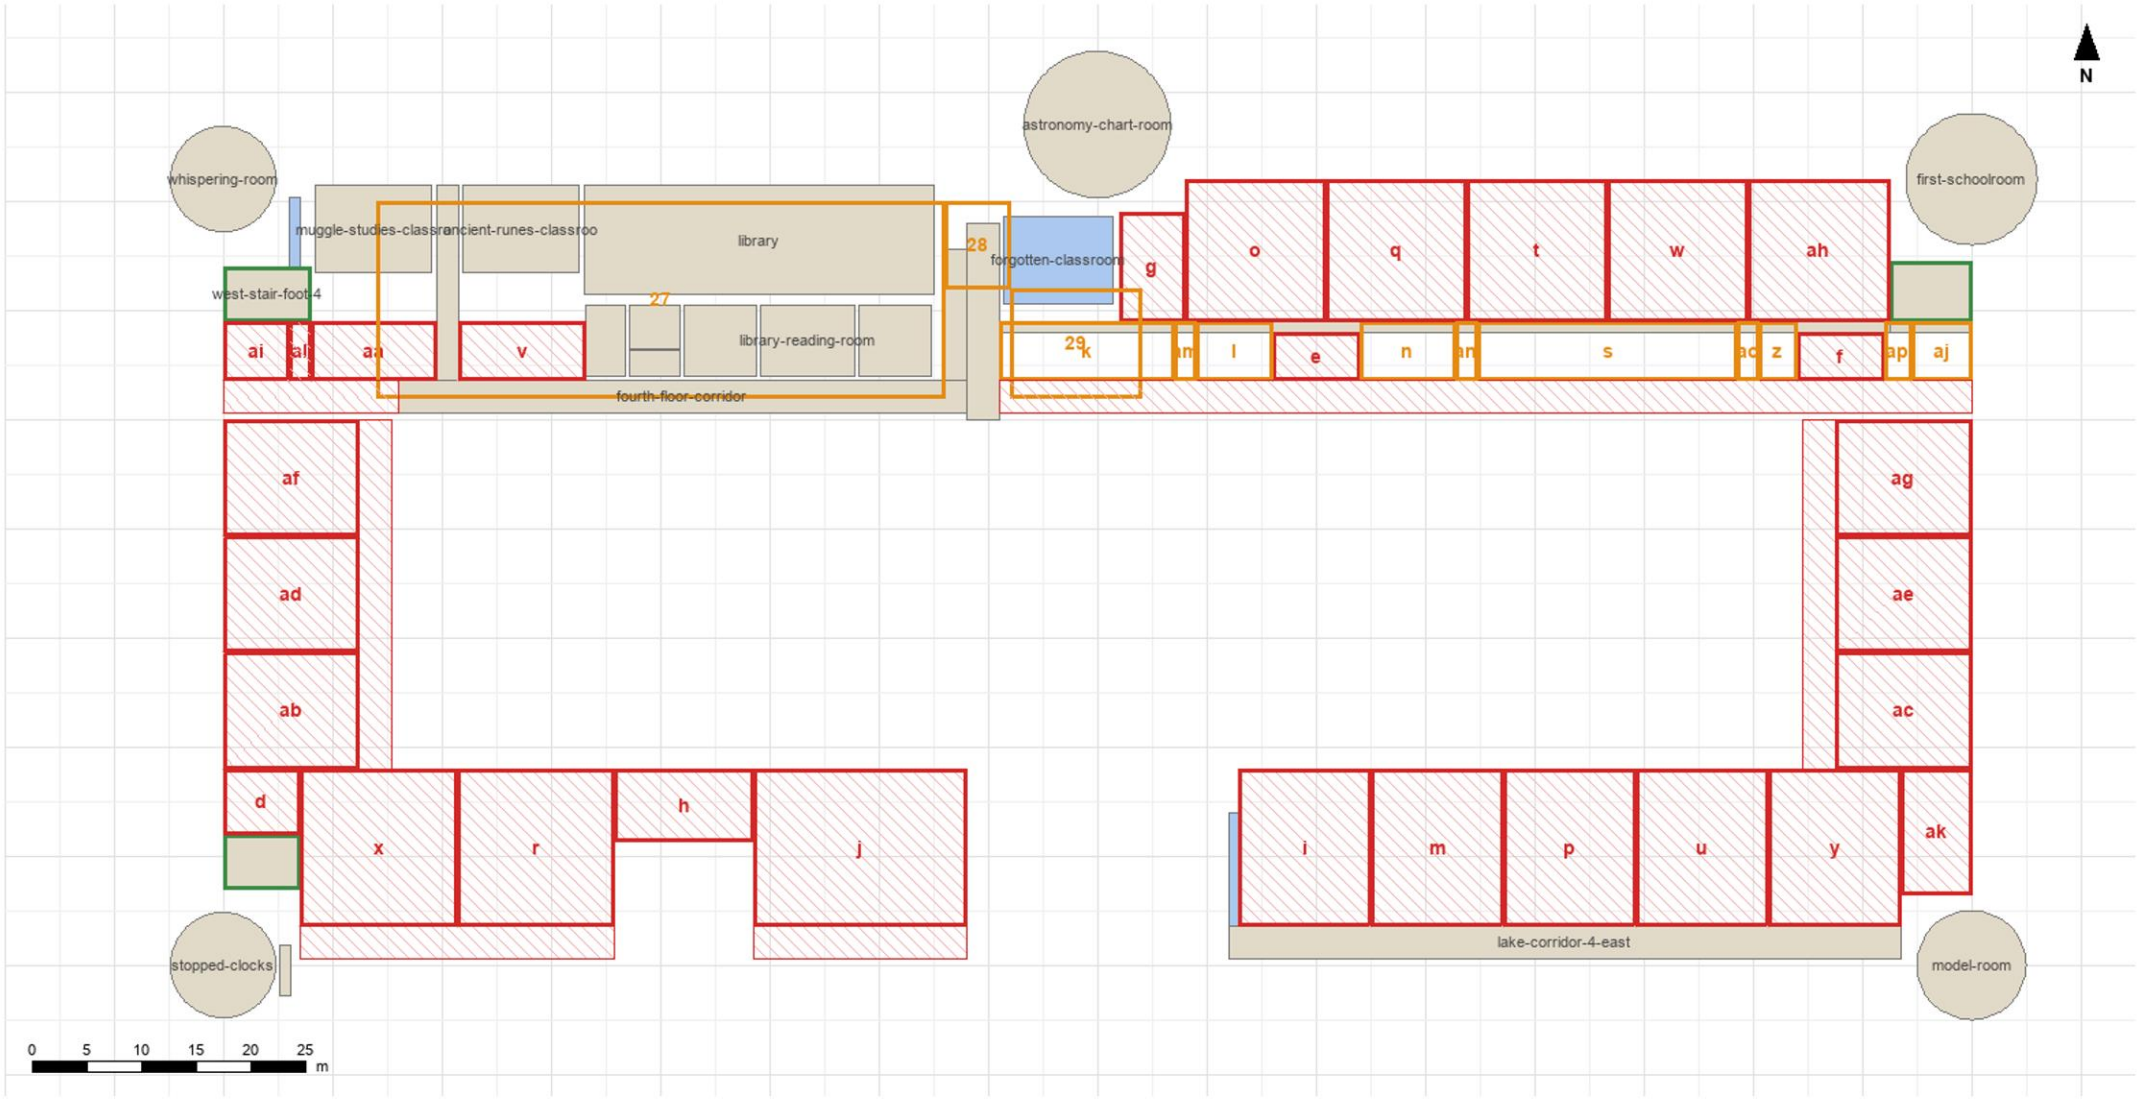


Plan: beige, built in the model (labelled by id); blue fill, built but on no layout room. Outlines, the agreed layout: red hatched missing, orange partly, blue built otherwise, green built. Grid 5 m.

missing fill d: Washrooms, girls' and boys', 45 m2, 4% built
missing fill e: Washrooms, girls' and boys', 37 m2, 6% built
missing fill f: Washrooms, girls' and boys', 37 m2, 6% built
missing fill g: The Astronomy Tower's stair foot, its stair to the top, 6
missing fill h: A Gryffindor storeroom at the tower's foot, 88 m2, 0% bui
missing fill i: The landscape painting's corridor, 181 m2, 3% built
missing fill j: The newspaper room: back issues of the Prophet, 286 m2, 0
partly fill k: A broom cupboard, 89 m2, 24% built
partly fill l: A store of spare desks and chairs, 40 m2, 23% built
missing fill m: Revision rooms for the exam years, 178 m2, 2% built
partly fill n: A linen cupboard, 50 m2, 23% built
missing fill o: The Herbology library: books that bite, 172 m2, 2% built
missing fill p: The Muggle Studies collection: plugs and batteries, 181 m
missing fill q: Staff bedrooms, 176 m2, 2% built
missing fill r: A house-elves' linen room, 214 m2, 0% built
partly fill s: Filch's cleaning cupboard, 132 m2, 23% built
missing fill t: Staff bedroom, 172 m2, 2% built
missing fill u: A disused classroom, 178 m2, 2% built
missing fill v: A store of old textbooks, 65 m2, 9% built
missing fill w: A teacher's study, 176 m2, 2% built
missing fill x: Staff bedroom, 210 m2, 1% built
missing fill y: A study room, 181 m2, 2% built
partly fill z: A lamp and candle cupboard, 21 m2, 23% built
missing fill aa: A store, 65 m2, 4% built
missing fill ab: The Ancient Runes teacher's study, 138 m2, 0% built
missing fill ac: A house-elves' linen room, 140 m2, 0% built
missing fill ad: The fourth-floor toilet, 138 m2, 0% built
missing fill ae: Staff bedroom, 140 m2, 0% built
missing fill af: The Ancient Runes store of tablets and stones, 134 m2, 0
missing fill ag: A disused classroom, 137 m2, 0% built
missing fill ah: A study room, 176 m2, 3% built
missing fill ai: A broom cupboard, 34 m2, 5% built
partly fill aj: A store of spare desks and chairs, 32 m2, 23% built
missing fill ak: A teacher's study, 79 m2, 0% built
missing fill al: A passage to the rooms behind, 12 m2, 5% built
partly fill am: A passage to the rooms behind, 12 m2, 23% built
partly fill an: A passage to the rooms behind, 12 m2, 23% built
partly fill ao: A passage to the rooms behind, 12 m2, 23% built
partly fill ap: A passage to the rooms behind, 15 m2, 23% built
partly named 27: Library, the Restricted Section at the back: "five floor
partly named 28: The Muggle Studies room, past the last stack (Magic), 52
partly named 29: The unused classroom with the Mirror of Erised, near the
corridors missing or partly: 11
model only forgotten-classroom: an unused classroom, desks stacked agains
model only keep-east-stairwell: the stair that never moves, in the keep's
model only west-tower-way-4: the passage from the West Tower's stair sout

Fifth floor (5): actuals and busts

Built in the model (v229): 28 rooms, 1677 m2. Agreed layout (v71): 7 rooms built, 0 built otherwise, 18 partly, 37 missing; 5515 m2 of it unbuilt. 9 model rooms on no layout room.

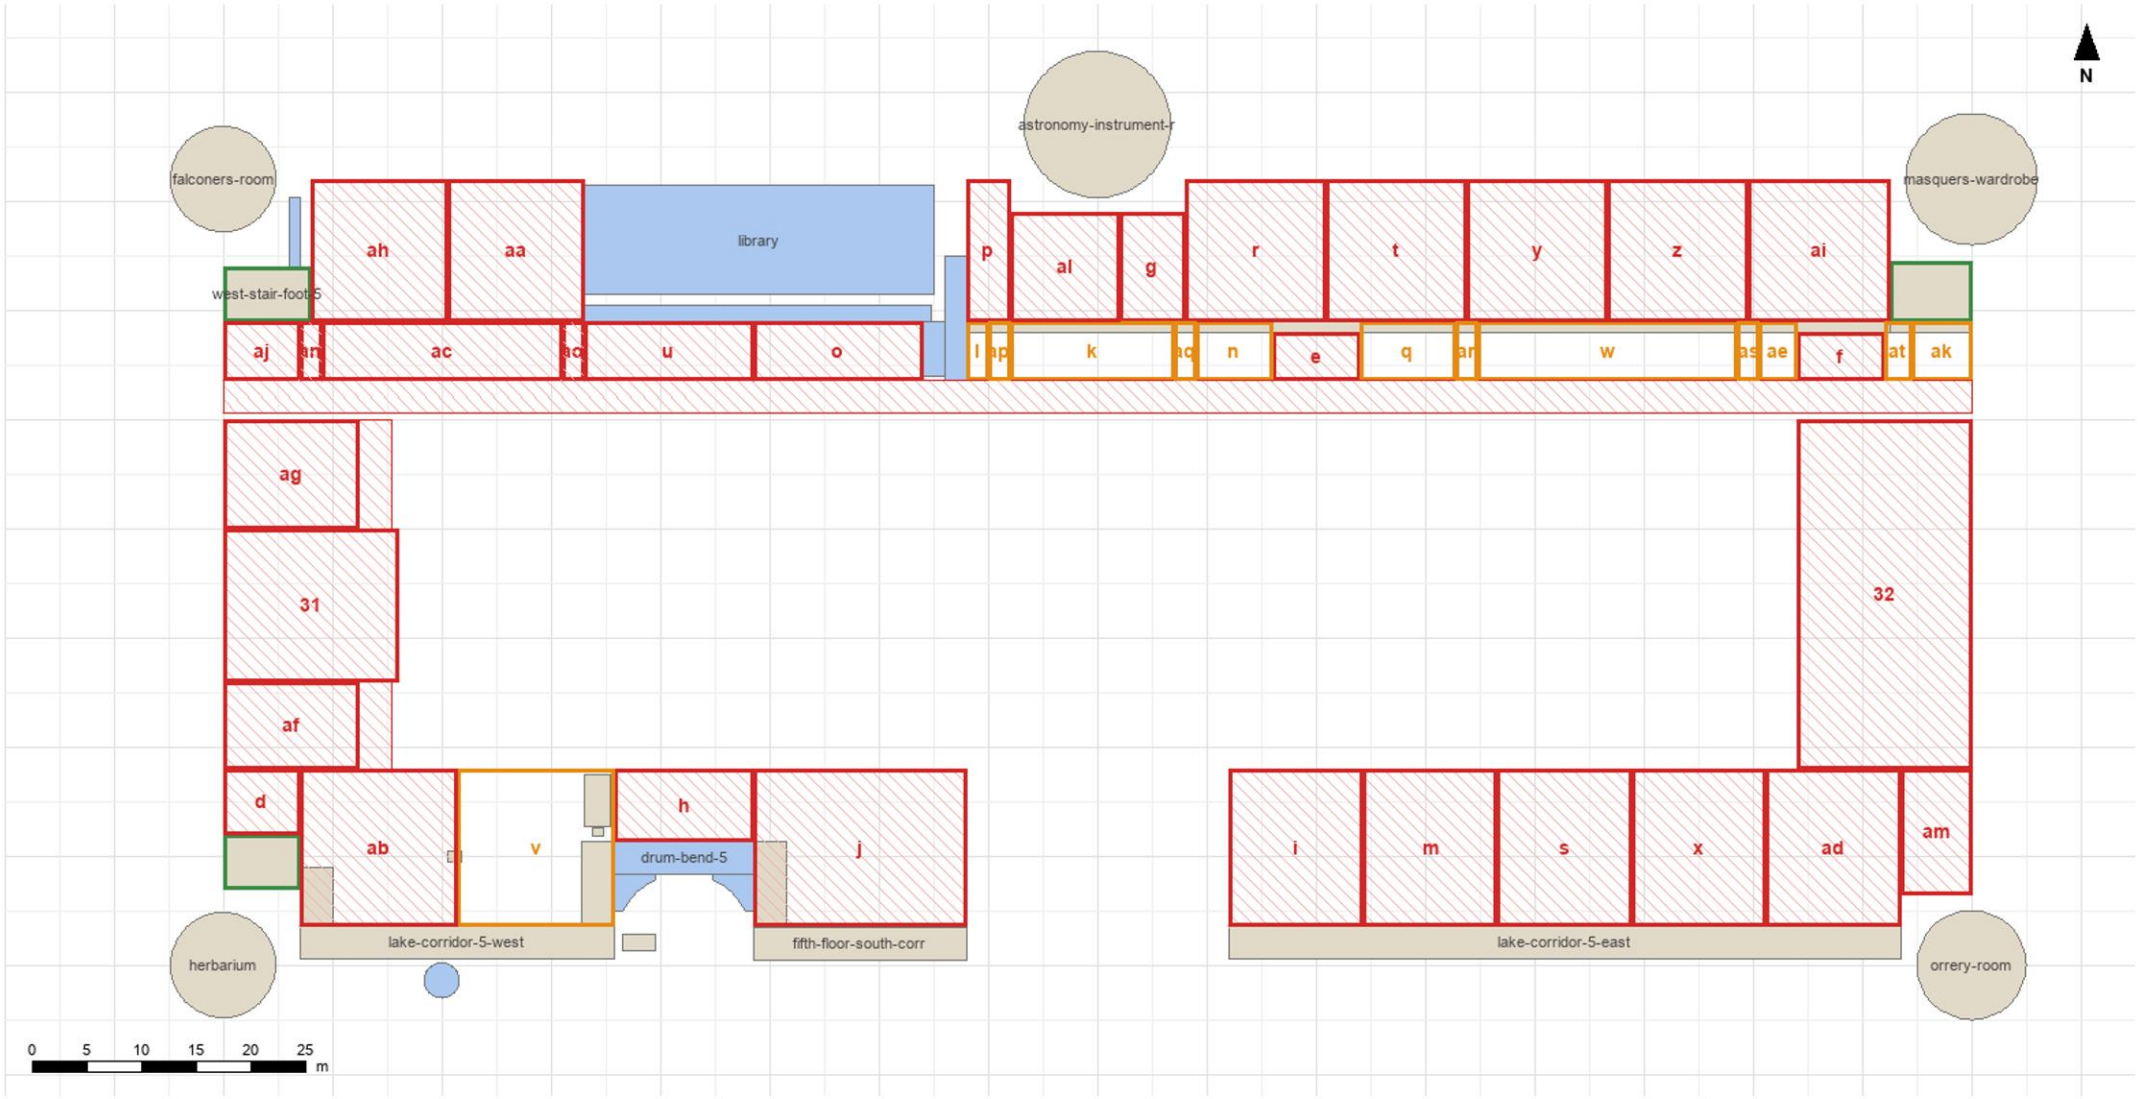

Plan: beige, built in the model (labelled by id); blue fill, built but on no layout room. Outlines, the agreed layout: red hatched missing, orange partly, blue built otherwise, green built. Grid 5 m.

missing fill d: Washrooms, girls' and boys', 45 m2, 4% built
missing fill e: Washrooms, girls' and boys', 37 m2, 6% built
missing fill f: Washrooms, girls' and boys', 37 m2, 6% built
missing fill g: The Astronomy Tower's stair foot, its stair to the top, 6
missing fill h: A Gryffindor storeroom at the tower's foot, 88 m2, 4% bui
missing fill i: The fifth-floor corridor of armour, to a spiral stair, 18
missing fill j: The Head Boy and Head Girl's study, 286 m2, 9% built
partly fill k: A broom cupboard, 84 m2, 23% built
partly fill l: A service passage, 12 m2, 31% built
missing fill m: The O.W.L. examiners' rooms, 181 m2, 2% built
partly fill n: A store of spare desks and chairs, 40 m2, 23% built
missing fill o: A linen cupboard, 87 m2, 6% built
missing fill p: Filch's cleaning cupboard, 56 m2, 5% built
partly fill q: A store of old textbooks, 50 m2, 23% built
missing fill r: Professor Sinistra's star-chart room, 172 m2, 2% built


missing fill s: The music room, 181 m2, 2% built
missing fill t: The ledgers of house points, 176 m2, 2% built
missing fill u: A lamp and candle cupboard, 87 m2, 5% built
partly fill v: The girls' dormitories' linen store, 214 m2, 20% built
partly fill w: A store, 132 m2, 23% built
missing fill x: Staff bedrooms, 181 m2, 2% built
missing fill y: Staff bedroom, 172 m2, 2% built
missing fill z: A study room, 176 m2, 2% built
missing fill aa: A teacher's study, 169 m2, 2% built
missing fill ab: Staff bedroom, 210 m2, 11% built
missing fill ac: A house-elves' linen room, 122 m2, 0% built
missing fill ad: A disused classroom, 185 m2, 2% built
partly fill ae: A store of spare desks and chairs, 21 m2, 23% built
missing fill af: The prefects' common room, 103 m2, 0% built
missing fill ag: A teacher's study, 128 m2, 0% built

missing fill ah: A disused classroom, 169 m2, 1% built
missing fill ai: A teacher's study, 176 m2, 3% built
missing fill aj: A linen cupboard, 40 m2, 5% built
partly fill ak: Filch's cleaning cupboard, 32 m2, 23% built
missing fill al: A teacher's study, 105 m2, 2% built
missing fill am: A teacher's study, 79 m2, 0% built
missing fill an: A passage to the rooms behind, 12 m2, 3% built
missing fill ao: A passage to the rooms behind, 12 m2, 1% built
partly fill ap: A passage to the rooms behind, 12 m2, 23% built
partly fill aq: A passage to the rooms behind, 12 m2, 23% built
partly fill ar: A passage to the rooms behind, 12 m2, 23% built
partly fill as: A passage to the rooms behind, 12 m2, 23% built
partly fill at: A passage to the rooms behind, 15 m2, 23% built
missing named 31: Prefects' bathroom, by Boris the Bewildered (the spot p
missing named 32: The east wing, named on the fifth floor, 524 m2, 0% bui

corridors missing or partly: 10
model only library: the library, 331 m2
model only back-stair-lobby-5: the back stair's lobby on 5, 24 m2
model only library-gallery: the gallery behind the library's shelves, the
model only library-gallery-way: the head of the gallery's stair and the w
model only oriel-bay: the window with no room, the Tudor oriel's lower st
model only west-tower-way-5: the passage from the West Tower's stair sout
model only drum-bend-5: the corridor round the Gryffindor Tower's foot on
model only ink-room: the ink room, behind a panel west of the Gryffindor
model only lamp-store-5: the lamp store east of the Gryffindor drum on 5,

Sixth floor (6): actuals and busts

Built in the model (v229): 30 rooms, 1947 m2. Agreed layout (v71): 7 rooms built, 3 built otherwise, 32 partly, 29 missing; 5345 m2 of it unbuilt. 9 model rooms on no layout room.

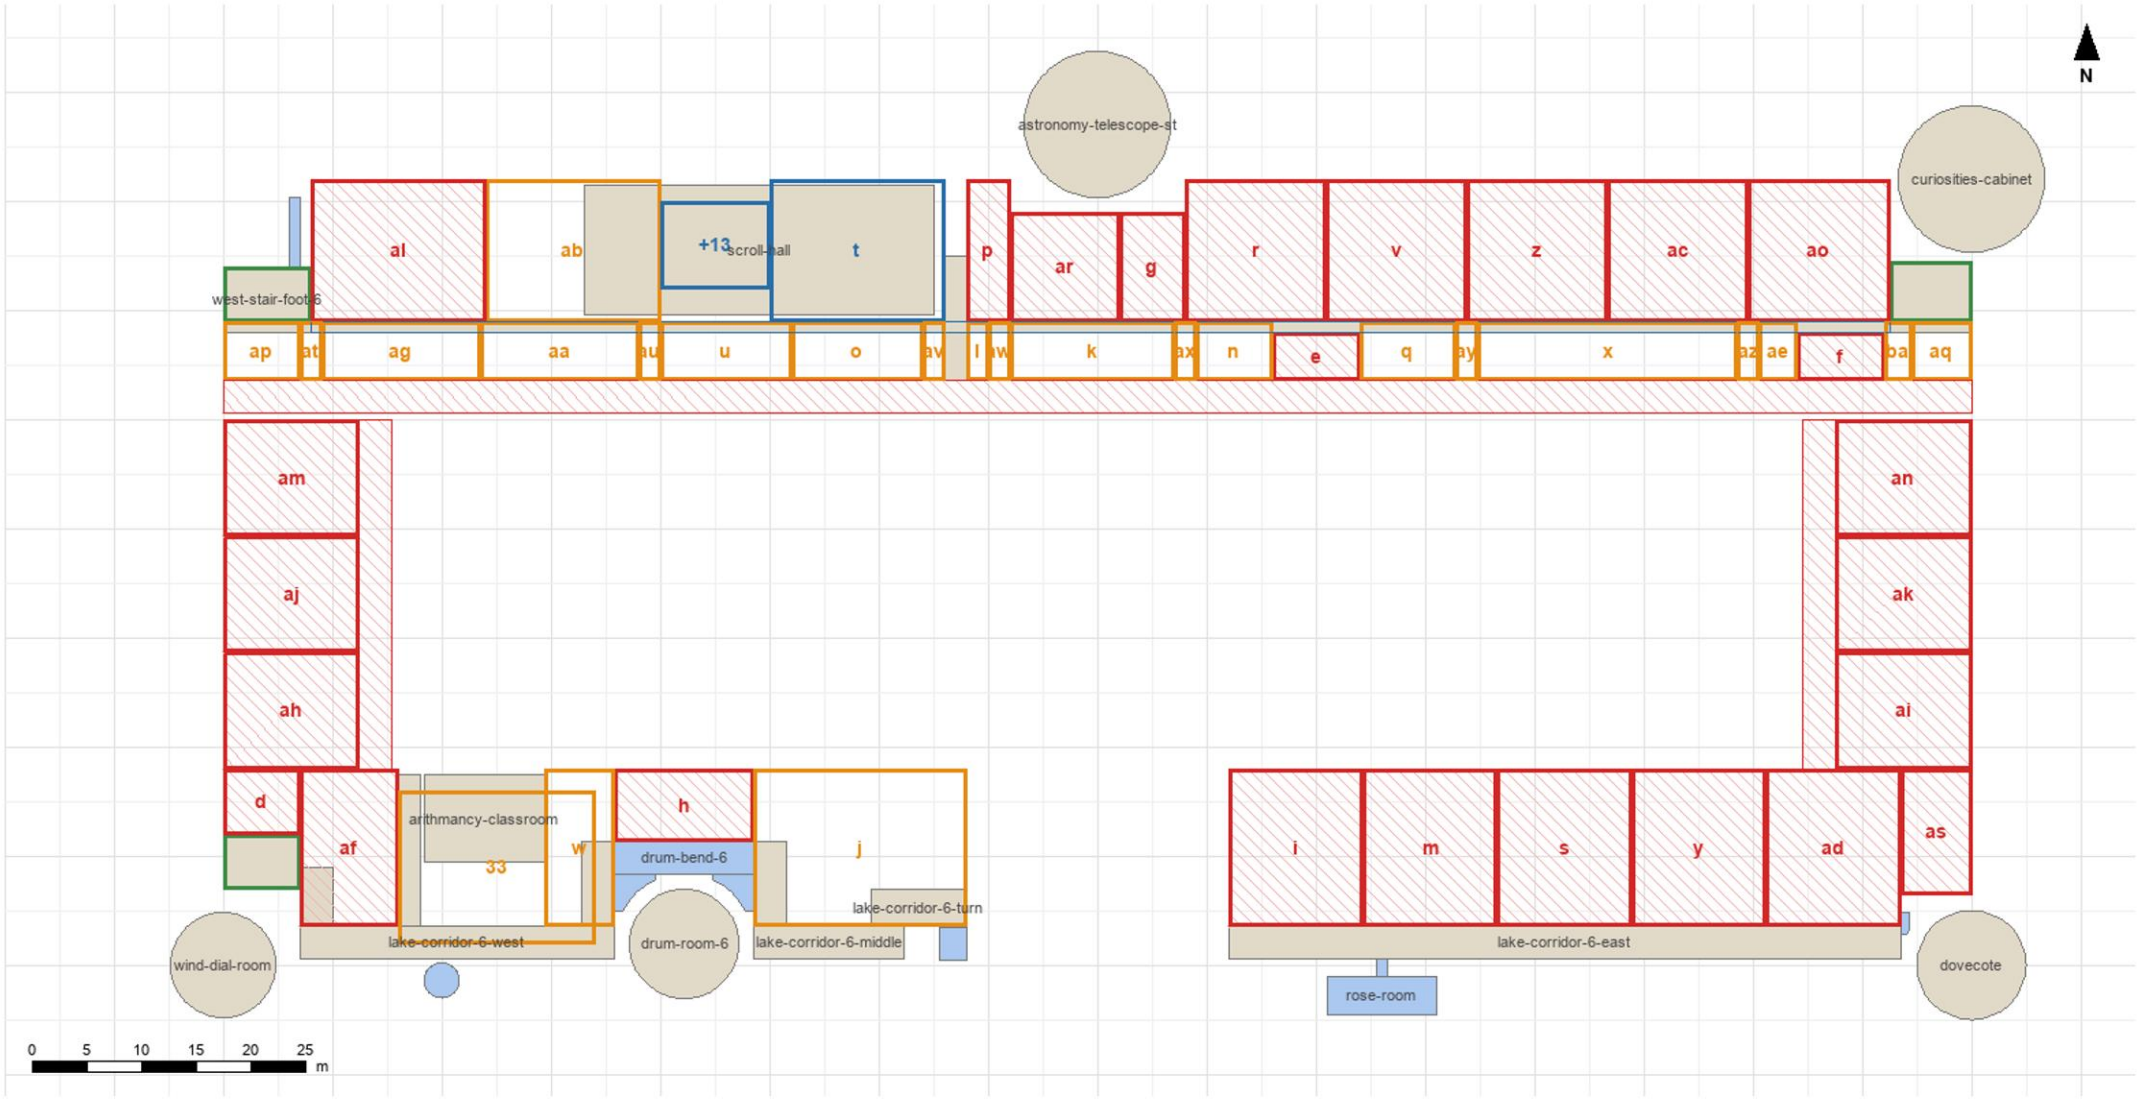


Plan: beige, built in the model (labelled by id); blue fill, built but on no layout room. Outlines, the agreed layout: red hatched missing, orange partly, blue built otherwise, green built. Grid 5 m.

missing fill d: Washrooms, girls' and boys', 45 m2, 4% built
missing fill e: Washrooms, girls' and boys', 37 m2, 6% built
missing fill f: Washrooms, girls' and boys', 37 m2, 6% built
missing fill g: The Astronomy Tower's stair foot, its stair to the top, 6
missing fill h: A Gryffindor storeroom at the tower's foot, 88 m2, 4% bui
missing fill i: The frog choir's practice room, 181 m2, 2% built
partly fill j: The clock room, where the castle's clocks are wound, 286 m
partly fill k: A broom cupboard, 84 m2, 23% built
partly fill l: A service passage, 12 m2, 31% built
missing fill m: Guest rooms for visiting parents, 181 m2, 2% built
partly fill n: The telescope store, 40 m2, 23% built
partly fill o: A house-elves' linen room, 67 m2, 23% built
missing fill p: Filch's cleaning cupboard, 56 m2, 5% built
partly fill q: A store of old textbooks, 50 m2, 23% built
missing fill r: A teacher's study, 172 m2, 2% built
missing fill s: Staff bedrooms, 181 m2, 2% built
partly fill u: A lamp and candle cupboard, 67 m2, 23% built
missing fill v: Staff bedroom, 176 m2, 2% built
partly fill w: Professor Vector's study, 98 m2, 30% built
partly fill x: A store, 132 m2, 23% built
missing fill y: A disused classroom, 181 m2, 2% built
missing fill z: A teacher's study, 172 m2, 2% built
partly fill aa: A broom cupboard, 81 m2, 23% built
partly fill ab: A study room, 215 m2, 42% built
missing fill ac: A disused classroom, 176 m2, 2% built
missing fill ad: A house-elves' linen room, 185 m2, 2% built
partly fill ae: A store of spare desks and chairs, 21 m2, 23% built
missing fill af: The Arithmancy store of number charts, 134 m2, 18% built
partly fill ag: A linen cupboard, 81 m2, 23% built
missing fill ah: Arithmancy room for the N.E.W.T. years, 138 m2, 0% built
missing fill ai: Staff bedroom, 140 m2, 0% built
missing fill aj: A disused classroom, 138 m2, 0% built
missing fill ak: A teacher's study, 140 m2, 0% built
missing fill al: Staff bedroom, 215 m2, 2% built
missing fill am: A study room, 134 m2, 0% built
missing fill an: A house-elves' linen room, 137 m2, 0% built
missing fill ao: Staff bedroom, 176 m2, 3% built
partly fill ap: Filch's cleaning cupboard, 40 m2, 23% built
partly fill aq: A store of old textbooks, 32 m2, 23% built
missing fill ar: A teacher's study, 105 m2, 2% built
missing fill as: A teacher's study, 79 m2, 0% built
partly fill at: A passage to the rooms behind, 12 m2, 23% built
partly fill au: A passage to the rooms behind, 12 m2, 23% built
partly fill av: A passage to the rooms behind, 12 m2, 31% built
partly fill aw: A passage to the rooms behind, 12 m2, 23% built
partly fill ax: A passage to the rooms behind, 12 m2, 23% built
partly fill ay: A passage to the rooms behind, 12 m2, 23% built
partly fill az: A passage to the rooms behind, 12 m2, 23% built
partly fill ba: A passage to the rooms behind, 15 m2, 23% built
partly named 33: Arithmancy classroom (proposed); the sixth floor holds t
corridors missing or partly: 11
model only secret-s4b: the store for the common room's fire, under the co
model only rose-room: the room behind the rose, under the Tudor bay's gab
model only rose-room-way: the short passage from the sixth floor's lake c
model only down-only-stair-way-6: the narrow way behind the lake corridor
model only tally-room: the tally room, the Tudor oriel's upper storey, 10
model only west-tower-way-6: the passage from the West Tower's stair sout
model only drum-bend-6: the corridor round the Gryffindor Tower's foot on
model only gryffindor-lav-witches-6: the witches' lavatory in the pocket
model only gryffindor-lav-wizards-6: the wizards' lavatory in the pocket

Seventh floor (7): actuals and busts

Built in the model (v229): 29 rooms, 2199 m2. Agreed layout (v71): 8 rooms built, 7 built otherwise, 28 partly, 20 missing; 3409 m2 of it unbuilt. 8 model rooms on no layout room.

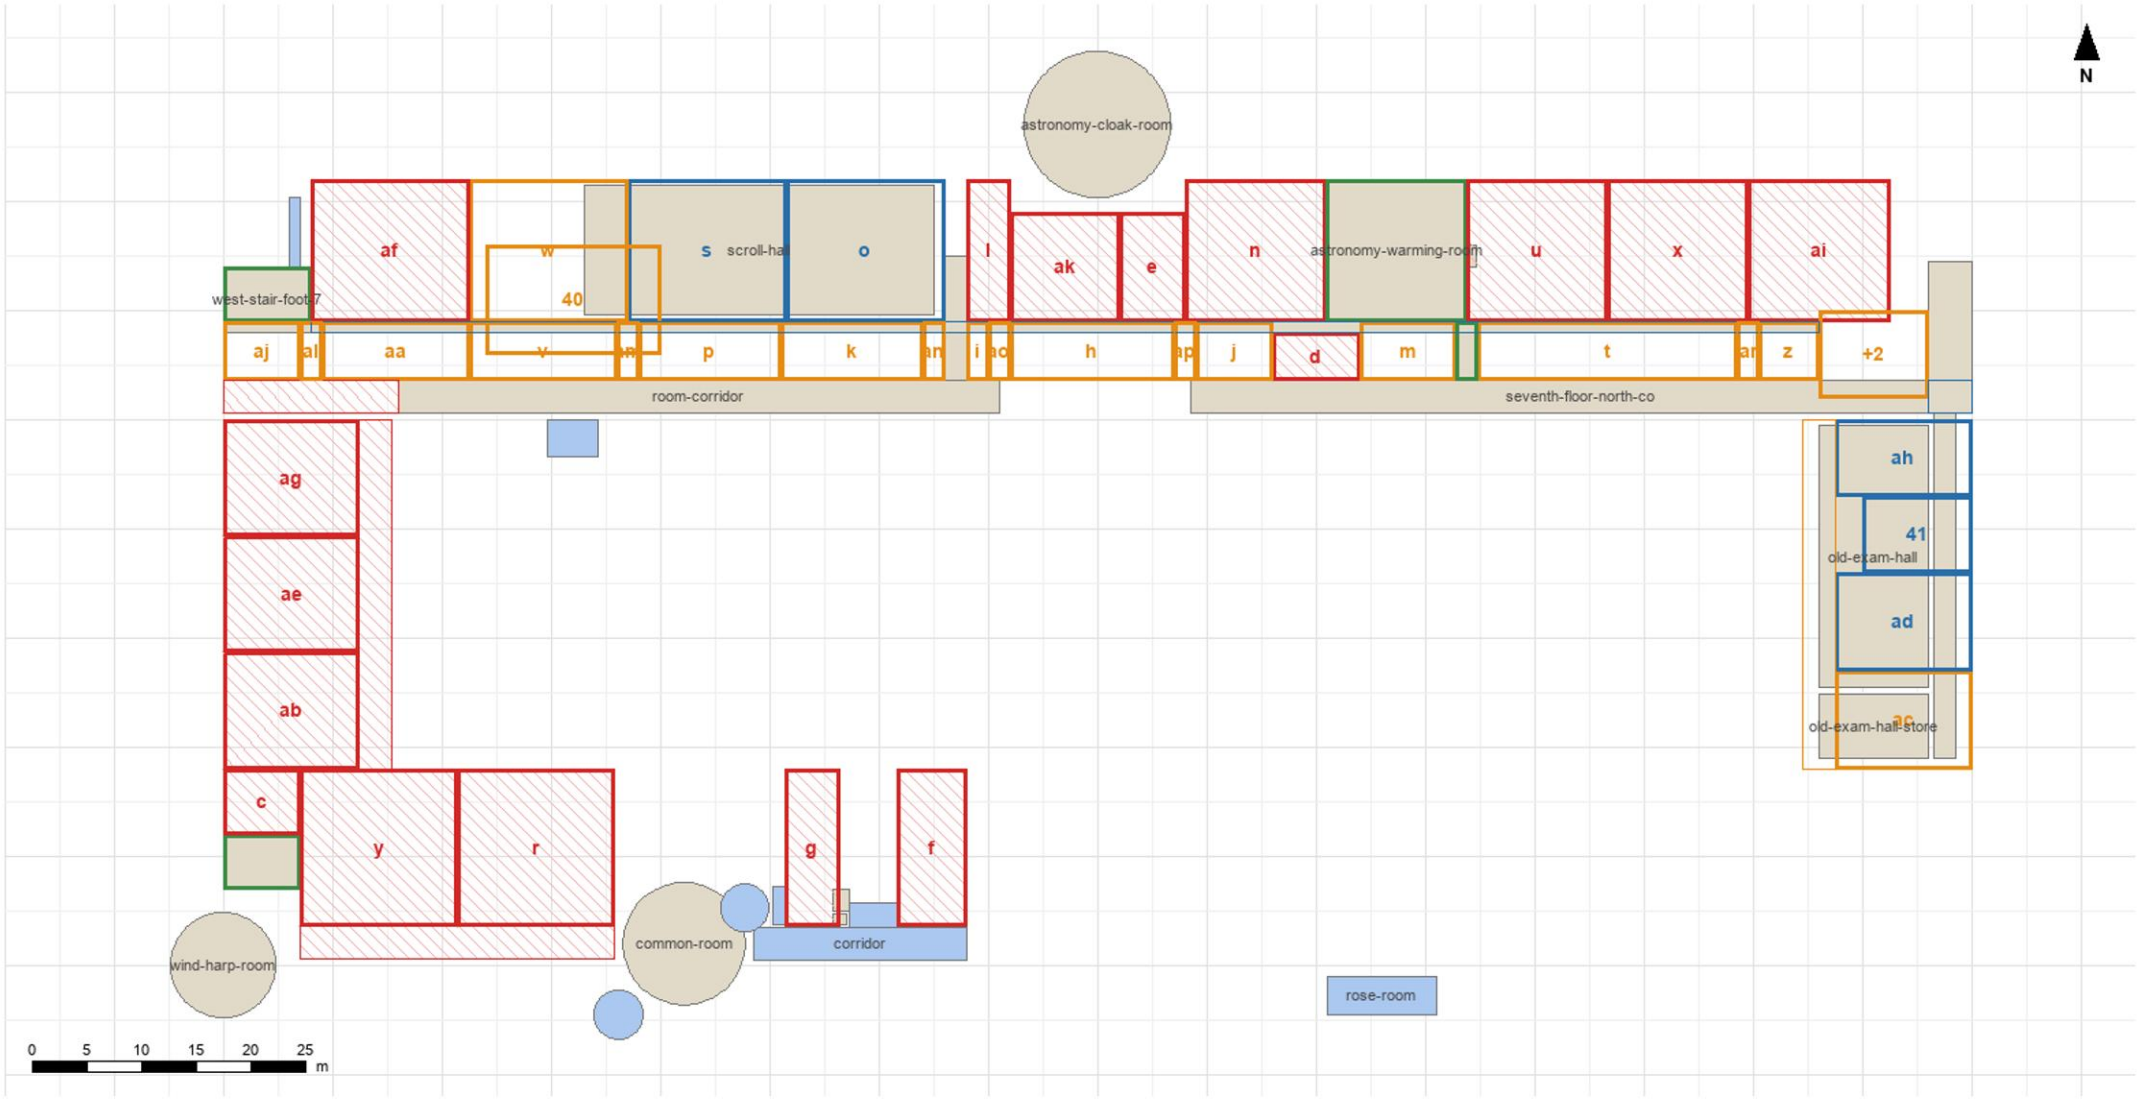

Plan: beige, built in the model (labelled by id); blue fill, built but on no layout room. Outlines, the agreed layout: red hatched missing, orange partly, blue built otherwise, green built. Grid 5 m.

missing fill c: Washrooms, girls' and boys', 45 m2, 4% built
missing fill d: Washrooms, girls' and boys', 37 m2, 11% built
missing fill e: The Astronomy Tower's stair foot, its stair to the top, 6
missing fill f: The Headmaster's guest rooms, 98 m2, 1% built
missing fill g: The seventh-floor broom cupboard, 76 m2, 5% built
partly fill h: A broom cupboard, 84 m2, 23% built
partly fill i: A service passage, 12 m2, 35% built
partly fill j: A store of spare desks and chairs, 40 m2, 27% built
partly fill k: A linen cupboard, 73 m2, 27% built
missing fill l: Filch's cleaning cupboard, 56 m2, 5% built
partly fill m: A store of old textbooks, 50 m2, 28% built
missing fill n: The corridor beneath the tallest tower, 172 m2, 4% built
partly fill p: A lamp and candle cupboard, 73 m2, 27% built
missing fill r: Staff bedrooms, 214 m2, 0% built
partly fill t: A store, 132 m2, 28% built

missing fill u: A teacher's study, 172 m2, 5% built
partly fill v: A broom cupboard, 76 m2, 27% built
partly fill w: Staff bedroom, 195 m2, 28% built
missing fill x: A study room, 176 m2, 2% built
missing fill y: A house-elves' linen room, 210 m2, 1% built
partly fill z: Professor Trelawney's sherry store, 32 m2, 27% built
partly fill aa: A house-elves' linen room, 76 m2, 25% built
missing fill ab: Staff bedroom, 138 m2, 0% built
partly fill ac: A disused classroom, 118 m2, 75% built
missing fill ae: A study room, 138 m2, 0% built
missing fill af: A teacher's study, 195 m2, 3% built
missing fill ag: A house-elves' linen room, 134 m2, 0% built
missing fill ai: A teacher's study, 176 m2, 1% built
partly fill aj: Filch's cleaning cupboard, 40 m2, 23% built
missing fill ak: A teacher's study, 105 m2, 2% built

partly fill al: A passage to the rooms behind, 12 m2, 23% built
partly fill am: A passage to the rooms behind, 12 m2, 27% built
partly fill an: A passage to the rooms behind, 12 m2, 35% built
partly fill ao: A passage to the rooms behind, 12 m2, 25% built
partly fill ap: A passage to the rooms behind, 12 m2, 24% built
partly fill ar: A passage to the rooms behind, 12 m2, 27% built
partly named 40: Room of Requirement on its own seventh-floor corridor (Q
partly named +2: Sir Cadogan's landing, at the top of the seventh long st
corridors missing or partly: 10
model only corridor: the Fat Lady's corridor, 63 m2
model only inglenook: the inglenook, where visitors wait, 11 m2
model only study: Clementine's study, a half-round room off the tower ins
model only lost-things: the room of lost things, behind the polite door,
model only den: the den, behind the little door, 18 m2
model only room-of-requirement: the Room of Requirement, on its own corri

model only rose-room: the room behind the rose, under the Tudor bay's gab
model only west-tower-way-7: the passage from the West Tower's stair sout