The disposition of the agreed layout's rooms, by floor (model v229, layout v71), sheet 1 of 5

Wall rule applied: inner walls 0.5, outer walls outward. Now: the room's state in the model today. Disposition: built; as drawn; trimmed round a kept room; follows a room the model holds elsewhere; reimagine (cannot be built as the layout drew it).

Cellars and dungeons (B): 8 built, 37 as drawn, 5 trimmed, 1 follows; 2 true voids, 8 thick walls

Code	Layout room	m2	Now	Disposition	Note
2	Hufflepuff's basement corridor, which al	168	partly 23%	trimmed	29.3 x 2.7 m (79 m2), round kitchens-corridor, kitc
ad	Potions dungeon for the N.E.W.T. years	132	missing	trimmed	12.1 x 4.0 m (48 m2), round walls
x	Potions dungeon for the O.W.L. years	132	missing	trimmed	12.1 x 4.0 m (48 m2), round walls
g	The house-elves' quarters	55	missing	trimmed	5.4 x 6.4 m (35 m2), round walls
c3	corridor	96	missing	trimmed	2.5 x 4.0 m (10 m2), round walls
3	Slytherin common room: the dungeons, und	384	missing	as drawn	32.0 x 12.0 m in its walls
4	Potions classroom, down in a dungeon (th	384	missing	as drawn	16.0 x 23.5 m in its walls
r	The wizard chess room	161	missing	as drawn	10.7 x 14.2 m in its walls
n	The dungeon store of old benches and des	161	missing	as drawn	10.7 x 14.2 m in its walls
v	The suits of armour's spare parts	161	missing	as drawn	10.7 x 13.9 m in its walls
l	Coal and log store for the castle's fire	148	missing	as drawn	12.4 x 11.2 m in its walls
q	The house banners and feast linen	148	missing	as drawn	12.4 x 11.2 m in its walls
af	The prefects' patrol room	148	missing	as drawn	12.7 x 11.2 m in its walls
o	A dungeon for detentions	148	missing	as drawn	12.4 x 11.2 m in its walls
u	The Christmas decorations, a dozen trees	148	missing	as drawn	12.4 x 11.2 m in its walls
aj	A store	136	missing	as drawn	15.5 x 8.2 m in its walls
ae	Portraits stacked, waiting for walls	132	missing	as drawn	12.2 x 10.2 m in its walls
y	Peeves's den of stolen chalk	132	missing	as drawn	12.2 x 10.2 m in its walls
ab	A practice room for spells gone wrong	132	missing	as drawn	12.2 x 10.2 m in its walls
w	The Potions ingredients store	130	missing	as drawn	8.5 x 13.9 m in its walls
ak	A store	75	missing	as drawn	6.2 x 11.2 m in its walls
t	A ghosts' gathering room, cold all year	55	missing	as drawn	7.4 x 6.6 m in its walls
f	The cold room for the feasts	55	missing	as drawn	7.4 x 6.6 m in its walls
h	The kitchen stores: flour, sugar, the pu	55	missing	as drawn	7.4 x 6.6 m in its walls
i	The brewing cellar, where slow potions s	55	missing	as drawn	7.4 x 6.6 m in its walls
m	Filch's store of confiscated things	55	missing	as drawn	7.4 x 6.6 m in its walls
p	The store of spare cauldrons	55	missing	as drawn	7.4 x 6.6 m in its walls
e	The scullery	55	missing	as drawn	7.4 x 6.6 m in its walls
j	The cellar of butterbeer and pumpkin jui	55	missing	as drawn	7.4 x 6.6 m in its walls
s	The quill, ink and parchment store	55	missing	as drawn	7.4 x 6.6 m in its walls
z	The candle store for the Great Hall	55	missing	as drawn	7.4 x 6.4 m in its walls
ag	The school's spare robes	55	missing	as drawn	7.7 x 6.4 m in its walls
ac	The laundry, by the kitchens	52	missing	as drawn	7.0 x 6.4 m in its walls
ah	The kitchens' bakery ovens	52	missing	as drawn	7.2 x 6.4 m in its walls
k	A broom cupboard	46	missing	as drawn	3.5 x 11.2 m in its walls
d	Washrooms, girls' and boys'	42	missing	as drawn	6.8 x 5.5 m in its walls
c	The south-west tower's stair foot, a sta	35	missing	as drawn	6.8 x 4.8 m in its walls
ai	A store of spare desks and chairs	34	missing	as drawn	2.8 x 11.2 m in its walls
b	The North Tower's stair foot, a stair be	30	missing	as drawn	7.2 x 3.8 m in its walls
c1	corridor	285	missing	as drawn	94.8 x 2.5 m in its walls
c4	corridor	96	missing	as drawn	2.8 x 31.5 m in its walls
c7	corridor	33	missing	as drawn	10.8 x 2.5 m in its walls
aa	Dungeon five, where the frog brains went	132	missing	follows	its ground is layout 4
5	Dungeon corridors, the deathday party (t	1248	partly 74%	built	as dungeon-corridor, hall-undercroft, founders-unde
1	Kitchens: four long tables, each exactly	900	built	built	as kitchens
a	The West Tower's stair foot, a stair bet	28	built	built	as west-stair-foot-b
+1	Snape's office, halfway down the cold pa	20	built	built	as snape-office
c2	corridor	184	built	built	as lake-corridor-b-east
c5	corridor	86	built	built	as lake-corridor-b-west
c6	corridor	58	built	built	as lake-corridor-b-keep
c8	corridor	13	built	built	as old-cells-passage

Ground floor (G): 49 built, 2 follows; 14 true voids, 17 thick walls

Code	Layout room	m2	Now	Disposition	Note
9	Marble staircase, facing the front doors	98	partly 38%	follows	stands as the marble staircase, in the entrance hal
v	A service passage	14	missing	follows	hung on 14, which stands as staff-room
11	Great Hall, through a doorway to the rig	900	built	built	as great-hall
8	Entrance Hall, its front doors in the no	480	built	built	as entrance-hall
h	The girls' toilets by the Great Hall's w	279	built otherwise	built	as peeves-lumber-room, girls-toilets-g, boys-toilet
p	The Quidditch teams' kit room	207	built	built	as quidditch-kit-room, drum-bend-g-west, kit-broom-
s	The Duelling Club's practice room	207	built	built	as duelling-practice-room, sw-corner-lobby-g
n	The post room, where the owls' parcels w	177	built	built	as post-room
t	The school archive of old registers	177	built	built	as registers-archive
g	A free classroom (Care of Magical Creatu	177	built	built	as free-classroom-g
k	The visitors' parlour, where parents wai	177	built	built	as visitors-parlour
q	The treatment room for Quidditch knocks	177	built	built	as treatment-room
12	The corridor of classrooms opposite the	156	built otherwise	built	as classroom-corridor, classroom-corridor-east
ab	The old trophies' overflow	132	built	built	as old-trophies-overflow
aa	The store of exam desks for the Great Ha	132	built	built	as exam-desks-store
x	The Herbology potting room and seed stor	132	built	built	as potting-room
z	Professor Sprout's study, by the greenho	132	built	built	as herbology-study-g
w	The house-elves' service stair from the	132	built	built	as elves-service-stair-g
y	The owl-treats store	132	built	built	as owl-treats-store
r	Classroom eleven, a forest room for Fire	132	built	built	as classroom-eleven
u	The staff dining room, behind the staff	132	built	built	as staff-dining-room
ac	A house-elves' linen room	132	built	built	as elves-linen-room-g
+11	The chamber off the Great Hall, behind t	121	built	built	as hall-chamber
13	Filch's office: Harry follows him "back	112	built otherwise	built	as filchs-office, filchs-store
14	The staff room: Harry goes "down" to it	112	built	built	as staff-dining-room, elves-linen-room-g
10	The small, empty chamber off the hall (t	96	built otherwise	built	as waiting-chamber, punishments-room
f	A Gryffindor storeroom at the tower's fo	85	built	built	as gryffindor-store-g
af	A teacher's study	75	built	built	as teachers-study-g
d	Washrooms, girls' and boys'	55	built	built	as washrooms-g-north
e	Washrooms, girls' and boys'	55	built	built	as washrooms-g-east
ad	Staff bedroom	55	built	built	as staff-bedroom-g
m	The cloakroom, wet boots and cloaks	47	built	built	as cloakroom-g
l	The porters' lodge by the front doors	47	built	built	as porters-lodge
o	Madam Hooch's store of school brooms	47	built	built	as school-brooms-store
c	Washrooms, girls' and boys'	42	built	built	as washrooms-g
b	The south-west tower's stair foot, a sta	35	built	built	as sw-stair-foot-g
a	The North Tower's stair foot, a stair be	30	built	built	as north-stair-foot-g
j	A store of spare desks and chairs	28	built	built	as spare-desks-store, entrance-hall
ae	A linen cupboard	28	built	built	as linen-cupboard-g-west
i	A broom cupboard	21	partly 54%	built	as hall-slot-cupboard, entrance-hall, great-hall (5
+12	The broom cupboard across the hall	2	built	built	as hall-cupboard
c1	corridor	184	built	built	as lake-corridor-g-east
c2	corridor	97	built	built	as classroom-corridor-east
c3	corridor	96	built	built	as west-wing-corridor-g
c4	corridor	96	built	built	as east-wing-corridor-g
c5	corridor	86	built	built	as lake-corridor-g-west
c6	corridor	60	built	built	as gate-passage
c7	corridor	58	built	built	as lake-corridor-g-mid
c8	corridor	21	built	built	as staff-passage
c9	corridor	12	built	built	as hall-chamber-way, hall-chamber
c10	corridor	9	built otherwise	built	as great-hall-doors-passage

First floor (1): 31 as drawn, 14 built, 1 reimagine, 3 trimmed, 4 follows; 12 true voids, 30 thick walls

Code	Layout room	m2	Now	Disposition	Note
16	McGonagall's study, first floor (off the	96	partly 24%	reimagine	a smaller room, 26 of 96 m2: 5.4 x 4.9 m left by fi
y	A teacher's study	91	missing	trimmed	5.9 x 10.5 m (62 m2), round walls
ac	A passage to the rooms behind	12	missing	trimmed	1.2 x 5.2 m (6 m2), round entrance-hall
c15	corridor	9	missing	trimmed	1.9 x 2.2 m (4 m2), round entrance-hall, great-hall
15	The moving staircases and the marble sta	1200	missing	as drawn	23.8 x 49.5 m in its walls
20	History of Magic classroom, "large enoug	392	missing	as drawn	27.5 x 13.5 m in its walls
h	The History of Magic archive of old exam	279	missing	as drawn	18.9 x 14.2 m in its walls
m	Madam Pomfrey's dispensary	207	missing	as drawn	13.9 x 14.2 m in its walls
q	The hospital wing's quiet rooms	207	missing	as drawn	13.9 x 13.9 m in its walls
o	Transfiguration store: cages of practice	161	missing	as drawn	10.7 x 14.2 m in its walls

The disposition of the agreed layout's rooms, by floor (model v229, layout v71), sheet 2 of 5

Wall rule applied: inner walls 0.5, outer walls outward. Now: the room's state in the model today. Disposition: built; as drawn; trimmed round a kept room; follows a room the model holds elsewhere; reimagine (cannot be built as the layout drew it).

l	Professor Binns's study, never used	161	missing	as drawn	10.7 x 14.2 m in its walls
s	Professor McGonagall's rooms	161	missing	as drawn	10.7 x 13.9 m in its walls
j	Transfiguration classroom for the N.E.W.	156	missing	as drawn	11.5 x 12.8 m in its walls
x	The Deputy Head's records room	132	missing	as drawn	11.9 x 10.2 m in its walls
t	The classroom with the chandelier	132	missing	as drawn	11.9 x 10.2 m in its walls
v	An empty classroom off the first-floor c	132	missing	as drawn	11.9 x 10.2 m in its walls
+8	The first-floor room over Filch's office	112	missing	as drawn	13.5 x 7.5 m in its walls
k	A broom cupboard	95	missing	as drawn	17.1 x 4.9 m in its walls
g	A Gryffindor storeroom at the tower's fo	85	missing	as drawn	12.3 x 6.4 m in its walls
aa	The staff library	75	missing	as drawn	6.2 x 11.0 m in its walls
p	A linen cupboard	65	missing	as drawn	11.5 x 4.9 m in its walls
n	A store of spare desks and chairs	47	missing	as drawn	3.1 x 12.8 m in its walls
u	A store of old textbooks	45	missing	as drawn	12.2 x 3.1 m in its walls
e	Washrooms, girls' and boys'	43	missing	as drawn	7.5 x 4.9 m in its walls
f	Washrooms, girls' and boys'	43	missing	as drawn	7.5 x 4.9 m in its walls
d	Washrooms, girls' and boys'	42	missing	as drawn	6.8 x 5.5 m in its walls
z	A store	38	missing	as drawn	6.8 x 4.9 m in its walls
w	The hospital wing's linen room	32	missing	as drawn	5.5 x 4.9 m in its walls
r	Filch's cleaning cupboard	26	missing	as drawn	4.3 x 4.9 m in its walls
i	A service passage	11	missing	as drawn	1.5 x 4.9 m in its walls
ab	A passage to the rooms behind	11	missing	as drawn	1.5 x 4.9 m in its walls
c4	corridor	96	missing	as drawn	2.5 x 31.5 m in its walls
c5	corridor	86	missing	as drawn	28.3 x 2.5 m in its walls
c6	corridor	58	missing	as drawn	18.9 x 2.5 m in its walls
c7	corridor	45	missing	as drawn	14.8 x 2.5 m in its walls
c8	corridor	41	missing	follows	it lies in the walls of the rooms beside it
c12	corridor	12	missing	follows	it lies in the walls of entrance-hall
c13	corridor	11	missing	follows	its ground is layout ab
c17	corridor	6	missing	follows	it lies in the walls of the rooms beside it
17	Transfiguration classroom, beside her st	432	partly 56%	built	as history-of-magic-classroom, history-of-magic-pas
19	Hospital wing: "up" from the dungeons; t	288	built otherwise	built	as hospital-wing, east-first-floor-corridor, pomfre
b	The North Tower's stair foot, a stair be	41	built	built	as north-stair-foot-1
a	The West Tower's stair foot, a stair bet	40	built	built	as west-stair-foot-1
c	The south-west tower's stair foot, a sta	35	built	built	as sw-stair-foot-1
ad	A passage to the rooms behind	11	built otherwise	built	as mcgonagall-landing-passage-1
c1	corridor	205	built	built	as first-floor-corridor
c2	corridor	100	built otherwise	built	as lake-corridor-1-east
c3	corridor	96	built	built	as east-first-floor-corridor
c9	corridor	37	built	built	as transfiguration-passage
c10	corridor	37	built	built	as history-of-magic-passage
c11	corridor	35	built	built	as hospital-passage
c14	corridor	11	built otherwise	built	as mcgonagall-landing-passage-1
c16	corridor	6	built otherwise	built	as mcgonagall-landing-passage-1

Second floor (2): 39 as drawn, 1 reimagine, 3 trimmed, 9 built, 6 follows; 13 true voids, 22 thick walls

Code	Layout room	m2	Now	Disposition	Note
18	Myrtle's bathroom, the Chamber's door: t	160	partly 46%	reimagine	a smaller room, 50 of 160 m2: 11.9 x 4.2 m left by
aa	Staff bedroom	155	missing	trimmed	11.9 x 7.4 m (88 m2), round walls
m	A linen cupboard	52	missing	trimmed	2.9 x 12.8 m (37 m2), round walls
j	A service passage	11	missing	trimmed	1.2 x 5.0 m (6 m2), round back-stair-lobby-2
p	The Gobstones Club room	177	missing	as drawn	11.8 x 14.2 m in its walls
v	Staff bedrooms	177	missing	as drawn	11.8 x 13.9 m in its walls
h	Lockhart's office, later a Defence spare	177	missing	as drawn	11.8 x 14.2 m in its walls
k	Slughorn's office, larger inside than ou	177	missing	as drawn	11.8 x 14.2 m in its walls
s	A duelling practice room	177	missing	as drawn	11.8 x 14.2 m in its walls
o	The Slug Club's dining room	168	missing	as drawn	12.4 x 12.8 m in its walls
t	The map room	168	missing	as drawn	12.4 x 12.5 m in its walls
af	A disused classroom	168	missing	as drawn	12.4 x 12.8 m in its walls
q	The second-floor girls' washroom, the on	168	missing	as drawn	12.4 x 12.5 m in its walls
u	A second years' study room	168	missing	as drawn	12.4 x 12.5 m in its walls
ad	A house-elves' linen room	155	missing	as drawn	12.2 x 12.0 m in its walls
ae	Staff bedroom	132	missing	as drawn	11.9 x 10.2 m in its walls
y	A teacher's study	132	missing	as drawn	11.9 x 10.2 m in its walls
ab	A study room	132	missing	as drawn	11.9 x 10.2 m in its walls
x	A disused classroom	130	missing	as drawn	8.5 x 13.9 m in its walls
r	A store of old textbooks	128	missing	as drawn	23.3 x 4.9 m in its walls
ag	A teacher's study	91	missing	as drawn	6.5 x 12.5 m in its walls
i	A broom cupboard	81	missing	as drawn	14.5 x 4.9 m in its walls
aj	A teacher's study	75	missing	as drawn	6.2 x 11.0 m in its walls
g	The Astronomy Tower's stair foot, its st	60	missing	as drawn	5.5 x 9.5 m in its walls
n	Filch's cleaning cupboard	48	missing	as drawn	8.3 x 4.9 m in its walls
e	Washrooms, girls' and boys'	43	missing	as drawn	7.5 x 4.9 m in its walls
f	Washrooms, girls' and boys'	43	missing	as drawn	7.5 x 4.9 m in its walls
d	Washrooms, girls' and boys'	42	missing	as drawn	6.8 x 5.5 m in its walls
l	A store of spare desks and chairs	38	missing	as drawn	6.5 x 4.9 m in its walls
ah	A broom cupboard	38	missing	as drawn	6.8 x 4.9 m in its walls
ac	A store	32	missing	as drawn	5.5 x 4.9 m in its walls
ai	A store of spare desks and chairs	30	missing	as drawn	5.2 x 4.9 m in its walls
z	A service passage	25	missing	as drawn	12.2 x 1.5 m in its walls
w	A lamp and candle cupboard	18	missing	as drawn	2.9 x 4.9 m in its walls
ap	A passage to the rooms behind	14	missing	as drawn	2.0 x 4.9 m in its walls
ak	A passage to the rooms behind	11	missing	as drawn	1.5 x 4.9 m in its walls
al	A passage to the rooms behind	11	missing	as drawn	1.5 x 4.9 m in its walls
am	A passage to the rooms behind	11	missing	as drawn	1.5 x 4.9 m in its walls
an	A passage to the rooms behind	11	missing	as drawn	1.5 x 4.9 m in its walls
ao	A passage to the rooms behind	11	missing	as drawn	1.5 x 4.9 m in its walls
c1	corridor	285	missing	as drawn	94.8 x 2.5 m in its walls
c4	corridor	96	missing	as drawn	2.5 x 31.5 m in its walls
c7	corridor	45	missing	as drawn	14.8 x 2.5 m in its walls
c8	corridor	14	missing	follows	its ground is layout ap
c9	corridor	11	missing	follows	its ground is layout ak
c10	corridor	11	missing	follows	its ground is layout al
c11	corridor	11	missing	follows	its ground is layout am
c12	corridor	11	missing	follows	its ground is layout an
c13	corridor	11	missing	follows	its ground is layout ao
+4	The second-floor corridor by Myrtle's do	96	built	built	as second-floor-east-corridor
b	The North Tower's stair foot, a stair be	41	built	built	as north-stair-foot-2
a	The West Tower's stair foot, a stair bet	40	built	built	as west-stair-foot-2
c	The south-west tower's stair foot, a sta	35	built	built	as sw-stair-foot-2
+5	The Defence office, its corridor's suit	20	built	built	as defence-office
c2	corridor	184	built	built	as lake-corridor-2-east
c3	corridor	156	built	built	as second-floor-corridor
c5	corridor	86	partly 65%	built	as unused-classroom-2-west, classroom-store-2-west
c6	corridor	58	built otherwise	built	as unused-classroom-2-east, defence-sitting-room, d

Third floor (3): 28 as drawn, 19 trimmed, 11 built, 2 reimagine, 7 follows; 11 true voids, 25 thick walls

Code	Layout room	m2	Now	Disposition	Note
aa	Charms classroom for the N.E.W.T. years	160	missing	reimagine	a smaller room, 23 of 160 m2: 11.5 x 2.0 m left by
aq	A passage to the rooms behind	14	partly 31%	reimagine	a thick wall, 0.6 x 4.7 m left by stone-bay
25	Charms classroom: near the forbidden cor	432	partly 31%	trimmed	16.4 x 10.2 m (167 m2), round charms-passage, charm
x	The Charms store: cushions, teacups and	160	missing	trimmed	7.4 x 12.2 m (90 m2), round walls
af	A teacher's study	132	missing	trimmed	12.2 x 4.0 m (49 m2), round walls
w	A store	127	partly 24%	trimmed	22.8 x 3.7 m (84 m2), round tapestry-passage-3-east
v	A lamp and candle cupboard	126	partly 28%	trimmed	22.7 x 3.4 m (77 m2), round tapestry-passage-3-west
n	A linen cupboard	84	partly 30%	trimmed	14.5 x 3.4 m (49 m2), round tapestry-passage-3
j	A broom cupboard	81	partly 23%	trimmed	14.6 x 3.7 m (54 m2), round tapestry-passage-3-east
ae	A store of spare desks and chairs	65	partly 27%	trimmed	11.2 x 3.4 m (38 m2), round tapestry-passage-3-west
o	Filch's cleaning cupboard	52	missing	trimmed	2.9 x 12.4 m (36 m2), round walls
p	A house-elves' linen room	41	partly 23%	trimmed	7.1 x 3.7 m (26 m2), round tapestry-passage-3-east
l	A store of spare desks and chairs	38	partly 23%	trimmed	6.6 x 3.7 m (24 m2), round tapestry-passage-3-east

The disposition of the agreed layout's rooms, by floor (model v229, layout v71), sheet 3 of 5

Wall rule applied: inner walls 0.5, outer walls outward. Now: the room's state in the model today. Disposition: built; as drawn; trimmed round a kept room; follows a room the model holds elsewhere; reimagine (cannot be built as the layout drew it).

e	Washrooms, girls' and boys'	35	partly 28%	trimmed	4.3 x 4.0 m (17 m2), round stone-bay
ap	A passage to the rooms behind	12	partly 24%	trimmed	1.5 x 3.9 m (6 m2), round tapestry-passage-3-east
k	A service passage	11	partly 31%	trimmed	1.2 x 3.7 m (4 m2), round tapestry-passage-3-east,
am	A passage to the rooms behind	11	partly 27%	trimmed	1.6 x 3.4 m (5 m2), round tapestry-passage-3-west
an	A passage to the rooms behind	11	partly 23%	trimmed	1.6 x 3.7 m (6 m2), round tapestry-passage-3-east
ao	A passage to the rooms behind	11	partly 23%	trimmed	1.6 x 3.7 m (6 m2), round tapestry-passage-3-east
c5	corridor	96	missing	trimmed	2.5 x 4.0 m (10 m2), round walls
c13	corridor	15	missing	trimmed	3.9 x 2.5 m (10 m2), round walls
23	The forbidden corridor: "the third-floor	448	missing	as drawn	16.0 x 27.5 m in its walls
i	Staff bedrooms	279	missing	as drawn	18.9 x 14.2 m in its walls
u	The armour gallery's repair room	207	missing	as drawn	13.9 x 14.2 m in its walls
ab	The trophy room's polishing room	207	missing	as drawn	13.9 x 13.9 m in its walls
s	The swivelling staircase	203	missing	as drawn	15.1 x 12.8 m in its walls
h	A third years' study room	174	missing	as drawn	11.6 x 14.2 m in its walls
y	A disused classroom	174	missing	as drawn	11.6 x 14.2 m in its walls
ac	A teacher's study	174	missing	as drawn	11.6 x 13.9 m in its walls
m	Staff bedroom	174	missing	as drawn	11.6 x 14.2 m in its walls
r	A study room	174	missing	as drawn	11.6 x 14.2 m in its walls
z	The Defence practice room, for jinxes an	169	missing	as drawn	12.5 x 12.8 m in its walls
ah	The room beside the trophy room	169	missing	as drawn	12.5 x 12.8 m in its walls
q	The Defence teacher's bedroom	160	missing	as drawn	11.8 x 12.8 m in its walls
t	A teacher's study	160	missing	as drawn	11.8 x 12.5 m in its walls
g	A Gryffindor storeroom at the tower's fo	85	missing	as drawn	12.3 x 6.4 m in its walls
al	A house-elves' linen room	75	missing	as drawn	6.2 x 11.0 m in its walls
f	The Astronomy Tower's stair foot, its st	60	missing	as drawn	5.5 x 9.5 m in its walls
c	Washrooms, girls' and boys'	42	missing	as drawn	6.8 x 5.5 m in its walls
d	Washrooms, girls' and boys'	35	missing	as drawn	7.5 x 3.9 m in its walls
aj	A linen cupboard	30	missing	as drawn	5.2 x 4.9 m in its walls
ak	Filch's cleaning cupboard	27	missing	as drawn	4.8 x 4.9 m in its walls
ad	A broom cupboard	26	missing	as drawn	4.3 x 4.9 m in its walls
26	The one-eyed witch's landing, directly b	24	missing	as drawn	7.5 x 2.5 m in its walls
c6	corridor	86	missing	as drawn	28.3 x 2.5 m in its walls
c7	corridor	65	missing	as drawn	21.1 x 2.5 m in its walls
c8	corridor	58	missing	as drawn	18.9 x 2.5 m in its walls
c11	corridor	18	missing	as drawn	2.5 x 5.5 m in its walls
c12	corridor	15	missing	as drawn	4.8 x 2.5 m in its walls
ai	A study room	132	missing	follows	its ground is layout 23
ag	Staff bedroom	132	missing	follows	its ground is layout 23
c14	corridor	14	partly 31%	follows	its ground is now stone-bay and their walls
c15	corridor	12	partly 24%	follows	it lies in the walls of tapestry-passage-3-east
c16	corridor	11	partly 27%	follows	it lies in the walls of tapestry-passage-3-west
c17	corridor	11	partly 23%	follows	it lies in the walls of tapestry-passage-3-east
c18	corridor	11	partly 23%	follows	it lies in the walls of tapestry-passage-3-east
22	Defence Against the Dark Arts classroom:	360	partly 56%	built	as defence-classroom, defence-store, third-floor-no
24	Trophy room, third floor (the spot propo	320	built	built	as trophy-room
+17	The long gallery of armour, by the troph	156	built	built	as armour-gallery
a	The North Tower's stair foot, a stair be	41	built	built	as north-stair-foot-3
b	The south-west tower's stair foot, a sta	35	built	built	as sw-stair-foot-3
c1	corridor	184	built	built	as lake-corridor-3-east
c2	corridor	165	built	built	as charms-corridor
c3	corridor	156	built	built	as third-floor-north-corridor
c4	corridor	126	built otherwise	built	as tapestry-passage-3-east, tapestry-passage-3-west
c9	corridor	37	built	built	as charms-passage
c10	corridor	30	built	built	as defence-passage

Fourth floor (4): 11 built, 35 as drawn, 11 trimmed, 5 follows; 13 true voids, 14 thick walls

Code	Layout room	m2	Now	Disposition	Note
s	Filch's cleaning cupboard	128	partly 23%	trimmed	23.3 x 3.7 m (86 m2), round elves-passage-4
29	The unused classroom with the Mirror of	120	partly 24%	trimmed	11.6 x 5.3 m (61 m2), round elves-passage-4, forgot
k	A broom cupboard	86	partly 24%	trimmed	3.0 x 3.7 m (11 m2), round elves-passage-4
n	A linen cupboard	48	partly 23%	trimmed	8.4 x 3.7 m (31 m2), round elves-passage-4
l	A store of spare desks and chairs	38	partly 23%	trimmed	6.6 x 3.7 m (24 m2), round elves-passage-4
aj	A store of spare desks and chairs	30	partly 23%	trimmed	5.2 x 3.7 m (19 m2), round north-stair-foot-4
z	A lamp and candle cupboard	18	partly 23%	trimmed	3.0 x 3.7 m (11 m2), round elves-passage-4
ap	A passage to the rooms behind	14	partly 23%	trimmed	2.0 x 3.7 m (7 m2), round north-stair-foot-4
am	A passage to the rooms behind	11	partly 23%	trimmed	1.6 x 3.7 m (6 m2), round elves-passage-4
an	A passage to the rooms behind	11	partly 23%	trimmed	1.6 x 3.7 m (6 m2), round elves-passage-4
ao	A passage to the rooms behind	11	partly 23%	trimmed	1.5 x 3.7 m (6 m2), round elves-passage-4
j	The newspaper room: back issues of the P	279	missing	as drawn	18.9 x 14.2 m in its walls
r	A house-elves' linen room	207	missing	as drawn	13.9 x 14.2 m in its walls
x	Staff bedroom	207	missing	as drawn	13.9 x 13.9 m in its walls
i	The landscape painting's corridor	174	missing	as drawn	11.6 x 14.2 m in its walls
u	A disused classroom	174	missing	as drawn	11.6 x 14.2 m in its walls
y	A study room	174	missing	as drawn	11.6 x 13.9 m in its walls
m	Revision rooms for the exam years	174	missing	as drawn	11.6 x 14.2 m in its walls
p	The Muggle Studies collection: plugs and	174	missing	as drawn	11.6 x 14.2 m in its walls
o	The Herbology library: books that bite	168	missing	as drawn	12.4 x 12.8 m in its walls
t	Staff bedroom	168	missing	as drawn	12.4 x 12.5 m in its walls
ah	A study room	168	missing	as drawn	12.4 x 12.8 m in its walls
q	Staff bedrooms	168	missing	as drawn	12.4 x 12.5 m in its walls
w	A teacher's study	168	missing	as drawn	12.4 x 12.5 m in its walls
ag	A disused classroom	132	missing	as drawn	12.2 x 10.2 m in its walls
af	The Ancient Runes store of tablets and s	132	missing	as drawn	11.9 x 10.2 m in its walls
ac	A house-elves' linen room	132	missing	as drawn	12.2 x 10.2 m in its walls
ae	Staff bedroom	132	missing	as drawn	12.2 x 10.2 m in its walls
ab	The Ancient Runes teacher's study	132	missing	as drawn	11.9 x 10.2 m in its walls
ad	The fourth-floor toilet	132	missing	as drawn	11.9 x 10.2 m in its walls
h	A Gryffindor storeroom at the tower's fo	85	missing	as drawn	12.3 x 6.4 m in its walls
ak	A teacher's study	75	missing	as drawn	6.2 x 11.0 m in its walls
v	A store of old textbooks	63	missing	as drawn	11.1 x 4.9 m in its walls
aa	A store	62	missing	as drawn	11.0 x 4.9 m in its walls
g	The Astronomy Tower's stair foot, its st	60	missing	as drawn	5.5 x 9.5 m in its walls
d	Washrooms, girls' and boys'	42	missing	as drawn	6.8 x 5.5 m in its walls
e	Washrooms, girls' and boys'	35	missing	as drawn	7.5 x 3.9 m in its walls
f	Washrooms, girls' and boys'	35	missing	as drawn	7.5 x 3.9 m in its walls
ai	A broom cupboard	32	missing	as drawn	5.8 x 4.9 m in its walls
al	A passage to the rooms behind	11	missing	as drawn	1.5 x 4.9 m in its walls
c1	corridor	267	missing	as drawn	88.8 x 2.5 m in its walls
c4	corridor	96	missing	as drawn	2.5 x 31.5 m in its walls
c5	corridor	96	missing	as drawn	2.5 x 31.5 m in its walls
c6	corridor	86	missing	as drawn	28.3 x 2.5 m in its walls
c8	corridor	58	missing	as drawn	18.9 x 2.5 m in its walls
c10	corridor	48	missing	as drawn	15.8 x 2.5 m in its walls
c12	corridor	14	partly 23%	follows	it lies in the walls of north-stair-foot-4
c13	corridor	11	missing	follows	its ground is layout al
c14	corridor	11	partly 23%	follows	it lies in the walls of elves-passage-4
c15	corridor	11	partly 23%	follows	it lies in the walls of elves-passage-4
c16	corridor	11	partly 23%	follows	it lies in the walls of elves-passage-4
27	Library, the Restricted Section at the b	936	partly 78%	built	as library, fourth-floor-corridor, ancient-runes-cl
28	The Muggle Studies room, past the last s	48	partly 68%	built	as library-corridor, back-stair-lobby-4, forgotten-
b	The North Tower's stair foot, a stair be	41	built	built	as north-stair-foot-4
a	The West Tower's stair foot, a stair bet	40	built	built	as west-stair-foot-4
c	The south-west tower's stair foot, a sta	35	built	built	as sw-stair-foot-4
c2	corridor	184	built	built	as lake-corridor-4-east
c3	corridor	156	built	built	as fourth-floor-corridor
c7	corridor	84	built	built	as elves-passage-4
c9	corridor	54	built	built	as library-corridor, back-stair-lobby-4
c11	corridor	36	built	built	as electives-passage-4
c17	corridor	5	built	built	as sw-turret-passage

The disposition of the agreed layout's rooms, by floor (model v229, layout v71), sheet 4 of 5

Wall rule applied: inner walls 0.5, outer walls outward. Now: the room's state in the model today. Disposition: built; as drawn; trimmed round a kept room; follows a room the model holds elsewhere; reimagine (cannot be built as the layout drew it).

Fifth floor (5): 35 as drawn, 13 trimmed, 7 built, 7 follows; 12 true voids, 13 thick walls

Code	Layout room	m2	Now	Disposition	Note
v	The girls' dormitories' linen store	207	partly 20%	trimmed	9.9 x 13.8 m (137 m2), round drum-bend-5-west, true
w	A store	128	partly 23%	trimmed	23.3 x 3.7 m (86 m2), round elves-passage-5
k	A broom cupboard	81	partly 23%	trimmed	14.6 x 3.7 m (54 m2), round elves-passage-5
q	A store of old textbooks	48	partly 23%	trimmed	8.4 x 3.7 m (31 m2), round elves-passage-5
n	A store of spare desks and chairs	38	partly 23%	trimmed	6.6 x 3.7 m (24 m2), round elves-passage-5
ak	Filch's cleaning cupboard	30	partly 23%	trimmed	5.2 x 3.7 m (19 m2), round north-stair-foot-5
ae	A store of spare desks and chairs	18	partly 23%	trimmed	3.0 x 3.7 m (11 m2), round elves-passage-5
at	A passage to the rooms behind	14	partly 23%	trimmed	2.0 x 3.7 m (7 m2), round north-stair-foot-5
l	A service passage	11	partly 31%	trimmed	1.2 x 3.7 m (4 m2), round elves-passage-5, back-sta
ap	A passage to the rooms behind	11	partly 23%	trimmed	1.6 x 3.7 m (6 m2), round elves-passage-5
aq	A passage to the rooms behind	11	partly 23%	trimmed	1.6 x 3.7 m (6 m2), round elves-passage-5
ar	A passage to the rooms behind	11	partly 23%	trimmed	1.6 x 3.7 m (6 m2), round elves-passage-5
as	A passage to the rooms behind	11	partly 23%	trimmed	1.5 x 3.7 m (6 m2), round elves-passage-5
32	The east wing, named on the fifth floor	512	missing	as drawn	16.0 x 31.5 m in its walls
j	The Head Boy and Head Girl's study	279	missing	as drawn	18.9 x 14.2 m in its walls
31	Prefects' bathroom, by Boris the Bewilde	224	missing	as drawn	15.8 x 13.5 m in its walls
ab	Staff bedroom	207	missing	as drawn	13.9 x 13.9 m in its walls
s	The music room	177	missing	as drawn	11.8 x 14.2 m in its walls
ad	A disused classroom	177	missing	as drawn	11.8 x 13.9 m in its walls
i	The fifth-floor corridor of armour, to a	177	missing	as drawn	11.8 x 14.2 m in its walls
m	The O.W.L. examiners' rooms	177	missing	as drawn	11.8 x 14.2 m in its walls
x	Staff bedrooms	177	missing	as drawn	11.8 x 14.2 m in its walls
r	Professor Sinistra's star-chart room	168	missing	as drawn	12.4 x 12.8 m in its walls
y	Staff bedroom	168	missing	as drawn	12.4 x 12.8 m in its walls
ai	A teacher's study	168	missing	as drawn	12.4 x 12.8 m in its walls
t	The ledgers of house points	168	missing	as drawn	12.4 x 12.5 m in its walls
z	A study room	168	missing	as drawn	12.4 x 12.8 m in its walls
aa	A teacher's study	162	missing	as drawn	12.0 x 12.8 m in its walls
ah	A disused classroom	162	missing	as drawn	12.0 x 12.8 m in its walls
ag	A teacher's study	124	missing	as drawn	11.9 x 9.5 m in its walls
ac	A house-elves' linen room	119	missing	as drawn	21.5 x 4.9 m in its walls
al	A teacher's study	100	missing	as drawn	9.5 x 9.5 m in its walls
af	The prefects' common room	99	missing	as drawn	11.9 x 7.5 m in its walls
h	A Gryffindor storeroom at the tower's fo	85	missing	as drawn	12.3 x 6.4 m in its walls
o	A linen cupboard	84	missing	as drawn	15.0 x 4.9 m in its walls
u	A lamp and candle cupboard	84	missing	as drawn	15.0 x 4.9 m in its walls
am	A teacher's study	75	missing	as drawn	6.2 x 11.0 m in its walls
g	The Astronomy Tower's stair foot, its st	60	missing	as drawn	5.5 x 9.5 m in its walls
p	Filch's cleaning cupboard	52	missing	as drawn	3.5 x 12.8 m in its walls
d	Washrooms, girls' and boys'	42	missing	as drawn	6.8 x 5.5 m in its walls
aj	A linen cupboard	38	missing	as drawn	6.8 x 4.9 m in its walls
e	Washrooms, girls' and boys'	35	missing	as drawn	7.5 x 3.9 m in its walls
f	Washrooms, girls' and boys'	35	missing	as drawn	7.5 x 3.9 m in its walls
an	A passage to the rooms behind	11	missing	as drawn	1.5 x 4.9 m in its walls
ao	A passage to the rooms behind	11	missing	as drawn	1.5 x 4.9 m in its walls
c1	corridor	480	missing	as drawn	160.0 x 2.5 m in its walls
c6	corridor	30	missing	as drawn	2.5 x 9.5 m in its walls
c7	corridor	24	missing	as drawn	2.5 x 7.5 m in its walls
c8	corridor	14	partly 23%	follows	it lies in the walls of north-stair-foot-5
c9	corridor	11	missing	follows	its ground is layout an
c10	corridor	11	missing	follows	its ground is layout ao
c11	corridor	11	partly 23%	follows	it lies in the walls of elves-passage-5
c12	corridor	11	partly 23%	follows	it lies in the walls of elves-passage-5
c13	corridor	11	partly 23%	follows	it lies in the walls of elves-passage-5
c14	corridor	11	partly 23%	follows	it lies in the walls of elves-passage-5
b	The North Tower's stair foot, a stair be	41	built	built	as north-stair-foot-5
a	The West Tower's stair foot, a stair bet	40	built	built	as west-stair-foot-5
c	The south-west tower's stair foot, a sta	35	built	built	as sw-stair-foot-5
c2	corridor	184	built	built	as lake-corridor-5-east
c3	corridor	86	built	built	as lake-corridor-5-west
c4	corridor	84	built	built	as elves-passage-5
c5	corridor	58	built	built	as fifth-floor-south-corridor

Sixth floor (6): 24 trimmed, 11 built, 28 as drawn, 8 follows; 18 true voids, 15 thick walls

Code	Layout room	m2	Now	Disposition	Note
j	The clock room, where the castle's clock	279	partly 21%	trimmed	15.7 x 10.6 m (166 m2), round lake-corridor-6-turn,
ab	A study room	208	partly 42%	trimmed	8.3 x 12.4 m (103 m2), round scroll-hall
af	The Arithmancy store of number charts	130	missing	trimmed	4.9 x 13.6 m (67 m2), round sw-corner-lobby-6
x	A store	128	partly 23%	trimmed	23.3 x 3.7 m (86 m2), round elves-passage-6
w	Professor Vector's study	92	partly 30%	trimmed	5.5 x 6.1 m (34 m2), round drum-bend-6-west
k	A broom cupboard	81	partly 23%	trimmed	14.6 x 3.7 m (54 m2), round elves-passage-6
aa	A broom cupboard	78	partly 23%	trimmed	14.0 x 3.7 m (52 m2), round elves-passage-6-west
ag	A linen cupboard	78	partly 23%	trimmed	14.0 x 3.7 m (52 m2), round elves-passage-6-west
o	A house-elves' linen room	65	partly 23%	trimmed	11.6 x 3.7 m (43 m2), round elves-passage-6-west
u	A lamp and candle cupboard	65	partly 23%	trimmed	11.6 x 3.7 m (43 m2), round elves-passage-6-west
q	A store of old textbooks	48	partly 23%	trimmed	8.4 x 3.7 m (31 m2), round elves-passage-6
n	The telescope store	38	partly 23%	trimmed	6.6 x 3.7 m (24 m2), round elves-passage-6
ap	Filch's cleaning cupboard	38	partly 23%	trimmed	6.8 x 3.7 m (25 m2), round west-stair-foot-6
aq	A store of old textbooks	30	partly 23%	trimmed	5.2 x 3.7 m (19 m2), round north-stair-foot-6
ae	A store of spare desks and chairs	18	partly 23%	trimmed	3.0 x 3.7 m (11 m2), round elves-passage-6
ba	A passage to the rooms behind	14	partly 23%	trimmed	2.0 x 3.7 m (7 m2), round north-stair-foot-6
l	A service passage	11	partly 31%	trimmed	1.2 x 3.7 m (4 m2), round elves-passage-6, back-sta
at	A passage to the rooms behind	11	partly 23%	trimmed	1.6 x 3.7 m (6 m2), round west-stair-foot-6, elves-
au	A passage to the rooms behind	11	partly 23%	trimmed	1.6 x 3.7 m (6 m2), round elves-passage-6-west
av	A passage to the rooms behind	11	partly 31%	trimmed	1.3 x 3.7 m (5 m2), round elves-passage-6-west, bac
aw	A passage to the rooms behind	11	partly 23%	trimmed	1.6 x 3.7 m (6 m2), round elves-passage-6
ax	A passage to the rooms behind	11	partly 23%	trimmed	1.6 x 3.7 m (6 m2), round elves-passage-6
ay	A passage to the rooms behind	11	partly 23%	trimmed	1.6 x 3.7 m (6 m2), round elves-passage-6
az	A passage to the rooms behind	11	partly 23%	trimmed	1.5 x 3.7 m (6 m2), round elves-passage-6
al	Staff bedroom	208	missing	as drawn	15.5 x 12.8 m in its walls
s	Staff bedrooms	177	missing	as drawn	11.8 x 14.2 m in its walls
ad	A house-elves' linen room	177	missing	as drawn	11.8 x 13.9 m in its walls
i	The frog choir's practice room	177	missing	as drawn	11.8 x 14.2 m in its walls
m	Guest rooms for visiting parents	177	missing	as drawn	11.8 x 14.2 m in its walls
y	A disused classroom	177	missing	as drawn	11.8 x 14.2 m in its walls
r	A teacher's study	168	missing	as drawn	12.4 x 12.8 m in its walls
z	A teacher's study	168	missing	as drawn	12.4 x 12.8 m in its walls
ao	Staff bedroom	168	missing	as drawn	12.4 x 12.8 m in its walls
v	Staff bedroom	168	missing	as drawn	12.4 x 12.5 m in its walls
ac	A disused classroom	168	missing	as drawn	12.4 x 12.8 m in its walls
an	A house-elves' linen room	132	missing	as drawn	12.2 x 10.2 m in its walls
am	A study room	132	missing	as drawn	11.9 x 10.2 m in its walls
ai	Staff bedroom	132	missing	as drawn	12.2 x 10.2 m in its walls
ak	A teacher's study	132	missing	as drawn	12.2 x 10.2 m in its walls
ah	Arithmancy room for the N.E.W.T. years	132	missing	as drawn	11.9 x 10.2 m in its walls
aj	A disused classroom	132	missing	as drawn	11.9 x 10.2 m in its walls
ar	A teacher's study	100	missing	as drawn	9.5 x 9.5 m in its walls
h	A Gryffindor storeroom at the tower's fo	85	missing	as drawn	12.3 x 6.4 m in its walls
as	A teacher's study	75	missing	as drawn	6.2 x 11.0 m in its walls
g	The Astronomy Tower's stair foot, its st	60	missing	as drawn	5.5 x 9.5 m in its walls
p	Filch's cleaning cupboard	52	missing	as drawn	3.5 x 12.8 m in its walls
d	Washrooms, girls' and boys'	42	missing	as drawn	6.8 x 5.5 m in its walls
e	Washrooms, girls' and boys'	35	missing	as drawn	7.5 x 3.9 m in its walls
f	Washrooms, girls' and boys'	35	missing	as drawn	7.5 x 3.9 m in its walls
c1	corridor	480	missing	as drawn	160.0 x 2.5 m in its walls
c4	corridor	96	missing	as drawn	2.5 x 31.5 m in its walls
c5	corridor	96	missing	as drawn	2.5 x 31.5 m in its walls
c9	corridor	14	partly 23%	follows	it lies in the walls of north-stair-foot-6

The disposition of the agreed layout's rooms, by floor (model v229, layout v71), sheet 5 of 5

Wall rule applied: inner walls 0.5, outer walls outward. Now: the room's state in the model today. Disposition: built; as drawn; trimmed round a kept room; follows a room the model holds elsewhere; reimagine (cannot be built as the layout drew it).


c10	corridor	11	partly 23%	follows	it lies in the walls of west-stair-foot-6, elves-pa
c11	corridor	11	partly 23%	follows	it lies in the walls of elves-passage-6-west
c12	corridor	11	partly 31%	follows	it lies in the walls of elves-passage-6-west, back-
c13	corridor	11	partly 23%	follows	it lies in the walls of elves-passage-6
c14	corridor	11	partly 23%	follows	it lies in the walls of elves-passage-6
c15	corridor	11	partly 23%	follows	it lies in the walls of elves-passage-6
c16	corridor	11	partly 23%	follows	it lies in the walls of elves-passage-6
33	Arithmancy classroom (proposed); the six	252	partly 57%	built	as arithmancy-classroom, lake-corridor-6-west, arit
t	A teacher's study	208	built otherwise	built	as scroll-hall
+13	A boys' bathroom on the sixth floor, the	80	built otherwise	built	as scroll-hall
b	The North Tower's stair foot, a stair be	41	built	built	as north-stair-foot-6
a	The West Tower's stair foot, a stair bet	40	built	built	as west-stair-foot-6
c	The south-west tower's stair foot, a sta	35	built	built	as sw-stair-foot-6
c2	corridor	184	built	built	as lake-corridor-6-east
c3	corridor	144	built otherwise	built	as elves-passage-6, elves-passage-6-west
c6	corridor	86	built	built	as lake-corridor-6-west
c7	corridor	51	built	built	as lake-corridor-6-middle
c8	corridor	28	built	built	as arithmancy-passage

Seventh floor (7): 15 as drawn, 17 built, 15 trimmed, 11 reimagine, 5 follows; 15 true voids, 6 thick walls

Code	Layout room	m2	Now	Disposition	Note
n	The corridor beneath the tallest tower	168	missing	reimagine	off the building: 47% inside the walls here
u	A teacher's study	168	missing	reimagine	off the building: 0% inside the walls here
ai	A teacher's study	168	missing	reimagine	off the building: 0% inside the walls here
x	A study room	168	missing	reimagine	off the building: 0% inside the walls here
t	A store	128	partly 28%	reimagine	off the building: 0% inside the walls here
+2	Sir Cadogan's landing, at the top of the	80	partly 26%	reimagine	off the building: 0% inside the walls here
m	A store of old textbooks	48	partly 28%	reimagine	off the building: 0% inside the walls here
d	Washrooms, girls' and boys'	35	missing	reimagine	off the building: 0% inside the walls here
z	Professor Trelawney's sherry store	29	partly 27%	reimagine	off the building: 0% inside the walls here
ar	A passage to the rooms behind	11	partly 27%	reimagine	off the building: 0% inside the walls here
c16	corridor	11	partly 27%	reimagine	off the building: 0% inside the walls here
w	Staff bedroom	188	partly 28%	trimmed	9.7 x 12.4 m (120 m2), round scroll-hall
40	Room of Requirement on its own seventh-f	160	partly 40%	trimmed	15.6 x 1.3 m (20 m2), round scroll-hall, elves-pass
h	A broom cupboard	81	partly 23%	trimmed	14.6 x 3.7 m (54 m2), round elves-passage-7
v	A broom cupboard	73	partly 27%	trimmed	13.0 x 2.1 m (27 m2), round elves-passage-7-west
aa	A house-elves' linen room	73	partly 25%	trimmed	13.0 x 3.4 m (44 m2), round elves-passage-7-west
k	A linen cupboard	70	partly 27%	trimmed	12.6 x 3.4 m (43 m2), round elves-passage-7-west
p	A lamp and candle cupboard	70	partly 27%	trimmed	11.0 x 3.4 m (37 m2), round elves-passage-7-west
j	A store of spare desks and chairs	38	partly 27%	trimmed	4.9 x 3.4 m (17 m2), round elves-passage-7
aj	Filch's cleaning cupboard	38	partly 23%	trimmed	6.8 x 3.7 m (25 m2), round west-stair-foot-7
i	A service passage	11	partly 35%	trimmed	1.2 x 3.4 m (4 m2), round elves-passage-7, back-sta
al	A passage to the rooms behind	11	partly 23%	trimmed	1.6 x 3.7 m (6 m2), round west-stair-foot-7, elves-
am	A passage to the rooms behind	11	partly 27%	trimmed	1.6 x 2.1 m (3 m2), round elves-passage-7-west
an	A passage to the rooms behind	11	partly 35%	trimmed	1.3 x 3.4 m (4 m2), round elves-passage-7-west, bac
ao	A passage to the rooms behind	11	partly 25%	trimmed	1.6 x 3.4 m (5 m2), round elves-passage-7
ap	A passage to the rooms behind	11	partly 24%	trimmed	1.6 x 3.4 m (5 m2), round elves-passage-7
r	Staff bedrooms	207	missing	as drawn	13.9 x 14.2 m in its walls
y	A house-elves' linen room	207	missing	as drawn	13.9 x 13.9 m in its walls
af	A teacher's study	188	missing	as drawn	14.0 x 12.8 m in its walls
ag	A house-elves' linen room	132	missing	as drawn	11.9 x 10.2 m in its walls
ab	Staff bedroom	132	missing	as drawn	11.9 x 10.2 m in its walls
ae	A study room	132	missing	as drawn	11.9 x 10.2 m in its walls
ak	A teacher's study	100	missing	as drawn	9.5 x 9.5 m in its walls
f	The Headmaster's guest rooms	91	missing	as drawn	5.8 x 14.2 m in its walls
g	The seventh-floor broom cupboard	71	missing	as drawn	4.5 x 14.2 m in its walls
e	The Astronomy Tower's stair foot, its st	60	missing	as drawn	5.5 x 9.5 m in its walls
l	Filch's cleaning cupboard	52	missing	as drawn	3.5 x 12.8 m in its walls
c	Washrooms, girls' and boys'	42	missing	as drawn	6.8 x 5.5 m in its walls
c4	corridor	96	missing	as drawn	2.5 x 31.5 m in its walls
c6	corridor	86	missing	as drawn	28.3 x 2.5 m in its walls
c7	corridor	48	missing	as drawn	15.8 x 2.5 m in its walls
c10	corridor	11	partly 23%	follows	it lies in the walls of west-stair-foot-7, elves-pa
c11	corridor	11	partly 27%	follows	it lies in the walls of elves-passage-7-west
c12	corridor	11	partly 35%	follows	it lies in the walls of elves-passage-7-west, back-
c13	corridor	11	partly 25%	follows	it lies in the walls of elves-passage-7
c14	corridor	11	partly 24%	follows	it lies in the walls of elves-passage-7
o	Professor Sinistra's study	188	built otherwise	built	as scroll-hall
s	A disused classroom	188	built otherwise	built	as scroll-hall
q	The Astronomy warming room, cocoa after	168	built	built	as astronomy-warming-room
ac	A disused classroom	112	partly 75%	built	as old-exam-hall-store, heads-corridor, old-exam-ha
ad	A teacher's study	112	built otherwise	built	as old-exam-hall, heads-corridor
ah	Staff bedroom	87	built otherwise	built	as old-exam-hall, heads-corridor
41	Dumbledore's corridor and the lone gargo	70	built otherwise	built	as old-exam-hall, heads-corridor
a	The West Tower's stair foot, a stair bet	40	built	built	as west-stair-foot-7
b	The south-west tower's stair foot, a sta	35	built	built	as sw-stair-foot-7
aq	A passage to the rooms behind	11	built	built	as warming-room-passage
c1	corridor	234	built	built	as seventh-floor-north-corridor-east
c2	corridor	156	built	built	as room-corridor
c3	corridor	138	built otherwise	built	as elves-passage-7-west, elves-passage-7, elves-pas
c5	corridor	96	partly 51%	built	as old-exam-hall, old-exam-hall-store (51% of it; t
c8	corridor	43	built	built	as north-tower-passage
c9	corridor	12	built otherwise	built	as seventh-floor-north-corridor-east
c15	corridor	11	built	built	as warming-room-passage

Cellars and dungeons (B): the layout's rooms after the wall rule, the true voids flagged


8 built, 37 as drawn, 5 trimmed, 1 follows. Voids: V1 288 m2 (8.4 wide), V3 34 m2 (3.8 wide).

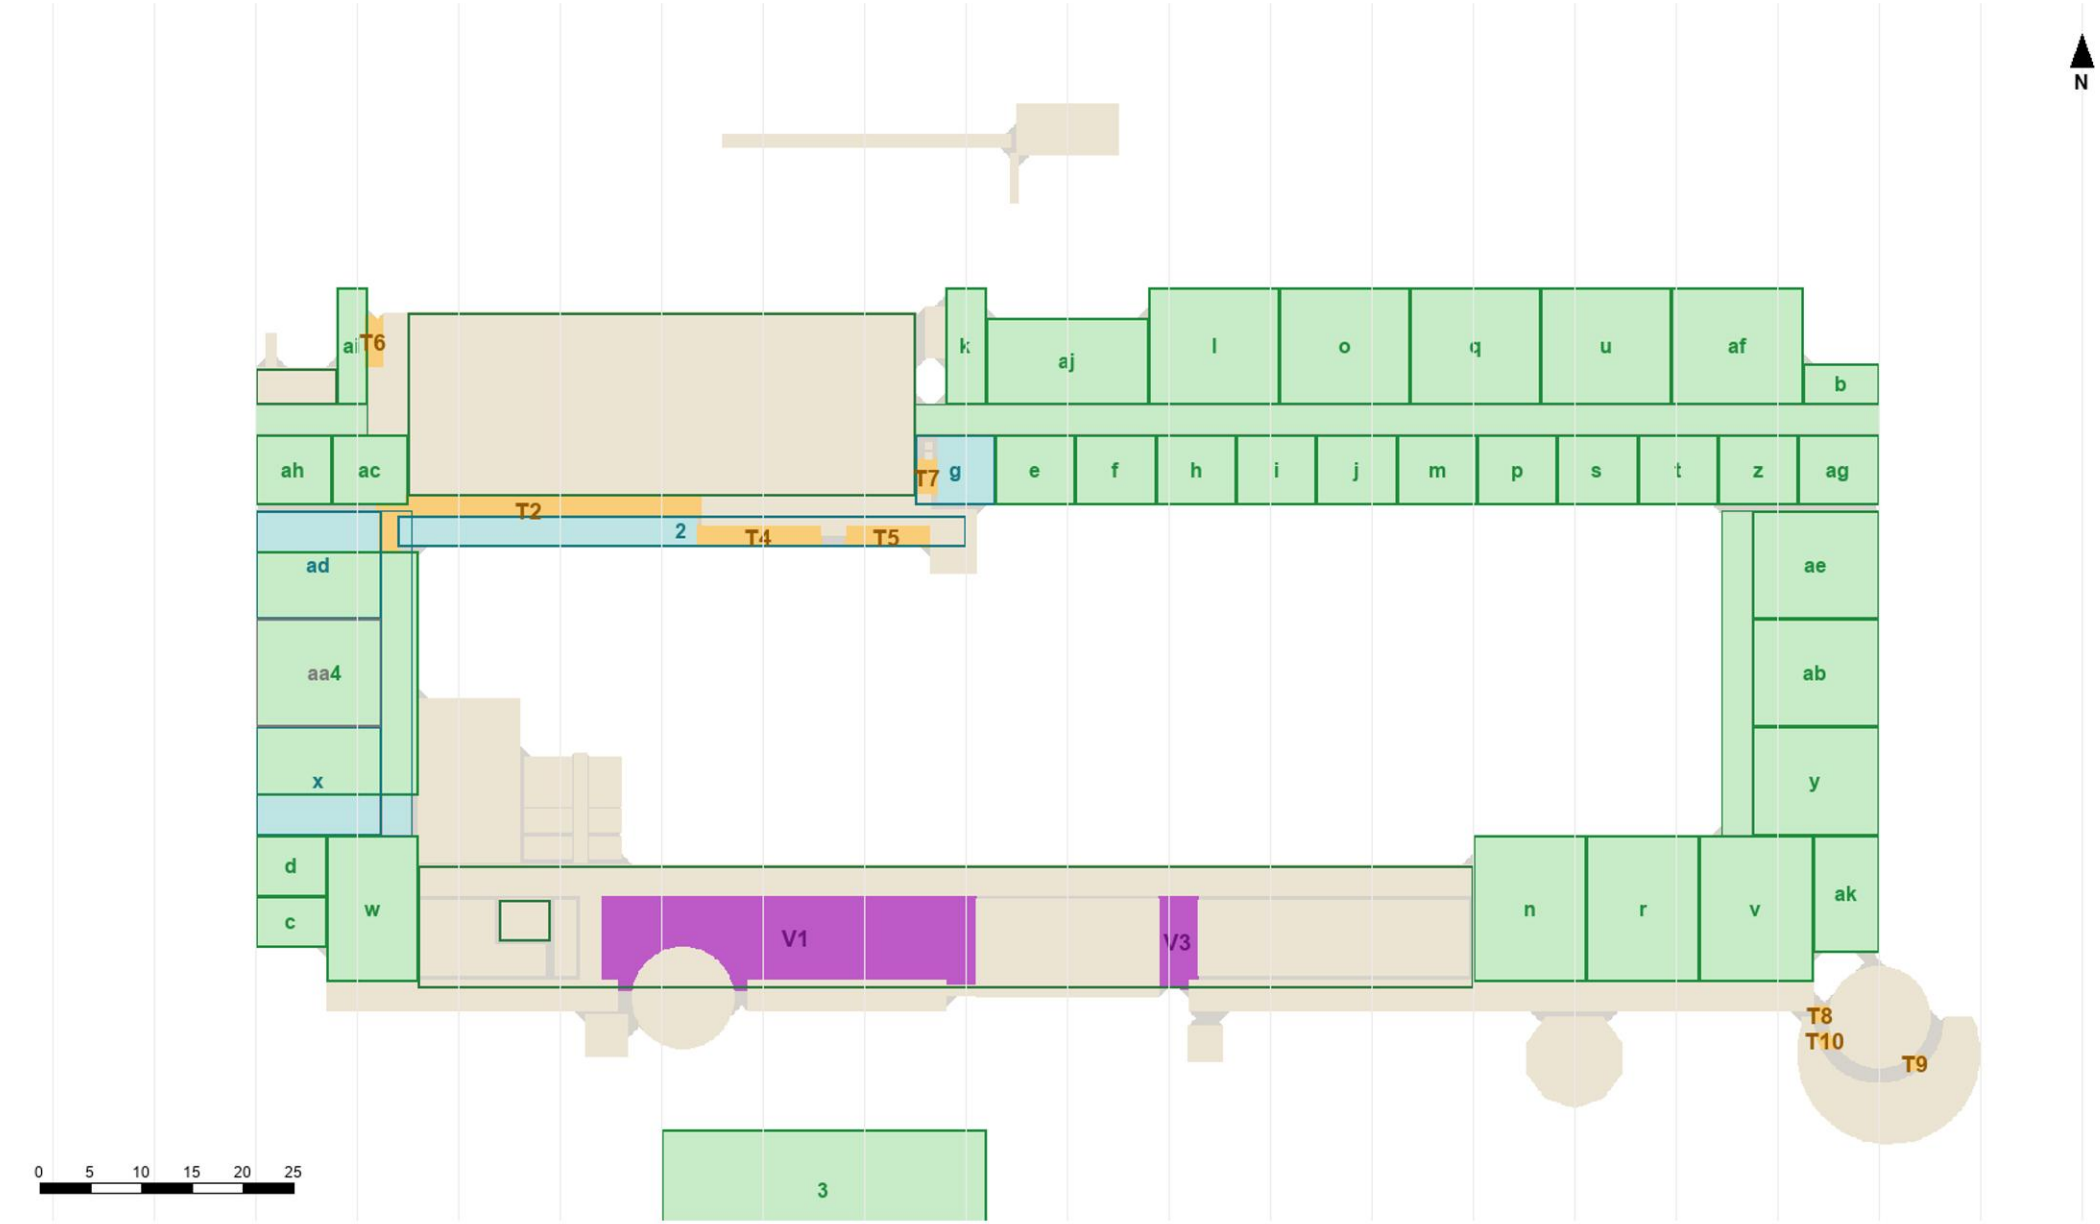

Fill: beige, built in the model; green, layout room as drawn inside its walls; teal, trimmed; pale red, what a reimagined room keeps; purple, a true void (3 m wide or more); amber, a thick wall (1.5 to 3 m). Outlines: the layout's rects; red thick, reimagine.

Ground floor (G): the layout's rooms after the wall rule, the true voids flagged


49 built, 2 follows. Voids: V1 1207 m2 (25.0 wide), V2 524 m2 (21.3 wide), V3 271 m2 (9.2 wide), V4 260 m2 (16.2 wide), V5 250 m2 (8.0 wide), V6 156 m2 (14.1 wide), V7 137 m2 (6.0 wide), V8 129 m2 (5.0 wide), V9 127 m2 (12.0 wide), V11 66 m2 (3.7 w

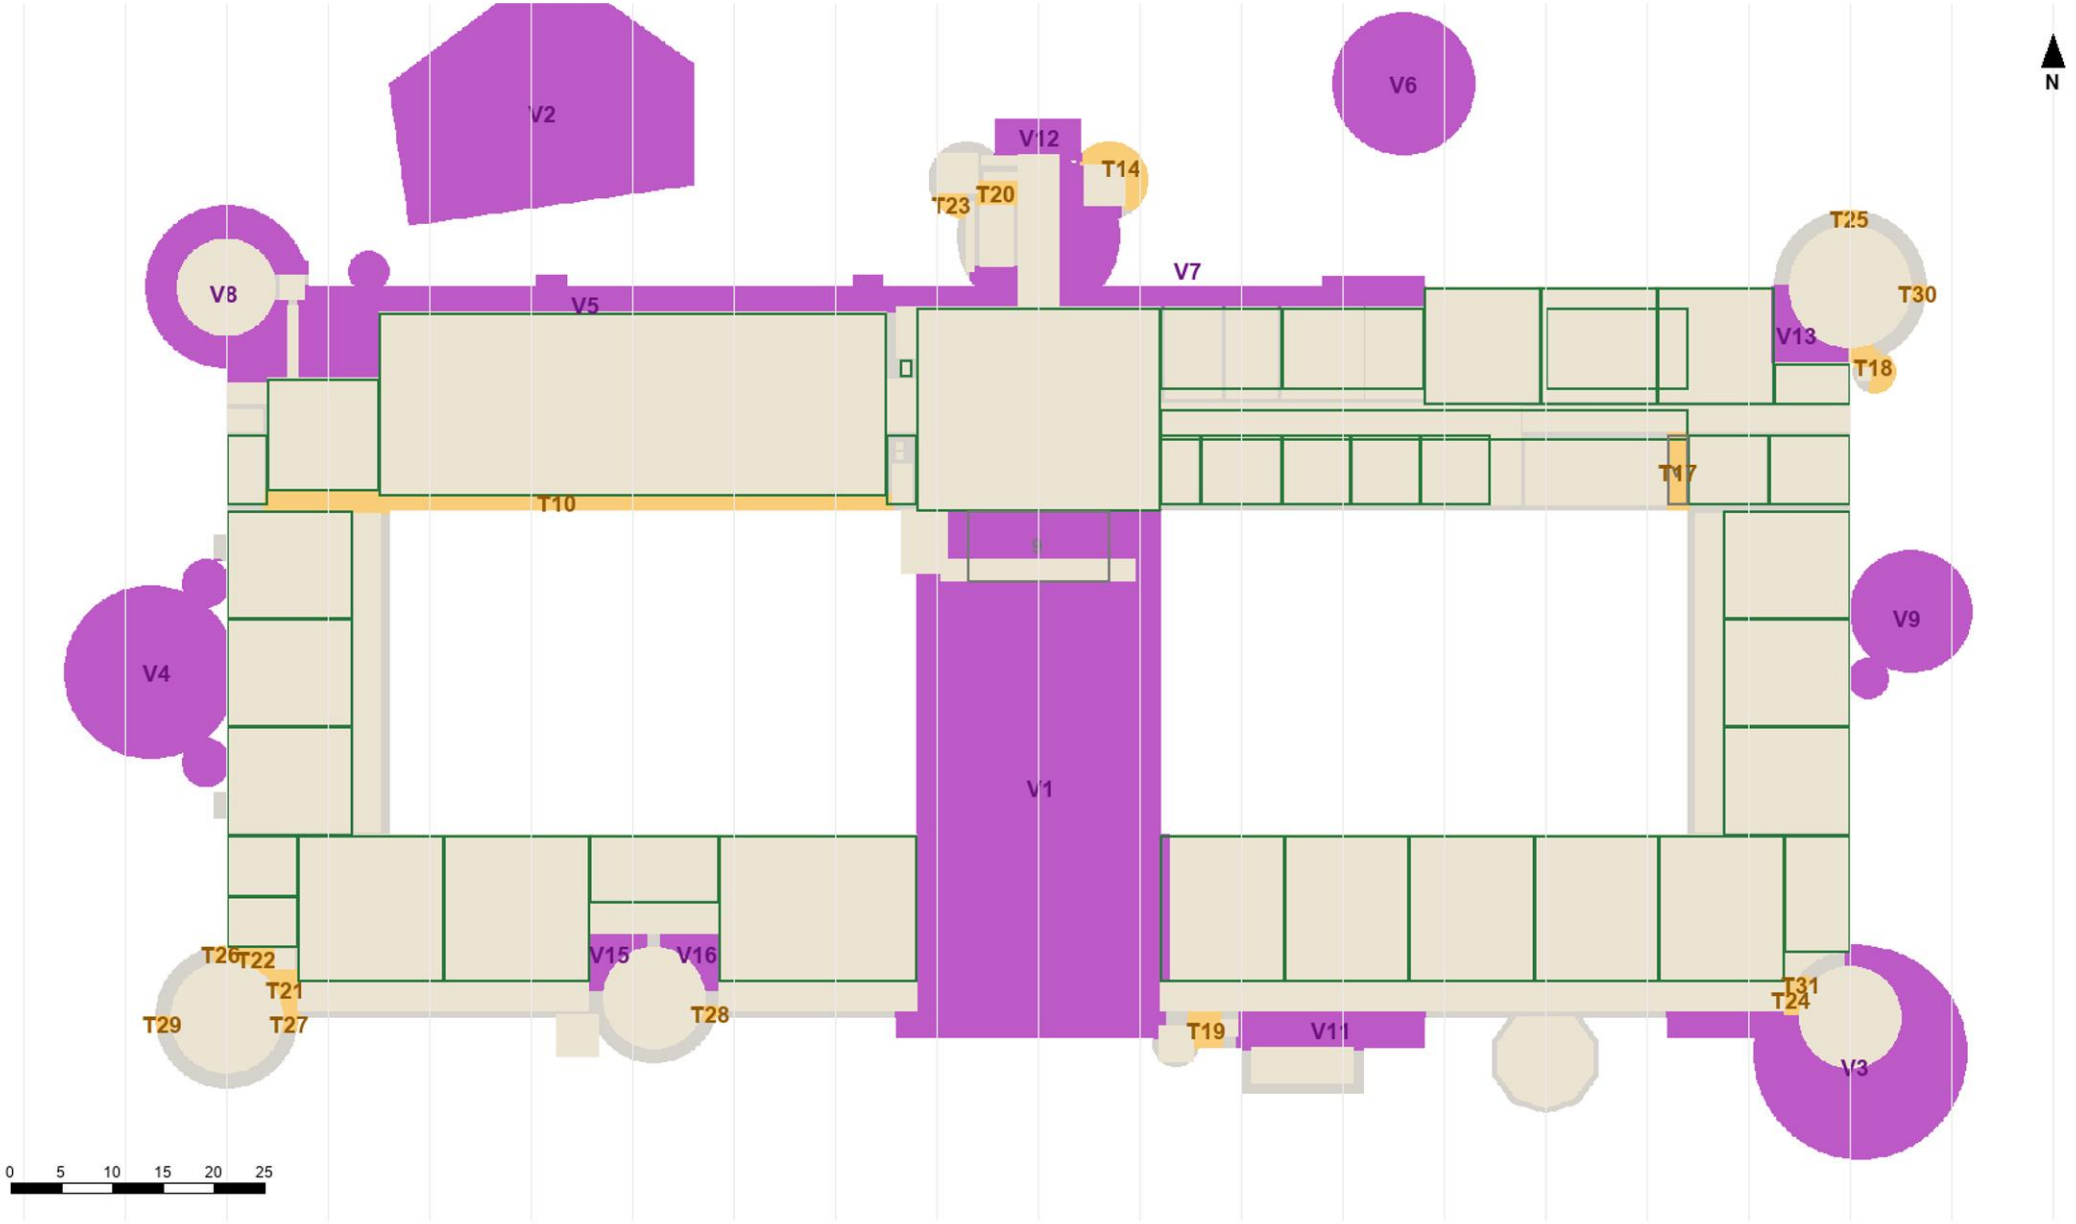

Fill: beige, built in the model; green, layout room as drawn inside its walls; teal, trimmed; pale red, what a reimagined room keeps; purple, a true void (3 m wide or more); amber, a thick wall (1.5 to 3 m). Outlines: the layout's rects; red thick, reimagine.

First floor (1): the layout's rooms after the wall rule, the true voids flagged

31 as drawn, 14 built, 1 reimagine, 3 trimmed, 4 follows. Voids: V1 260 m2 (16.2 wide), V2 194 m2 (13.4 wide), V3 131 m2 (12.1 wide), V4 121 m2 (4.2 wide), V5 83 m2 (6.7 wide), V7 76 m2 (3.7 wide), V10 55 m2 (4.6 wide), V11 54 m2 (4.0 wide), V12 49

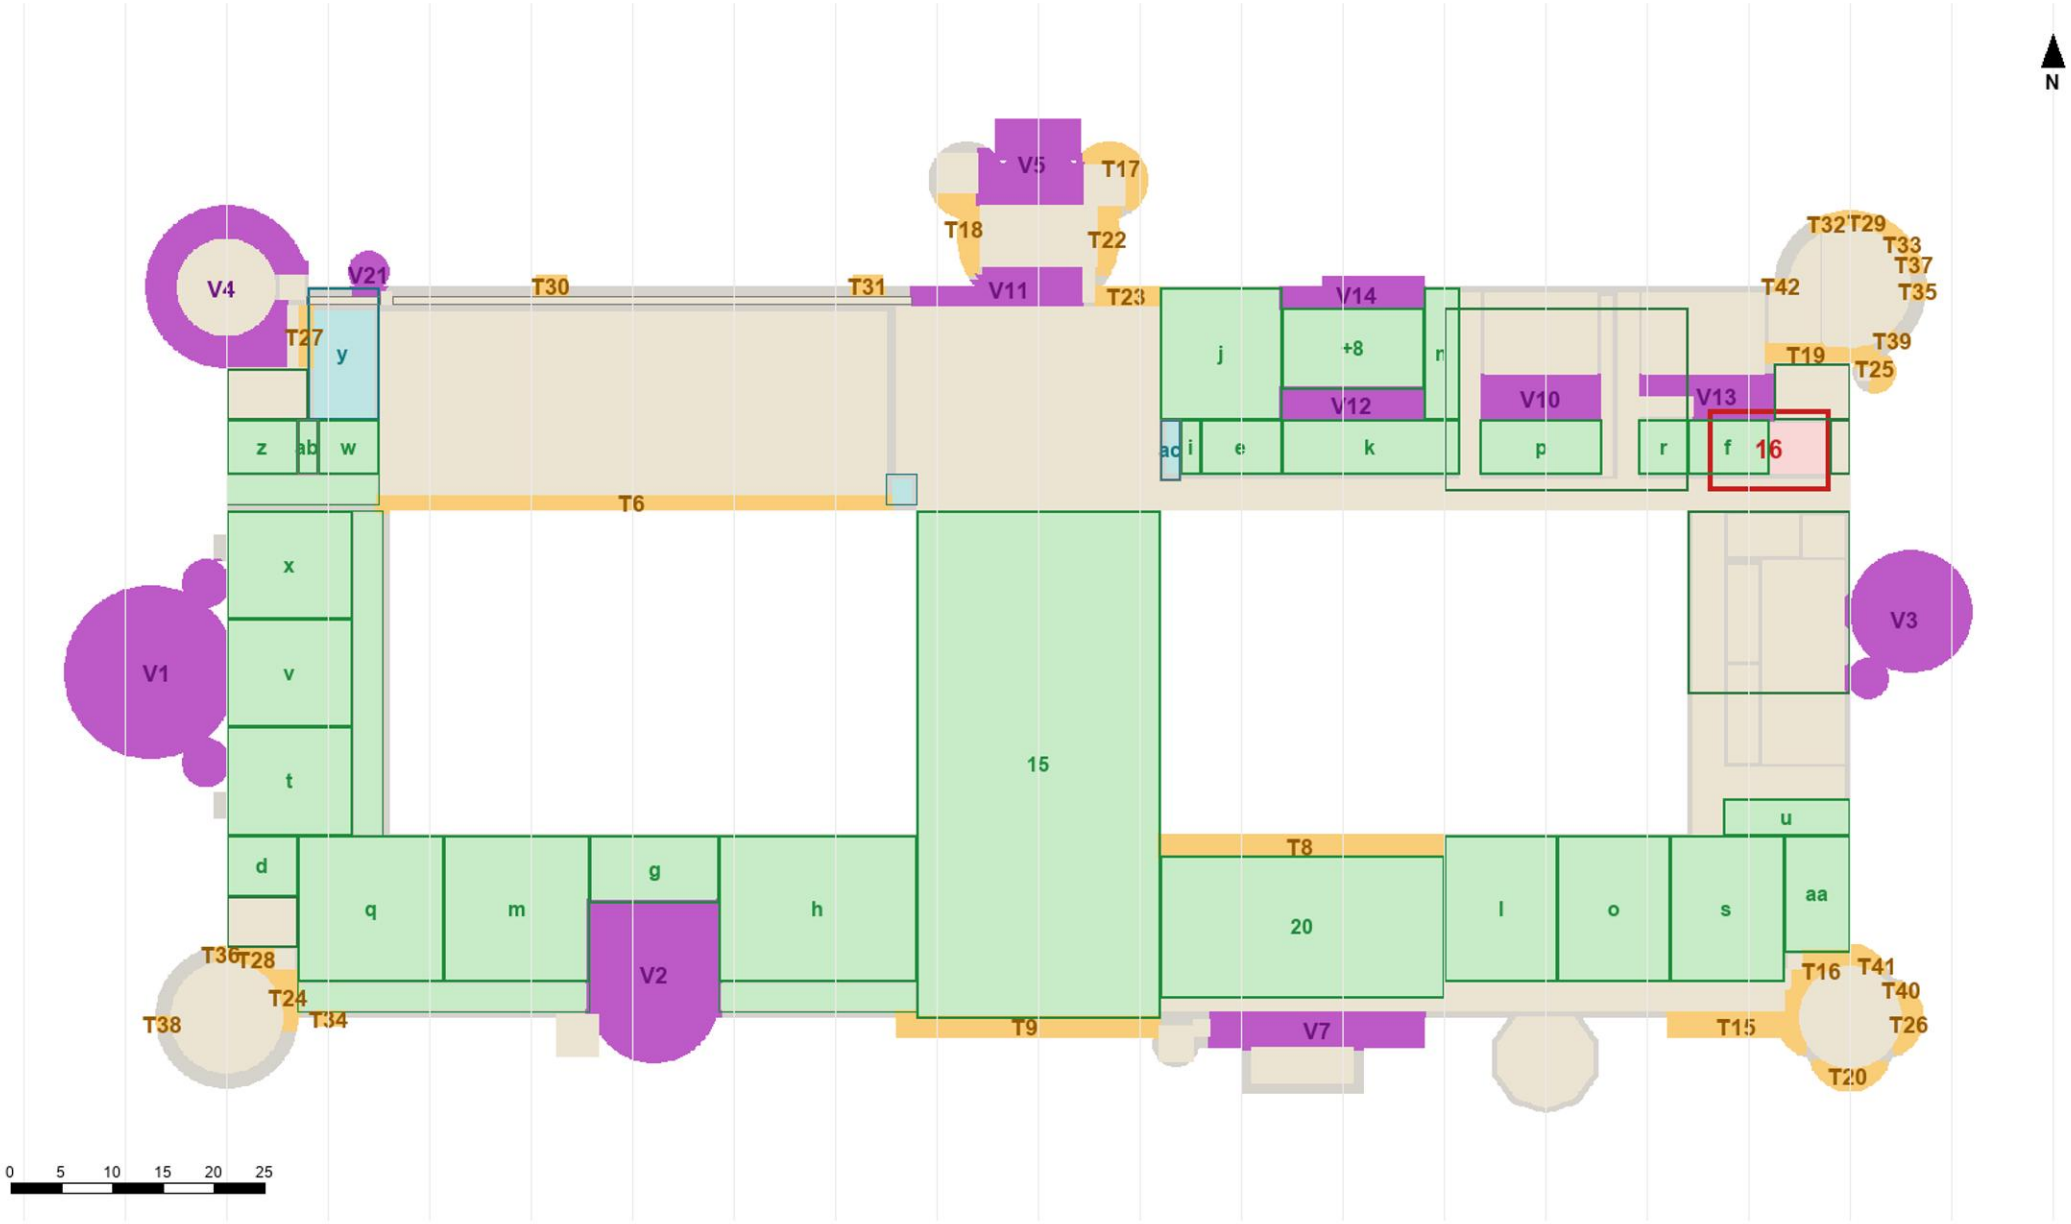


Fill: beige, built in the model; green, layout room as drawn inside its walls; teal, trimmed; pale red, what a reimagined room keeps; purple, a true void (3 m wide or more); amber, a thick wall (1.5 to 3 m). Outlines: the layout's rects; red thick, reimagine.

16 McGonagall's study, first fl: a smaller room, 26 of 96 m2: 5.4 x 4.9 m left by first-floor-corridor, north-stair-foot-1

Second floor (2): the layout's rooms after the wall rule, the true voids flagged

39 as drawn, 1 reimagine, 3 trimmed, 9 built, 6 follows. Voids: V1 1286 m2 (24.8 wide), V2 260 m2 (16.2 wide), V3 238 m2 (13.8 wide), V4 140 m2 (3.6 wide), V5 128 m2 (12.1 wide), V6 82 m2 (3.7 wide), V8 50 m2 (4.2 wide), V9 48 m2 (3.4 wide), V11 30

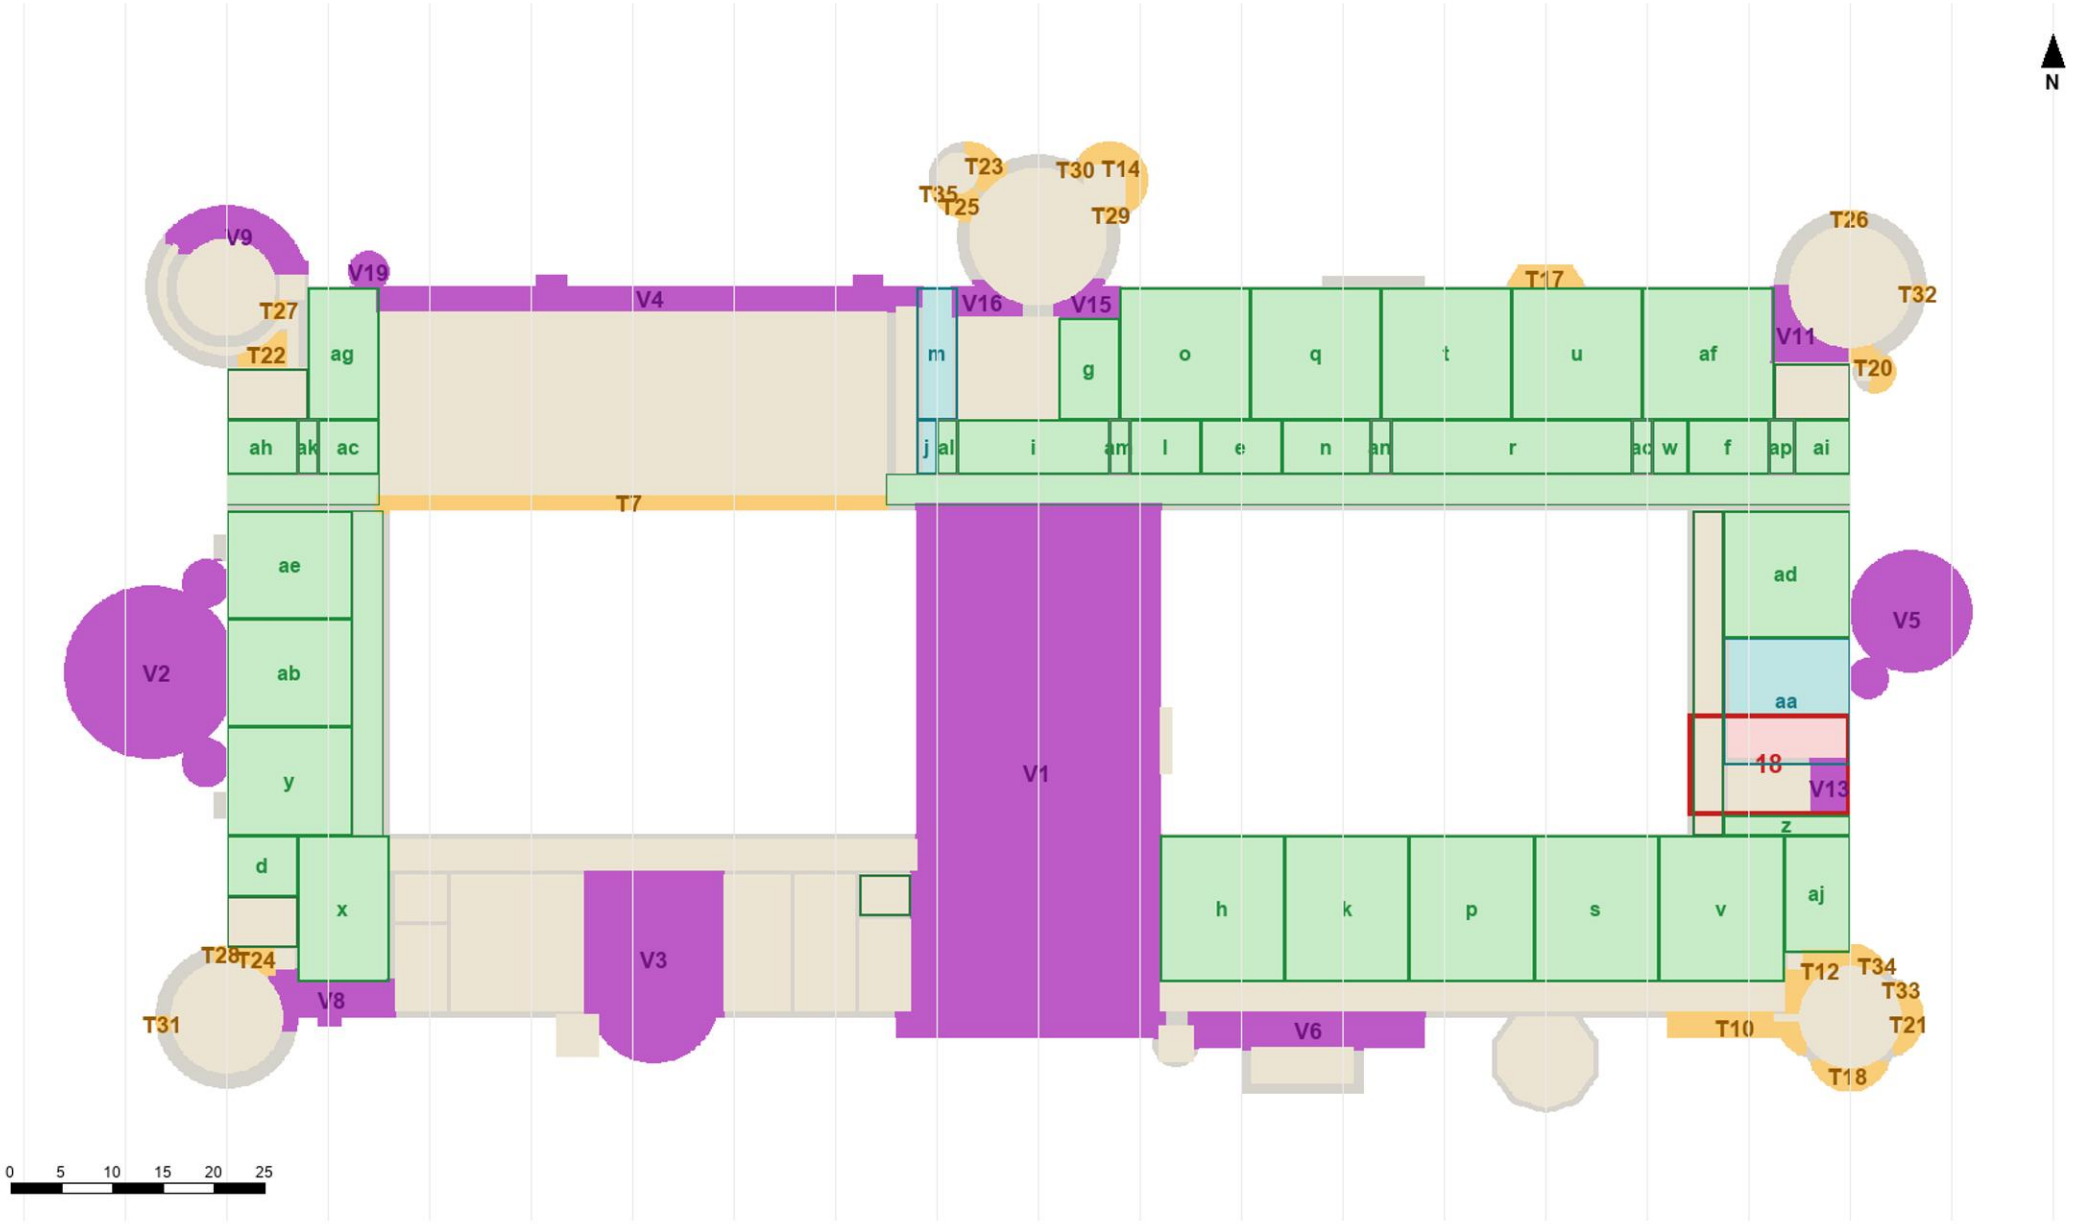


Fill: beige, built in the model; green, layout room as drawn inside its walls; teal, trimmed; pale red, what a reimagined room keeps; purple, a true void (3 m wide or more); amber, a thick wall (1.5 to 3 m). Outlines: the layout's rects; red thick, reimagine.

18 Myrtle's bathroom, the Chamb: a smaller room, 50 of 160 m2: 11.9 x 4.2 m left by myrtles-bathroom, second-floor-east-corridor

Third floor (3): the layout's rooms after the wall rule, the true voids flagged

28 as drawn, 19 trimmed, 11 built, 2 reimagine, 7 follows. Voids: V1 1255 m2 (24.4 wide), V2 256 m2 (16.0 wide), V3 194 m2 (13.4 wide), V4 128 m2 (12.1 wide), V5 113 m2 (3.8 wide), V6 82 m2 (3.7 wide), V7 41 m2 (6.0 wide), V10 22 m2 (3.0 wide), V12

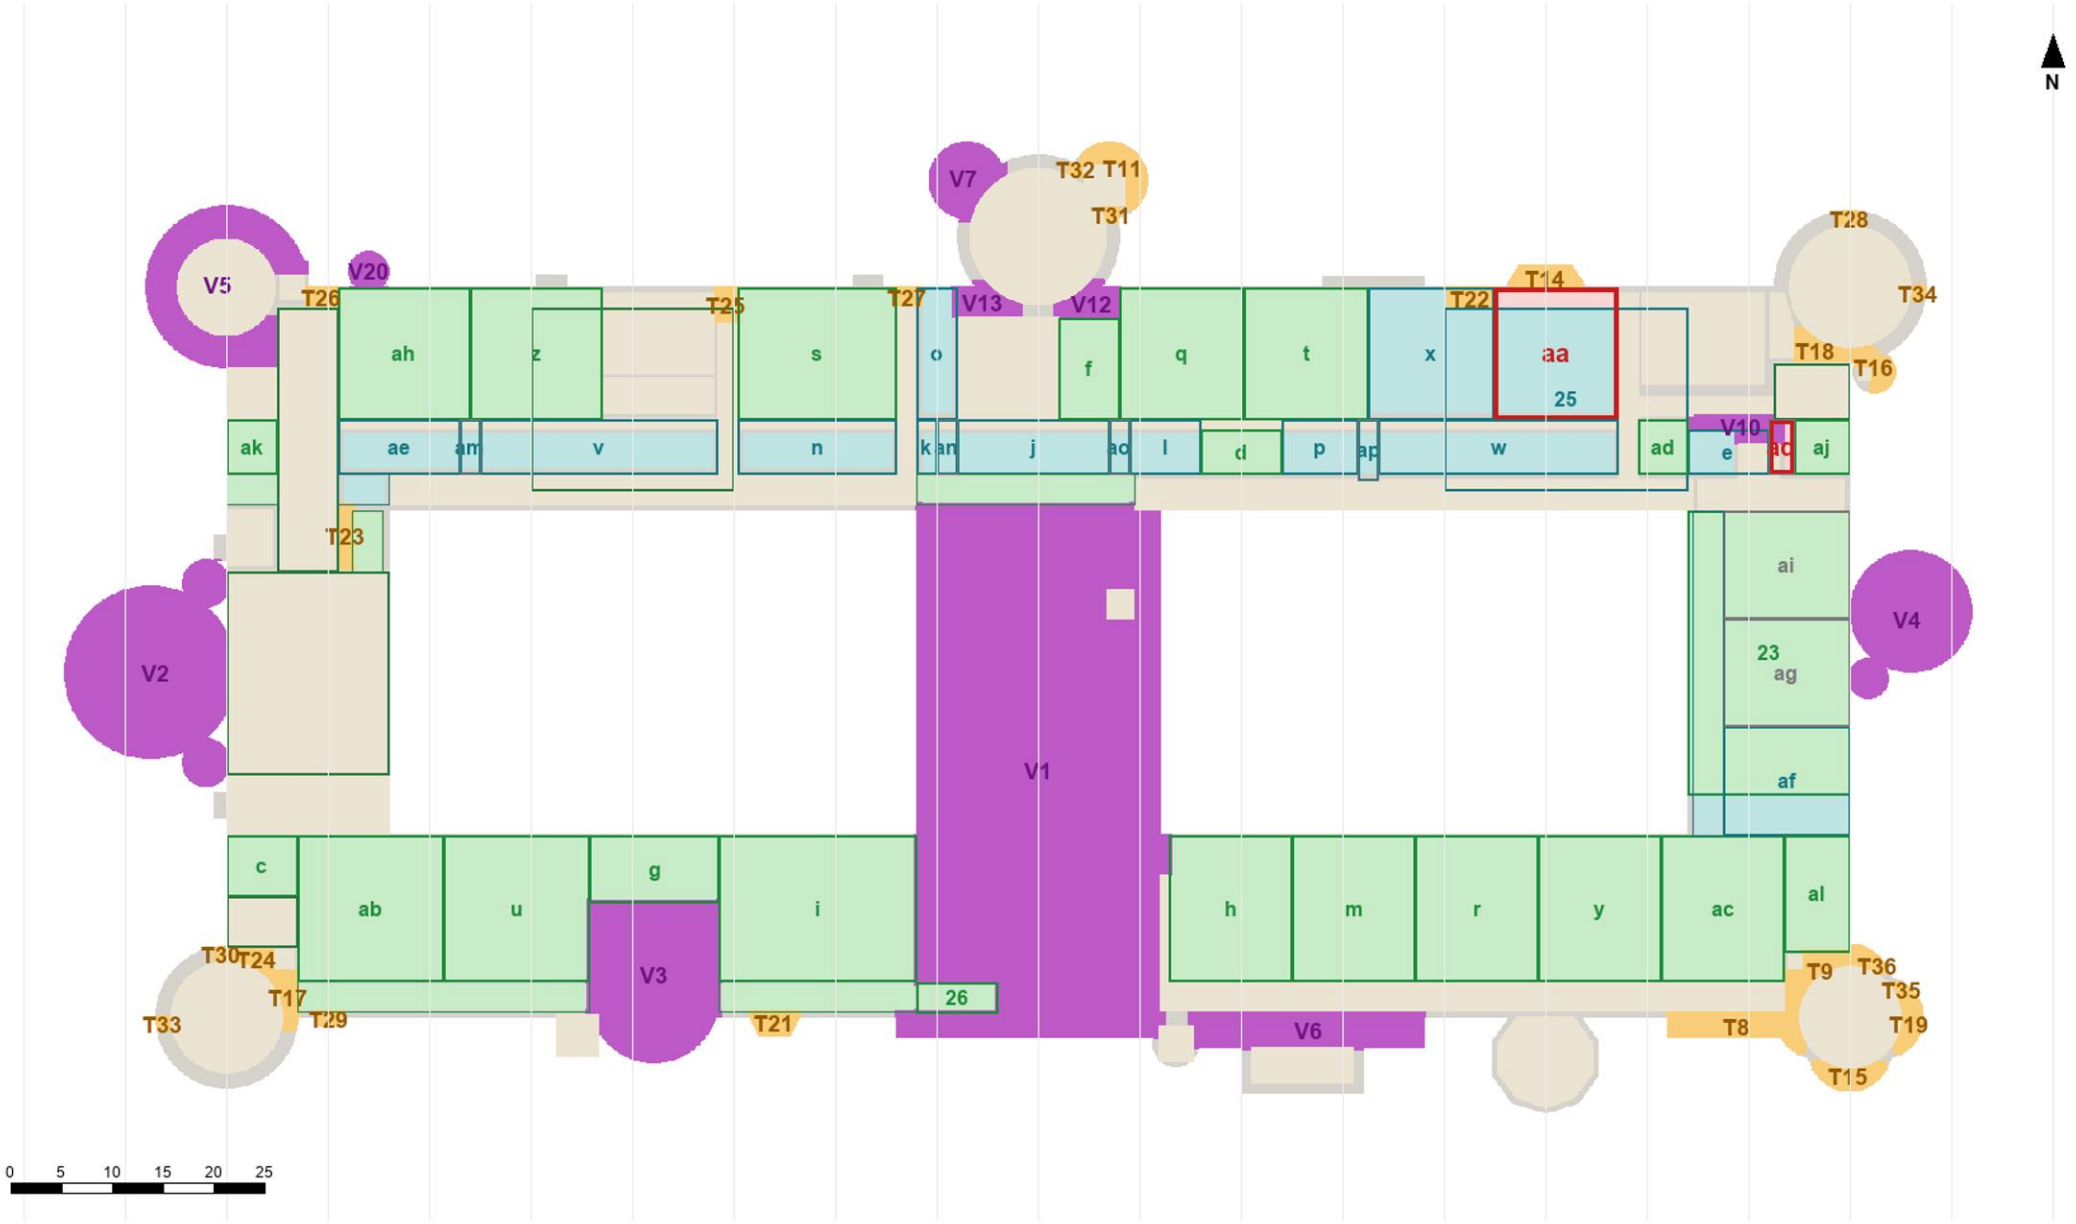


Fill: beige, built in the model; green, layout room as drawn inside its walls; teal, trimmed; pale red, what a reimagined room keeps; purple, a true void (3 m wide or more); amber, a thick wall (1.5 to 3 m). Outlines: the layout's rects; red thick, reimagine.

aa Charms classroom for the N.E: a smaller room, 23 of 160 m2: 11.5 x 2.0 m left by its neighbours

aq A passage to the rooms behin: a thick wall, 0.6 x 4.7 m left by stone-bay

Fourth floor (4): the layout's rooms after the wall rule, the true voids flagged


11 built, 35 as drawn, 11 trimmed, 5 follows. Voids: V1 1300 m2 (25.4 wide), V2 260 m2 (16.2 wide), V3 194 m2 (13.4 wide), V4 137 m2 (8.2 wide), V5 128 m2 (12.1 wide), V6 121 m2 (4.2 wide), V7 88 m2 (9.8 wide), V8 70 m2 (3.0 wide), V9 67 m2 (4.0 wi

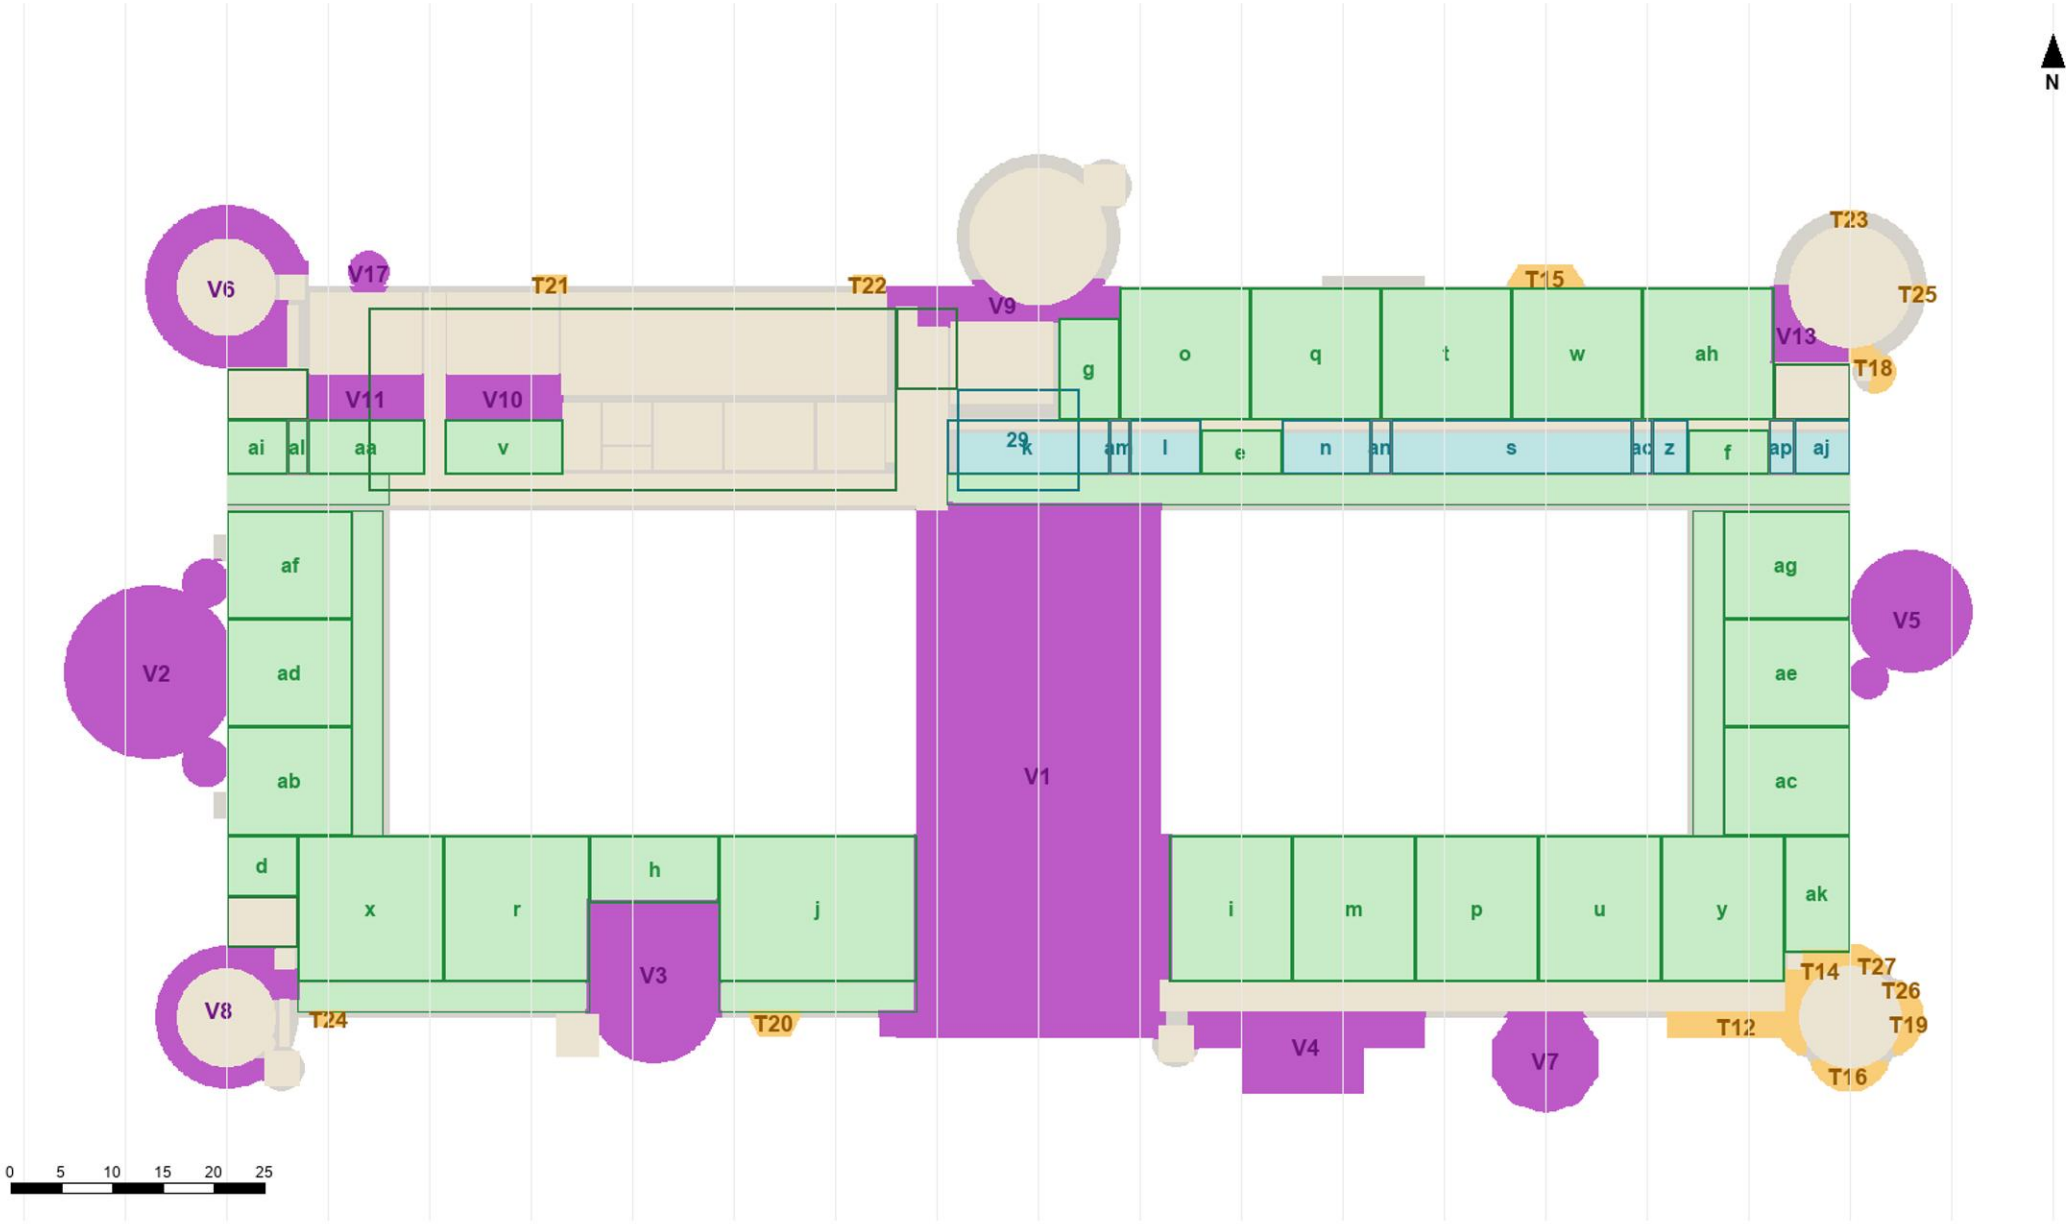

Fill: beige, built in the model; green, layout room as drawn inside its walls; teal, trimmed; pale red, what a reimagined room keeps; purple, a true void (3 m wide or more); amber, a thick wall (1.5 to 3 m). Outlines: the layout's rects; red thick, reimagine.

Fifth floor (5): the layout's rooms after the wall rule, the true voids flagged


35 as drawn, 13 trimmed, 7 built, 7 follows. Voids: V1 1285 m2 (24.4 wide), V2 260 m2 (16.2 wide), V3 137 m2 (8.2 wide), V4 128 m2 (12.1 wide), V5 123 m2 (9.0 wide), V6 121 m2 (4.2 wide), V7 96 m2 (9.8 wide), V8 80 m2 (3.0 wide), V10 30 m2 (4.0 wid

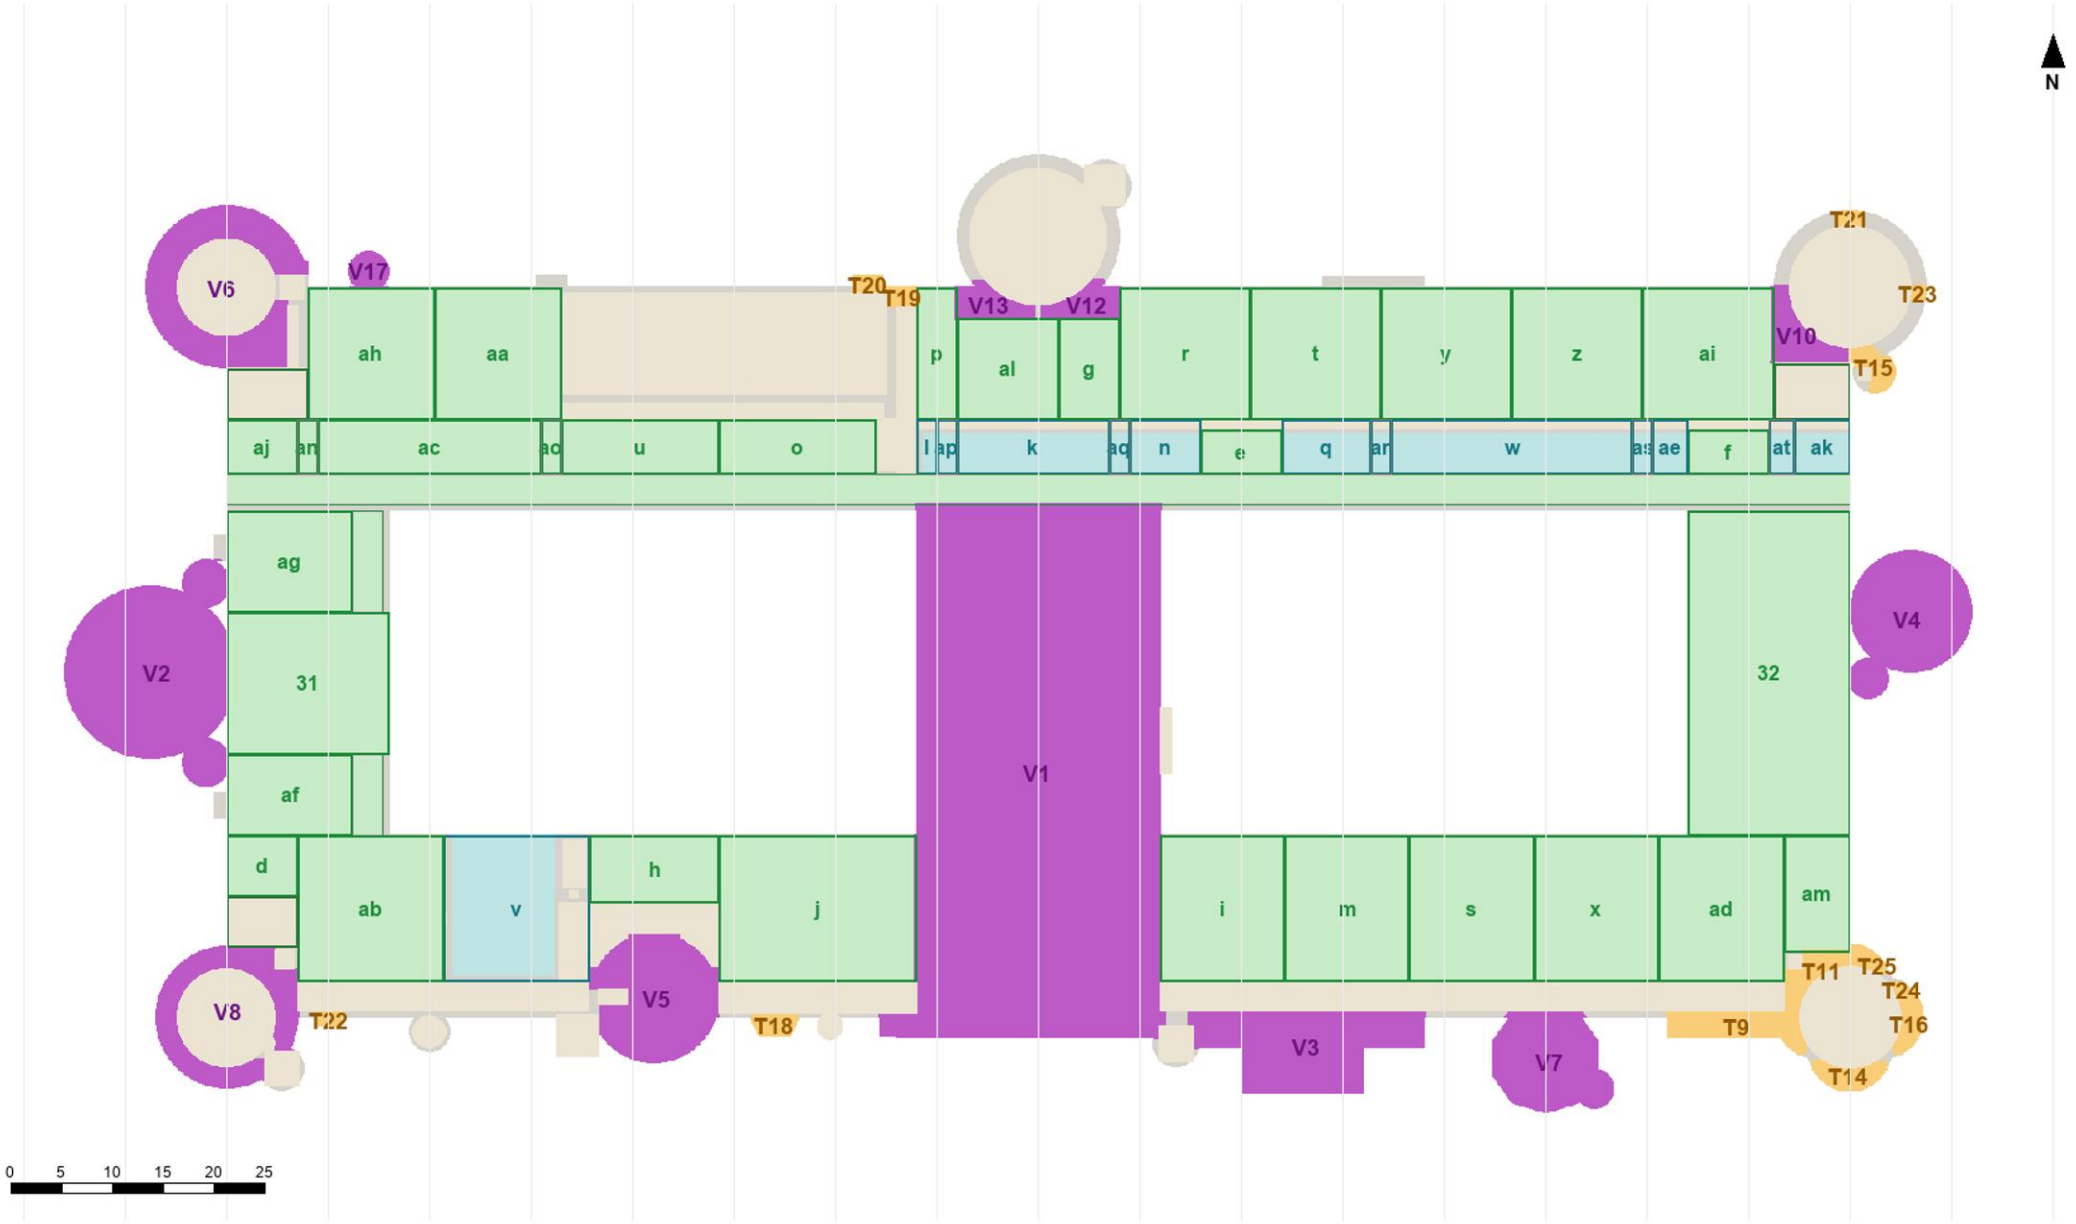

Fill: beige, built in the model; green, layout room as drawn inside its walls; teal, trimmed; pale red, what a reimagined room keeps; purple, a true void (3 m wide or more); amber, a thick wall (1.5 to 3 m). Outlines: the layout's rects; red thick, reimagine.

Sixth floor (6): the layout's rooms after the wall rule, the true voids flagged


24 trimmed, 11 built, 28 as drawn, 8 follows. Voids: V1 1273 m2 (24.4 wide), V2 260 m2 (16.2 wide), V3 196 m2 (13.3 wide), V4 128 m2 (12.1 wide), V5 96 m2 (9.8 wide), V6 90 m2 (5.7 wide), V7 81 m2 (3.0 wide), V8 38 m2 (3.6 wide), V10 34 m2 (3.8 wid

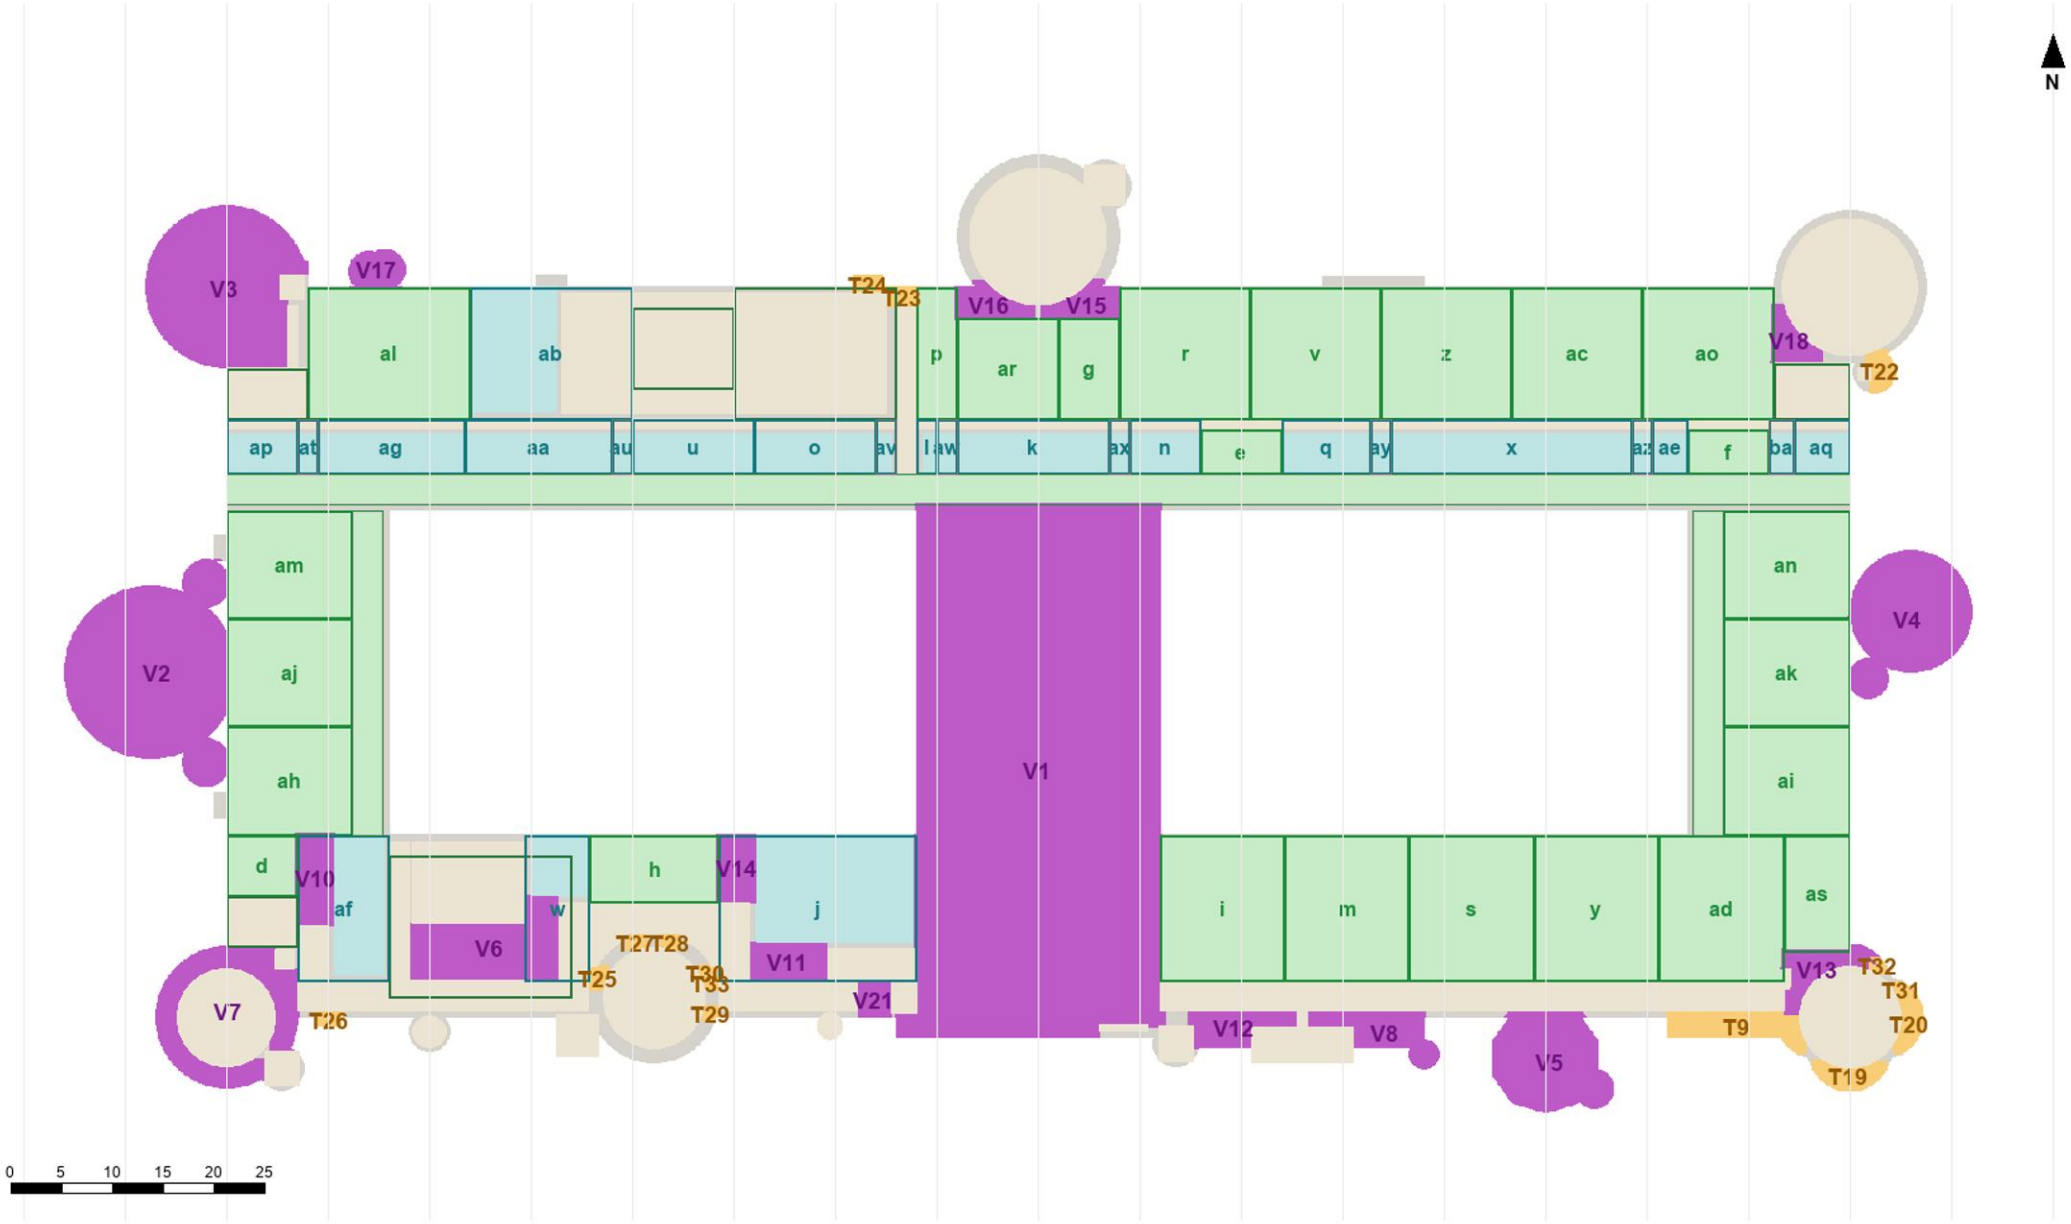

Fill: beige, built in the model; green, layout room as drawn inside its walls; teal, trimmed; pale red, what a reimagined room keeps; purple, a true void (3 m wide or more); amber, a thick wall (1.5 to 3 m). Outlines: the layout's rects; red thick, reimagine.

Seventh floor (7): the layout's rooms after the wall rule, the true voids flagged

15 as drawn, 17 built, 15 trimmed, 11 reimagine, 5 follows. Voids: V1 1331 m2 (24.4 wide), V2 562 m2 (18.2 wide), V3 260 m2 (16.2 wide), V4 195 m2 (13.3 wide), V5 177 m2 (14.1 wide), V6 139 m2 (11.8 wide), V7 102 m2 (6.4 wide), V8 98 m2 (10.4 wide

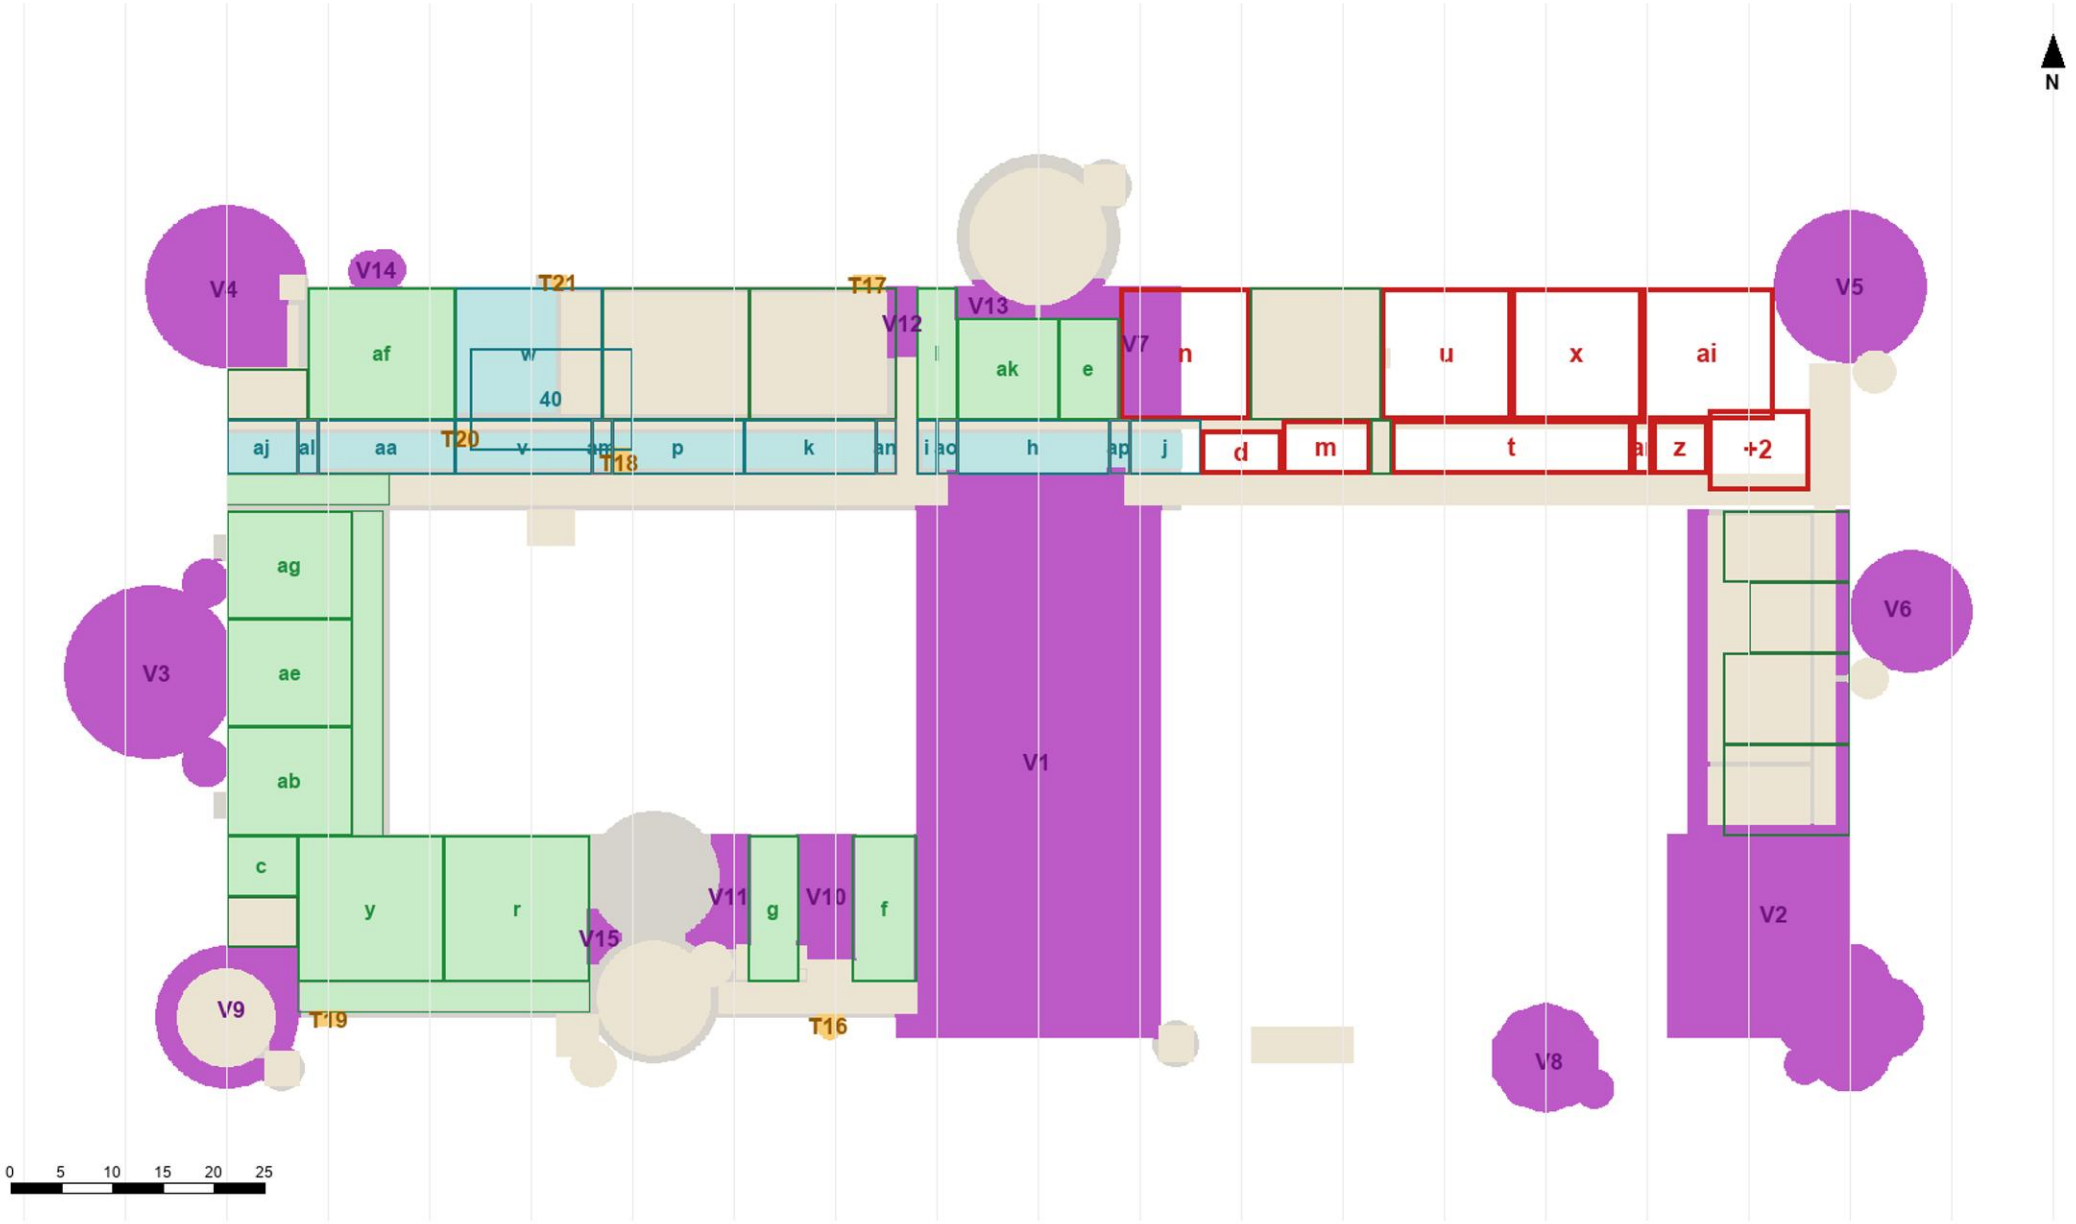

Fill: beige, built in the model; green, layout room as drawn inside its walls; teal, trimmed; pale red, what a reimagined room keeps; purple, a true void (3 m wide or more); amber, a thick wall (1.5 to 3 m). Outlines: the layout's rects; red thick, reimagine.

n The corridor beneath the tal: off the building: 47% inside the walls here

u A teacher's study: off the building: 0% inside the walls here

ai A teacher's study: off the building: 0% inside the walls here

x A study room: off the building: 0% inside the walls here

t A store: off the building: 0% inside the walls here

+2 Sir Cadogan's landing, at th: off the building: 0% inside the walls here

m A store of old textbooks: off the building: 0% inside the walls here

d Washrooms, girls' and boys': off the building: 0% inside the walls here

z Professor Trelawney's sherry: off the building: 0% inside the walls here

ar A passage to the rooms behin: off the building: 0% inside the walls here

c16 corridor: off the building: 0% inside the walls here