Hogwarts, floor by floor: every place and every space between

The Architect, 14 October 2026, for Godric. The castle model (page/castle-model.js, version 25) and the step 3 sheet, under 1.1, 2.1, 3.1, Q48b's 3 and 4.1.

How to read it

One floor a page, below ground to the tower tops, all at one scale (north up, the bar 50 m), a schedule under each plan.

Numbers are the named places: the first draft's (1 to 48) and the canon sweep's (+1 to +48), each with its book line. Brown is built, hatched designed, blue placed by the books, dotted inferred, dashed proposed.

Built so far, the places the boys can already walk: the Gryffindor common room, the dormitory above it, and the Fat Lady's corridor to her portrait (the seventh floor and the tower tops, in brown).

Letters, in purple rooms, are this drawing's fill: every range has a corridor along one face and rooms along the other, cut from whatever the named places leave free, and each room is given a use and a name. Green: a place the books name but do not place (the sweep's unplaced rows, each checked in the text); purple: ours. A room of ours with a canon nod names its line.

The rule of the fill

Canon first. Then what a working castle school needs near what it serves: each subject's second classroom, store and teacher's rooms beside its named classroom; the kitchens' rooms by the kitchens. Stairs and washrooms stack: each tower's foot gives a stair between every floor in the corner it leaves in its range, and the washrooms keep the same three places on every floor (two in the north range, one by the south-west tower), skipped only where a named place takes the spot. Cupboards and stores fill the deep middle of the north range, where no window reaches. A classroom goes only in a room at least 7 m across, and no range repeats a room's name on one floor. Then a few rooms for the boys to find (a wizard chess room, Peeves's den of stolen chalk, portraits waiting for walls). No corridor runs past nothing.

The count

310 spaces given a use: 14 canon, 296 ours. By floor: B 35, G 32, 1 28, 2 31, 3 36, 4 38, 5 35, 6 40, 7 35, T 0.

Open


All of the fill is a proposal: mark any room and it changes. The fill goes into the model only once you have looked; the Map is inked from the model.

The castle's layout, below ground: the cellars and dungeons

The Architect, 14 October 2026, for Godric, on the castle model, version 25. Under 1.1, 2.1, 3.1 and Q48b's 3. North up; the bar 50 m. Numbers: the step 3 sheet's places (+ the canon sweep's); letters, purple: this sheet's fill, every space given a use.

Below ground: the dungeons and the cellars

floor at -5.2 m

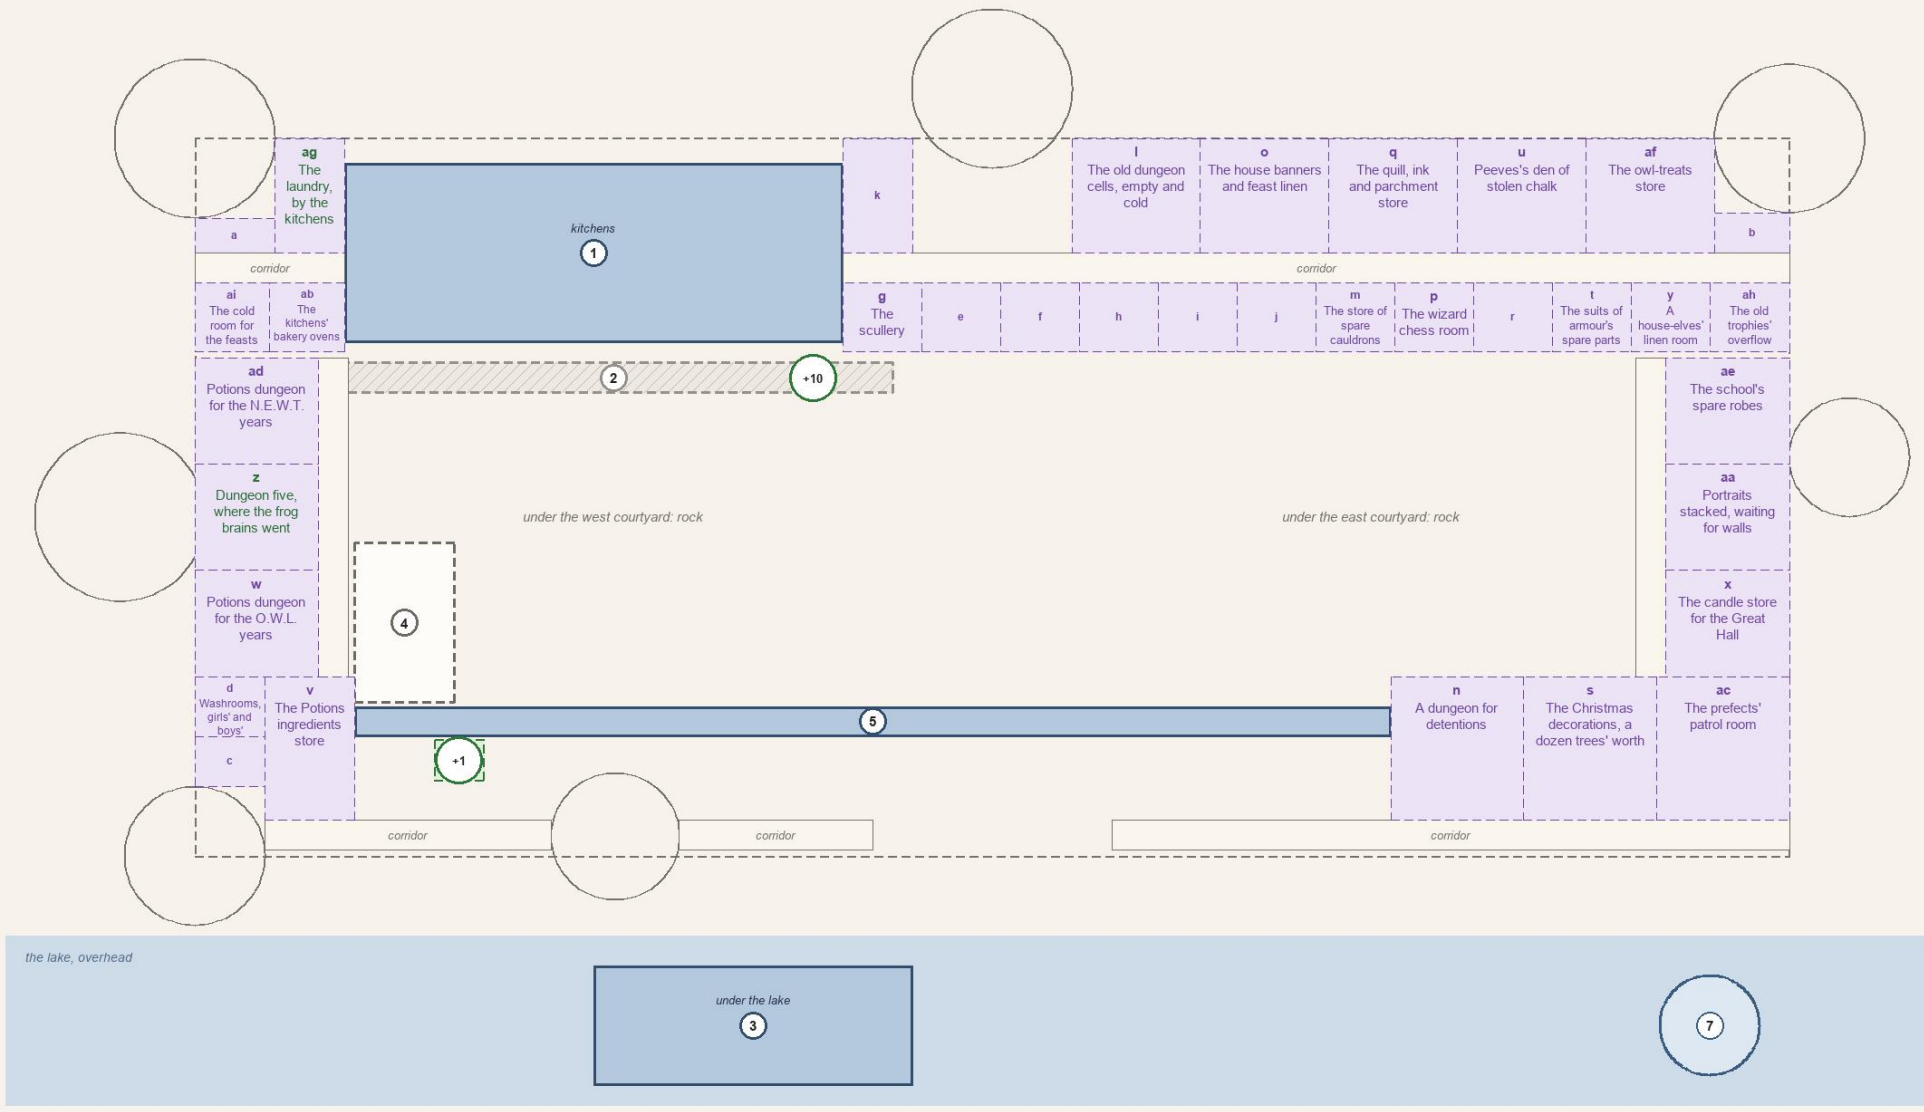

Named places on this floor (the step 3 sheet: numbers the first draft's, + the canon sweep's)

1 Kitchens [books] (GoF 21)
2 Hufflepuff's basement corridor, which also leads to the kitchens (Hufflepuff's room off the list) [off] (OotP 18, HBP 21)
3 Slytherin common room [books] (DH 23)
4 Potions classroom, down in a dungeon (the spot proposed) [proposed] (PS 8)
5 Dungeon corridors, the deathday party (the spot proposed) [books] (CoS 8)
6 The chambers under the trapdoor, "miles under the school" [inferred] (PS 16)
7 Chamber of Secrets [inferred] (CoS 16)
+1 Snape's office, halfway down the cold passage, by Potions (CoS 5, GoF 25) [canon]
+10 The fruit-bowl painting, the kitchens' door (GoF 21) [canon]

The towers at this level

Astronomy Tower: its stair to the top
Ravenclaw Tower: its tight spiral stair (+23)
Gryffindor Tower: below the common room: the house's storerooms (ours)
West Tower: its stair; Flitwick's office on 7 (42)
North Tower: its stair; the trapdoor landing on 7 (+3)
south-west tower: a stair and staff rooms (ours)
Dumbledore's tower: the gargoyle's moving stair on 7 (41)

Cores not on this floor (a named place takes the spot)

A Gryffindor storeroom at the tower's foot: 5 takes it


This sheet's fill, every space given a use (green: canon, purple: ours)

a The West Tower's stair foot, a stair between every floor [ours: PS 8: "a hundred and forty-two staircases"] core, 8 by 4 m
b The North Tower's stair foot, a stair between every floor [ours: PS 8: "a hundred and forty-two staircases"] core, 8 by 4 m
c The south-west tower's stair foot, a stair between every floor [ours: PS 8: "a hundred and forty-two staircases"] core, 7 by 5 m
d Washrooms, girls' and boys' [ours] core, 7 by 6 m
e The kitchen stores: flour, sugar, the pumpkins [ours] north range, 8 by 7 m
f The brewing cellar, where slow potions steep [ours] north range, 8 by 7 m
g The scullery [ours] north range, 8 by 7 m
h The cellar of butterbeer and pumpkin juice [ours] north range, 8 by 7 m
i Coal and log store for the castle's fires [ours] north range, 8 by 7 m
j Filch's store of confiscated things [ours] north range, 8 by 7 m
k The house-elves' quarters [ours] north range, 7 by 12 m
l The old dungeon cells, empty and cold [ours] north range, 13 by 12 m
m The store of spare cauldrons [ours] north range, 8 by 7 m
n A dungeon for detentions [ours] south range, east, 13 by 14 m
o The house banners and feast linen [ours] north range, 13 by 12 m
p The wizard chess room [ours] north range, 8 by 7 m
q The quill, ink and parchment store [ours] north range, 13 by 12 m
r A ghosts' gathering room, cold all year [ours] north range, 8 by 7 m
s The Christmas decorations, a dozen trees' worth [ours] south range, east, 13 by 14 m
t The suits of armour's spare parts [ours] north range, 8 by 7 m
u Peeves's den of stolen chalk [ours] north range, 13 by 12 m
v The Potions ingredients store [ours] south range, west, 9 by 14 m
w Potions dungeon for the O.W.L. years [ours] west range, 12 by 11 m
x The candle store for the Great Hall [ours] east range, 12 by 11 m
y A house-elves' linen room [ours] north range, 8 by 7 m
z Dungeon five, where the frog brains went [canon: CoS 8] west range, 12 by 11 m
aa Portraits stacked, waiting for walls [ours] east range, 12 by 11 m
ab The kitchens' bakery ovens [ours] north range, 8 by 7 m
ac The prefects' patrol room [ours] south range, east, 13 by 14 m
ad Potions dungeon for the N.E.W.T. years [ours] west range, 12 by 11 m
ae The school's spare robes [ours] east range, 12 by 11 m
af The owl-treats store [ours] north range, 13 by 12 m
ag The laundry, by the kitchens [canon: CoS 12; its spot ours] north range, 7 by 12 m
ah The old trophies' overflow [ours] north range, 8 by 7 m
ai The cold room for the feasts [ours] north range, 8 by 7 m

The castle's layout, the ground floor

The Architect, 14 October 2026, for Godric, on the castle model, version 25. Under 1.1, 2.1, 3.1 and Q48b's 3. North up; the bar 50 m. Numbers: the step 3 sheet's places (+ the canon sweep's); letters, purple: this sheet's fill, every space given a use.

Ground floor

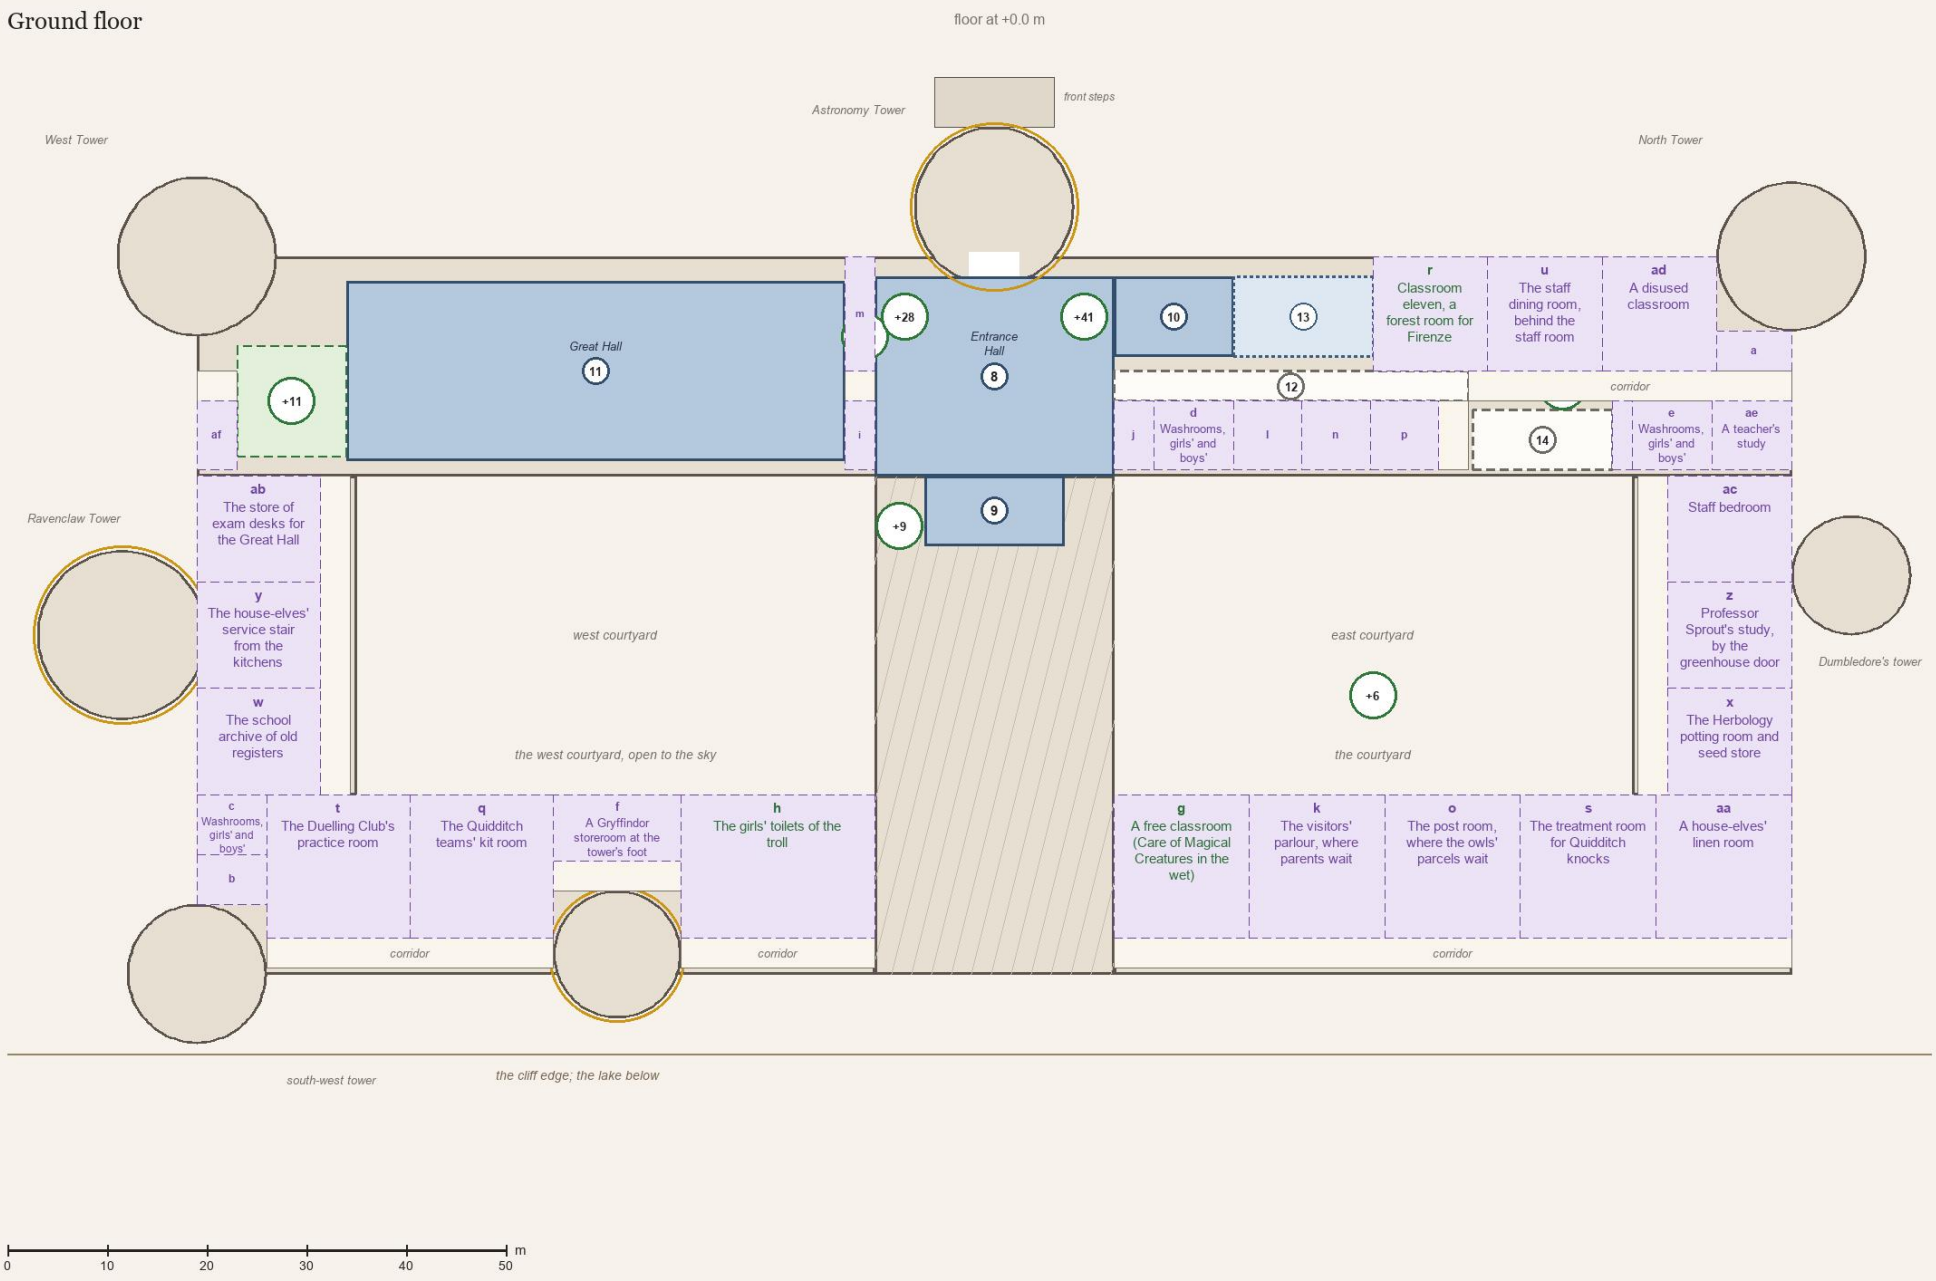

Named places on this floor (the step 3 sheet: numbers the first draft's, + the canon sweep's)

8 Entrance Hall, its front doors in the north face under the Astronomy Tower [books] (PS 7, OotP 31)
9 Marble staircase, facing the front doors [books] (PS 7, PoA 14)
10 The small, empty chamber off the hall (the side proposed) [books] (PS 7)
11 Great Hall, through a doorway to the right on entering, so west of the hall [books] (PS 7)
12 The corridor of classrooms opposite the Great Hall's door [proposed] (OotP 27)
13 Filch's office [inferred] (CoS 8)
14 The staff room [proposed] (PS 11)
+9 The Hufflepuff door, right of the marble staircase, steps down (GoF 17) [canon]
+6 The courtyard, by the staff room, its balcony and steps (OotP 17, OotP 12, CoS 6) [canon]
+11 The chamber off the Great Hall, behind the staff table (GoF 16, 17) [canon]
+12 The broom cupboard across the hall (PoA 21) [canon]
+27 The staff room's two gargoyles at its door (OotP 17) [canon]
+28 The Entrance Hall's balcony (DH 32) [canon]
+41 The tapestry door and narrow stair up from the hall (GoF 12) [canon]

The model's rooms with no number (page/castle-model.js, version 25)

the passage past the staff room door (staff-passage)

The towers at this level

Astronomy Tower: its stair to the top
Ravenclaw Tower: its tight spiral stair (+23)
Gryffindor Tower: below the common room: the house's storerooms (ours)
West Tower: its stair; Flitwick's office on 7 (42)
North Tower: its stair; the trapdoor landing on 7 (+3)
south-west tower: a stair and staff rooms (ours)
Dumbledore's tower: the gargoyle's moving stair on 7 (41)

Cores not on this floor (a named place takes the spot)

The West Tower's stair foot, a stair between every floor: +11 takes it

This sheet's fill, every space given a use (green: canon, purple: ours)


a The North Tower's stair foot, a stair between every floor [ours: PS 8: "a hundred and forty-two staircases"] core, 8 by 4 m
b The south-west tower's stair foot, a stair between every floor [ours: PS 8: "a hundred and forty-two staircases"] core, 7 by 5 m
c Washrooms, girls' and boys' [ours] core, 7 by 6 m
d Washrooms, girls' and boys' [ours] core, 8 by 7 m
e Washrooms, girls' and boys' [ours] core, 8 by 7 m
f A Gryffindor storeroom at the tower's foot [ours] core, 13 by 7 m
g A free classroom (Care of Magical Creatures in the wet) [canon: OotP 18] south range, east, 14 by 14 m
h The girls' toilets of the troll [canon: PS 10; its floor ours] south range, west, 19 by 14 m
i A broom cupboard [ours] north range, 3 by 7 m
j A store of spare desks and chairs [ours] north range, 4 by 7 m
k The visitors' parlour, where parents wait [ours] south range, east, 14 by 14 m
l The porters' lodge by the front doors [ours] north range, 7 by 7 m
m A linen cupboard [ours] north range, 3 by 12 m
n The cloakroom, wet boots and cloaks [ours] north range, 7 by 7 m
o The post room, where the owls' parcels wait [ours] south range, east, 14 by 14 m
p Madam Hooch's store of school brooms [ours] north range, 7 by 7 m
q The Quidditch teams' kit room [ours] south range, west, 14 by 14 m
r Classroom eleven, a forest room for Firenze [canon: OotP 27: off the Entrance Hall, opposite the Great Hall] north range, 12 by 12 m
s The treatment room for Quidditch knocks [ours] south range, east, 14 by 14 m
t The Duelling Club's practice room [ours: the club canon (CoS 11)] south range, west, 14 by 14 m
u The staff dining room, behind the staff room [ours] north range, 12 by 12 m
v A service passage [ours] north range, 2 by 7 m
w The school archive of old registers [ours] west range, 12 by 11 m
x The Herbology potting room and seed store [ours] east range, 12 by 11 m
y The house-elves' service stair from the kitchens [ours] west range, 12 by 11 m
z Professor Sprout's study, by the greenhouse door [ours] east range, 12 by 11 m
aa A house-elves' linen room [ours] south range, east, 14 by 14 m
ab The store of exam desks for the Great Hall [ours] west range, 12 by 11 m
ac Staff bedroom [ours] east range, 12 by 11 m
ad A disused classroom [ours] north range, 12 by 12 m
ae A teacher's study [ours] north range, 8 by 7 m
af Filch's cleaning cupboard [ours] north range, 4 by 7 m

The castle's layout, the first floor

The Architect, 14 October 2026, for Godric, on the castle model, version 25. Under 1.1, 2.1, 3.1 and Q48b's 3. North up; the bar 50 m. Numbers: the step 3 sheet's places (+ the canon sweep's); letters, purple: this sheet's fill, every space given a use.

First floor

floor at +5.2 m

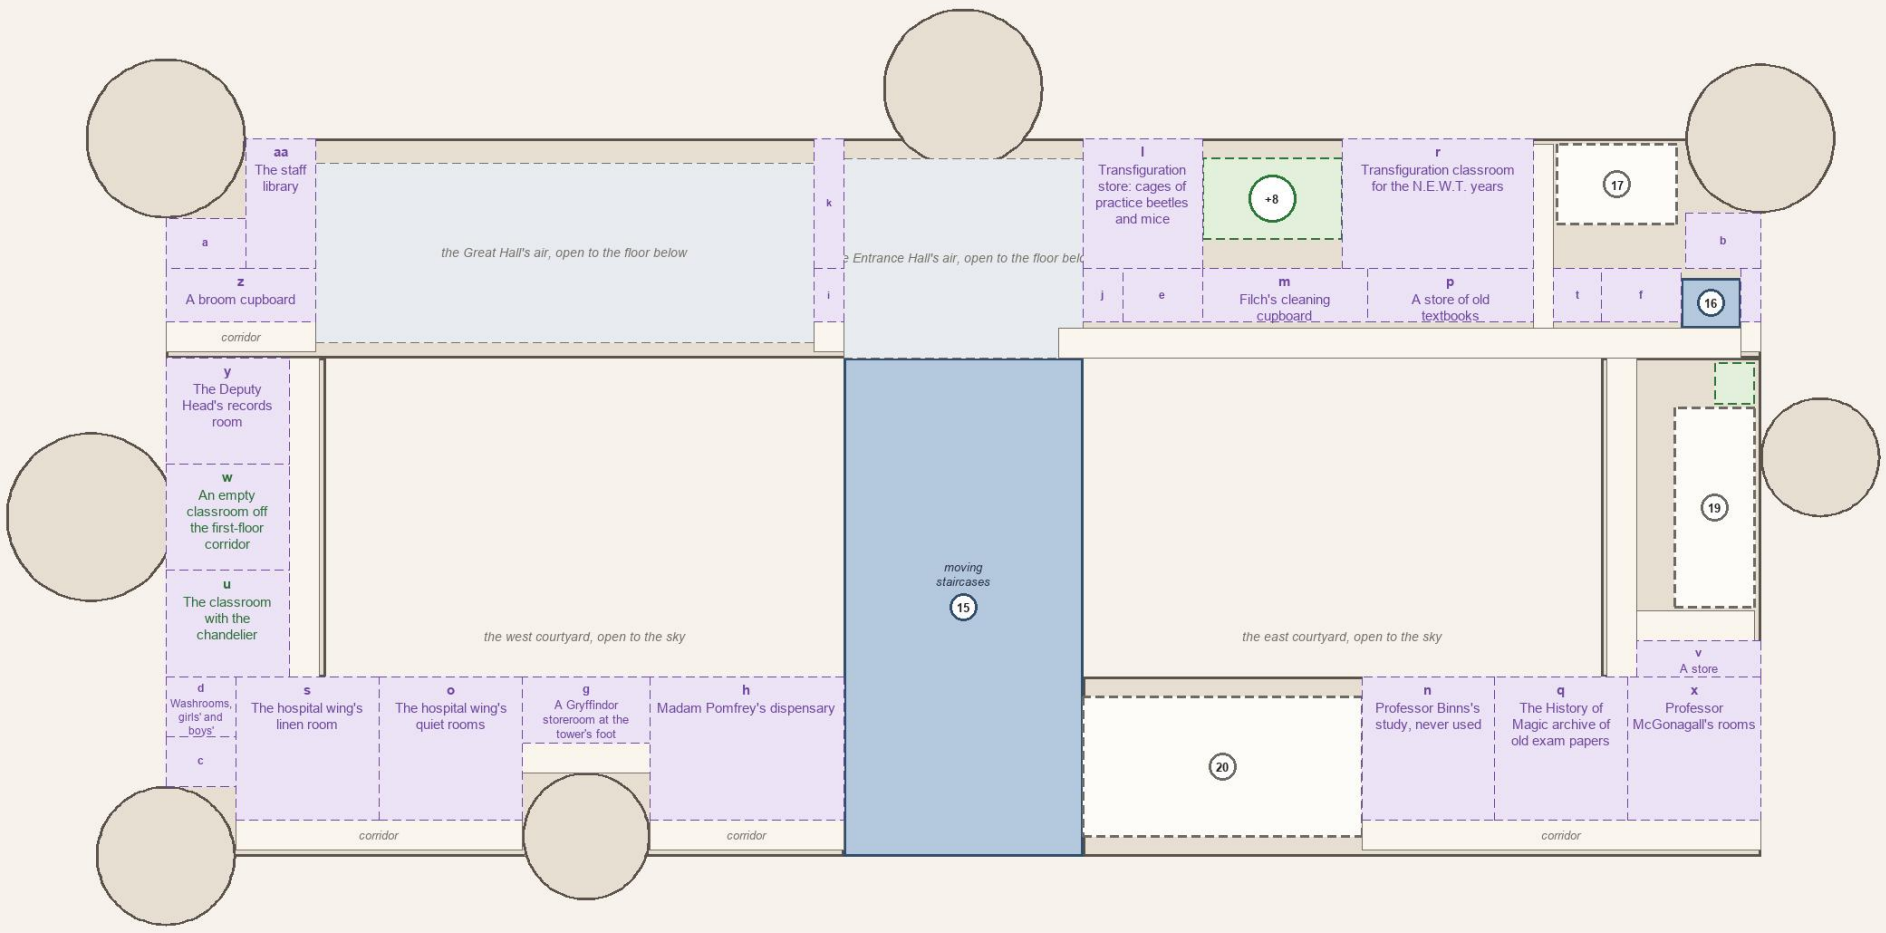

0 10 20 30 40 50 m

N

Named places on this floor (the step 3 sheet: numbers the first draft's, + the canon sweep's)

15 The moving staircases and the marble staircase in one hall, the front doors to the cliff face [books] (PS 8)
16 McGonagall's study, first floor (off the list [books] (PS 15)
17 Transfiguration classroom, beside her study [proposed]
19 Hospital wing [proposed] (PS 8)
20 History of Magic classroom, "large enough" for a class [proposed] (PoA 12)
+8 The Vanishing Cabinet's room, right over Filch's office (OotP 28, CoS 8) [canon]

The model's rooms with no number (page/castle-model.js, version 25)

the first floor's corridor (first-floor-corridor)
the first floor's corridor down the east range (east-first-floor-corridor)
the passage outside the hospital wing (hospital-passage)
Madam Pomfrey's office (pomfrey-office)
the passage to the Transfiguration classroom (transfiguration-passage)

Open to the floor below (a hall or room rising through this storey)

the Entrance Hall's air, 24 by 20 m
the Great Hall's air, 50 by 18 m

The towers at this level

Astronomy Tower: its stair to the top
Ravenclaw Tower: its tight spiral stair (+23)
Gryffindor Tower: below the common room: the house's storerooms (ours)
West Tower: its stair; Flitwick's office on 7 (42)
North Tower: its stair; the trapdoor landing on 7 (+3)
south-west tower: a stair and staff rooms (ours)
Dumbledore's tower: the gargoyle's moving stair on 7 (41)

Cores not on this floor (a named place takes the spot)

The Astronomy Tower's stair foot, its stair to the top: the Entrance Hall's air takes it

This sheet's fill, every space given a use (green: canon, purple: ours)


a The West Tower's stair foot, a stair between every floor [ours: PS 8: "a hundred and forty-two staircases"] core, 8 by 5 m
b The North Tower's stair foot, a stair between every floor [ours: PS 8: "a hundred and forty-two staircases"] core, 8 by 6 m
c The south-west tower's stair foot, a stair between every floor [ours: PS 8: "a hundred and forty-two staircases"] core, 7 by 5 m
d Washrooms, girls' and boys' [ours] core, 7 by 6 m
e Washrooms, girls' and boys' [ours] core, 8 by 5 m
f Washrooms, girls' and boys' [ours] core, 8 by 5 m
g A Gryffindor storeroom at the tower's foot [ours] core, 13 by 7 m
h Madam Pomfrey's dispensary [ours] south range, west, 19 by 14 m
i A broom cupboard [ours] north range, 3 by 5 m
j A store of spare desks and chairs [ours] north range, 4 by 5 m
k A linen cupboard [ours] north range, 3 by 13 m
l Transfiguration store: cages of practice beetles and mice [ours] north range, 12 by 13 m
m Filch's cleaning cupboard [ours] north range, 17 by 5 m
n Professor Binns's study, never used [ours] south range, east, 13 by 14 m
o The hospital wing's quiet rooms [ours] south range, west, 14 by 14 m
p A store of old textbooks [ours] north range, 17 by 5 m
q The History of Magic archive of old exam papers [ours] south range, east, 13 by 14 m
r Transfiguration classroom for the N.E.W.T. years [ours] north range, 19 by 13 m
s The hospital wing's linen room [ours] south range, west, 14 by 14 m
t A lamp and candle cupboard [ours] north range, 5 by 5 m
u The classroom with the chandelier [canon: OotP 18] west range, 12 by 11 m
v A store [ours] east range, 12 by 4 m
w An empty classroom off the first-floor corridor [canon: OotP 32] west range, 12 by 11 m
x Professor McGonagall's rooms [ours] south range, east, 13 by 14 m
y The Deputy Head's records room [ours] west range, 12 by 11 m
z A broom cupboard [ours] north range, 15 by 5 m
aa The staff library [ours] north range, 7 by 13 m
ab A service passage [ours] north range, 2 by 5 m

The castle's layout, the second floor

The Architect, 14 October 2026, for Godric, on the castle model, version 25. Under 1.1, 2.1, 3.1 and Q48b's 3. North up; the bar 50 m. Numbers: the step 3 sheet's places (+ the canon sweep's); letters, purple: this sheet's fill, every space given a use.

Second floor

floor at +10.4 m

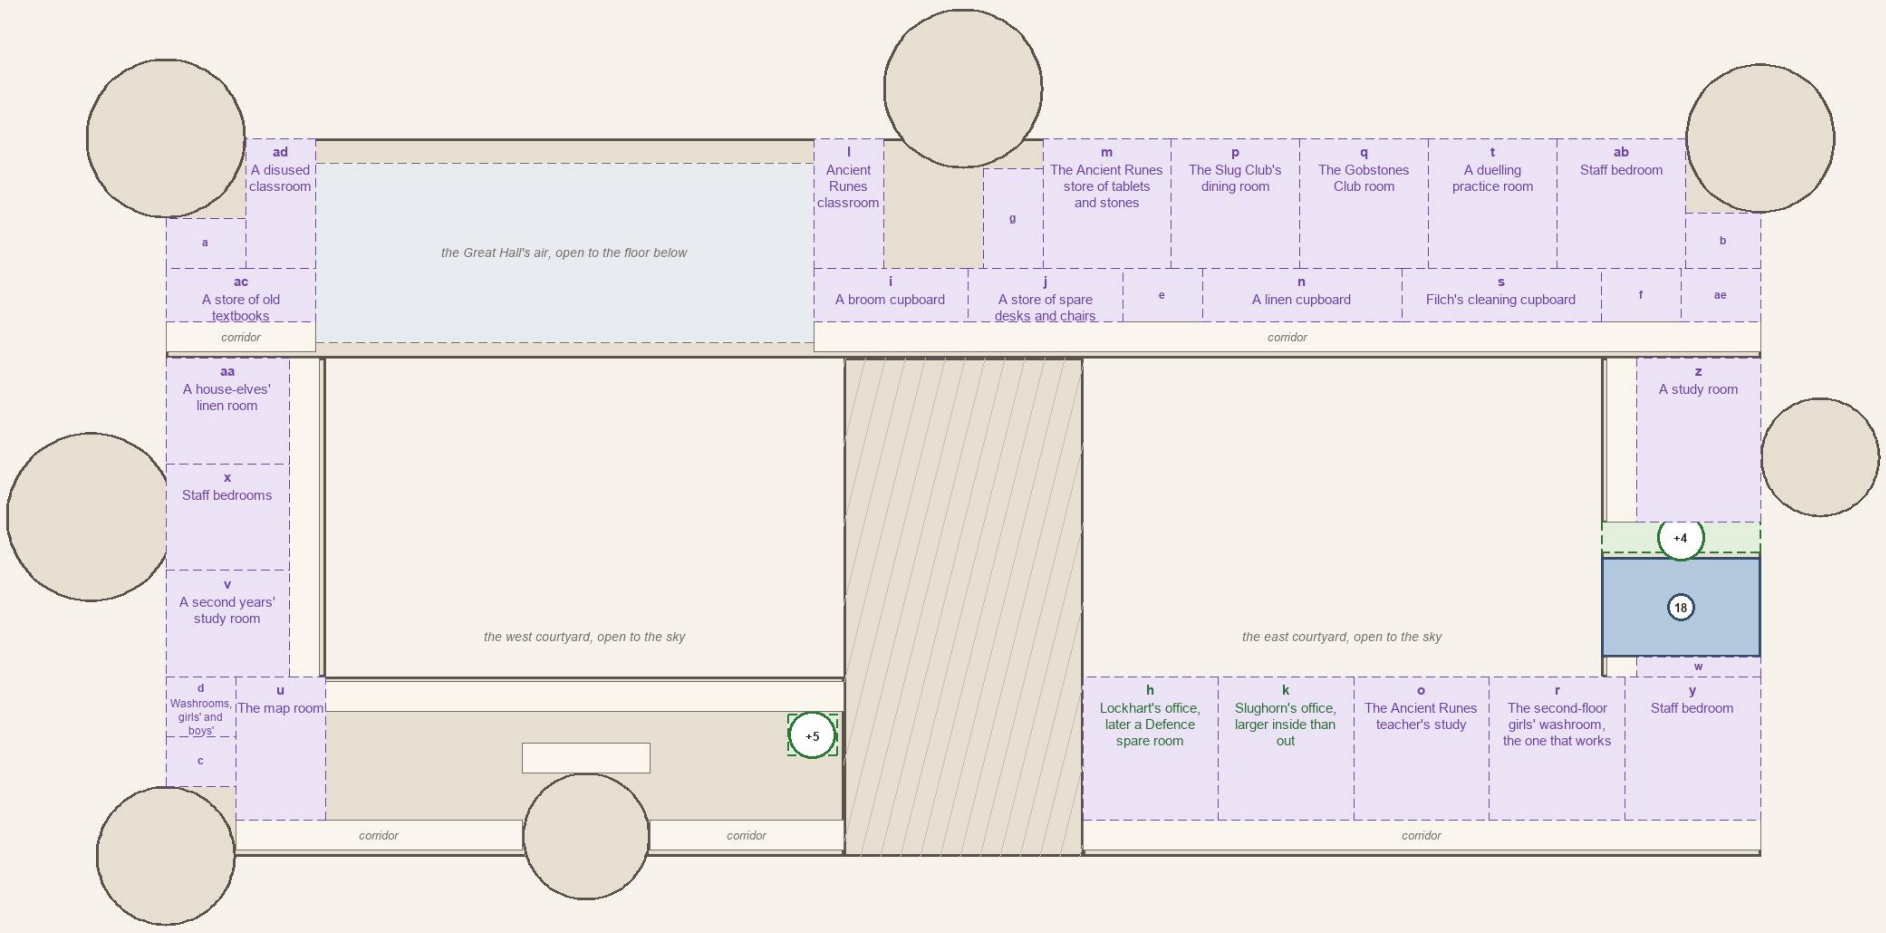

0 10 20 30 40 50 m

N

Named places on this floor (the step 3 sheet: numbers the first draft's, + the canon sweep's)

18 Myrtle's bathroom, the Chamber's door [books] (CoS 8, GoF 22)
+4 The writing on the wall: the last, deserted passage, by Myrtle's (CoS 8, 16) [canon]
+7 The trick-step tapestry stair, four down to two (GoF 25, HBP 14) [canon]
+29 The fireworks corridor, one floor below the Defence office (OotP 28) [canon]
+5 The Defence office (Umbridge's), its corridor's suit of armour (OotP 13, 29) [canon]

The model's rooms with no number (page/castle-model.js, version 25)

the second floor's corridor (second-floor-corridor)

Open to the floor below (a hall or room rising through this storey)

the Great Hall's air, 50 by 18 m

The towers at this level

Astronomy Tower: its stair to the top
Ravenclaw Tower: its tight spiral stair (+23)
Gryffindor Tower: below the common room: the house's storerooms (ours)
West Tower: its stair; Flitwick's office on 7 (42)
North Tower: its stair; the trapdoor landing on 7 (+3)
south-west tower: a stair and staff rooms (ours)
Dumbledore's tower: the gargoyle's moving stair on 7 (41)

Cores not on this floor (a named place takes the spot)

A Gryffindor storeroom at the tower's foot: the second floor's corridor takes it

This sheet's fill, every space given a use (green: canon, purple: ours)


a The West Tower's stair foot, a stair between every floor [ours: PS 8: "a hundred and forty-two staircases"] core, 8 by 5 m
b The North Tower's stair foot, a stair between every floor [ours: PS 8: "a hundred and forty-two staircases"] core, 8 by 6 m
c The south-west tower's stair foot, a stair between every floor [ours: PS 8: "a hundred and forty-two staircases"] core, 7 by 5 m
d Washrooms, girls' and boys' [ours] core, 7 by 6 m
e Washrooms, girls' and boys' [ours] core, 8 by 5 m
f Washrooms, girls' and boys' [ours] core, 8 by 5 m
g The Astronomy Tower's stair foot, its stair to the top [ours] core, 6 by 10 m
h Lockhart's office, later a Defence spare room [canon: CoS 7, CoS 9, CoS 16] south range, east, 14 by 14 m
i A broom cupboard [ours] north range, 16 by 5 m
j A store of spare desks and chairs [ours] north range, 16 by 5 m
k Slughorn's office, larger inside than out [canon: HBP 15: up the marble staircase; its floor ours] south range, east, 14 by 14 m
l Ancient Runes classroom [ours: the subject canon, the room ours] north range, 7 by 13 m
m The Ancient Runes store of tablets and stones [ours] north range, 13 by 13 m
n A linen cupboard [ours] north range, 20 by 5 m
o The Ancient Runes teacher's study [ours] south range, east, 14 by 14 m
p The Slug Club's dining room [ours: the club canon (HBP 7)] north range, 13 by 13 m
q The Gobstones Club room [ours: the club canon (OotP 17)] north range, 13 by 13 m
r The second-floor girls' washroom, the one that works [ours] south range, east, 14 by 14 m
s Filch's cleaning cupboard [ours] north range, 20 by 5 m
t A duelling practice room [ours] north range, 13 by 13 m
u The map room [ours] south range, west, 9 by 14 m
v A second years' study room [ours] west range, 12 by 11 m
w A service passage [ours] east range, 12 by 2 m
x Staff bedrooms [ours] west range, 12 by 11 m
y Staff bedroom [ours] south range, east, 14 by 14 m
z A study room [ours] east range, 12 by 16 m
aa A house-elves' linen room [ours] west range, 12 by 11 m
ab Staff bedroom [ours] north range, 13 by 13 m
ac A store of old textbooks [ours] north range, 15 by 5 m
ad A disused classroom [ours] north range, 7 by 13 m
ae A lamp and candle cupboard [ours] north range, 8 by 5 m

The castle's layout, the third floor

The Architect, 14 October 2026, for Godric, on the castle model, version 25. Under 1.1, 2.1, 3.1 and Q48b's 3. North up; the bar 50 m. Numbers: the step 3 sheet's places (+ the canon sweep's); letters, purple: this sheet's fill, every space given a use.

Third floor

floor at +15.6 m

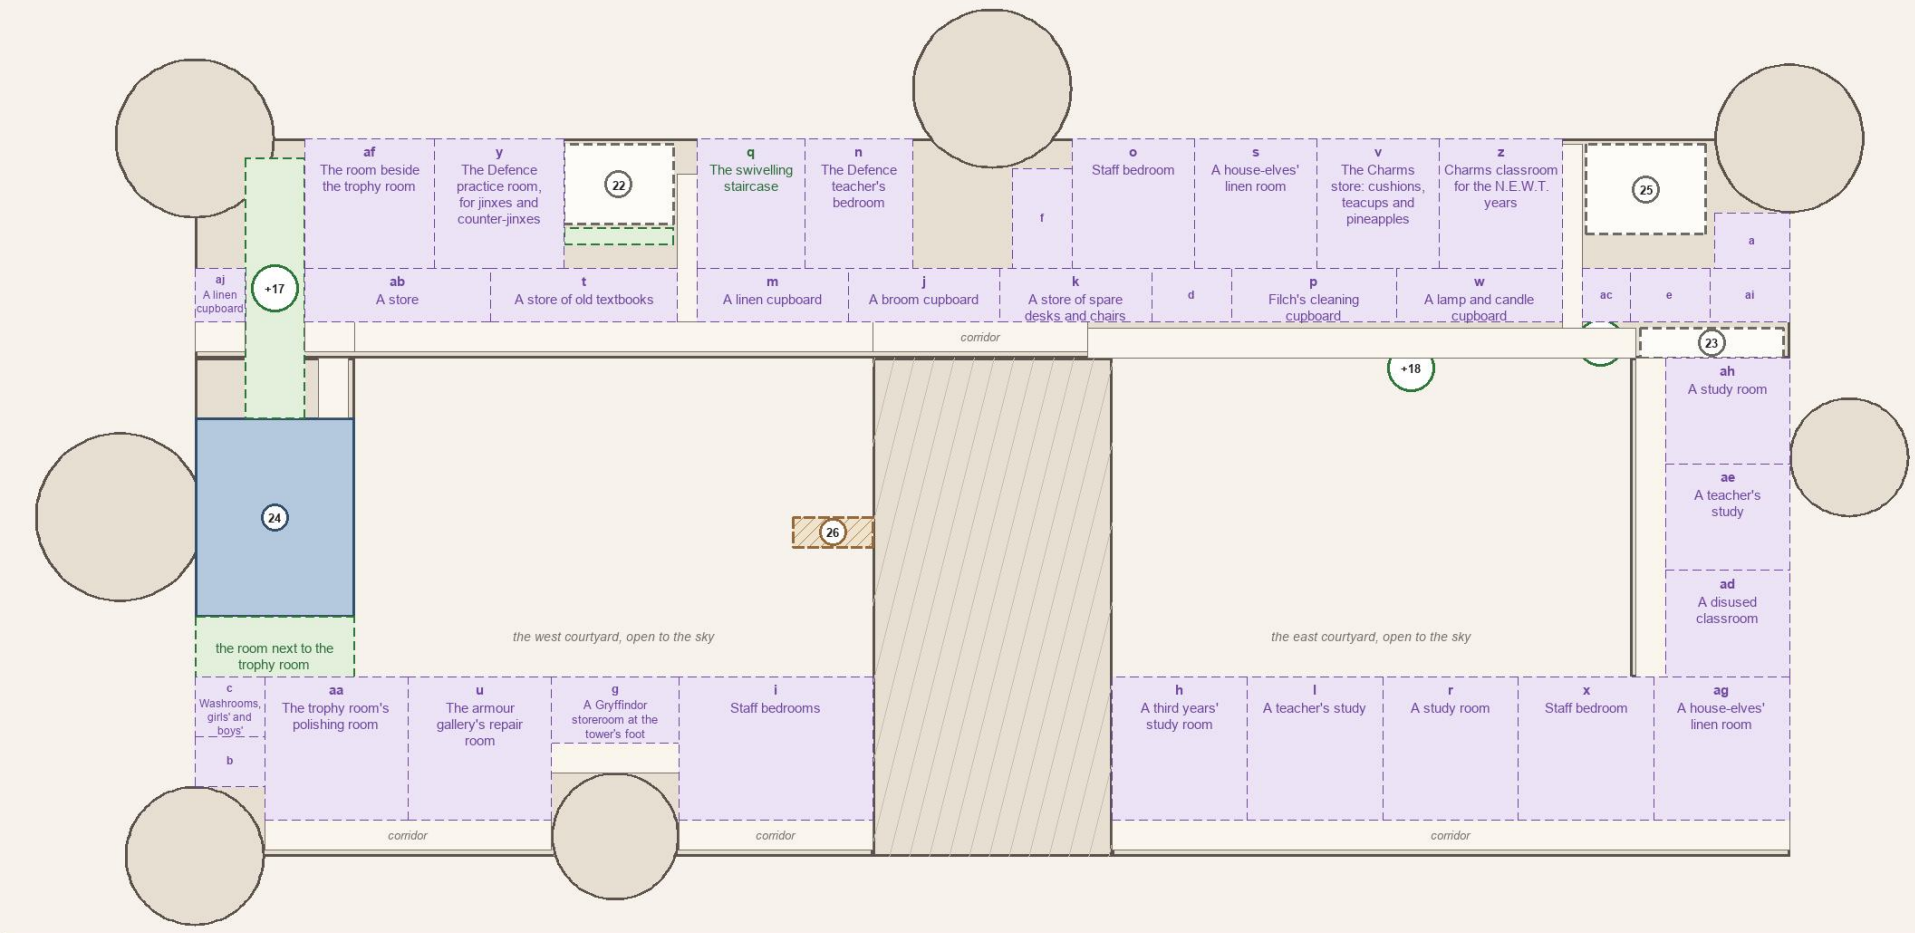





Named places on this floor (the step 3 sheet: numbers the first draft's, + the canon sweep's)

22 Defence Against the Dark Arts classroom [proposed] (PoA 9)
23 The forbidden corridor [proposed] (PS 7)
24 Trophy room, third floor (the spot proposed) [books] (PS 9)
25 Charms classroom [proposed] (PS 9)
26 The one-eyed witch's landing, directly beneath the corridor's landing, on the stair hall's well [designed] (PoA 10, 14)
+15 The Charms corridor, ending at the forbidden door (PS 9) [canon]
+17 The long gallery of armour, by the trophy room (PS 9) [canon]
+18 The drunk monks, by the Charms corridor (HBP 17) [canon]

The model's rooms with no number (page/castle-model.js, version 25)

the room next to the trophy room (trophy-next-room)
the third floor's corridor along the west courtyard (third-floor-north-corridor)
the passage to the Defence classroom (defence-passage)
the Defence store of dark creatures in crates (defence-store)
the Charms corridor (charms-corridor)
the passage to the Charms classroom (charms-passage)

The towers at this level

Astronomy Tower: its stair to the top
Ravenclaw Tower: its tight spiral stair (+23)
Gryffindor Tower: below the common room: the house's storerooms (ours)
West Tower: its stair; Flitwick's office on 7 (42)
North Tower: its stair; the trapdoor landing on 7 (+3)
south-west tower: a stair and staff rooms (ours)
Dumbledore's tower: the gargoyle's moving stair on 7 (41)

Cores not on this floor (a named place takes the spot)

The West Tower's stair foot, a stair between every floor: +17 takes it

This sheet's fill, every space given a use (green: canon, purple: ours)


a The North Tower's stair foot, a stair between every floor [ours: PS 8: "a hundred and forty-two staircases"] core, 8 by 6 m
b The south-west tower's stair foot, a stair between every floor [ours: PS 8: "a hundred and forty-two staircases"] core, 7 by 5 m
c Washrooms, girls' and boys' [ours] core, 7 by 6 m
d Washrooms, girls' and boys' [ours] core, 8 by 5 m
e Washrooms, girls' and boys' [ours] core, 8 by 5 m
f The Astronomy Tower's stair foot, its stair to the top [ours] core, 6 by 10 m
g A Gryffindor storeroom at the tower's foot [ours] core, 13 by 7 m
h A third years' study room [ours] south range, east, 14 by 14 m
i Staff bedrooms [ours] south range, west, 19 by 14 m
j A broom cupboard [ours] north range, 15 by 5 m
k A store of spare desks and chairs [ours] north range, 15 by 5 m
l A teacher's study [ours] south range, east, 14 by 14 m
m A linen cupboard [ours] north range, 15 by 5 m
n The Defence teacher's bedroom [ours] north range, 11 by 13 m
o Staff bedroom [ours] north range, 12 by 13 m
p Filch's cleaning cupboard [ours] north range, 17 by 5 m
q The swivelling staircase [canon: OotP 32] north range, 11 by 13 m
r A study room [ours] south range, east, 14 by 14 m
s A house-elves' linen room [ours] north range, 12 by 13 m
t A store of old textbooks [ours] north range, 19 by 5 m
u The armour gallery's repair room [ours] south range, west, 14 by 14 m
v The Charms store: cushions, teacups and pineapples [ours] north range, 12 by 13 m
w A lamp and candle cupboard [ours] north range, 17 by 5 m
x Staff bedroom [ours] south range, east, 14 by 14 m
y The Defence practice room, for jinxes and counter-jinxes [ours] north range, 13 by 13 m
z Charms classroom for the N.E.W.T. years [ours] north range, 12 by 13 m
aa The trophy room's polishing room [ours] south range, west, 14 by 14 m
ab A store [ours] north range, 19 by 5 m
ac A broom cupboard [ours] north range, 5 by 5 m
ad A disused classroom [ours] east range, 12 by 11 m
ae A teacher's study [ours] east range, 12 by 11 m
af The room beside the trophy room [ours] north range, 13 by 13 m
ag A house-elves' linen room [ours] south range, east, 14 by 14 m
ah A study room [ours] east range, 12 by 11 m
ai A store of spare desks and chairs [ours] north range, 8 by 5 m
aj A linen cupboard [ours] north range, 5 by 5 m

The castle's layout, the fourth floor

The Architect, 14 October 2026, for Godric, on the castle model, version 25. Under 1.1, 2.1, 3.1 and Q48b's 3. North up; the bar 50 m. Numbers: the step 3 sheet's places (+ the canon sweep's); letters, purple: this sheet's fill, every space given a use.

Fourth floor

floor at +20.8 m

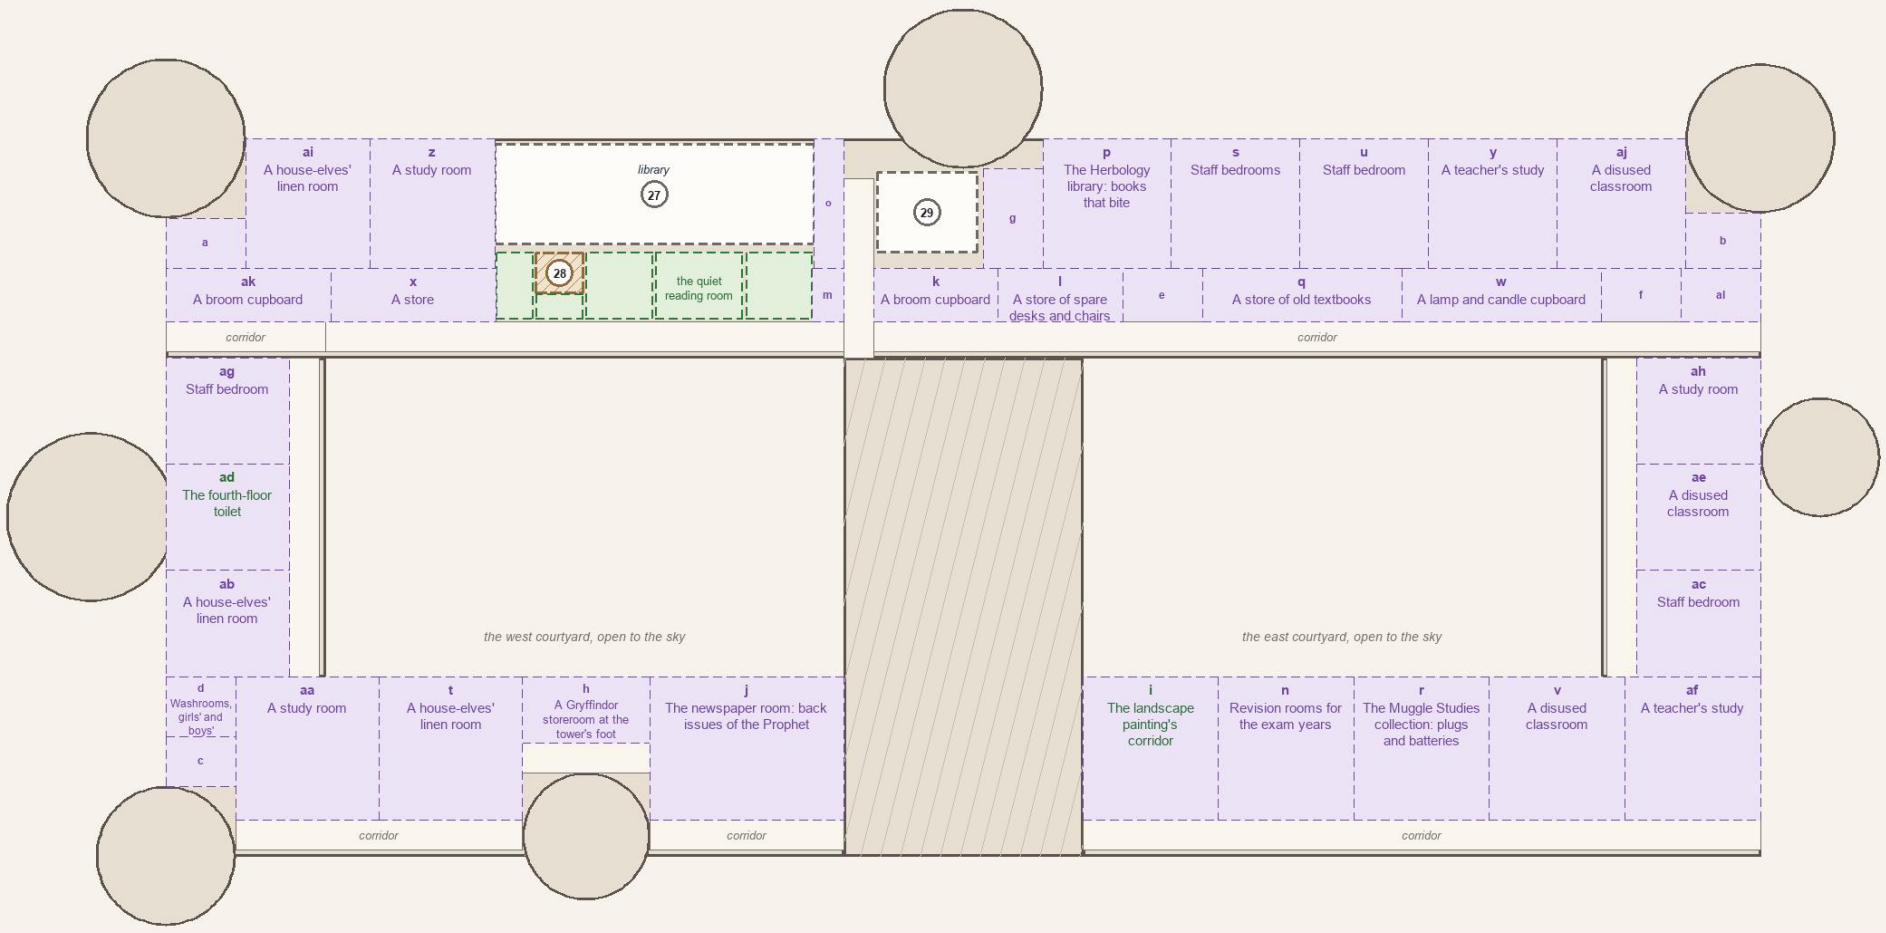

Named places on this floor (the step 3 sheet: numbers the first draft's, + the canon sweep's)

27 Library, the Restricted Section at the back [proposed] (PS 12)
28 The Muggle Studies room, past the last stack (Magic) [designed]
29 The unused classroom with the Mirror of Erised, near the library [proposed] (PS 12)
30 The passage behind the mirror, fourth floor, caved in [inferred] (PoA 10, OotP 17)

The model's rooms with no number (page/castle-model.js, version 25)

the fourth floor's corridor along the west courtyard (fourth-floor-corridor)
the corridor to the library (library-corridor)
Madam Pince's office and book-mending room (pince-office)
the quiet reading room (library-reading-room)
the library's map and atlas room (library-map-room)
the Muggle Studies collection's store (muggle-studies-store)
the Muggle Studies teacher's study (muggle-studies-study)

The towers at this level

Astronomy Tower: its stair to the top
Ravenclaw Tower: its tight spiral stair (+23)
Gryffindor Tower: below the common room: the house's storerooms (ours)
West Tower: its stair; Flitwick's office on 7 (42)
North Tower: its stair; the trapdoor landing on 7 (+3)
south-west tower: a stair and staff rooms (ours)
Dumbledore's tower: the gargoyle's moving stair on 7 (41)

This sheet's fill, every space given a use (green: canon, purple: ours)


a The West Tower's stair foot, a stair between every floor [ours: PS 8: "a hundred and forty-two staircases"] core, 8 by 5 m
b The North Tower's stair foot, a stair between every floor [ours: PS 8: "a hundred and forty-two staircases"] core, 8 by 6 m
c The south-west tower's stair foot, a stair between every floor [ours: PS 8: "a hundred and forty-two staircases"] core, 7 by 5 m
d Washrooms, girls' and boys' [ours] core, 7 by 6 m
e Washrooms, girls' and boys' [ours] core, 8 by 5 m
f Washrooms, girls' and boys' [ours] core, 8 by 5 m
g The Astronomy Tower's stair foot, its stair to the top [ours] core, 6 by 10 m
h A Gryffindor storeroom at the tower's foot [ours] core, 13 by 7 m
i The landscape painting's corridor [canon: PoA 8] south range, east, 14 by 14 m
j The newspaper room: back issues of the Prophet [ours] south range, west, 19 by 14 m
k A broom cupboard [ours] north range, 12 by 5 m
l A store of spare desks and chairs [ours] north range, 12 by 5 m
m A linen cupboard [ours] north range, 3 by 5 m
n Revision rooms for the exam years [ours] south range, east, 14 by 14 m
o Filch's cleaning cupboard [ours] north range, 3 by 13 m
p The Herbology library: books that bite [ours] north range, 13 by 13 m
q A store of old textbooks [ours] north range, 20 by 5 m
r The Muggle Studies collection: plugs and batteries [ours: a nod to CoS 3] south range, east, 14 by 14 m
s Staff bedrooms [ours] north range, 13 by 13 m
t A house-elves' linen room [ours] south range, west, 14 by 14 m
u Staff bedroom [ours] north range, 13 by 13 m
v A disused classroom [ours] south range, east, 14 by 14 m
w A lamp and candle cupboard [ours] north range, 20 by 5 m
x A store [ours] north range, 17 by 5 m
y A teacher's study [ours] north range, 13 by 13 m
z A study room [ours] north range, 12 by 13 m
aa A study room [ours] south range, west, 14 by 14 m
ab A house-elves' linen room [ours] west range, 12 by 11 m
ac Staff bedroom [ours] east range, 12 by 11 m
ad The fourth-floor toilet [canon: OotP 28] west range, 12 by 11 m
ae A disused classroom [ours] east range, 12 by 11 m
af A teacher's study [ours] south range, east, 14 by 14 m
ag Staff bedroom [ours] west range, 12 by 11 m
ah A study room [ours] east range, 12 by 11 m
ai A house-elves' linen room [ours] north range, 12 by 13 m
aj A disused classroom [ours] north range, 13 by 13 m
ak A broom cupboard [ours] north range, 17 by 5 m
al A store of spare desks and chairs [ours] north range, 8 by 5 m

The castle's layout, the fifth floor

The Architect, 14 October 2026, for Godric, on the castle model, version 25. Under 1.1, 2.1, 3.1 and Q48b's 3. North up; the bar 50 m. Numbers: the step 3 sheet's places (+ the canon sweep's); letters, purple: this sheet's fill, every space given a use.

Fifth floor

floor at +26.0 m

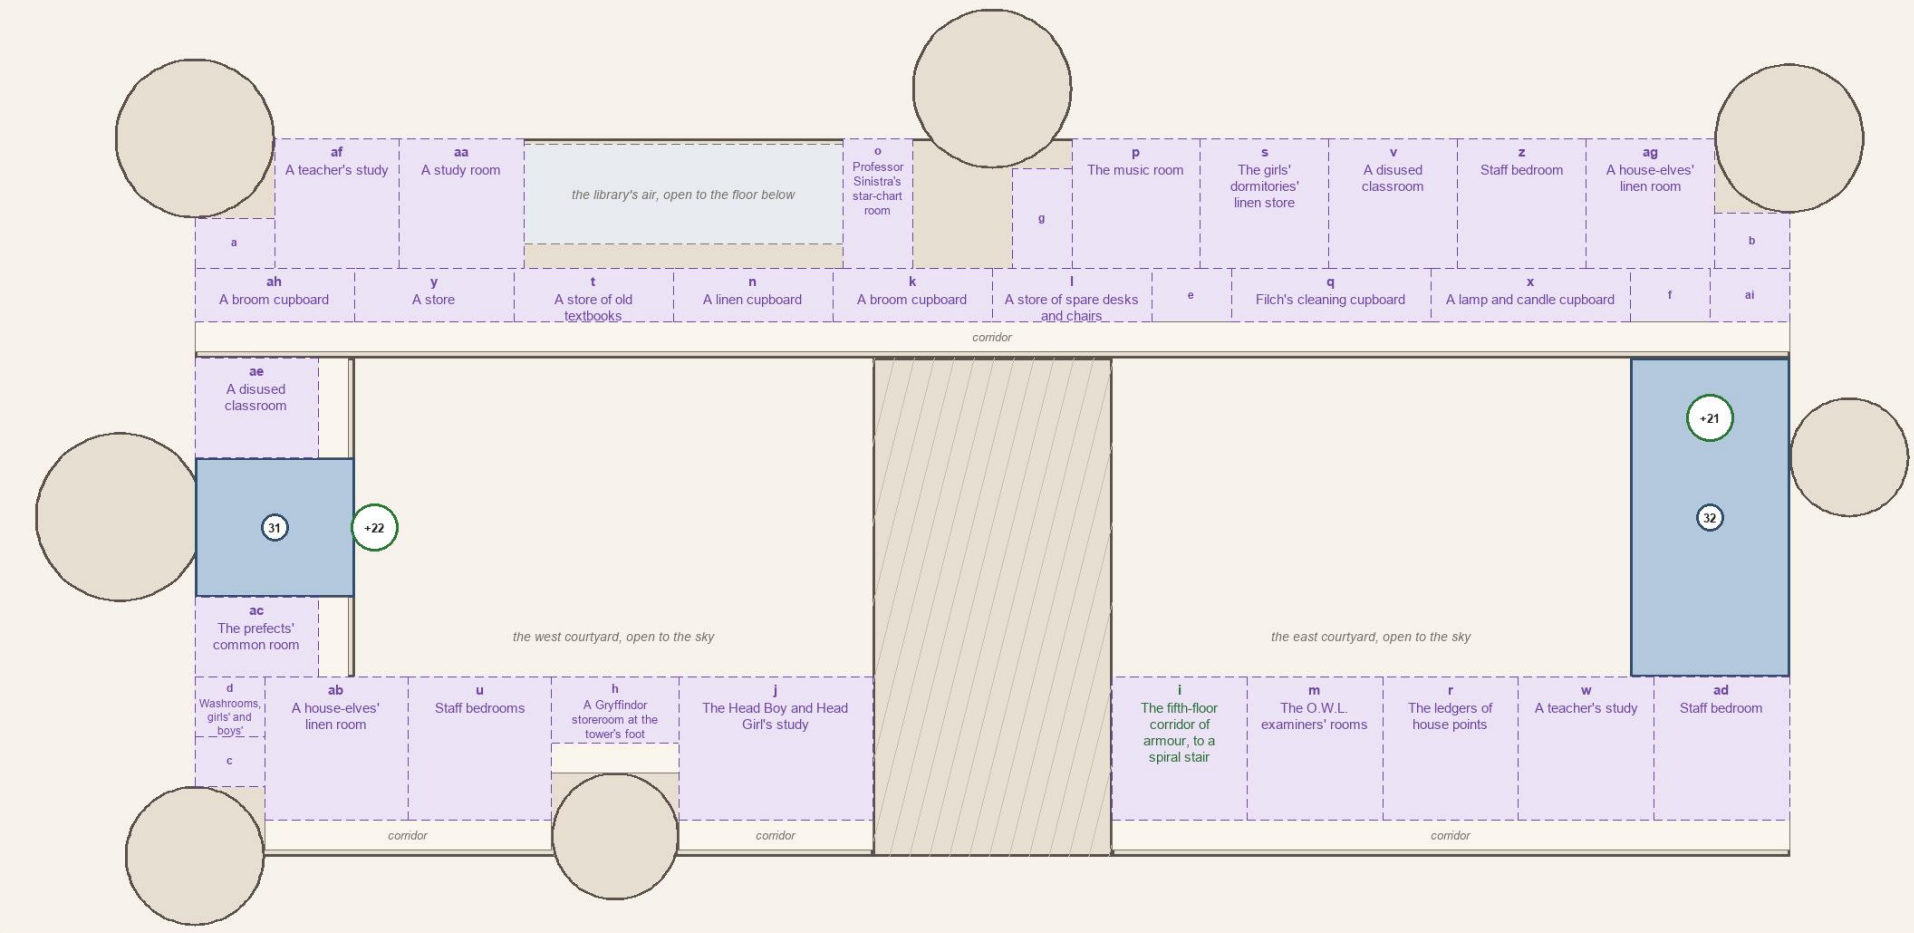

0 10 20 30 40 50 m

N

Named places on this floor (the step 3 sheet: numbers the first draft's, + the canon sweep's)

31 Prefects' bathroom, by Boris the Bewildered (the spot proposed) [books] (GoF 23)
32 The east wing, named on the fifth floor [books] (OotP 30)
+22 Boris the Bewildered; the fourth door to his left (GoF 23, 25) [canon]
+21 Gregory the Smarmy's corridor, the east wing (OotP 29, 30) [canon]

Open to the floor below (a hall or room rising through this storey)

the library's air, 32 by 10 m

The towers at this level

Astronomy Tower: its stair to the top
Ravenclaw Tower: its tight spiral stair (+23)
Gryffindor Tower: below the common room: the house's storerooms (ours)
West Tower: its stair; Flitwick's office on 7 (42)
North Tower: its stair; the trapdoor landing on 7 (+3)
south-west tower: a stair and staff rooms (ours)
Dumbledore's tower: the gargoyle's moving stair on 7 (41)

This sheet's fill, every space given a use (green: canon, purple: ours)


a The West Tower's stair foot, a stair between every floor [ours: PS 8: "a hundred and forty-two staircases"] core, 8 by 5 m
b The North Tower's stair foot, a stair between every floor [ours: PS 8: "a hundred and forty-two staircases"] core, 8 by 6 m
c The south-west tower's stair foot, a stair between every floor [ours: PS 8: "a hundred and forty-two staircases"] core, 7 by 5 m
d Washrooms, girls' and boys' [ours] core, 7 by 6 m
e Washrooms, girls' and boys' [ours] core, 8 by 5 m
f Washrooms, girls' and boys' [ours] core, 8 by 5 m
g The Astronomy Tower's stair foot, its stair to the top [ours] core, 6 by 10 m
h A Gryffindor storeroom at the tower's foot [ours] core, 13 by 7 m
i The fifth-floor corridor of armour, to a spiral stair [canon: DH 29] south range, east, 14 by 14 m
j The Head Boy and Head Girl's study [ours] south range, west, 19 by 14 m
k A broom cupboard [ours] north range, 16 by 5 m
l A store of spare desks and chairs [ours] north range, 16 by 5 m
m The O.W.L. examiners' rooms [ours] south range, east, 14 by 14 m
n A linen cupboard [ours] north range, 16 by 5 m
o Professor Sinistra's star-chart room [ours] north range, 7 by 13 m
p The music room [ours] north range, 13 by 13 m
q Filch's cleaning cupboard [ours] north range, 20 by 5 m
r The ledgers of house points [ours] south range, east, 14 by 14 m
s The girls' dormitories' linen store [ours] north range, 13 by 13 m
t A store of old textbooks [ours] north range, 16 by 5 m
u Staff bedrooms [ours] south range, west, 14 by 14 m
v A disused classroom [ours] north range, 13 by 13 m
w A teacher's study [ours] south range, east, 14 by 14 m
x A lamp and candle cupboard [ours] north range, 20 by 5 m
y A store [ours] north range, 16 by 5 m
z Staff bedroom [ours] north range, 13 by 13 m
aa A study room [ours] north range, 12 by 13 m
ab A house-elves' linen room [ours] south range, west, 14 by 14 m
ac The prefects' common room [ours] west range, 12 by 8 m
ad Staff bedroom [ours] south range, east, 14 by 14 m
ae A disused classroom [ours] west range, 12 by 10 m
af A teacher's study [ours] north range, 12 by 13 m
ag A house-elves' linen room [ours] north range, 13 by 13 m
ah A broom cupboard [ours] north range, 16 by 5 m
ai A store of spare desks and chairs [ours] north range, 8 by 5 m

The castle's layout, the sixth floor

The Architect, 14 October 2026, for Godric, on the castle model, version 25. Under 1.1, 2.1, 3.1 and Q48b's 3. North up; the bar 50 m. Numbers: the step 3 sheet's places (+ the canon sweep's); letters, purple: this sheet's fill, every space given a use.

Sixth floor

floor at +31.2 m

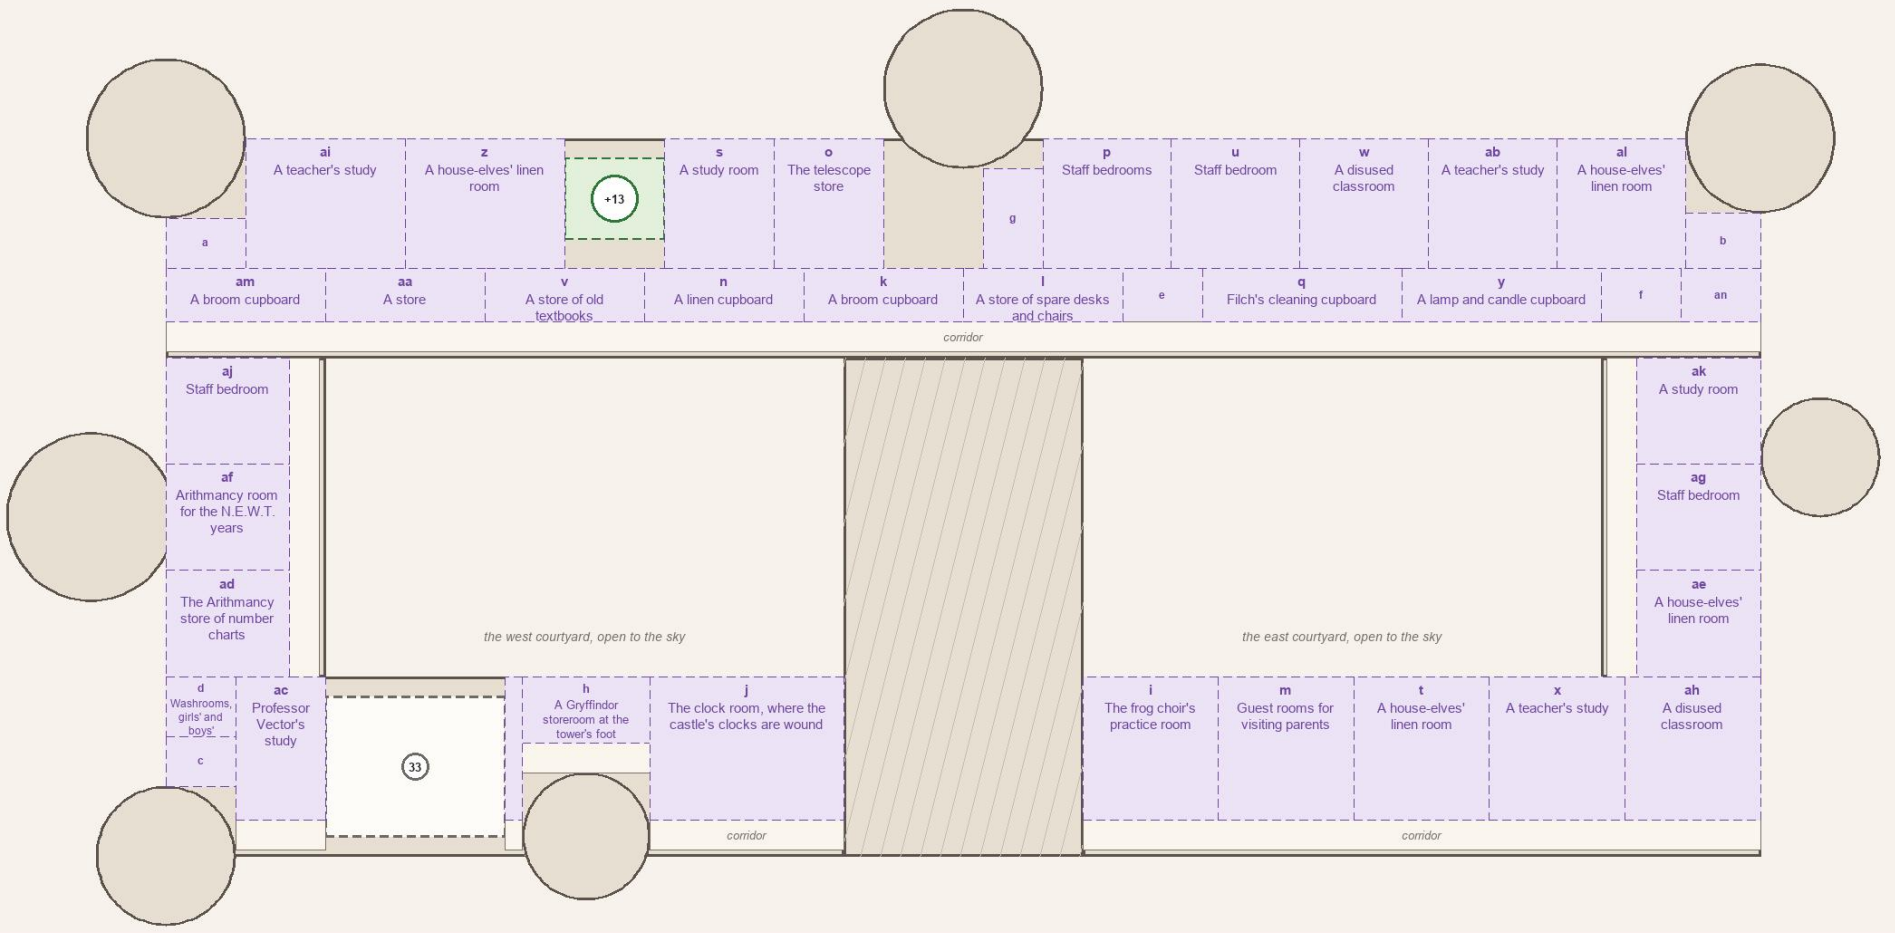

0 10 20 30 40 50 m

N

Named places on this floor (the step 3 sheet: numbers the first draft's, + the canon sweep's)

33 Arithmancy classroom (proposed) [proposed]
+13 The boys' bathroom, the floor below the Room (HBP 24) [canon]

The towers at this level

Astronomy Tower: its stair to the top
Ravenclaw Tower: its tight spiral stair (+23)
Gryffindor Tower: below the common room: the house's storerooms (ours)
West Tower: its stair; Flitwick's office on 7 (42)
North Tower: its stair; the trapdoor landing on 7 (+3)
south-west tower: a stair and staff rooms (ours)
Dumbledore's tower: the gargoyle's moving stair on 7 (41)


This sheet's fill, every space given a use (green: canon, purple: ours)

a The West Tower's stair foot, a stair between every floor [ours: PS 8: "a hundred and forty-two staircases"] core, 8 by 5 m
b The North Tower's stair foot, a stair between every floor [ours: PS 8: "a hundred and forty-two staircases"] core, 8 by 6 m
c The south-west tower's stair foot, a stair between every floor [ours: PS 8: "a hundred and forty-two staircases"] core, 7 by 5 m
d Washrooms, girls' and boys' [ours] core, 7 by 6 m
e Washrooms, girls' and boys' [ours] core, 8 by 5 m
f Washrooms, girls' and boys' [ours] core, 8 by 5 m
g The Astronomy Tower's stair foot, its stair to the top [ours] core, 6 by 10 m
h A Gryffindor storeroom at the tower's foot [ours] core, 13 by 7 m
i The frog choir's practice room [ours] south range, east, 14 by 14 m
j The clock room, where the castle's clocks are wound [ours] south range, west, 19 by 14 m
k A broom cupboard [ours] north range, 16 by 5 m
l A store of spare desks and chairs [ours] north range, 16 by 5 m
m Guest rooms for visiting parents [ours] south range, east, 14 by 14 m
n A linen cupboard [ours] north range, 16 by 5 m
o The telescope store [ours] north range, 11 by 13 m
p Staff bedrooms [ours] north range, 13 by 13 m
q Filch's cleaning cupboard [ours] north range, 20 by 5 m
r A service passage [ours] south range, west, 2 by 14 m
s A study room [ours] north range, 11 by 13 m
t A house-elves' linen room [ours] south range, east, 14 by 14 m
u Staff bedroom [ours] north range, 13 by 13 m
v A store of old textbooks [ours] north range, 16 by 5 m
w A disused classroom [ours] north range, 13 by 13 m
x A teacher's study [ours] south range, east, 14 by 14 m
y A lamp and candle cupboard [ours] north range, 20 by 5 m
z A house-elves' linen room [ours] north range, 16 by 13 m
aa A store [ours] north range, 16 by 5 m
ab A teacher's study [ours] north range, 13 by 13 m
ac Professor Vector's study [ours: Arithmancy's teacher canon] south range, west, 9 by 14 m
ad The Arithmancy store of number charts [ours] west range, 12 by 11 m
ae A house-elves' linen room [ours] east range, 12 by 11 m
af Arithmancy room for the N.E.W.T. years [ours] west range, 12 by 11 m
ag Staff bedroom [ours] east range, 12 by 11 m
ah A disused classroom [ours] south range, east, 14 by 14 m
ai A teacher's study [ours] north range, 16 by 13 m
aj Staff bedroom [ours] west range, 12 by 11 m
ak A study room [ours] east range, 12 by 11 m
al A house-elves' linen room [ours] north range, 13 by 13 m
am A broom cupboard [ours] north range, 16 by 5 m
an A store of spare desks and chairs [ours] north range, 8 by 5 m

The castle's layout, the seventh floor

The Architect, 14 October 2026, for Godric, on the castle model, version 25. Under 1.1, 2.1, 3.1 and Q48b's 3. North up; the bar 50 m. Numbers: the step 3 sheet's places (+ the canon sweep's); letters, purple: this sheet's fill, every space given a use.

Seventh floor: the built suite at true size, in place

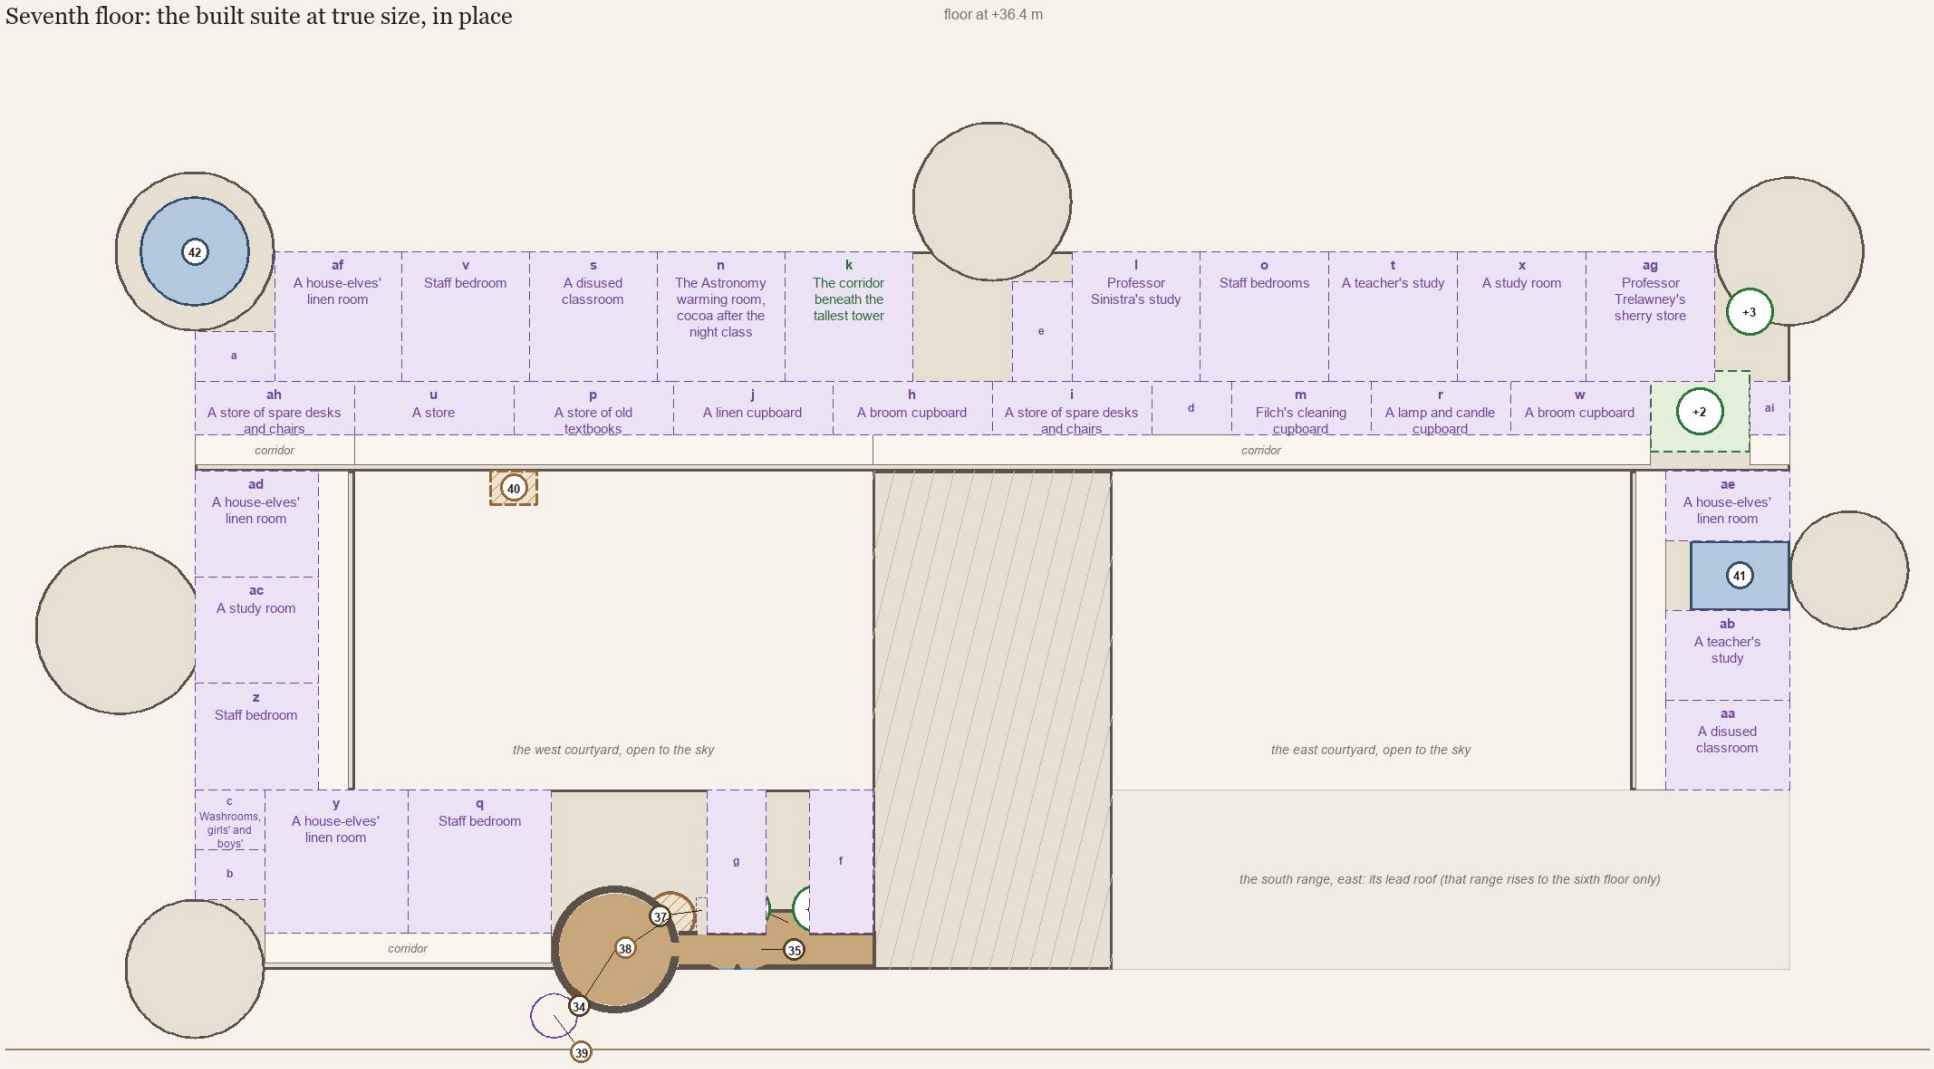

Named places on this floor (the step 3 sheet: numbers the first draft's, + the canon sweep's)

34 Gryffindor common room [built] (PS 9)
35 The Fat Lady's corridor [built] (PS 7, OotP 13)
36 The inglenook, where visitors wait [built]
37 The polite door (built) and the room of lost things behind it, bigger inside (designed) [built]
38 Clementine's study [designed]
39 The little door at the stair's foot (built in grey) and the den behind it [designed]
40 Room of Requirement on its own seventh-floor corridor (Q48b's option 3 [designed] (OotP 18, HBP 24)
41 Dumbledore's corridor and the lone gargoyle, round the other side of the castle from the Room (HBP 21, HBP 10) [books] (HBP 25)
42 Flitwick's office, seventh floor of the West Tower [books] (PoA 21)
+2 Sir Cadogan's landing, at the top of the seventh long stair (PoA 6, 14) [canon]
+3 The North Tower stair and the trapdoor landing (PoA 6, 16) [canon]
+14 Lachlan the Lanky, at the stair head, turning right (OotP 13) [canon]
+20 Paracelsus halfway down the passage; Wilfred the Wistful (OotP 14) [canon]

The model's rooms with no number (page/castle-model.js, version 25)

the Room's corridor (room-corridor)

The towers at this level

Astronomy Tower: its stair to the top
Ravenclaw Tower: its tight spiral stair (+23)
Gryffindor Tower: below the common room: the house's storerooms (ours)
West Tower: its stair; Flitwick's office on 7 (42)
North Tower: its stair; the trapdoor landing on 7 (+3)
south-west tower: a stair and staff rooms (ours)
Dumbledore's tower: the gargoyle's moving stair on 7 (41)

Cores not on this floor (a named place takes the spot)

The North Tower's stair foot, a stair between every floor: +2 takes it
Washrooms, girls' and boys': +2 takes it

This sheet's fill, every space given a use (green: canon, purple: ours)


a The West Tower's stair foot, a stair between every floor [ours: PS 8: "a hundred and forty-two staircases"] core, 8 by 5 m
b The south-west tower's stair foot, a stair between every floor [ours: PS 8: "a hundred and forty-two staircases"] core, 7 by 5 m
c Washrooms, girls' and boys' [ours] core, 7 by 6 m
d Washrooms, girls' and boys' [ours] core, 8 by 5 m
e The Astronomy Tower's stair foot, its stair to the top [ours] core, 6 by 10 m
f The Headmaster's guest rooms [ours] south range, west, 6 by 14 m
g The seventh-floor broom cupboard [ours] south range, west, 6 by 14 m
h A broom cupboard [ours] north range, 16 by 5 m
i A store of spare desks and chairs [ours] north range, 16 by 5 m
j A linen cupboard [ours] north range, 16 by 5 m
k The corridor beneath the tallest tower [canon: PS 14] north range, 13 by 13 m
l Professor Sinistra's study [ours] north range, 13 by 13 m
m Filch's cleaning cupboard [ours] north range, 14 by 5 m
n The Astronomy warming room, cocoa after the night class [ours] north range, 13 by 13 m
o Staff bedrooms [ours] north range, 13 by 13 m
p A store of old textbooks [ours] north range, 16 by 5 m
q Staff bedroom [ours] south range, west, 14 by 14 m
r A lamp and candle cupboard [ours] north range, 14 by 5 m
s A disused classroom [ours] north range, 13 by 13 m
t A teacher's study [ours] north range, 13 by 13 m
u A store [ours] north range, 16 by 5 m
v Staff bedroom [ours] north range, 13 by 13 m
w A broom cupboard [ours] north range, 14 by 5 m
x A study room [ours] north range, 13 by 13 m
y A house-elves' linen room [ours] south range, west, 14 by 14 m
z Staff bedroom [ours] west range, 12 by 11 m
aa A disused classroom [ours] east range, 12 by 9 m
ab A teacher's study [ours] east range, 12 by 9 m
ac A study room [ours] west range, 12 by 11 m
ad A house-elves' linen room [ours] west range, 12 by 11 m
ae A house-elves' linen room [ours] east range, 12 by 7 m
af A house-elves' linen room [ours] north range, 13 by 13 m
ag Professor Trelawney's sherry store [ours: a nod to HBP 25] north range, 13 by 13 m
ah A store of spare desks and chairs [ours] north range, 16 by 5 m
ai A linen cupboard [ours] north range, 4 by 5 m

The castle's layout, the tower tops

The Architect, 14 October 2026, for Godric, on the castle model, version 25. Under 1.1, 2.1, 3.1 and Q48b's 3. North up; the bar 50 m. Numbers: the step 3 sheet's places (+ the canon sweep's); letters, purple: this sheet's fill, every space given a use.

Above the seventh: the tower tops

the dormitory at +64.2 m

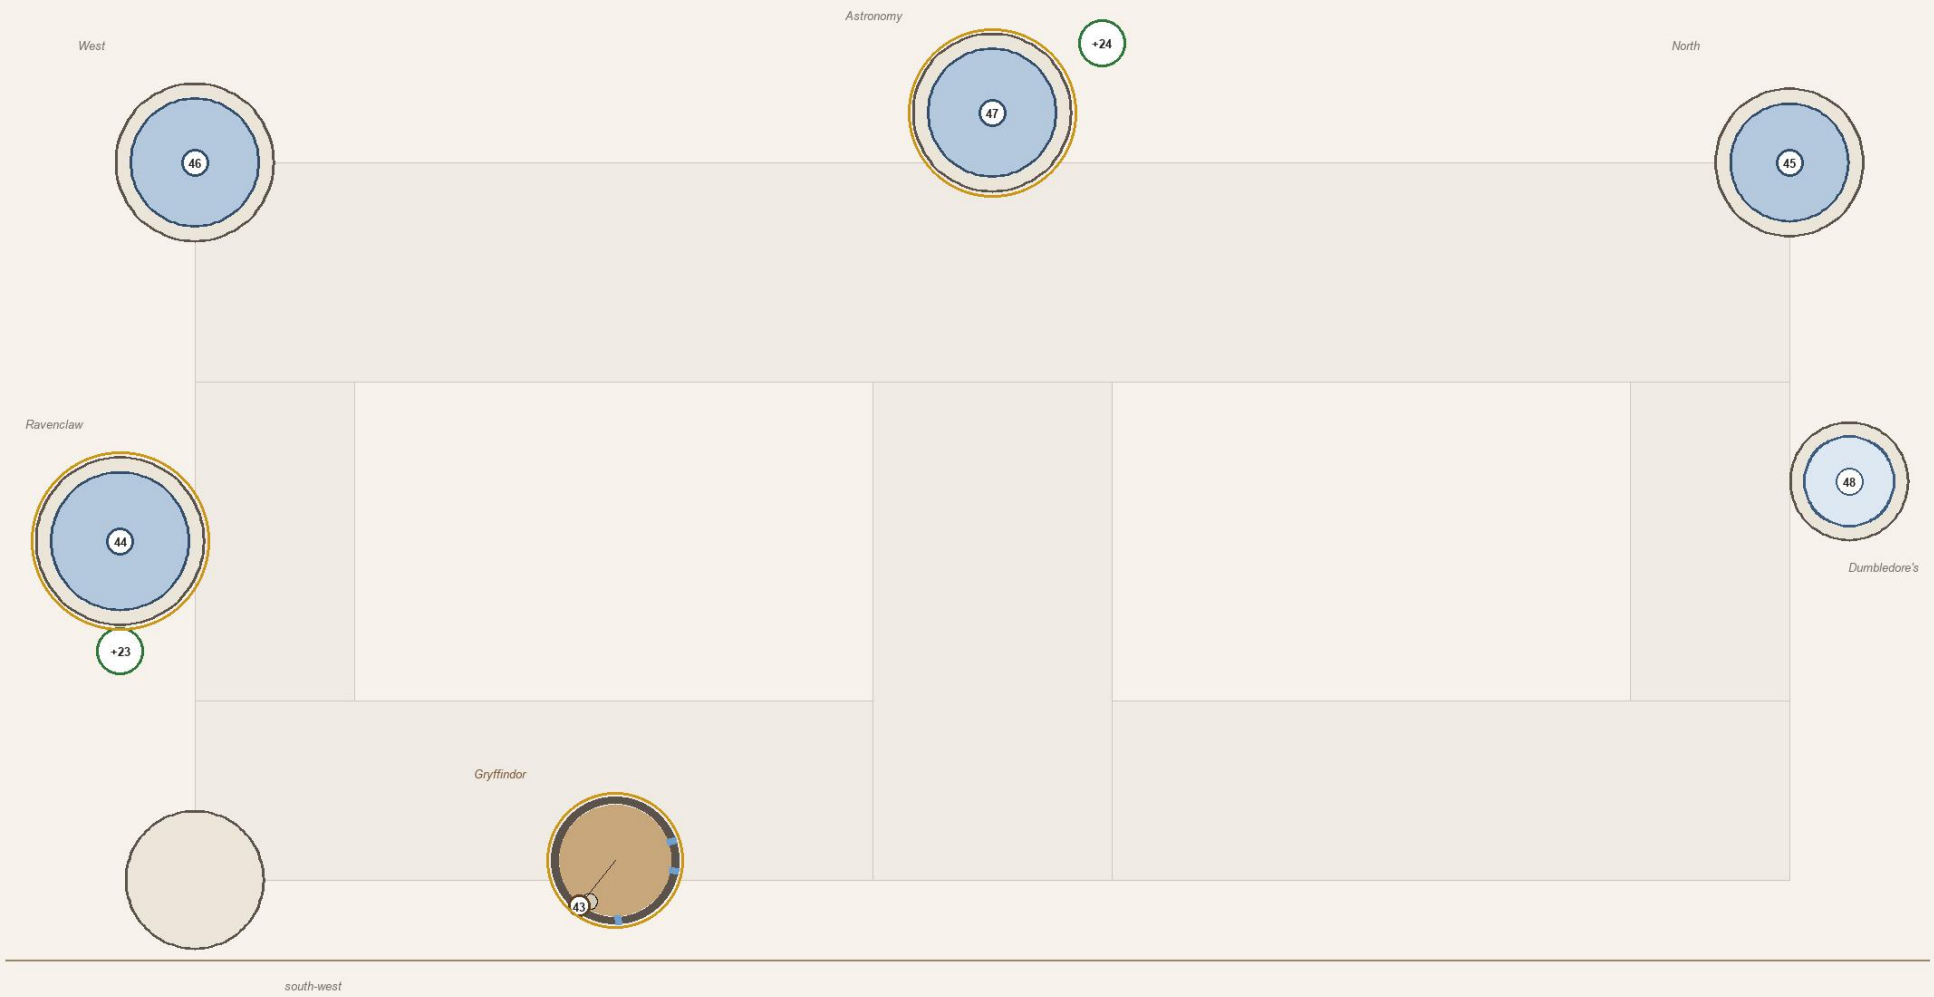





Named places on this floor (the step 3 sheet: numbers the first draft's, + the canon sweep's)

43 Gryffindor dormitory, 7.4 m above the common room [built] (PS 7)
44 Ravenclaw common room [books] (OotP 18, DH 29)
45 Divination, the top of the North Tower [books] (PoA 6, GoF 13)
46 The Owlery, the top of the West Tower [books] (GoF 15)
47 Astronomy Tower, the tallest, directly above the front doors [books] (PS 15, OotP 31)
48 Dumbledore's office [inferred] (CoS 12)
+24 The Astronomy Tower's ramparts, the parapet over the doors (HBP 27, OotP 31) [canon]
+23 Ravenclaw's tight spiral stair and the eagle door (DH 29) [canon]

The towers at this level

Astronomy Tower: the Astronomy classroom and ramparts (47, +24)
Ravenclaw Tower: Ravenclaw common room and dormitories (44)
Gryffindor Tower: the dormitories (43)
West Tower: the Owlery (46)
North Tower: Divination, through the trapdoor (45)
south-west tower: a lookout over the lake (ours)
Dumbledore's tower: the Headmaster's office (48)