
Hogwarts in section and elevation: the base design

The Architect, 15 October 2026, for Godric. Drawn from the castle model (version 28) and the layout drawn with it. Three sections, four elevations, each 1:500 at A3.

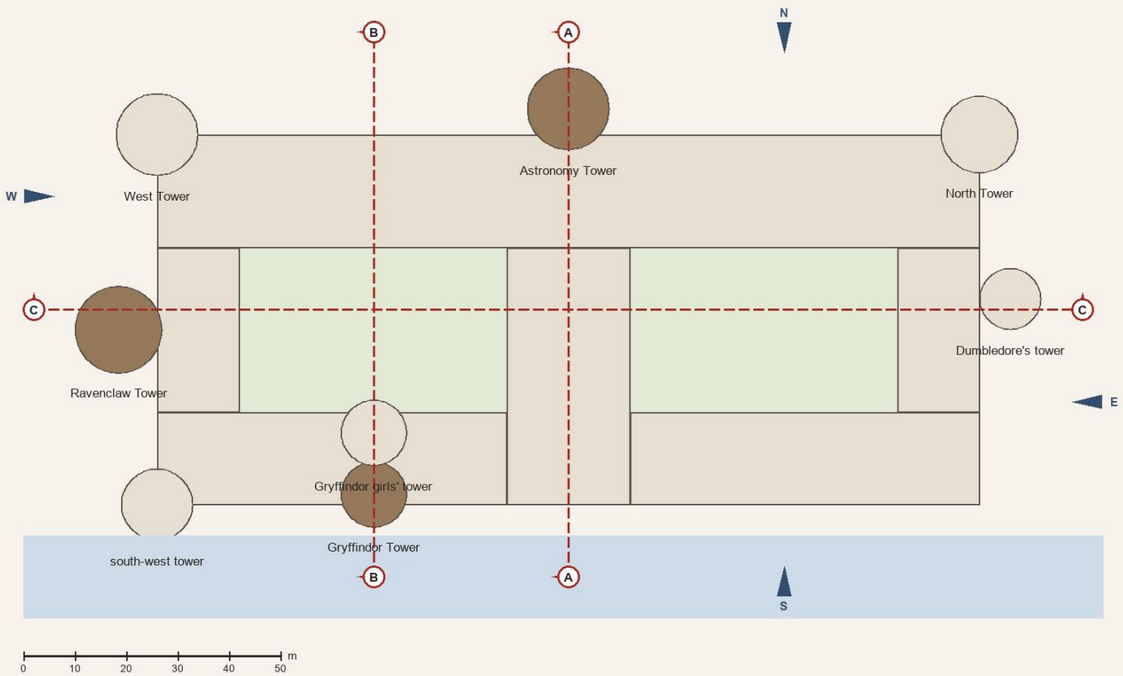

The drawings, and why each

Section A-A: through the stair hall, north to south, looking west
The castle's spine. The front doors under the Astronomy Tower, the Entrance Hall rising through two storeys, the marble staircase and the well of moving staircases up to the roof, the south face on the cliff and the lake below it.

Section B-B: through Gryffindor Tower and the Great Hall, looking west
Where the boys live, in the whole castle. The built common room and dormitory at the top of their tower, the Great Hall and the kitchens under it, the library on 4, the Room's corridor on 7 with the Room beyond, and the Slytherin common room deep under the lake.

Section C-C: across the two courtyards, west to east, looking north
The castle's width. Ravenclaw Tower and the west range (Potions, the trophy room, the prefects' bathroom), the two courtyards open to the sky, the stair hall's well, the east range (the hospital wing, the forbidden corridor, Dumbledore's corridor) and his tower; the north range's courtyard face beyond, with the Room's bay on 7.

The south elevation: from the lake
The view the boys see first, from the boats (PS 6): the cliff, the south ranges and the stair hall's face, Gryffindor Tower standing proud at the west end with the corridor's windows, the high towers behind.

The north elevation: the entrance front
The front doors under the Astronomy Tower, the highest tower, the Great Hall's high windows, the West Tower and the North Tower at the corners.

The east elevation: from the greenhouses
Dumbledore's tower against the east range, the North Tower at the north-east corner, the cliff falling to the lake at the south end.

The west elevation: from the Quidditch side
Ravenclaw Tower against the west range, the West Tower and the south-west tower at the corners, the Owlery at the West Tower's top.


The heights

Storeys	5.2 m; cellars -5.2; the seventh floor +36.4; roofs +41.6 the model (3.1); the books give no floor count
The two halls	the Great Hall three storeys, clear 14.9; the Entrance Hall two the model (15.1); the ceiling "too high to make out" (PS 7)
Astronomy Tower	ramparts +66.0, parapet +67.2: the highest "the highest of the castle" (HBP 27), "the tallest" (PoA 16)
Ravenclaw Tower	its common room at the top, a cone to +64.0 one of "the three highest towers" (DH 31)
Gryffindor Tower	the dormitory at the top, +48.3; a cone to +60.0 built to the model; "at the top of the tower" (GoF 12)
The lower towers	West +49.0, North +58.0, Dumbledore's +57.0, south-west +55.0 the Owlery at the West Tower's top (GoF 15); Divination at the North's (PoA 6)
The cliff, the lake	the lake at -18: an 18 m cliff "high on the cliff over the lake" (CoS 5)
Slytherin's room	under the lake bed, -32, a long stair down "under the lake, so the light's all green" (DH 23)

Dashed or grey: proposed, not yet in the model (the tower tops, the lake, the roofs, the window rhythm).

Checked: the layout puts 0 rooms and 1 corridor runs in the air of the tall rooms (the two halls, the library); any found are left out here.


The south elevation, from the lake (sheet S)

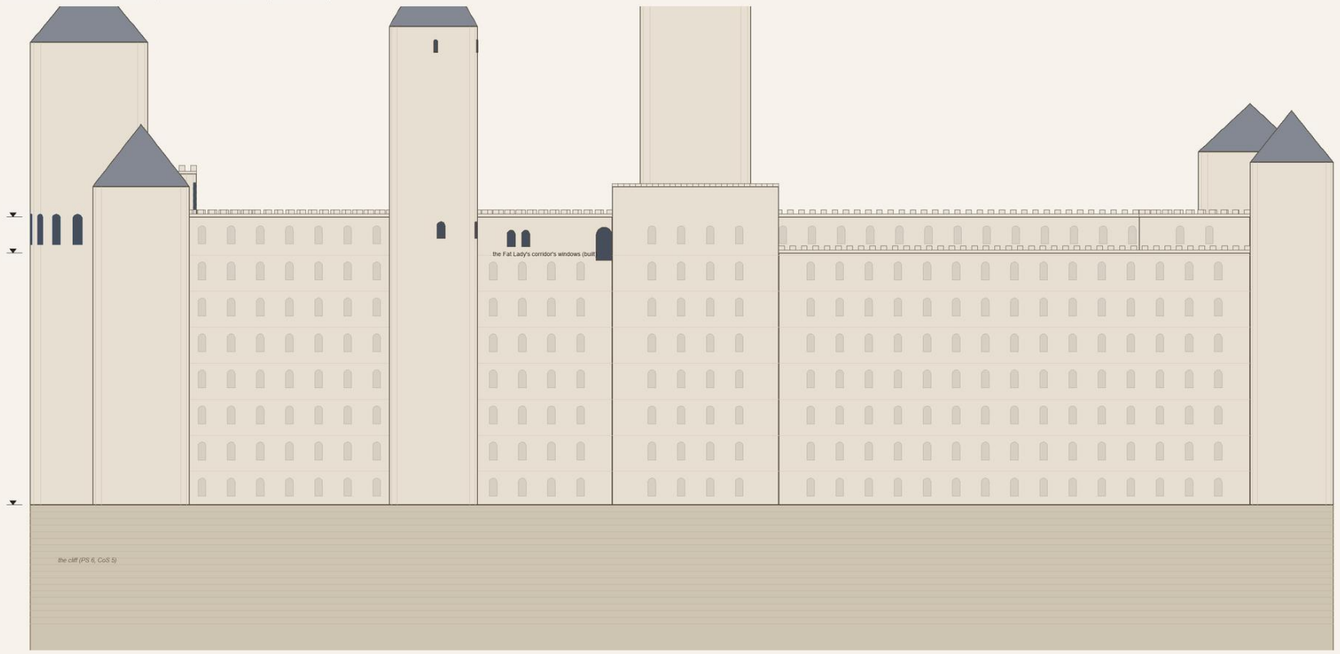


Section A-A: through the stair hall, north to south, looking west

The Architect, 15 October 2026, for Godric. The castle model, version 28, and the layout drawn with it; 1:500 at A3.

The castle's spine. The front doors under the Astronomy Tower, the Entrance Hall rising through [illegible] storeys, the marble staircase and the well of moving staircases up to the roof, the south face on the cliff and the lake [illegible] it.

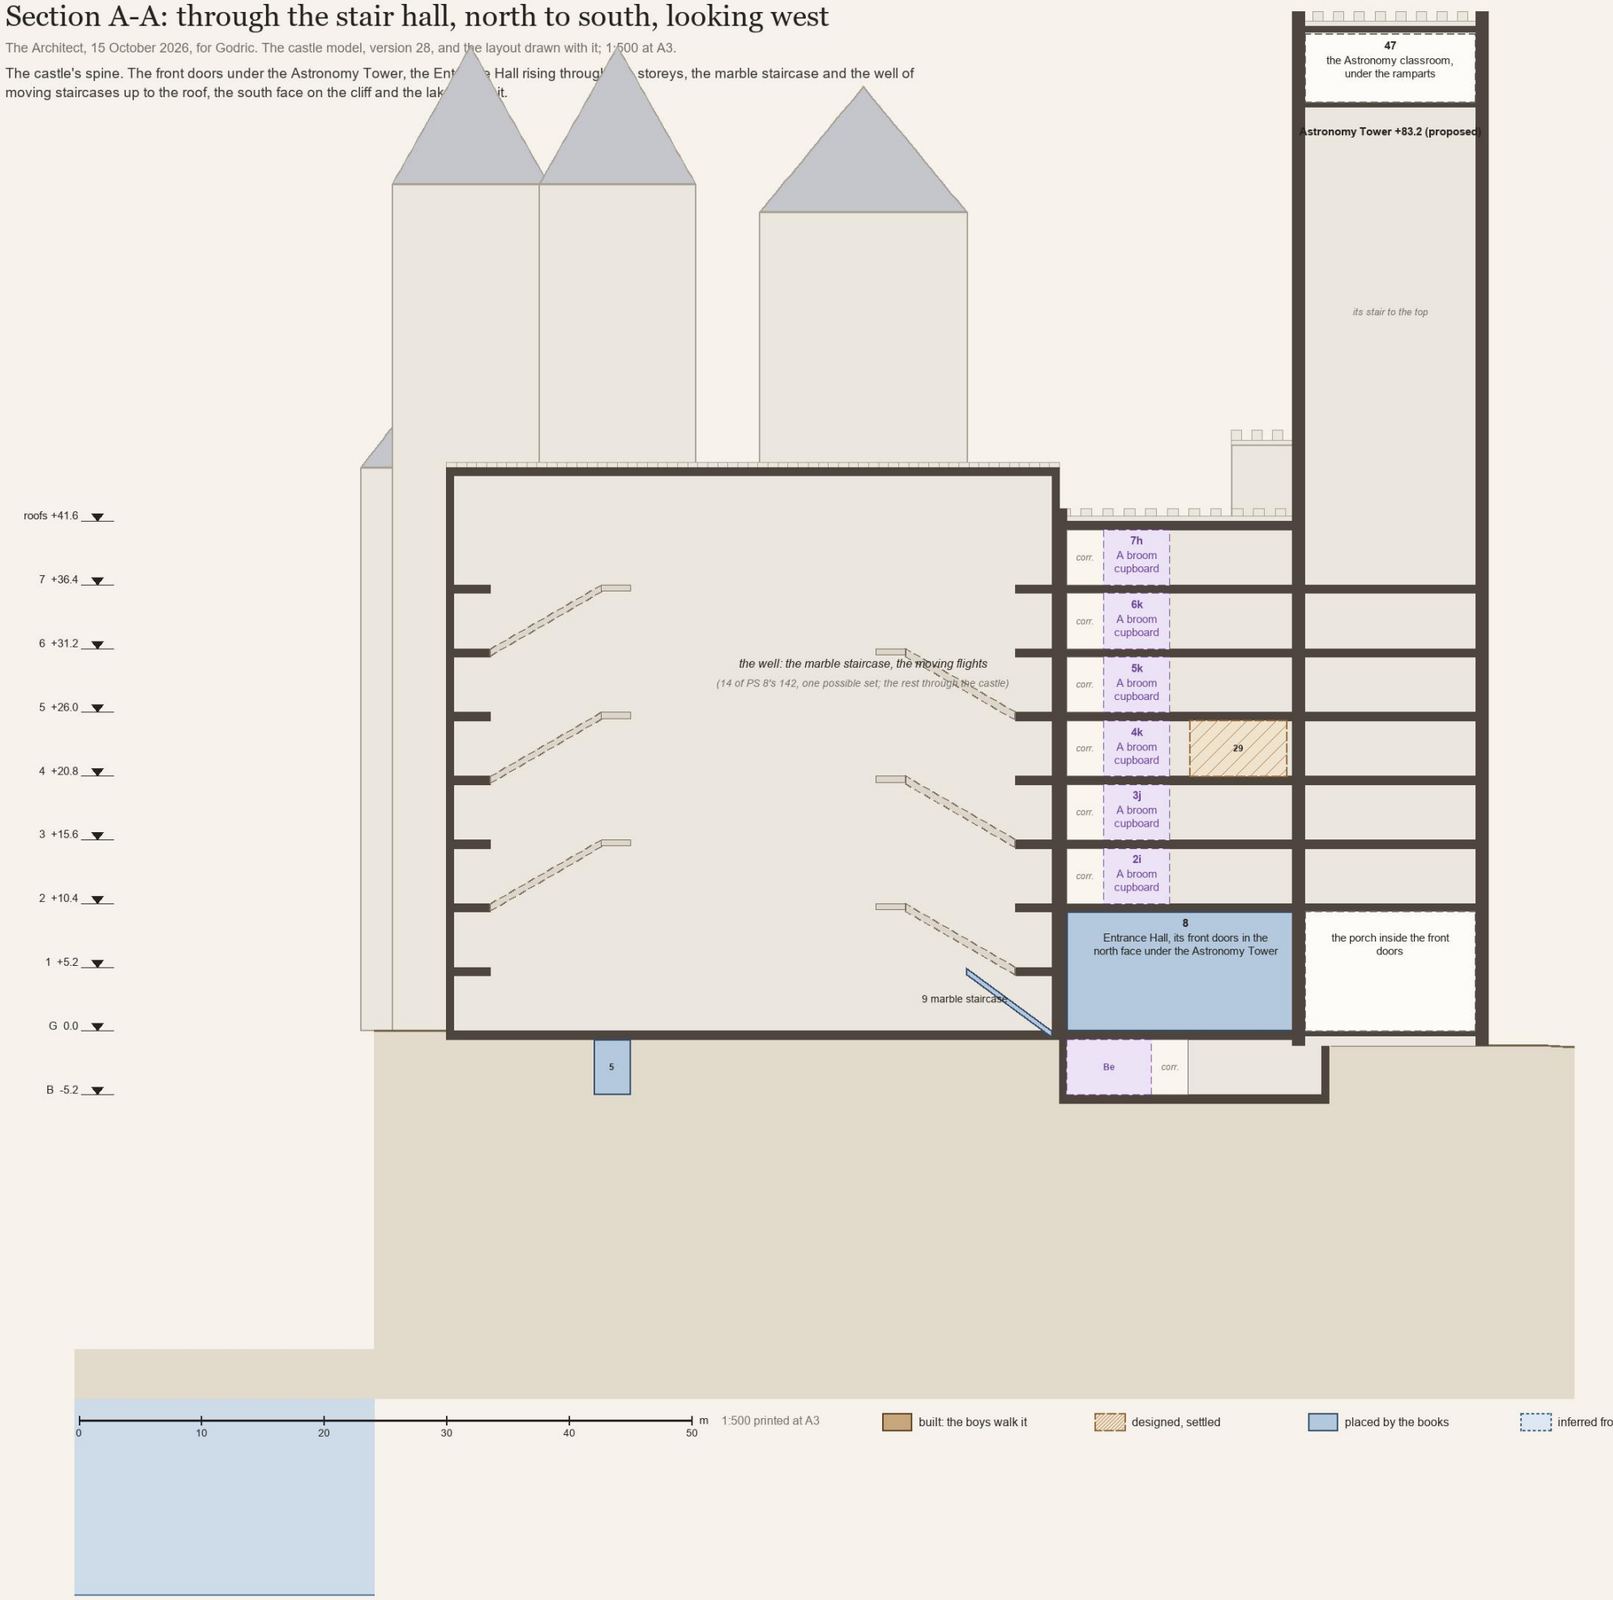

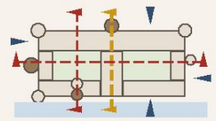

Cut, floor by floor (numbers: named places; letters: the layout's fill)

7: 7h A broom cupboard
6: 6k A broom cupboard
5: 5k A broom cupboard
4: 4k A broom cupboard; 29 The forgotten classroom, desks stacked against the walls
3: 3j A broom cupboard
2: 2i A broom cupboard
G: 8 Entrance Hall, its front doors in the north face under the Astronomy Tower
B: 5 Dungeon corridors; Be The kitchen stores: flour, sugar, the pumpkins


The towers cut


Astronomy Tower: top +83.2, proposed (the highest tower: PoA 16, HBP 27; crenellated ramparts, HBP 27; its parapet over the front doors, OotP 31)

Section B-B: through Gryffindor Tower and the Great Hall, looking west

The Architect, 15 October 2026, for Godric. The castle model, version 28, and the layout drawn with it; 1:500 at A3.

Where the boys live, in the whole castle. The built common room and dormitory at the top of the tower, the Great Hall and the kitchens under it, the library on 4, the Room's corridor on 7 with the Room beyond, and the [illegible] common room under the lake.

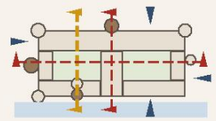

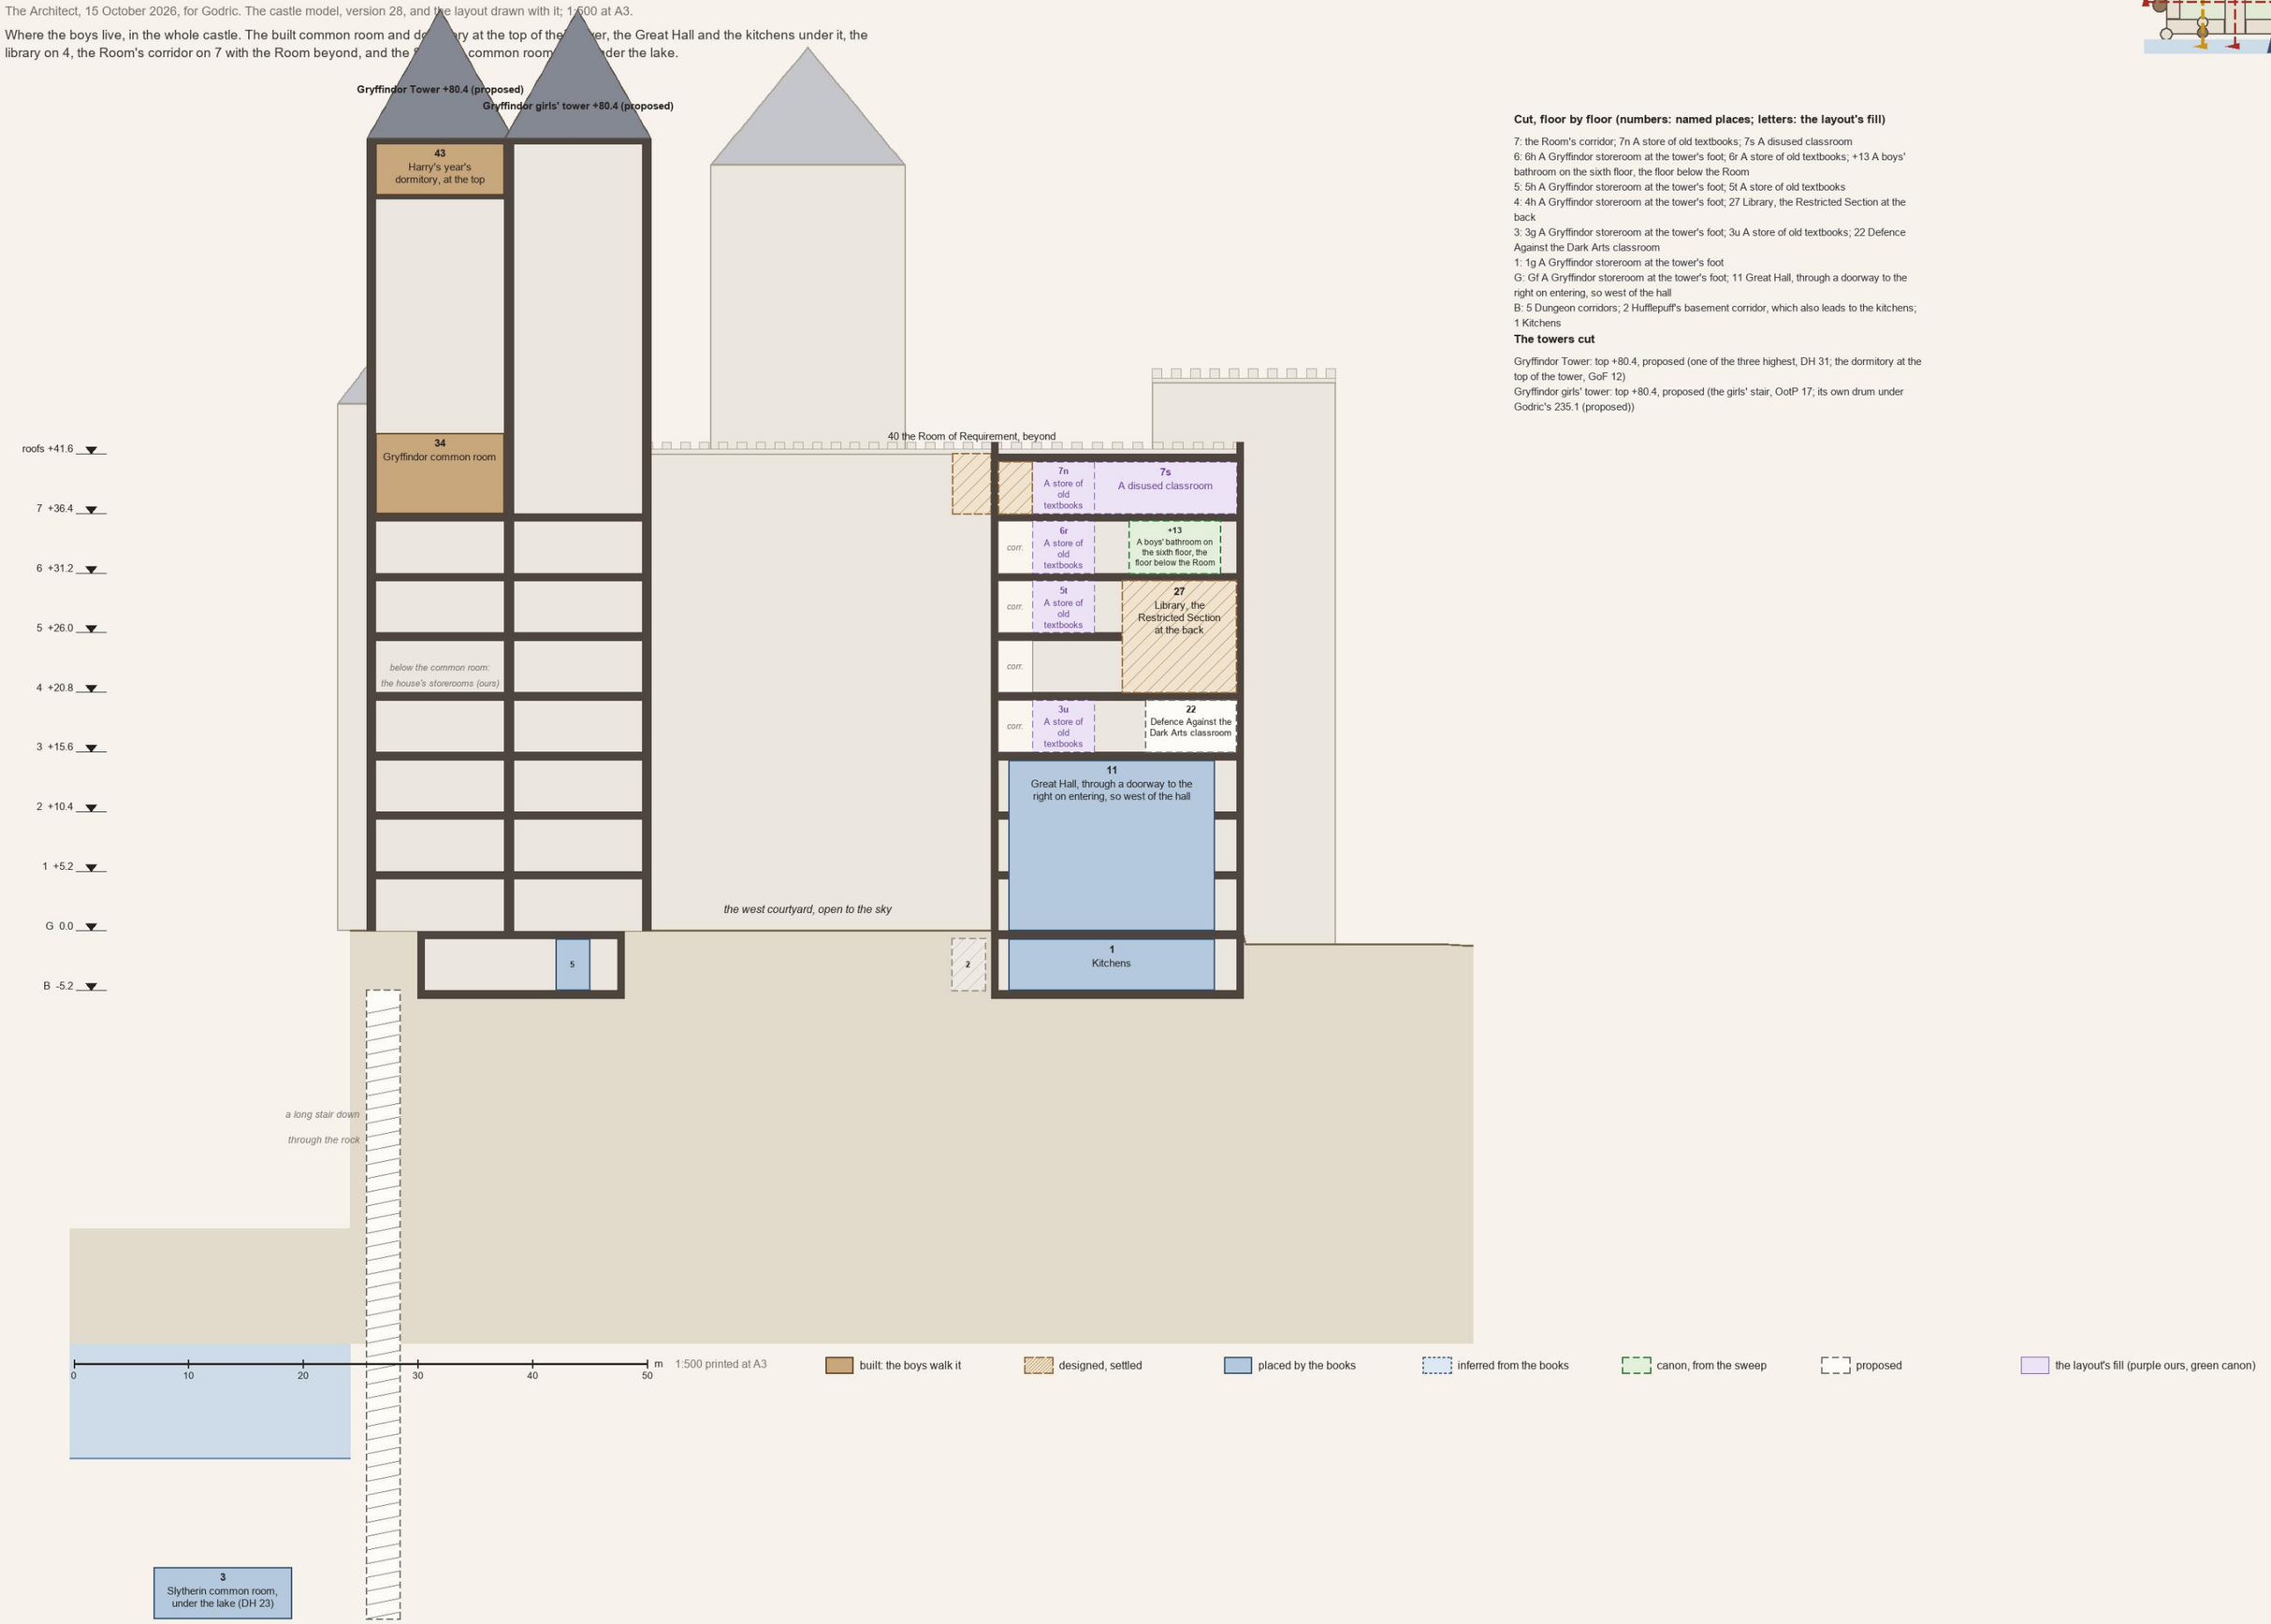

Cut, floor by floor (numbers: named places; letters: the layout's fill)

7: the Room's corridor; 7n A store of old textbooks; 7s A disused classroom
6: 6h A Gryffindor storeroom at the tower's foot; 6r A store of old textbooks; +13 A boys' bathroom on the sixth floor, the floor below the Room
5: 5h A Gryffindor storeroom at the tower's foot; 5t A store of old textbooks
4: 4h A Gryffindor storeroom at the tower's foot; 27 Library, the Restricted Section at the back
3: 3g A Gryffindor storeroom at the tower's foot; 3u A store of old textbooks; 22 Defence Against the Dark Arts classroom
1: 1g A Gryffindor storeroom at the tower's foot
G: Gf A Gryffindor storeroom at the tower's foot; 11 Great Hall, through a doorway to the right on entering, so west of the hall
B: 5 Dungeon corridors; 2 Hufflepuff's basement corridor, which also leads to the kitchens; 1 Kitchens


The towers cut


Gryffindor Tower: top +80.4, proposed (one of the three highest, DH 31; the dormitory at the top of the tower, GoF 12)
Gryffindor girls' tower: top +80.4, proposed (the girls' stair, OotP 17; its own drum under Godric's 235.1 (proposed))

Section C-C: across the two courtyards, west to east, looking north

The Architect, 15 October 2026, for Godric. The castle model, version 28, and the layout drawn with it; 1:500 at A3.

The castle's width. Ravenclaw Tower and the west range (Potions, the trophy room, the prefects' bathroom), the two courtyards open to the sky, the stair hall's well, the east range (the hospital wing, the forbidden corridor, Dumbledore's corridor) and his tower; the north range's courtyard face beyond, with the Room's bay o

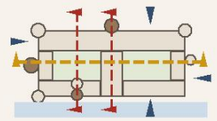


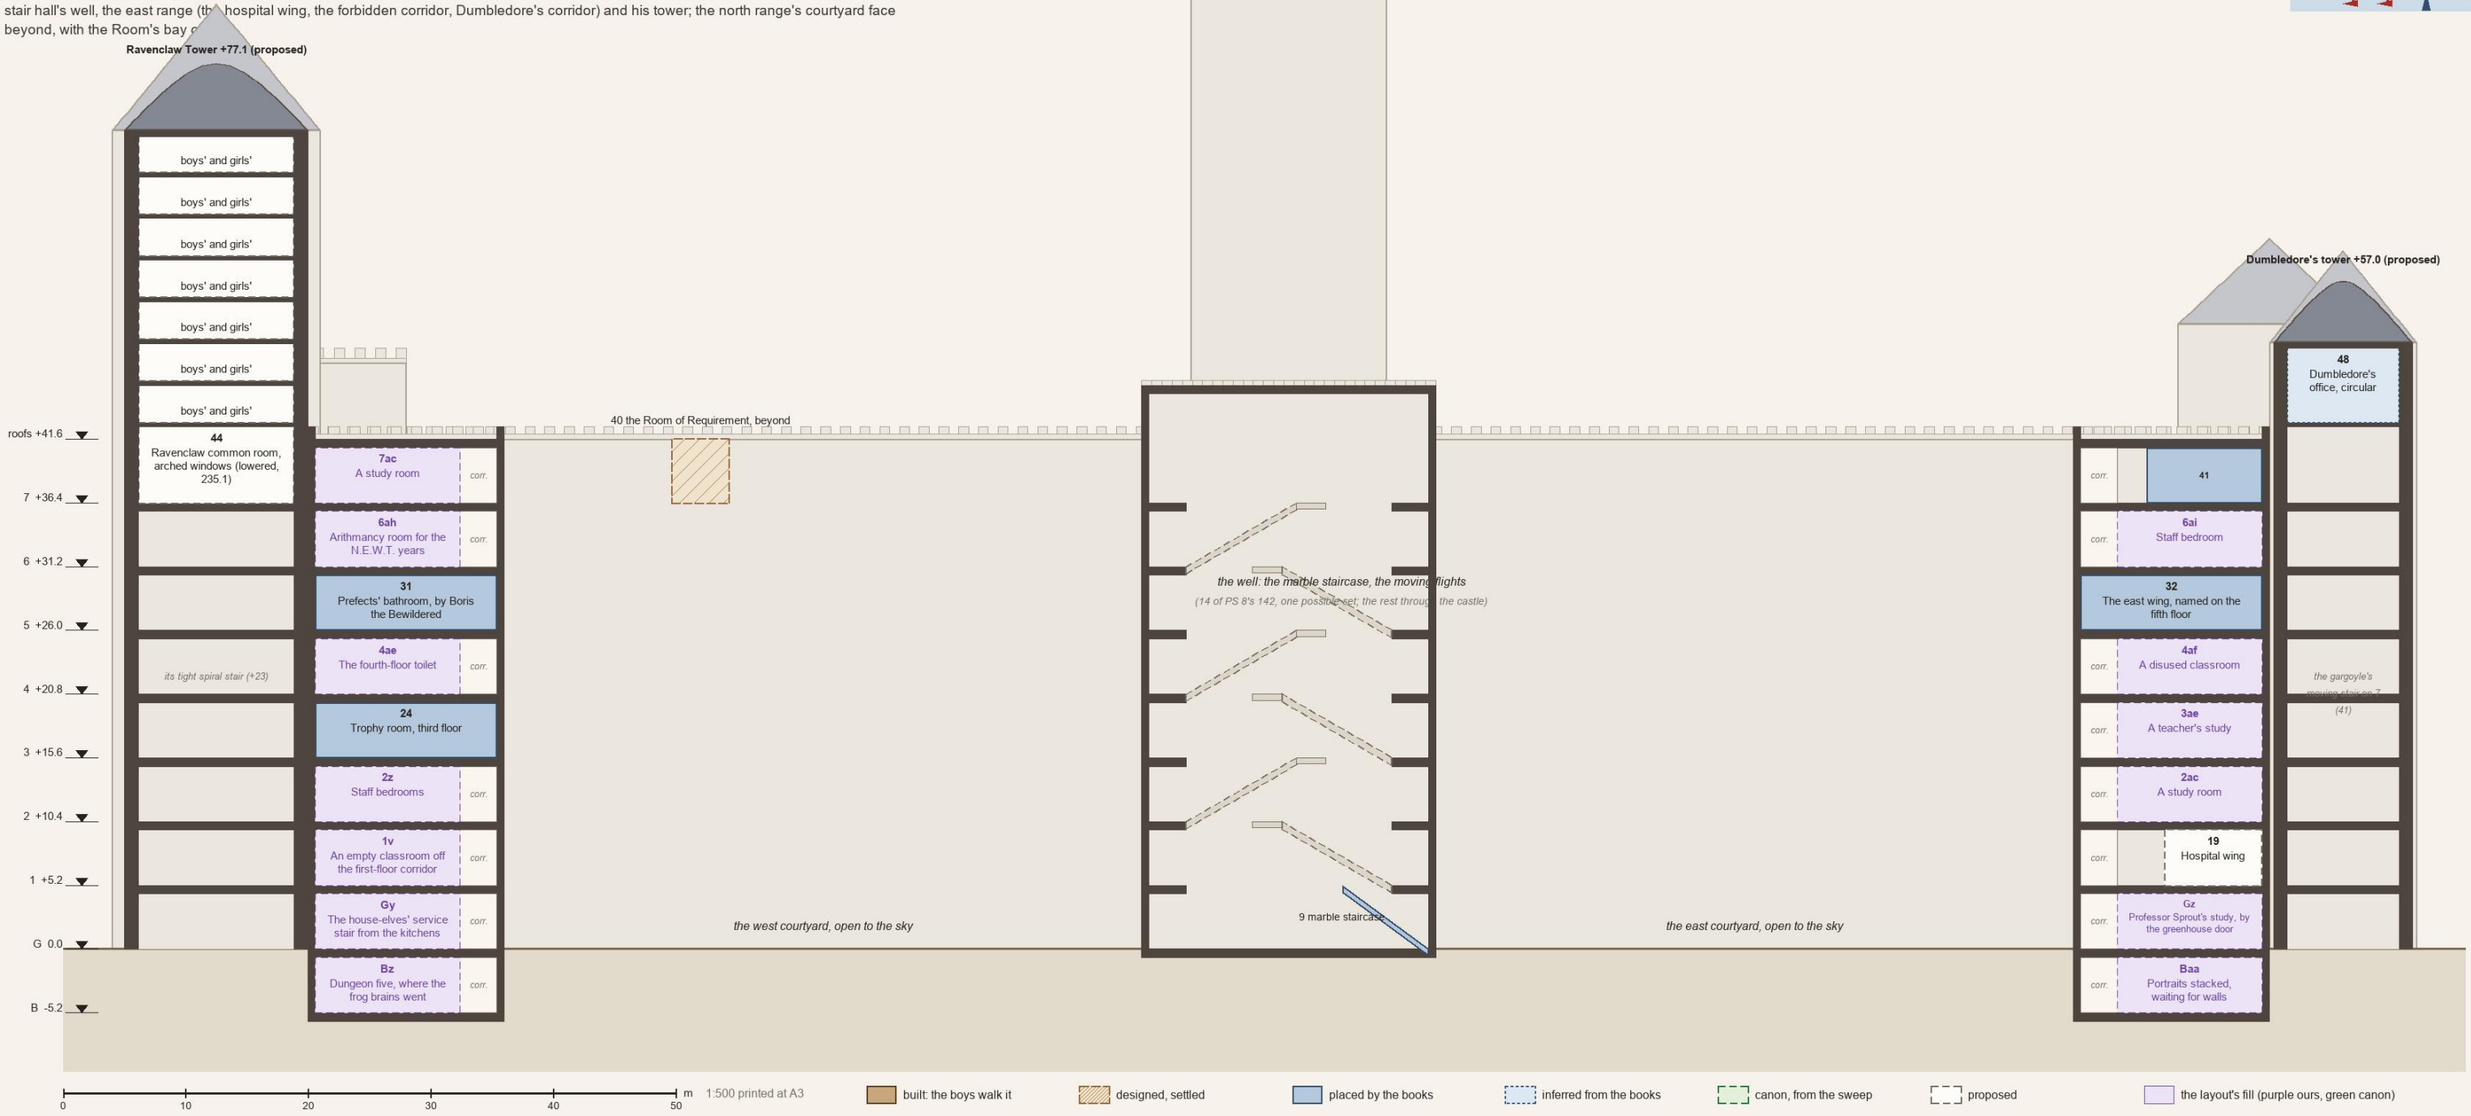

The south elevation: from the lake

The Architect, 15 October 2026, for Godric. The castle model, version 28, and the layout drawn with it; 1:500 at A3.

The view the boys see first, from the boats (PS 6): the cliff, the south ranges and the stair hall's face, Gryffindor Tower standing proud at the west end with the corridor's windows, the high towers behind.

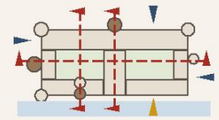

roofs +41.6

7 +36.4

G 0.0

the Fat Lady's corridor's windows (built)

the cliff (PS 6, CoS 5)

0 10 20 30 40 50 m

1:500 printed at A3

built: the boys walk it

designed, settled

placed by the books

inferred from the books

canon, from the sweep

proposed

the layout's fill (purple ours, green canon)


the wide opening in the cliff face, behind its ivy, to the underground harbour (PS 6)

the lake, +-46 (proposed)

The north elevation: the entrance front

The Architect, 15 October 2026, for Godric. The castle model, version 28, and the layout drawn with it; 1:500 at A3.

The front doors under the Astronomy Tower, the highest tower, the Great Hall's high windows, the West Tower and the North Tower at the corners.

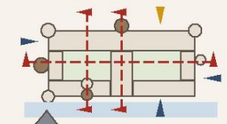

roofs +41.6

7 +36.4

G 0.0

Flitwick's window, the thirteenth from the right (PoA 21)

11 the Great Hall: its high windows (OotP 11)

the front doors, below the parapet (OotP 31)

0 10 20 30 40 50 m

1:500 printed at A3

built: the boys walk it

designed, settled

placed by the books

inferred from the books

canon, from the sweep


proposed


the layout's fill (purple ours, green canon)

The east elevation: from the greenhouses

The Architect, 15 October 2026, for Godric. The castle model, version 28, and the layout drawn with it; 1:500 at A3.

Dumbledore's tower against the east range, the North Tower at the north-east corner, the cliff face to the lake at the south end.

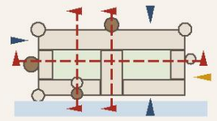


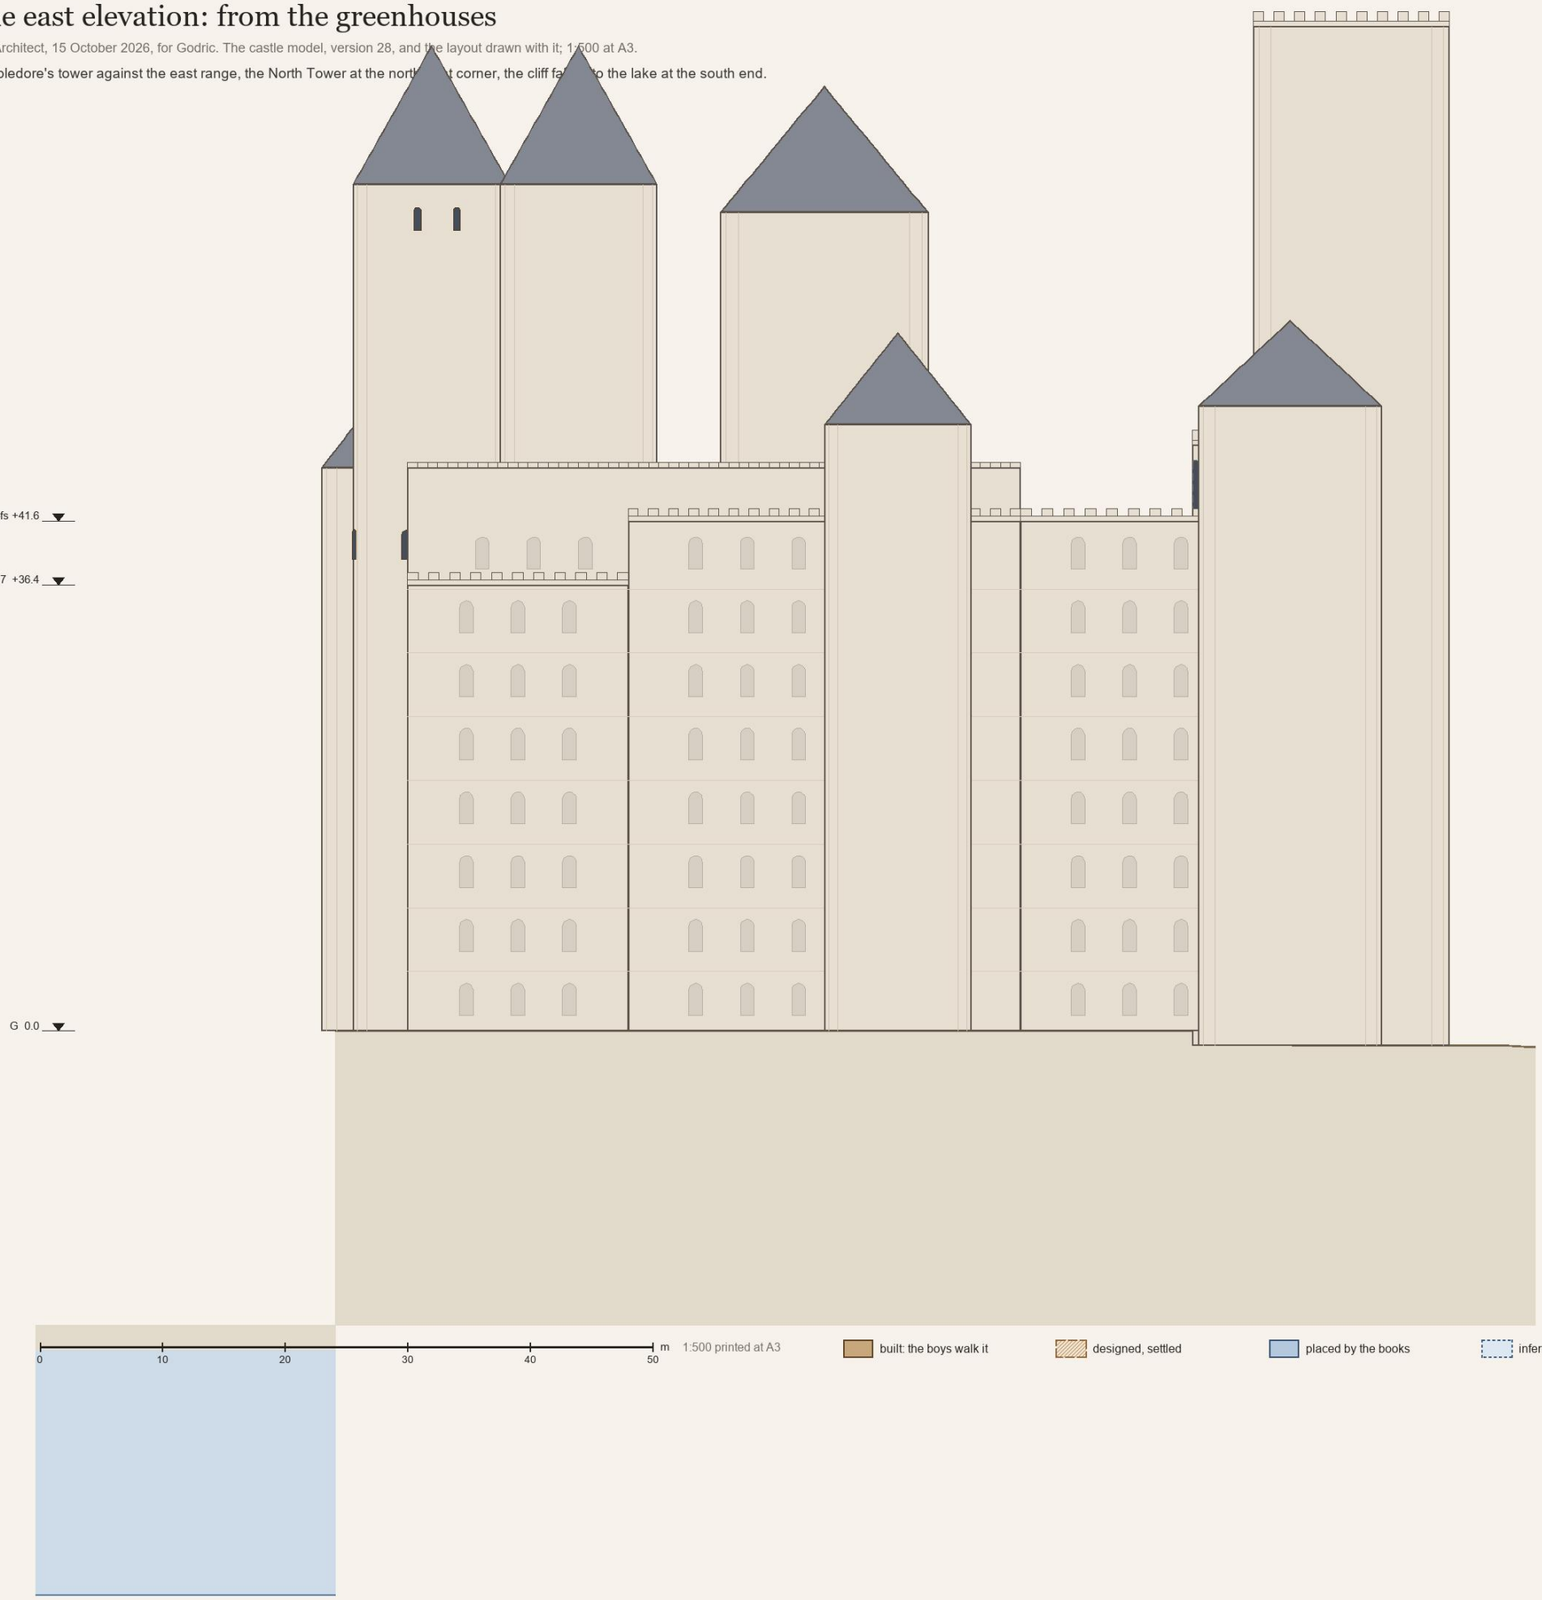


The west elevation from the Quidditch side

The Architect, 15 October 2, version 28, and the layout drawn with it; 1:500 at A3.

Ravenclaw Tower against the north-west tower and the south-west tower at the corners, the Owlery at the West Tower's top.

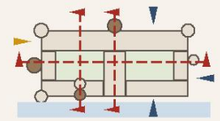

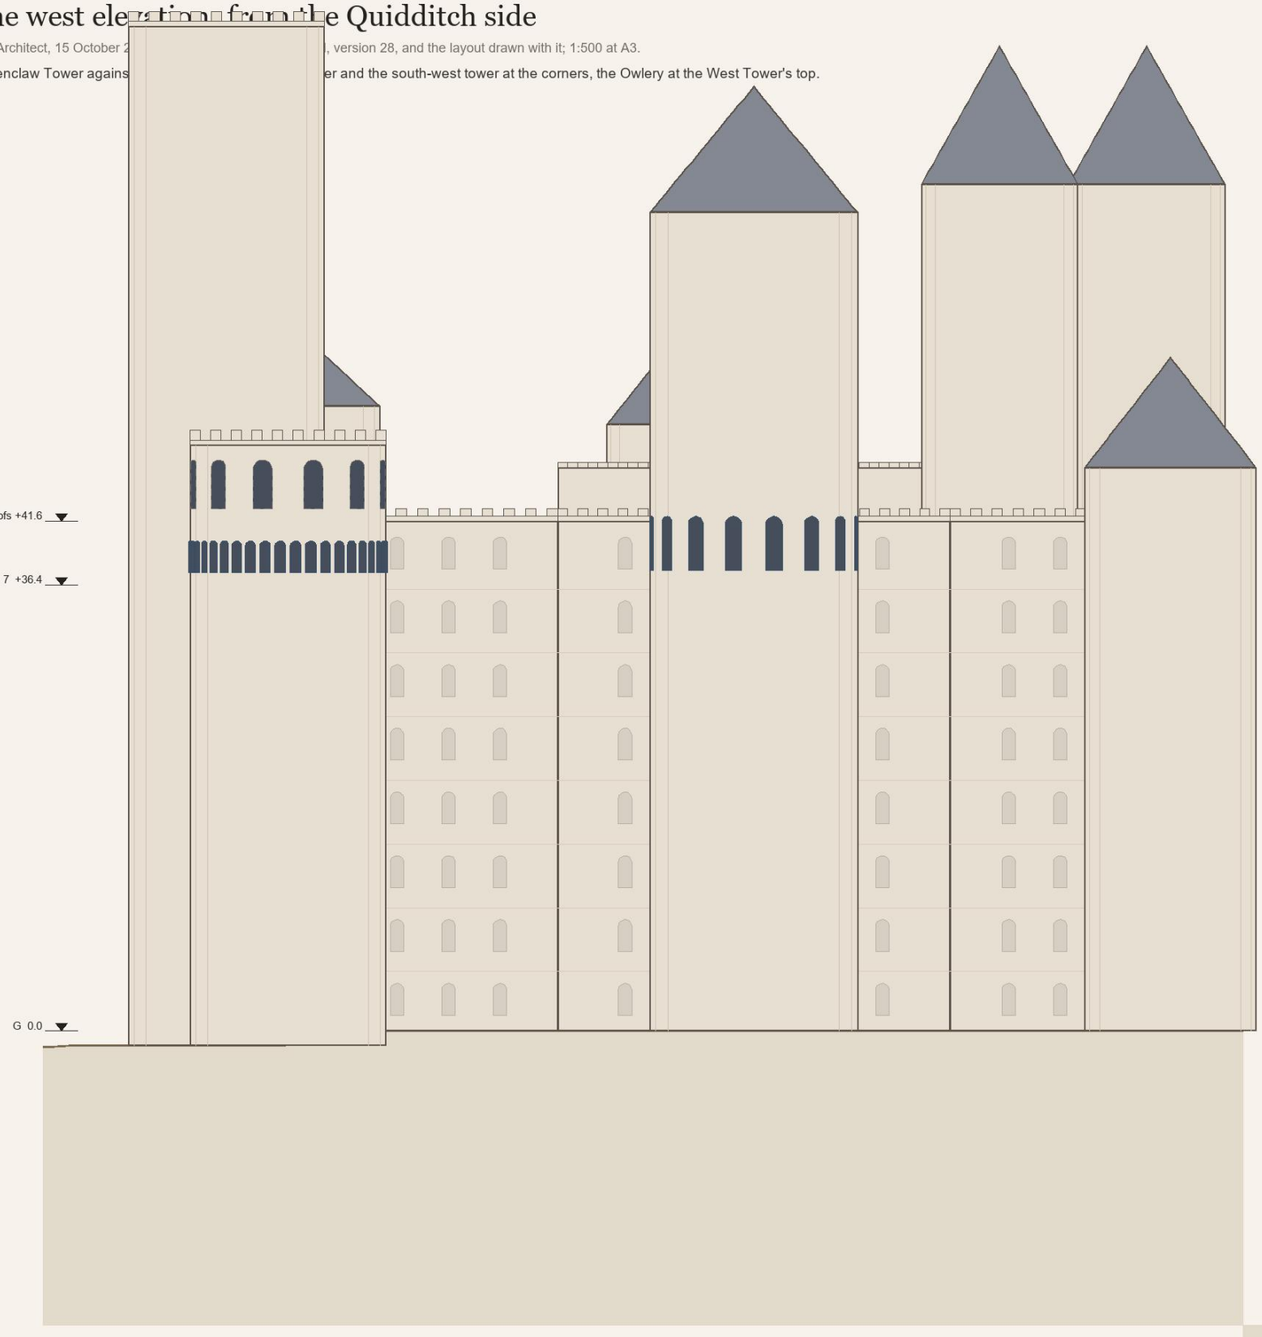

0 10 20 30 40 50 m — 1:500 printed at A3

built: the boys walk it

designed, settled

placed by the books

inferred from the books

canon, from the sweep

proposed

the layout's fill (purple ours, green canon)